

СТИСЛА ПОЯСНЮВАЛЬНА ЗАПИСКА

1. Стационарна тимчасова споруда для здійснення підприємницької діяльності, яка має торговельні приміщення для тимчасового перебування людей.

Ступінь вогнестійкості — IIIa

За умовну позначку 0.000 прийнятий рівень чистої підлоги ТС.

Кіоск має прямокутну форму.

Габаритні розміри у плані — 3.35м x 2.30м.

Загальна площа — 6.60м²

Загальна висота — 3.00 м

Площа твердого покриття — 7.71м²

Внутрішня висота складає — 2.70м

Стіни споруди запроектовані товщиною 100 мм із сертифікованим утеплювачем із мінеральної вати та обшивкою з обох сторін.

Обшивка сторін по каркасу: зовнішня — по металевому каркасу металеві листи, внутрішня (стіни та стеля) — вагонка.

Підлога — дерев'яні дошки 40 мм по металевому каркасу з утеплювачем з пенополістерольних плит та покриттям антипіринами та антигрибковими засобами.

Покрівля — по металевим прогонам і решетуванню з покриттям профнастілом, з утеплювачем з мінераловатних плит, гідро- та пароізоляцією

Зовнішня обробка:

поверхні стін — металеві листи;

вікна — металопластикові із вакуумними склопакетами,

двері — металеві листи.

покрівля — профнастіл.

2. Тимчасова споруда підключається до мереж електропостачання згідно з чинними нормами та ТУ. Точка підключення згідно з ТУ.

Опалення - електричне з встановленням навісних електро-конвекторів з регулюванням температури.

Освітлення приміщення виконується світильниками з діодними лампами.

Розподільні мережі виконані проводами із мідними жилами, що прокладені у трубах та приховані в обшивці стін.

Захист мереж від дії струмів, коротких замикань та перевантажень здійснюється автоматичними вимикачами щитка. Передбачене заземлення.

3. Благоустрій прилеглої території виконується згідно з планом благоустрою. Освітлення території передбачене світильниками, що розміщуються на основному фасаді та над входом в ТС.

Директор ТОВ "Архітектурне Бюро "АРКАДІЯ" Смаглій Д.П.

Архітектор

Кваліфікаційний сертифікат серія АА №002590



Глінін Д.Ю.

ЕСКІЗ МАЙБУТНЬОЇ ЗАМІНИ "Марсель"



Директор ТОВ "Архітектурне Бюро "Аркадія"

Архітектор


Кваліфікаційний сертифікат серія АА №002590



Смаглій Д.П.

Глінін Д.Ю.

ПЛАН ТС М 1:50

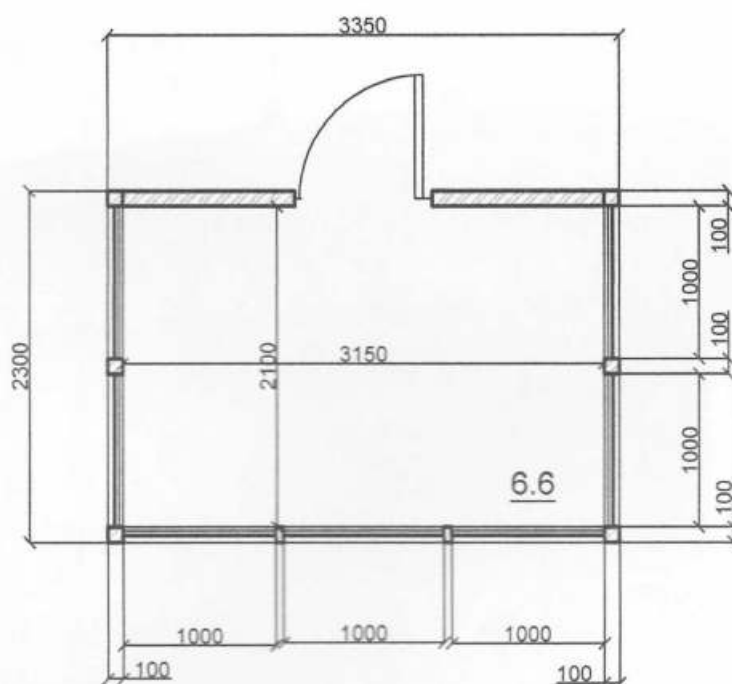

Директор ТОВ "Архітектура Бюро " Аркадія"

Архітектор

Кваліфікаційний сертифікат серія АА №002590





Смаглій Д.П.

Глінін Д.Ю.

СХЕМА РОЗМІЩЕННЯ ТС М 1:200

Площа земельної ділянки згідно з документами на
землекористування - землі міста

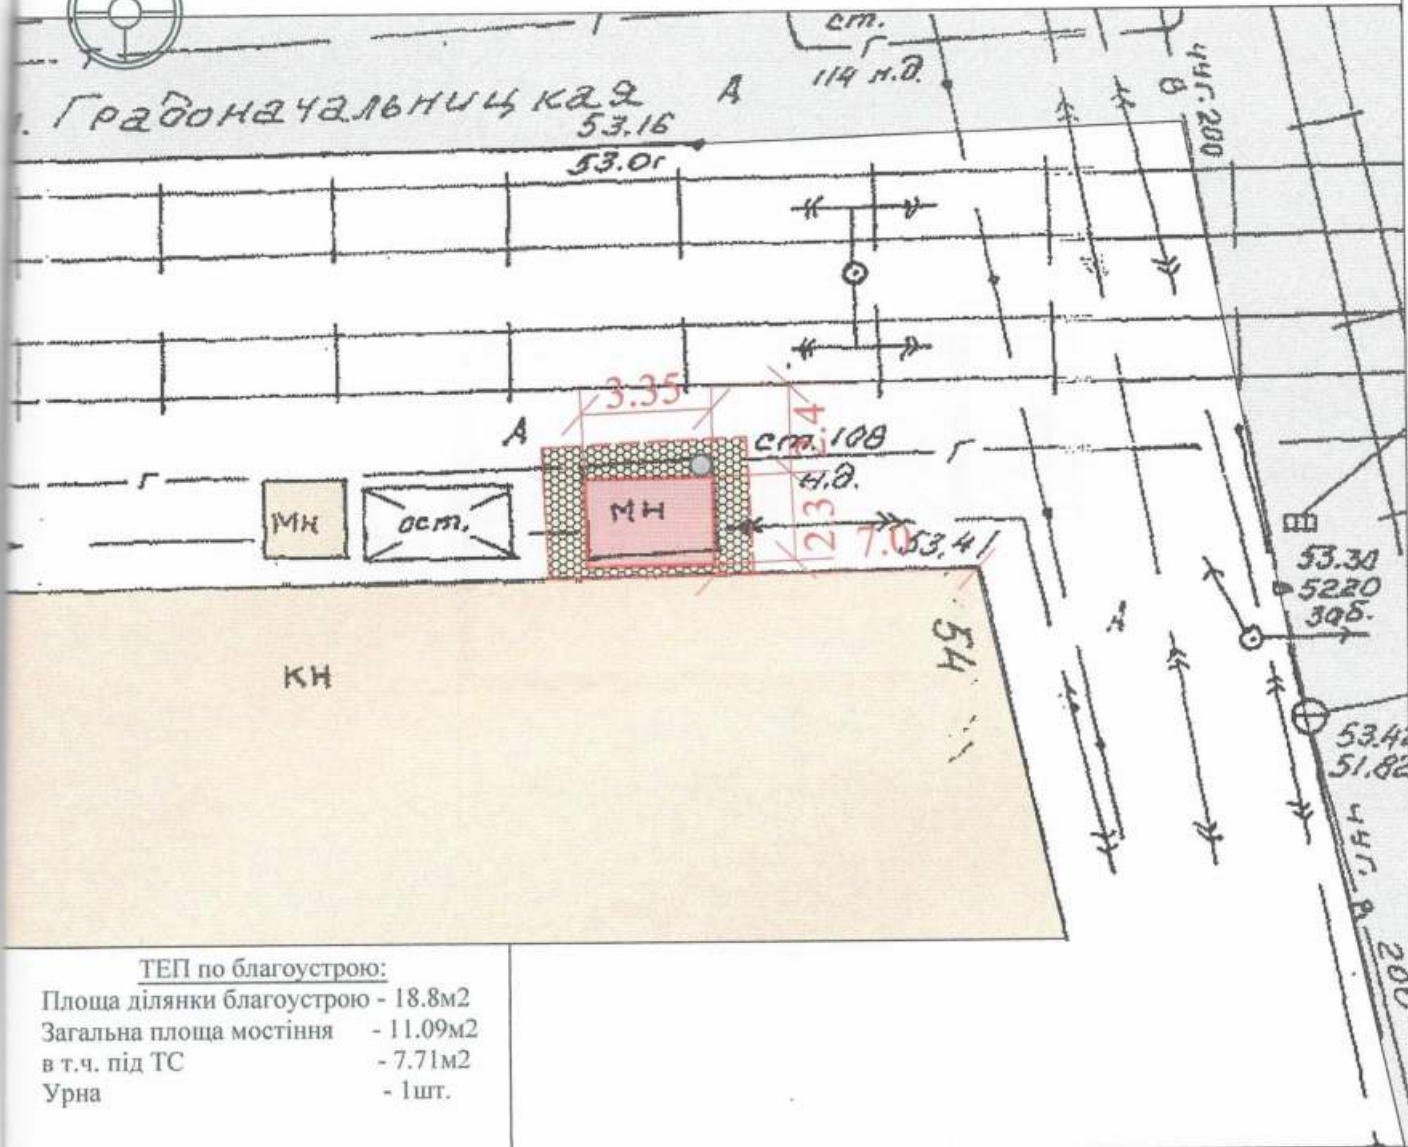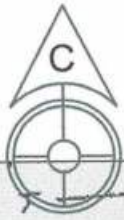

ТЕП по благоустрою:

Площа ділянки благоустрою - 18.8м²
Загальна площа мостіння - 11.09м²
в т.ч. під ТС - 7.71м²
Урна - 1шт.

Умовні позначення:



- існуючі газони



- тротуарна плитка



- існуюче асфальтне покриття



- урна



- межа благоустрою ділянки розміщення ТС



- існуюча ТС



- існуючі будівлі



- існуючі дороги

Директор ТОВ "Архітектурне Бюро "Аркадія"

Смаглій Д.П.

Архітектор


Кваліфікаційний сертифікат серія АА №002590

Глінін Д.Ю.



СИТУАЦІЙНИЙ ПЛАН М 1:2000

Місце розміщення об'єкту

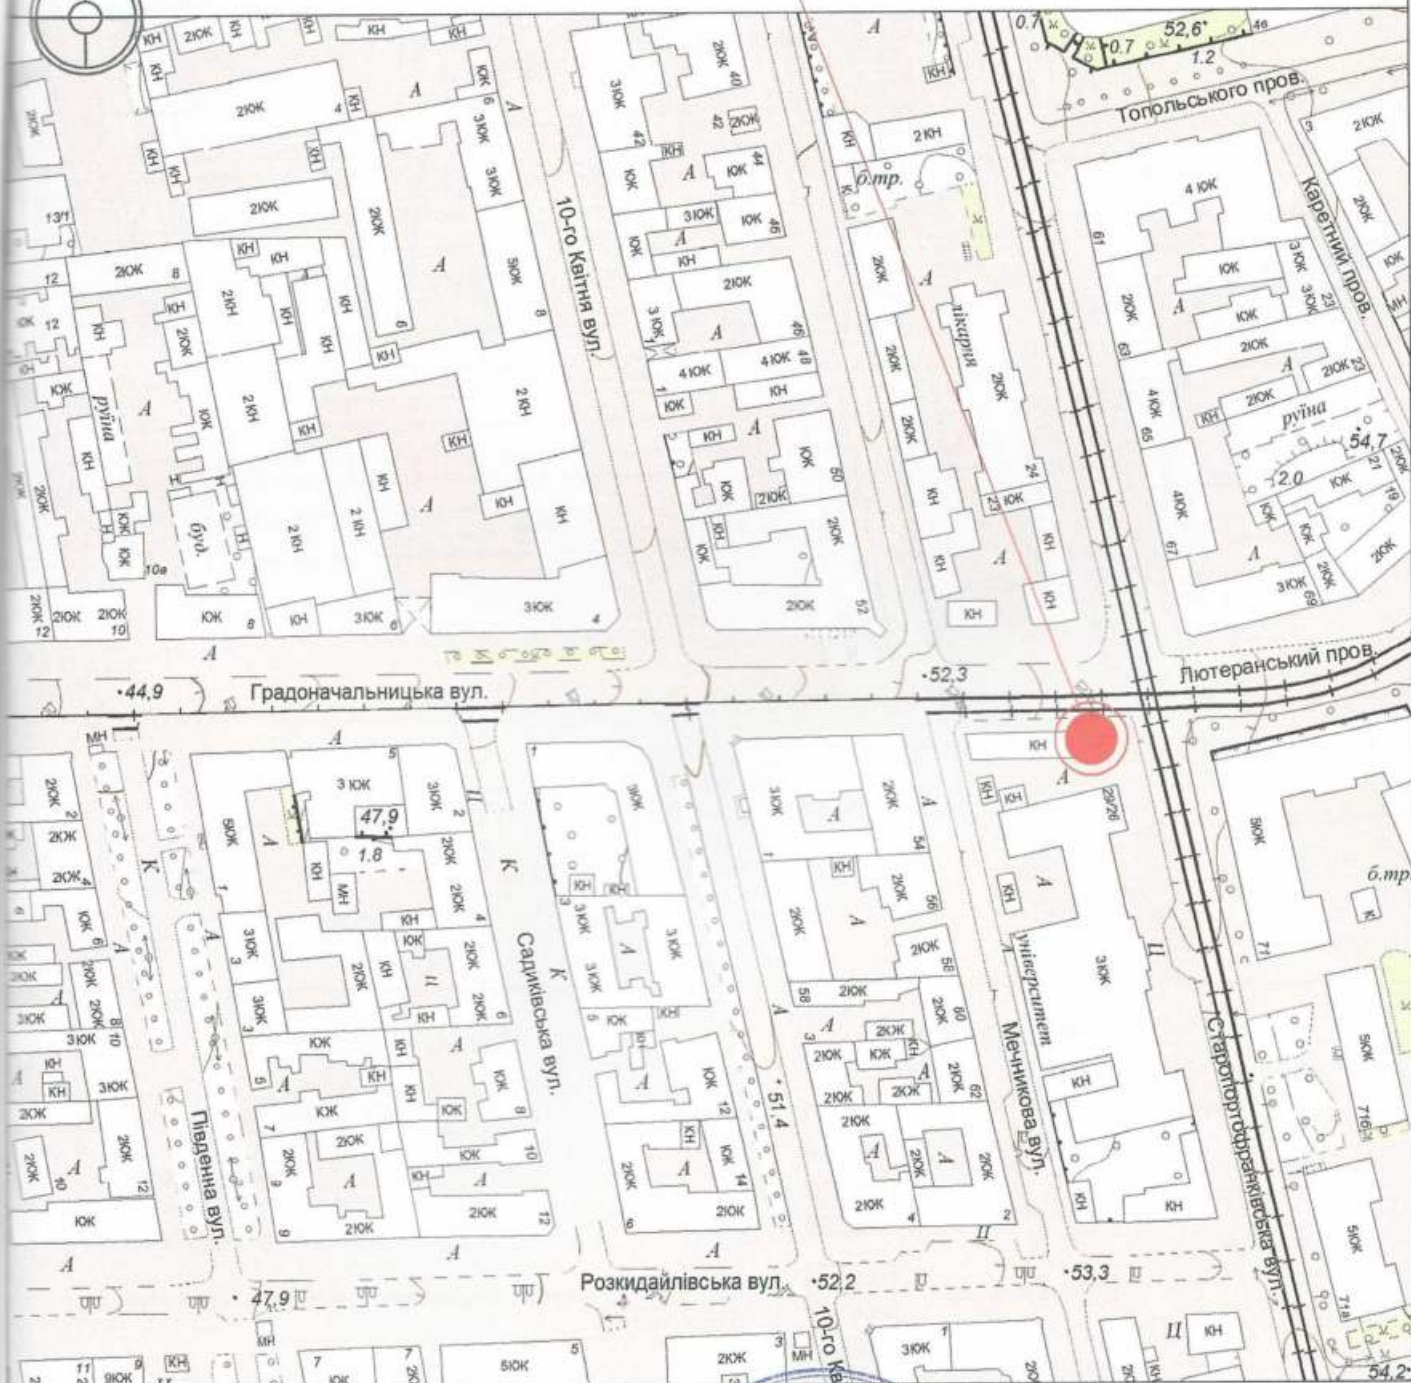

Директор ТОВ "Архітектурне Бюро "Аркадія"

Архітектор

Кваліфікаційний сертифікат серія АА №002590



"АРХІТЕКТУРНЕ БЮРО
"АРКАДІЯ" Смага Д.П.

Глінін Д.Ю.

Ідент. код
40175885