

СТИСЛА ПОЯСНЮВАЛЬНА ЗАПИСКА

1. Група Стационарних тимчасових споруд для здійснення підприємницької діяльності має торговельні приміщення для тимчасового перебування людей.
 2. За умовну позначку ± 0.000 прийнятий рівень чистої підлоги ТС.
Ступень вогнестійкості - Ша.
Габаритні розміри павільйона у плані неправильної форми - 7,00м. х 9,59м. х 2,50м. х 3,60м. х 2,50м. х 5,40м. х 7,00м. х 18,60м.
Загальна площа ТС - 18,19 м², 22,22 м², 9,55 м², 24,19 м², 12,51 м² та 25,20 м².
Площа твердого покриття – 121,20 м².
Внутрішня висота від рівня чистої підлоги складає - 3,00м.
Загальна висота складає - 3,90 м.
Грунт заснування, до встановлення ТС, ретельно утрамбовується щебнем та укладається бетонна тротуарна плитка.
Стіни споруди запроектовані товщиною 100 мм із утеплювачем з мінеральної вати та обшивкою з обох сторін.
Обшивка стін по каркасу. Фасадне скління з вакуумними склопакетами, внутрішня обробка (стіни та стеля) – пластикова вагонка.
Підлога - дерев'яні дошки 40 мм по металевому каркасу з утеплювачем з мінераловатних плит та покриттям з негорючого матеріалу.
Покрівля - металева, по металевим прогонам і решетуванню, з утеплювачем з мінераловатних плит, гідро- і пароізоляцією.
- Зовнішня обробка:
- поверхні стін - фасадне скління з вакуумними склопакетами, обшивка зовні-металевий лист,
покрівля – металевий лист для зовнішніх робіт.
3. Тимчасова споруда підключається до мереж електропостачання згідно з діючими нормами та ТУ. Точка підключення - згідно з ТУ.
Опалення - електричне з встановленням навісних електро-конвекторів з регулюванням температури.
Освітлення приміщення виконується світильниками з люмінесцентними лампами.
Розподільні мережі виконані проводами з мідними жилами, що прокладені у трубах та приховані в обшивці стін.
Захист мереж від дії струмів коротких замикань та перевантажень здійснюється автоматичними вимикачами щитка.
 4. Благоустрій прилеглої території виконується згідно з планом благоустрою.

Директор ПП «АРХМАЙСТЕР»

Архітектор

Кваліфікаційний сертифікат серія АР №000262




Горбачова Н.В


Бойцова С.П

ЕСКІЗИ ФАСАДІВ ТС

Головний фасад ТС М 1:100

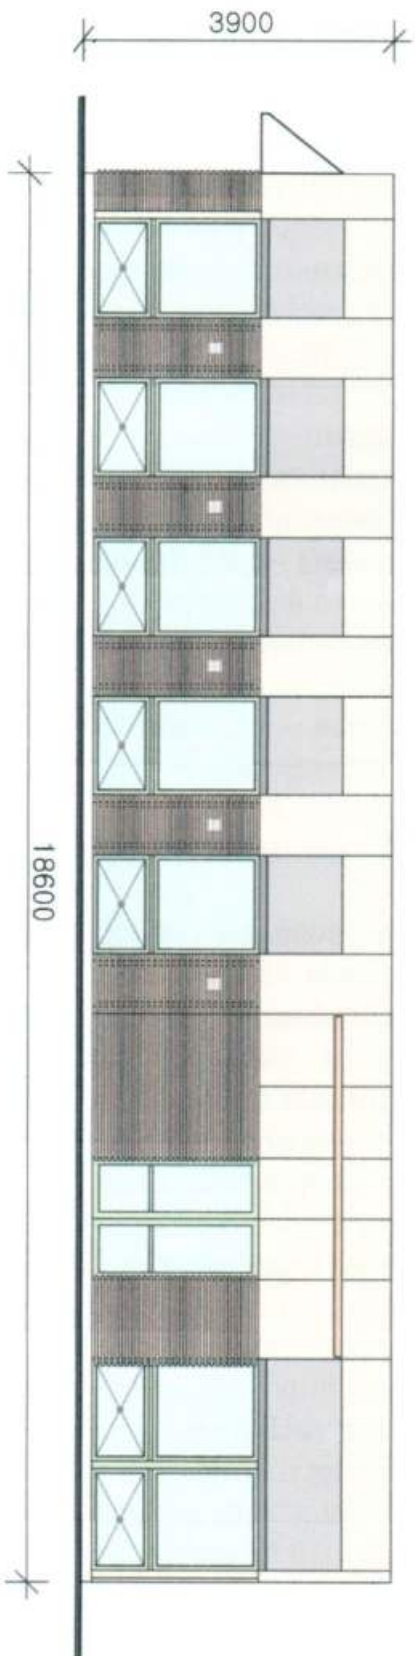

Бічний фасад ТС М 1:100

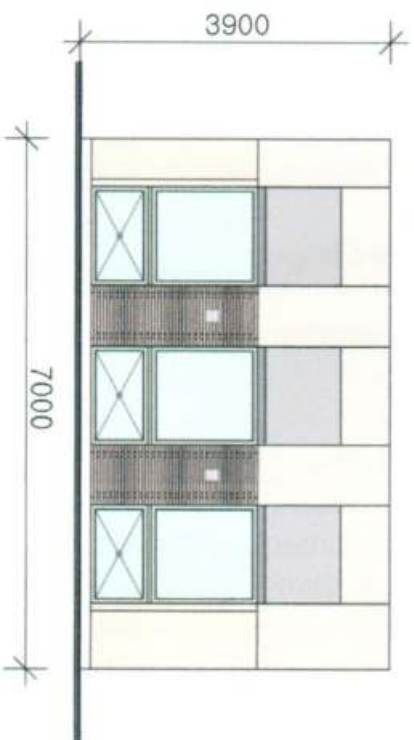

Директор ПП «АРХМАЙСТЕР»

Архітектор

Кваліфікаційний сертифікат серія АР №000262



Горбачова Н.В

Бойцова С.П


Architectural floor plan of a building with the following dimensions and room numbers:

- Overall width: 7000
- Overall height: 9595
- Room 18,19: Located in the upper left section.
- Room 22,22: Located in the upper right section.
- Room 9,55: Located in the lower left section.
- Room 24,19: Located in the lower right section.
- Room 12,51: Located in the bottom left corner.
- Room 25,20: Located in the bottom right corner.
- Dimensions: 100, 6750, 2500, 3605, 5400, 18600.

Бойцова С.П

СХЕМА РОЗМІЩЕННЯ ТС М 1:200

Площа земельної ділянки згідно з документами
на землекористування - землі міста

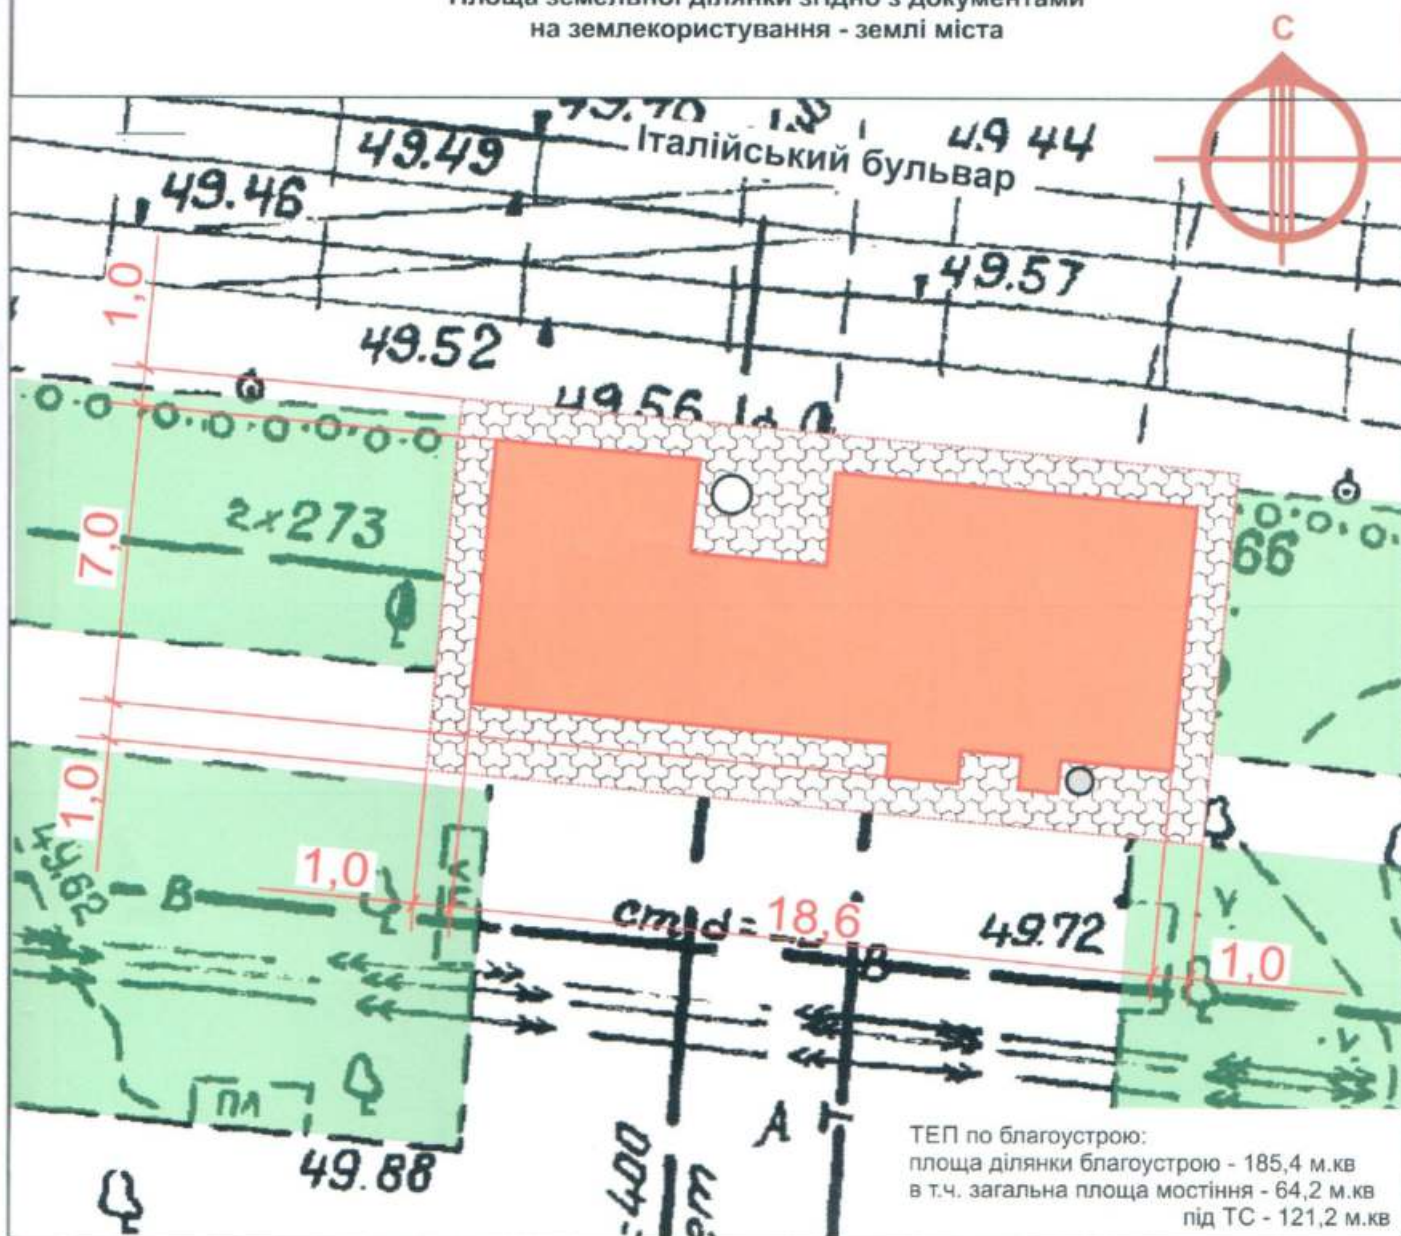

Умовні позначення:



- озеленення



- тротуарна плитка



- асфальтне покриття



- урна



- межа благоустрою ділянки
розміщення ТС



- проектна ТС



- існуючі будівлі



- існуючі дороги



- підключення до мереж
електропостачання

Директор ПП «АРХМАЙСТЕР»

Архітектор

Кваліфікаційний сертифікат серія АР №000262



Горбачова Н.В

Бойцова С.П

Ситуаційний план 1:2000

Місце розміщення об'єкту



Директор ПП «АРХМАЙСТЕР»

Архітектор

Кваліфікаційний сертифікат серія АР №000262



Горбачова Н.В

Бойцова С.П