

## ПОЯСНЮВАЛЬНА ЗАПИСКА

1. Стационарних тимчасових споруд для здійснення підприємницької діяльності має торговельні приміщення для тимчасового перебування людей.

Ступінь вогнестійкості - III а.

Габаритні розміри у плані 4,1 м X 3,6

Площа забудови - 14,76 м<sup>2</sup>

Загальна площа – 13,26 м<sup>2</sup>

Площа твердого покриття - 14,76 м<sup>2</sup>

Загальна висота – 3,00 м

Внутрішня висота складає – 2,40 м

рунт заснування, до встановлення ТС, ретельно утрамбовується щебенем та ладається бетонна тротуарна плитка.

іни групи споруд запроектовані товщиною 100 мм із сертифікованим утеплювачем із неральної вати та обшивкою з обох сторін.

бшивка стін по каркасу: зовнішня – колірний металевий профіль; внутрішня (стіни й еля) – пластикова вагонка.

ідлога – дерев'яні дошки 40 мм по металевому каркасу з утеплювачем монополістерольних плит та покриттям з негорючого матеріалу.

аповнення прорізів з метало пластикового профілю та рольгратами.

окрівля – по металевих прогонах і решетуванню з покриттям із профільованного галевого листа, з утеплювачем з мінераловатних плит, гідро- і пароізоляцією.

овнішня обробка:

іверхні стін – колірний металевий профіль;

ікна – металопластикові;

івері – металопластикові;

іокрівля – профільований сталевий лист;

іолірне вирішення фасадів дивись графічний додаток.

Внутрішню обробку виконати згідно індивідуального дизайну-проекту із астосуванням негорючих оздоблювальних матеріалів, з підтвердженням сертифікатом.

2. Підключення до інженерних мереж:- тимчасова споруда підключається до нуючої електромережі, згідно договору про постачання електричної енергії.

Опалювання – електричне з встановленням навісних електро - конвекторів з регулюванням температури.

Освітлення приміщення виконане стельовими світильниками з люмінесцентними лампами.

Архітектор

Кваліфікаційний сертифікат, серія АА № 002057




Давидова В.В.

ЕСКІЗ МАЙБУТНЬОЇ ЗАМІНИ  
"Марсель"




# ЕСКІЗИ ФАСАДІВ ТС М 1:50

Фасад в осях 1-2

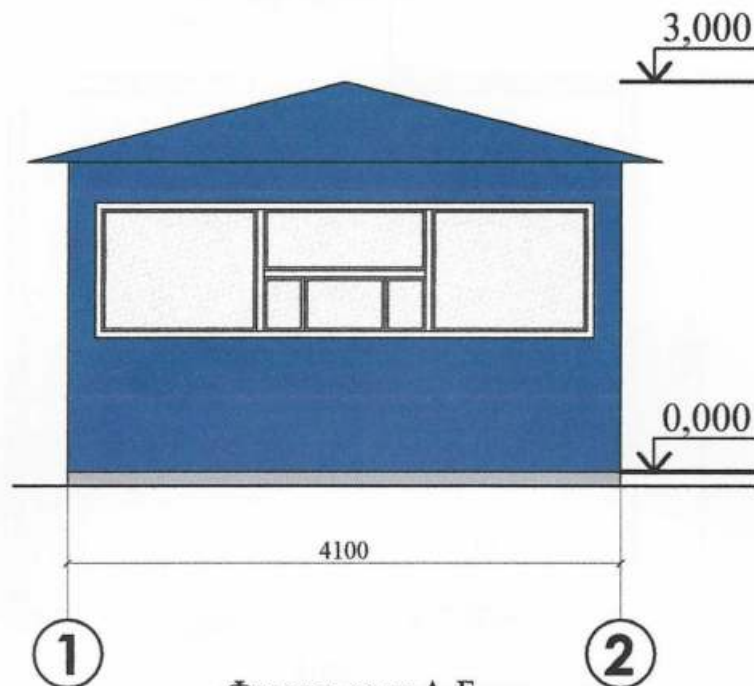

Фасад в осях А-Б

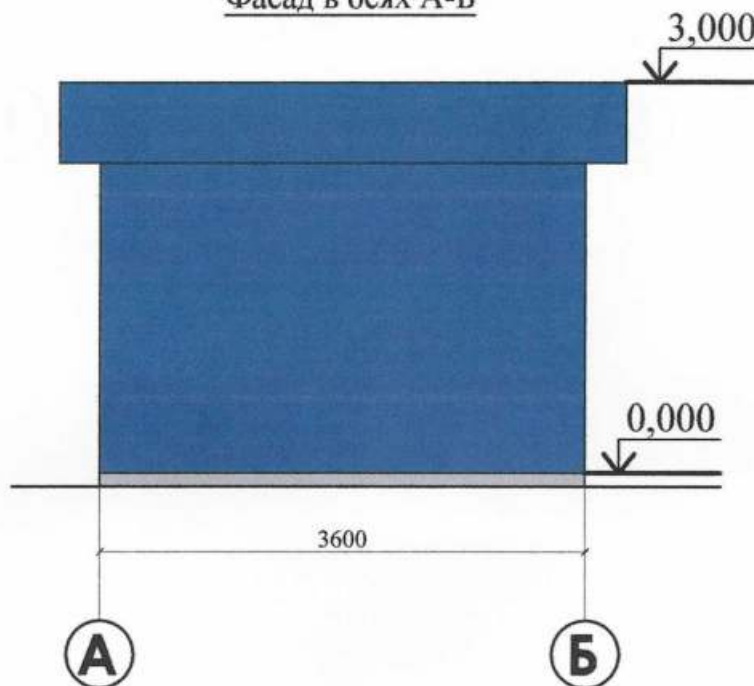


Архітектор  
Кваліфікаційний сертифікат, серія АА № 002057



Давидова В.В.

# ПЛАН ТС М 1:50

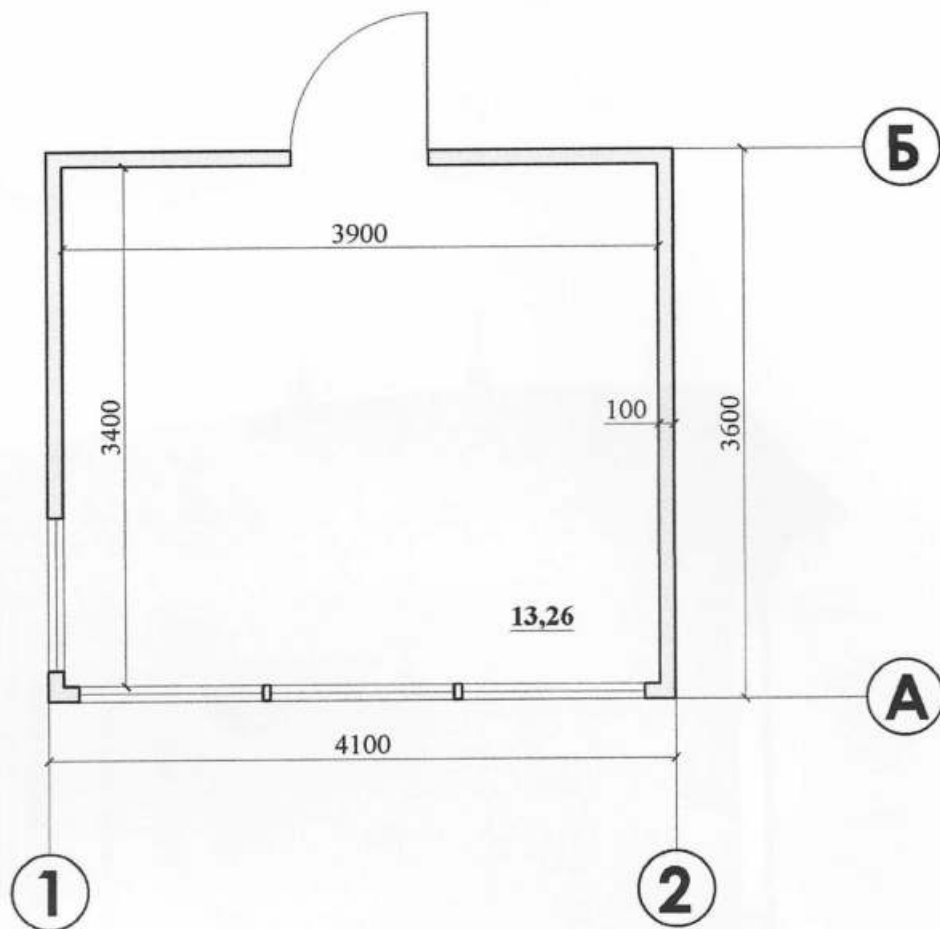


Архітектор  
Кваліфікаційний сертифікат, серія АА № 002057



Давидова В.В.

# СХЕМА РОЗМІЩЕННЯ ТС М 1:500

Площа земельної ділянки згідно з документами на землекористування - землі міста

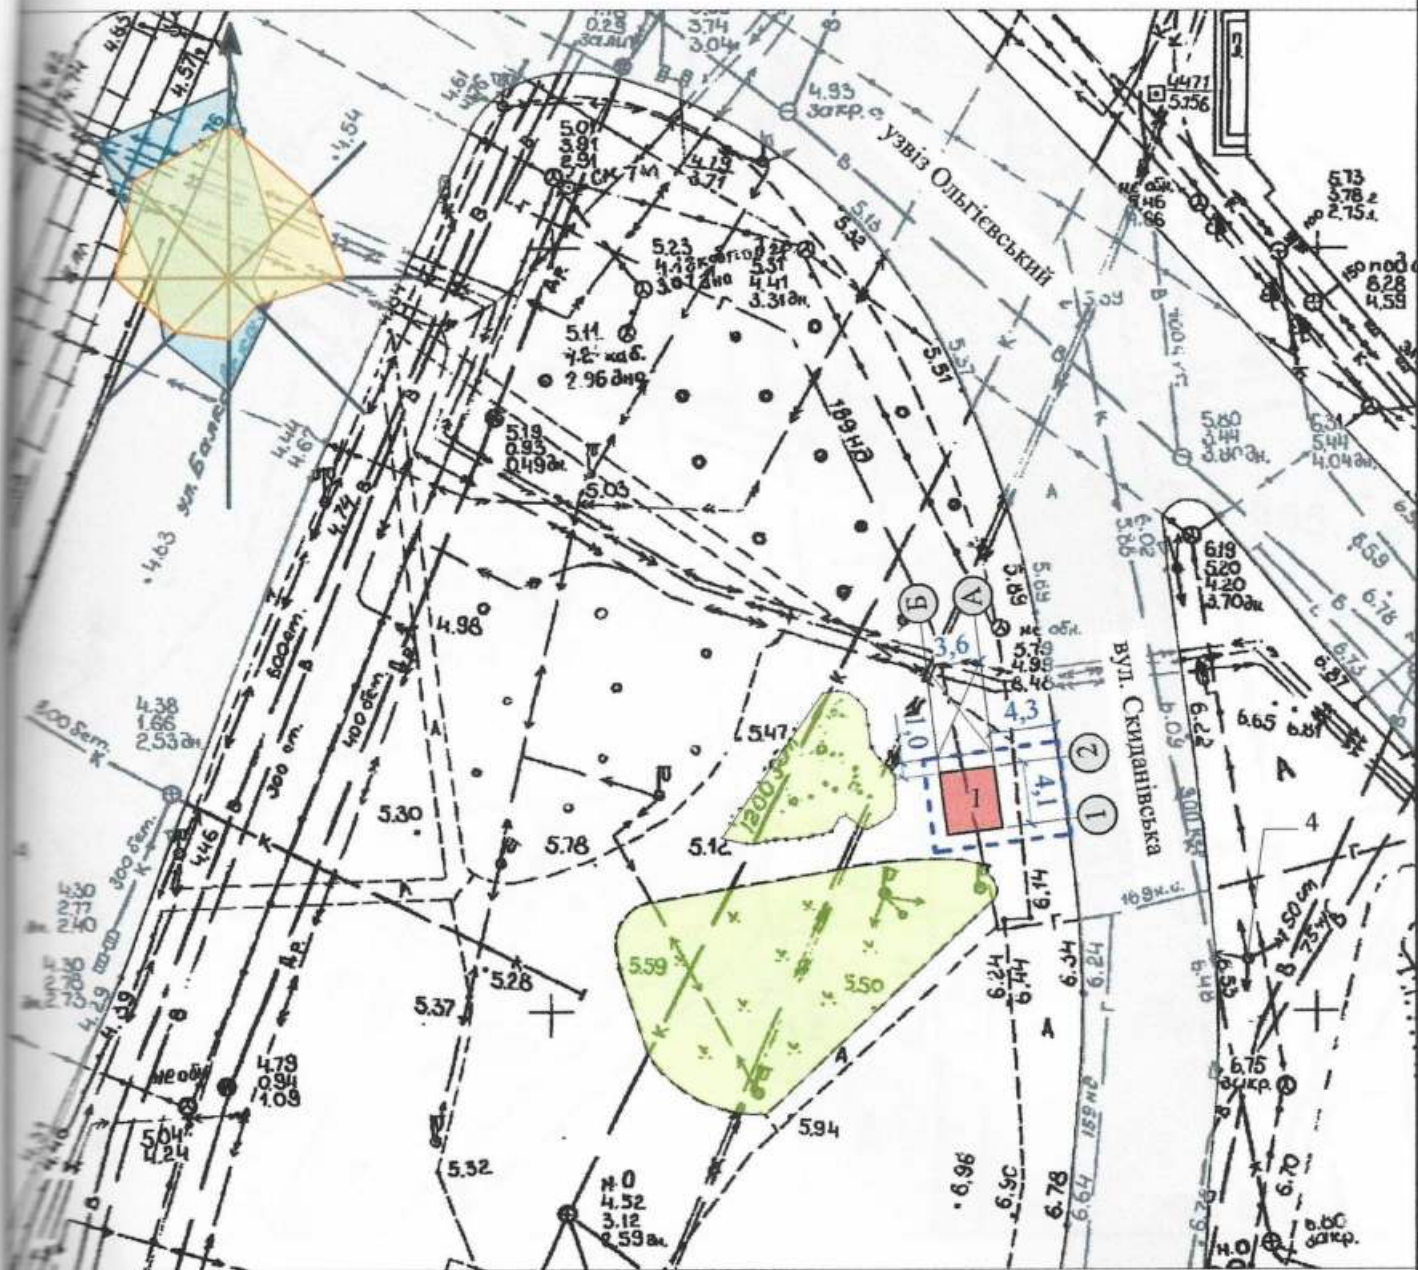

## Експлікація:

- 1) місце розташування ТС;
- 2) червоні лінії;
- 3) лінії регулювання забудови;
- 4) місця підключення до інженерних мереж.

## Умовні позначення

- Існуюча дорога
- Існуючі споруди
- Існуюче озеленення
- Тимчасова споруда
- Територія, що підлягає благоустрою

Архітектор

Кваліфікаційний сертифікат, серія АА № 002057




Давидова В.В.

# СИТУАЦІЙНИЙ ПЛАН

## М 1:2000

Місце розміщення об'єкта

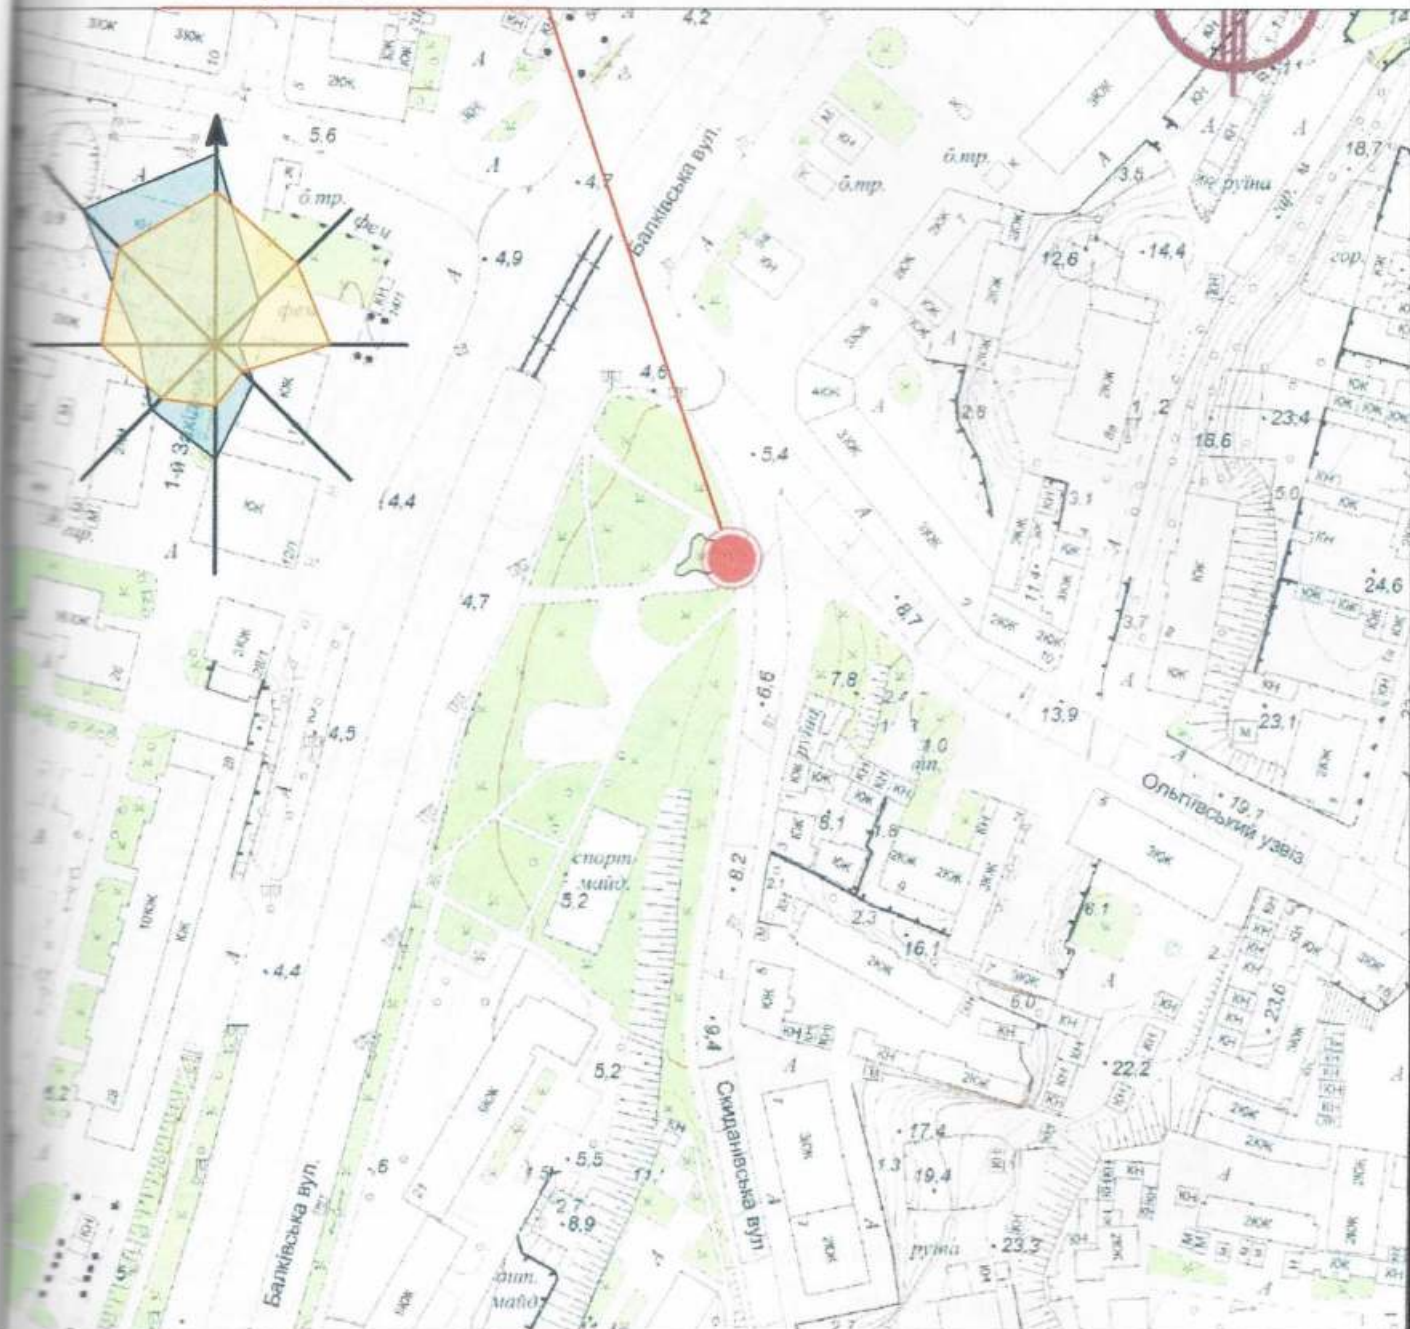

Архітектор  
Кваліфікаційний сертифікат, серія АА № 002057



Давидова В.В.