

ПОЯСНЮВАЛЬНА ЗАПИСКА

1. Група тимчасових споруд (ТС) для здійснення підприємницької діяльності має закриті приміщення для тимчасового перебування людей.
За умовну позначку 0.000 прийнятий рівень чистої підлоги ТС.
Ступінь вогнестійкості - Ша. Кількість тимчасових споруд, всього - 4 шт.
Габаритні розміри стаціонарних споруд в плані -
- 6.40м x 4.50м. Площа ТС - 28.80м². Кількість ТС - 3 шт.
- 5.80м x 4.50м. Площа ТС - 26.10м². Кількість ТС - 1 шт.
Площа забудови групи ТС - 112.50м².
У павільйонах розташовані приміщення, загальною площею - 105.27м².
Внутрішня висота групи ТС від рівня чистої підлоги складає - 2.80м.
Загальна висота групи ТС - 3.00м.
Грунт заснування, до встановлення групи ТС, ретельно утрамбован щебнем та укладається тротуарна плитка. Група ТС встановлена без улаштування фундаментів.
Стіни споруд запроектовані по типу «Сендвич», товщиною 100мм із утеплювачем з мінеральної вати та обшивкою з обох сторін.
Обшивка стін по каркасу: зовнішня - декоративна дерев'яна напівкругла вагонка, внутрішня (стіни й стеля) - декоративні дерев'яні панелі.
Підлога - дерев'яні дошки 40мм по металевому каркасу з утеплювачем із мінераловатних плит та покриттям з негорючого матеріалу.
Покрівля - по металевим прогонам і решетуванню з покриттям із профільованого сталевих листа, з утеплювачем із мінераловатних плит, гідро- і пароізоляцією.

Зовнішня обробка.

поверхні стін - декоративна дерев'яна напівкругла вагонка;
вікна - відсутні;
двері - дерев'яні;
покрівля - профільований сталевий лист;

2. Група ТС підключена до мереж електропостачання згідно з діючими нормами та ТУ. Точка підключення - близька опора, що розташована поряд з територією ділянки, згідно з ТУ.

Опалювання - електричне з встановленням навісних електро-конвекторів з регулюванням температури.

Освітлення приміщення виконане стельовими світильниками з люмінесцентними лампами.

Розподільні мережі павільйонів, виконані проводами з мідними жилами, що прокладені у трубах та приховані в обшивці стін. Мережі обрані по тривалодопустимим струмам навантаження.

Захист мереж від дії струмів коротких замикань і перевантаження здійснюється автоматичними вимикачами щитка.

3. Благоустрій прилеглої території виконується згідно з планом благоустрою.

Освітлення території передбачене світильниками, що розташовані під козирьками ТС.

ГАП

Кваліфікаційний сертифікат серія АА №000199

Архітектор




Ігнатова Л.А.

Чабан Л.В.

ЕСКІЗИ ФАСАДІВ ГРУПИ ТС, М 1:100

Головний фасад

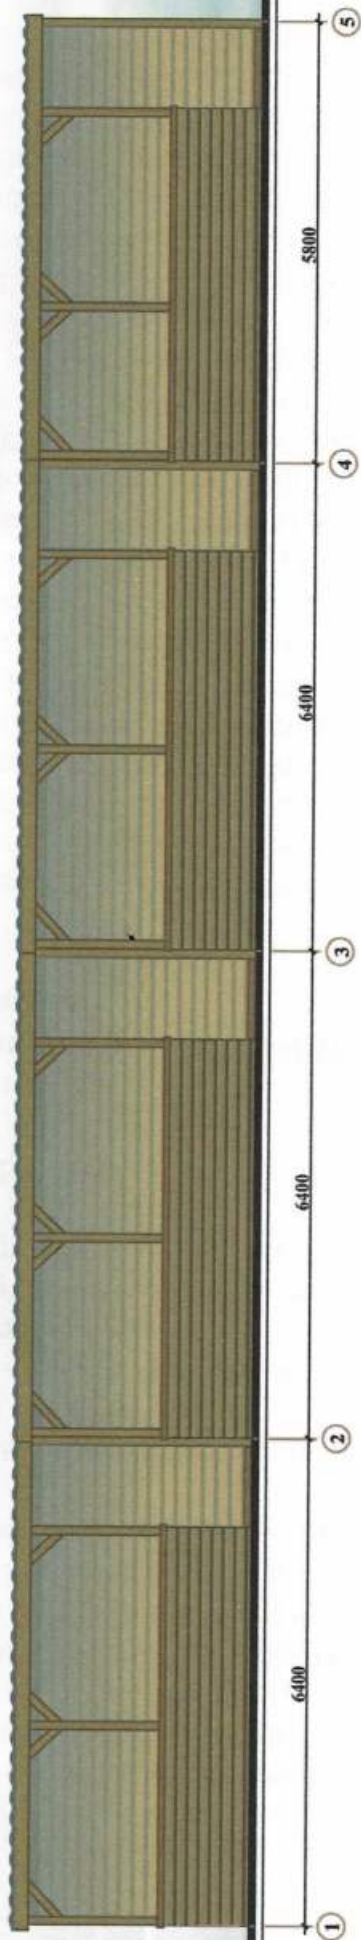

Бічний фасад



ГАП
Кваліфікаційний сертифікат серія АА №000199


Архітектор

Ігнатова Л.А.

Чабан Л.В.



ПЛАН ГРУПИ ТС, М 1:100

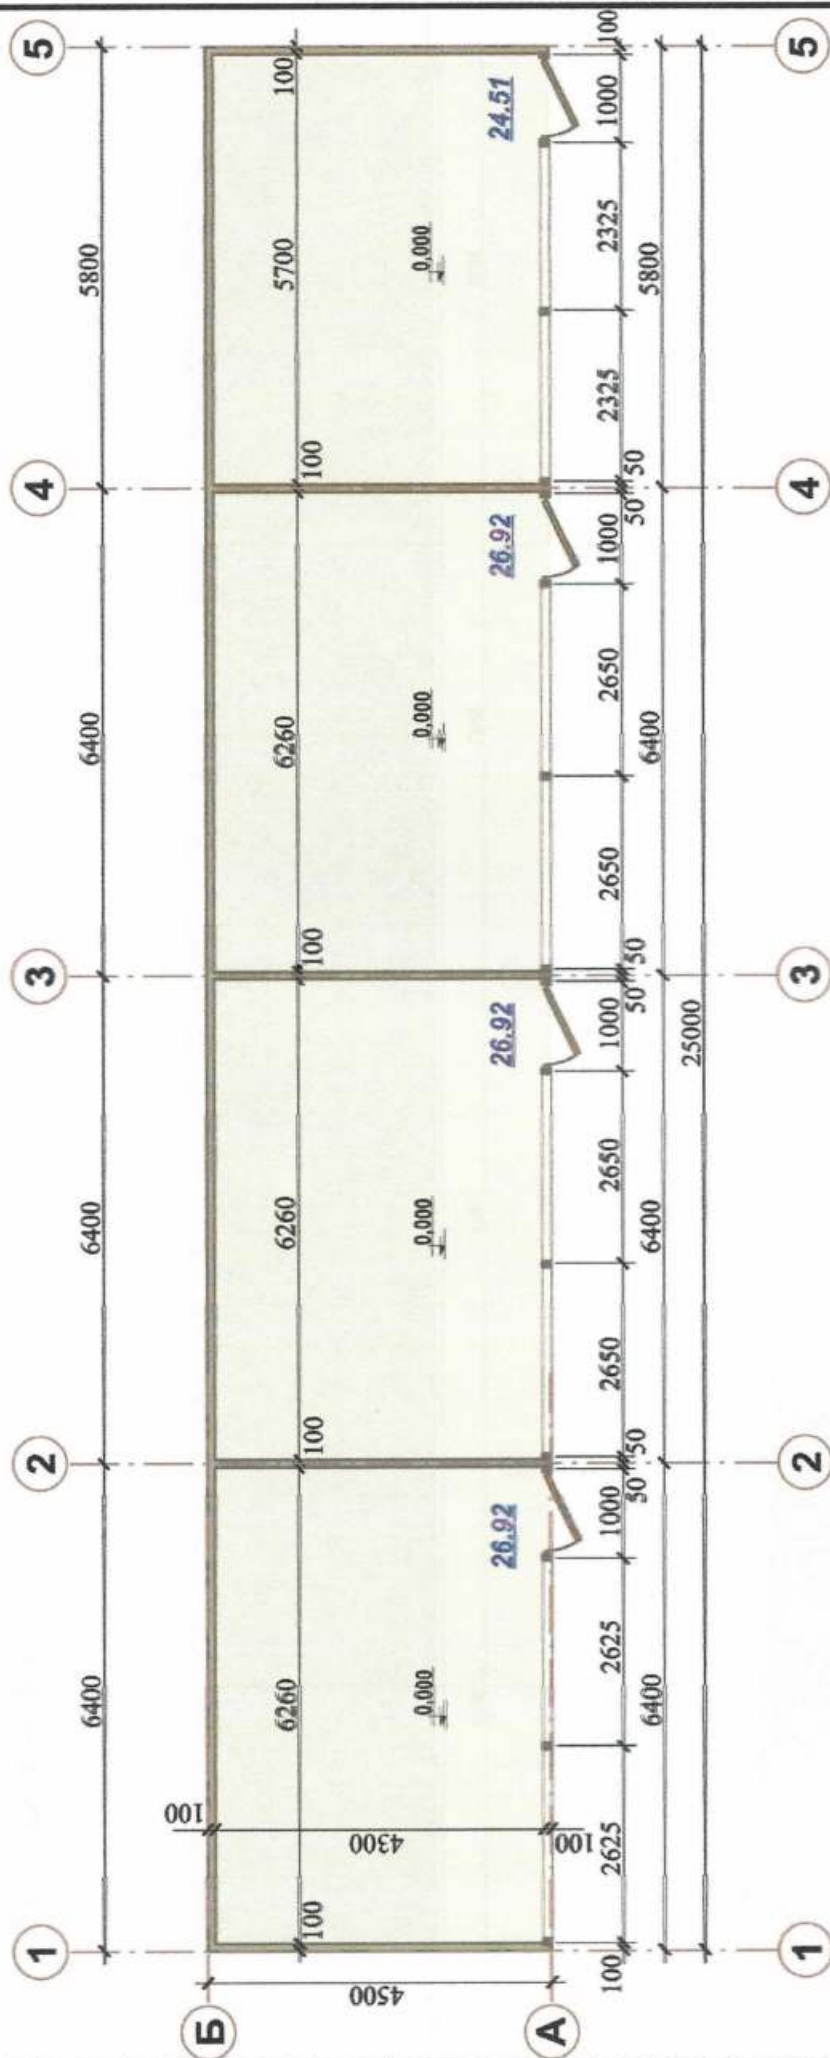

Ігнатова Л.А.

ГАП
Кваліфікаційний сертифікат серія АА №000199

Чабан Л.В.


Архітектор



СХЕМА РОЗМІЩЕННЯ ТС М 1:500

Площа земельної ділянки згідно з документами на землекористування

Город земель фонд земля м.Одеси

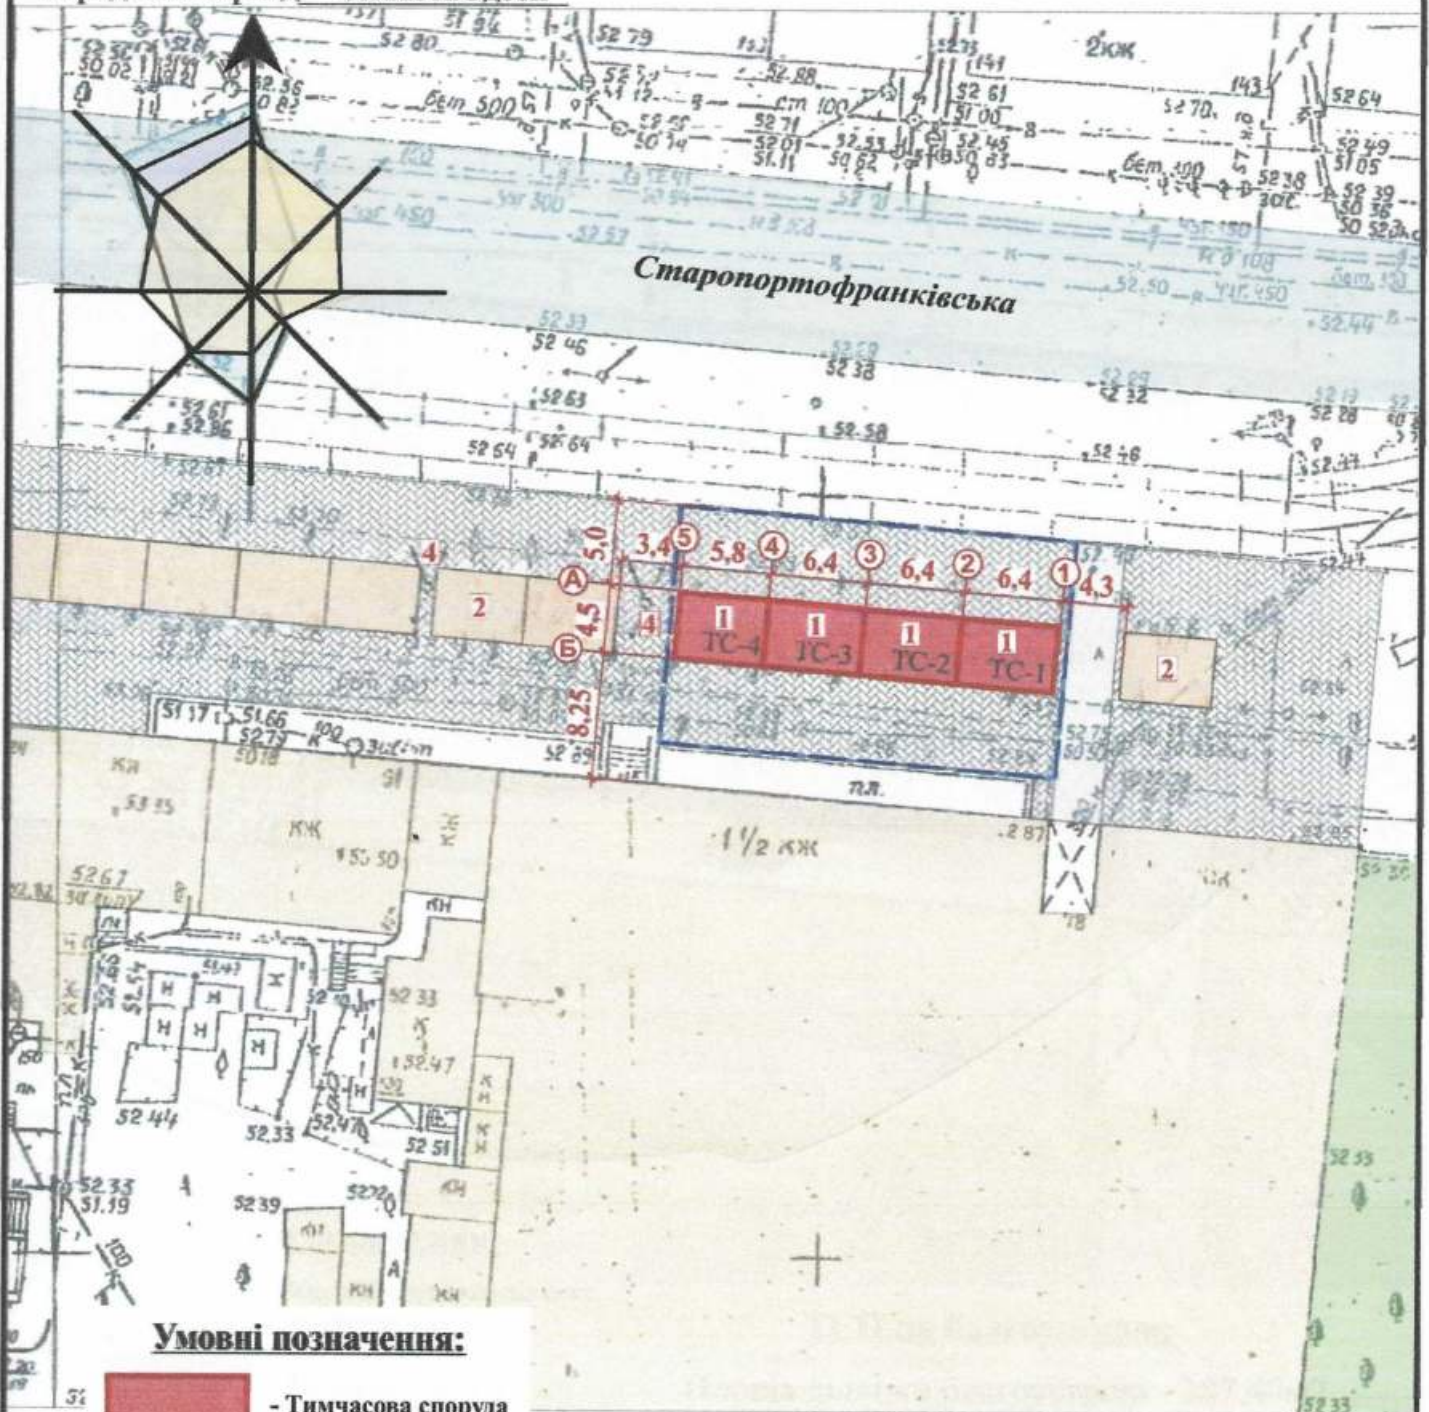

Умовні позначення:

- Тимчасова споруда
- Існуючі будівлі і споруди
- Існуючі дороги
- Озеленення
- Межа благоустрою ділянки розміщення ТС

Експлікація:

- 1) місце розташування ТС;
- 2) лінії регулювання забудови;
- 3) червоні лінії;
- 4) місця підключення до інженерних мереж.

ГАП
Кваліфікаційний сертифікат серія АА №000199


Архітектор

Ігнатова Л.А.

Чабан Л.В.



СИТУАЦІЙНИЙ ПЛАН, М 1:2000

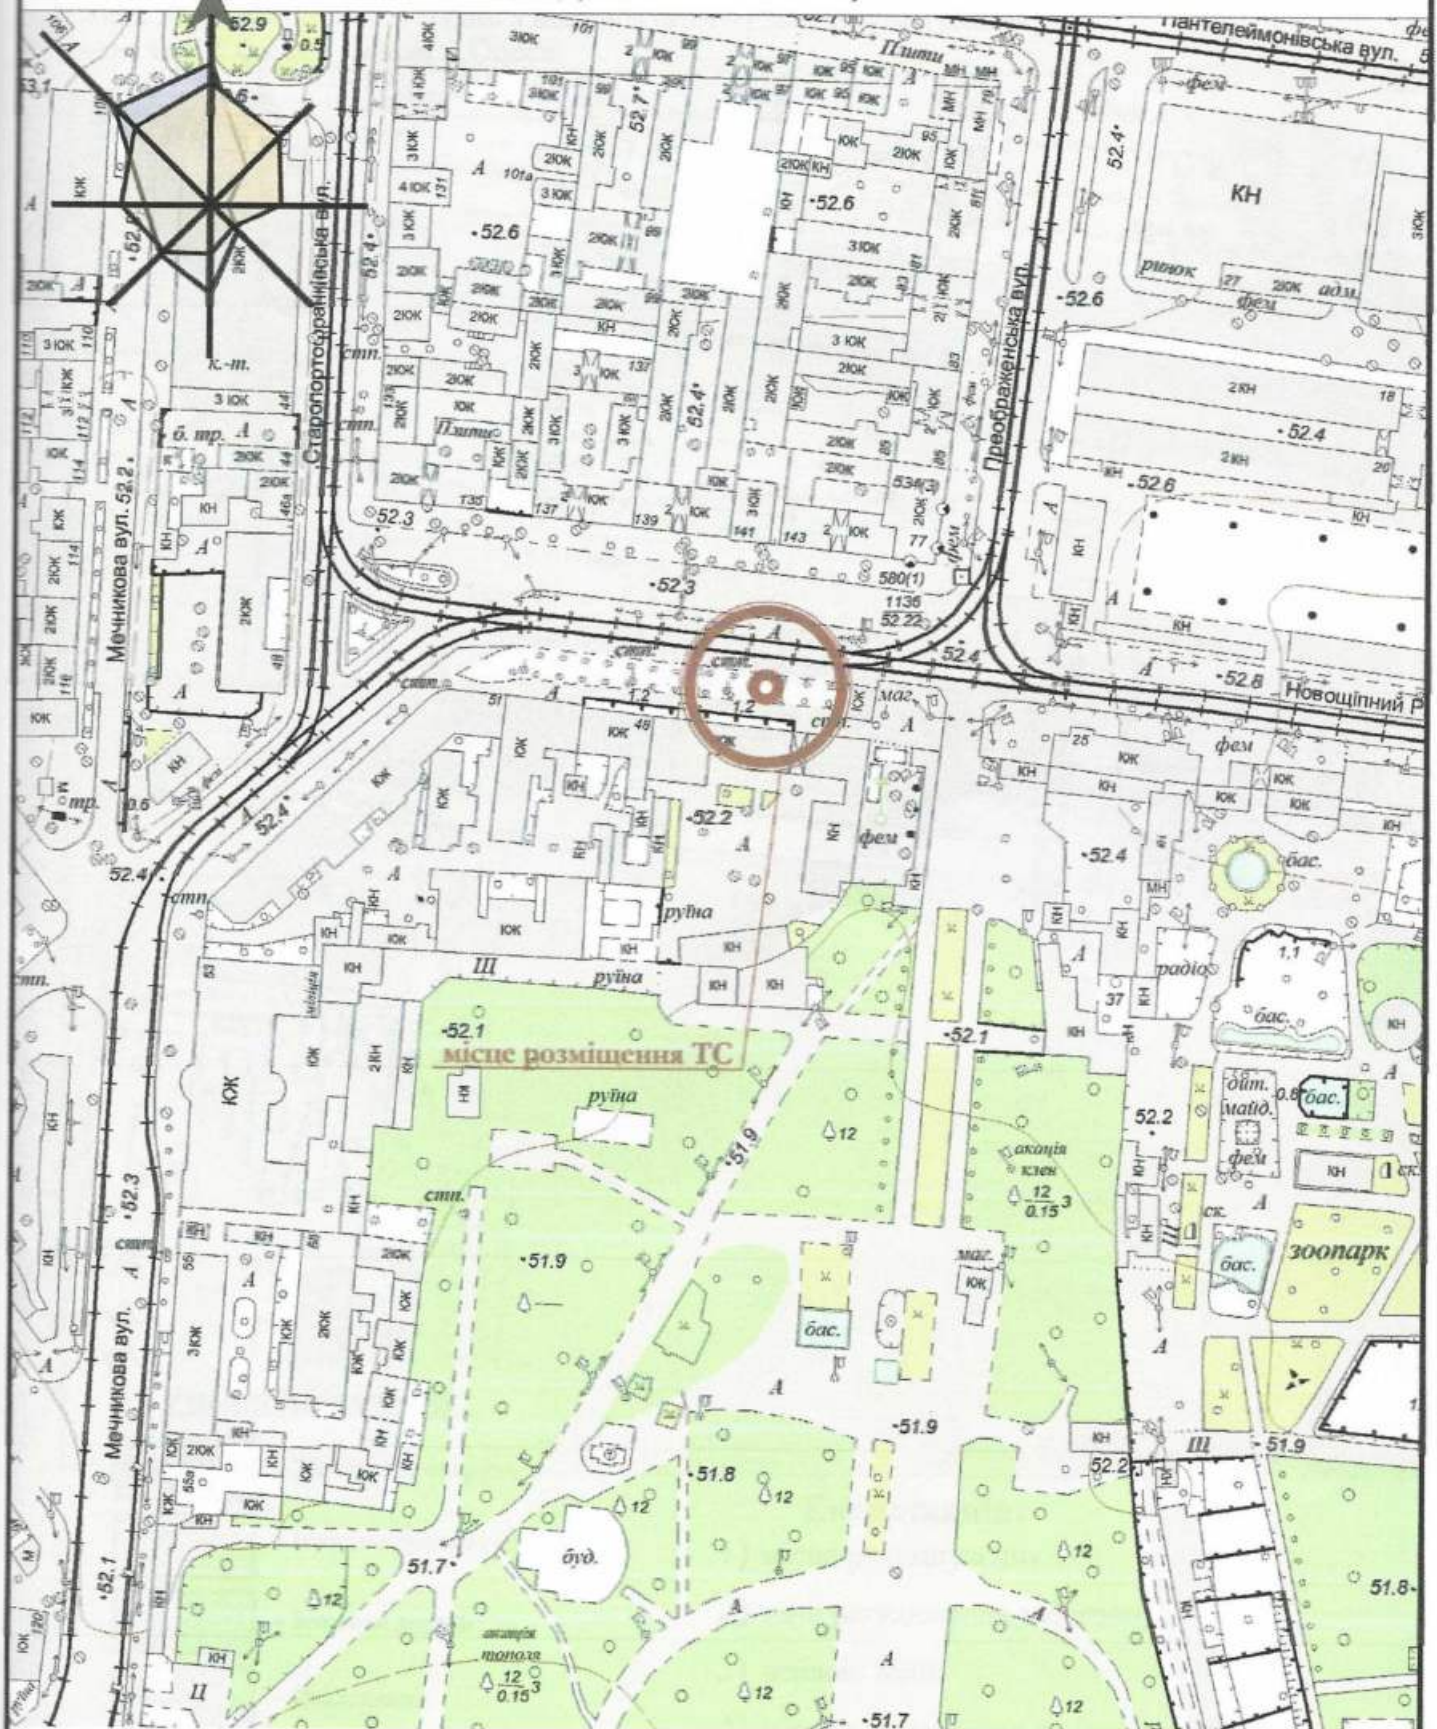

ГАП
Кваліфікаційний сертифікат серія АА №000199
Архітектор



Ігнатова Л.А.

Чабан Л.В.