

СТИСЛА ПОЯСНЮВАЛЬНА ЗАПИСКА

1. Стационарна тимчасова споруда для здійснення підприємницької діяльності має торговельні приміщення для тимчасового перебування людей.
 2. За умовну позначку ± 0.000 прийнятий рівень чистої підлоги ТС.
- Ступень вогнестійкості - Ша.
- Габаритні розміри павільйона у плані - 3,00x2,00 м.
- Загальна площа ТС - 5,04 м². Площа твердого покриття – 6,00 м².
- Внутрішня висота від рівня чистої підлоги складає - 2,50м.
- Загальна висота складає - 3, 51 м.
- Грунт заснування, до встановлення ТС, ретельно утрамбовується щебнем та укладається бетонна тротуарна плитка.
- Стіни споруди запроектовані товщиною 100 мм із утеплювачем з мінеральної вати та обшивкою з обох сторін.
- Обшивка стін по каркасу. Фасадне скління з вакуумними склопакетами, внутрішня обробка (стіни та стеля) – пластикова вагонка.
- Підлога - дерев'яні дошки 40 мм по металевому каркасу з утеплювачем з мінераловатних плит та покриттям з негорючого матеріалу.
- Покрівля - металева, по металевим прогонам і решетуванню, з утеплювачем з мінераловатних плит, гідро- і пароізоляцією.

Зовнішня обробка:

поверхні стін - фасадне скління з вакуумними склопакетами, обшивка зовні-
дерв'яний брус,
покрівля – металева черепиця.

3. Тимчасова споруда підключається до мереж електропостачання згідно з діючими нормами та ТУ. Точка підключення - згідно з ТУ.
- Опалення - електричне з встановленням навісних електро-конвекторів з регулюванням температури.
- Освітлення приміщення виконується світильниками з люмінісцентними лампами.
- Розподільні мережі виконані проводами з мідними жилами, що прокладені у трубах та приховані в обшивці стін.
- Захист мереж від дії струмів коротких замикань та перевантажень здійснюється автоматичними вимикачами щитка.
4. Благоустрій прилеглої території виконується згідно з планом благоустрою.

Директор ПП «АРХМАЙСТЕР»

Архітектор

Кваліфікаційний сертифікат серія АР №000262


Дорбачова Н.В

Бойцова С.П




ЕСКІЗИ ФАСАДІВ ТС

Головний фасад ТС М 1:50

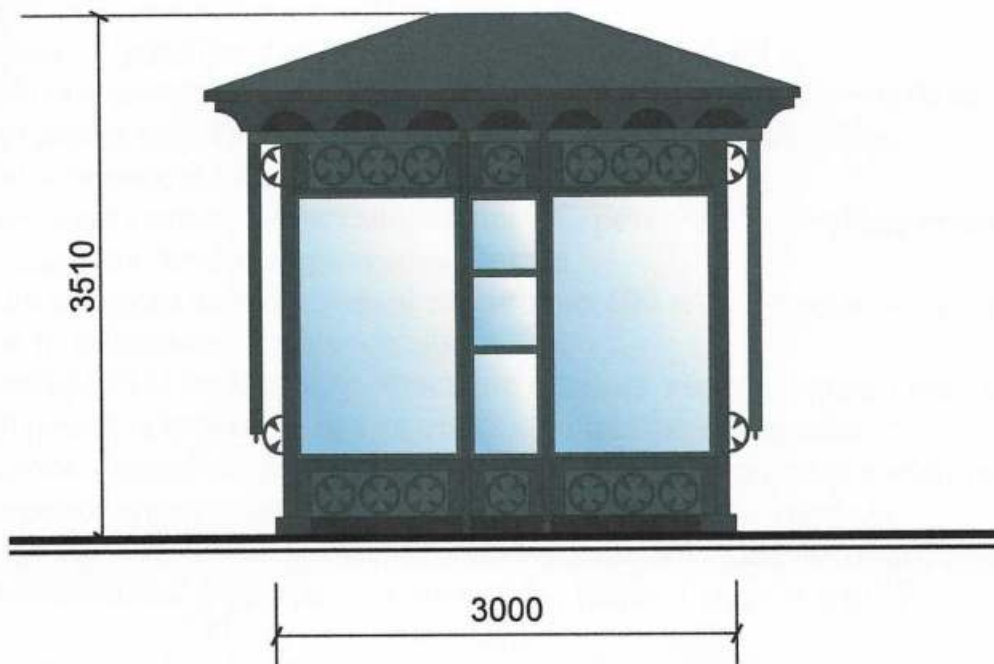

Бічний фасад ТС М 1:50

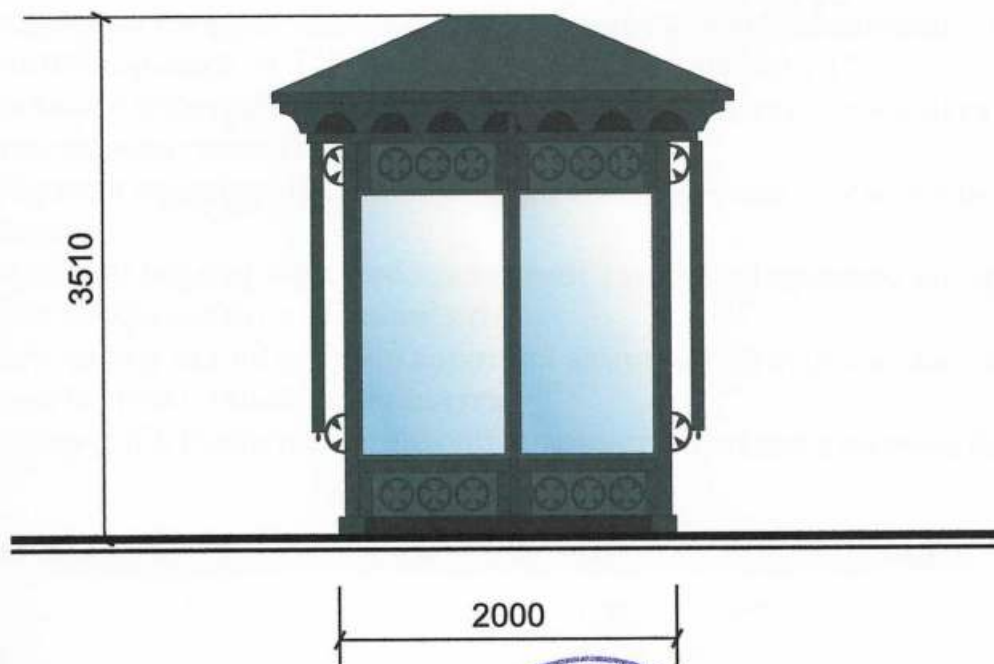

Директор ПП «АРХМАЙСТЕР»

Архітектор


Кваліфікаційний сертифікат серія АР №000262



Горбачова Н.В

Бойцова С.П

План ТС М 1:50

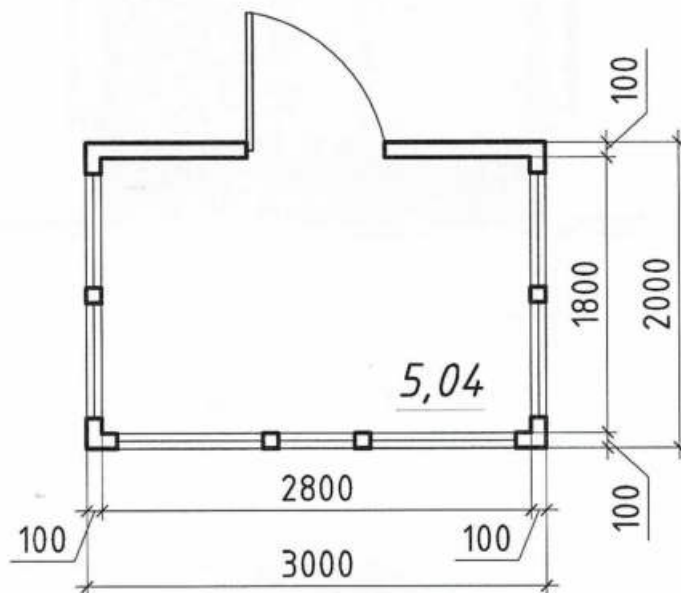

Директор ПП «АРХМАЙСТЕР»

Архітектор


Кваліфікаційний сертифікат серія АР №000262



Горбачова Н.В

Бойцова С.П

**Площа земельної ділянки згідно з документами
на землекористування - землі міста**

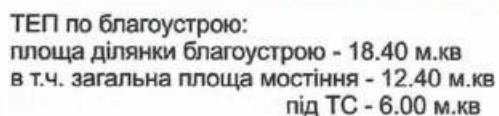

 - озеленення
 - тротуарна плитка
 - асфальтне покриття
 - урна

-  - межа благоустрою ділянки розміщення ТС
-  - проектна ТС
-  - існуючі будівлі
-  - існуючі дороги
-  - підключення до мереж електропостачання

Архітектор
Кваліфікаційний сертифікат серія АР №000262


Бойцова С.П



Ситуаційний план 1:2000

Місце розміщення об'єкту

С

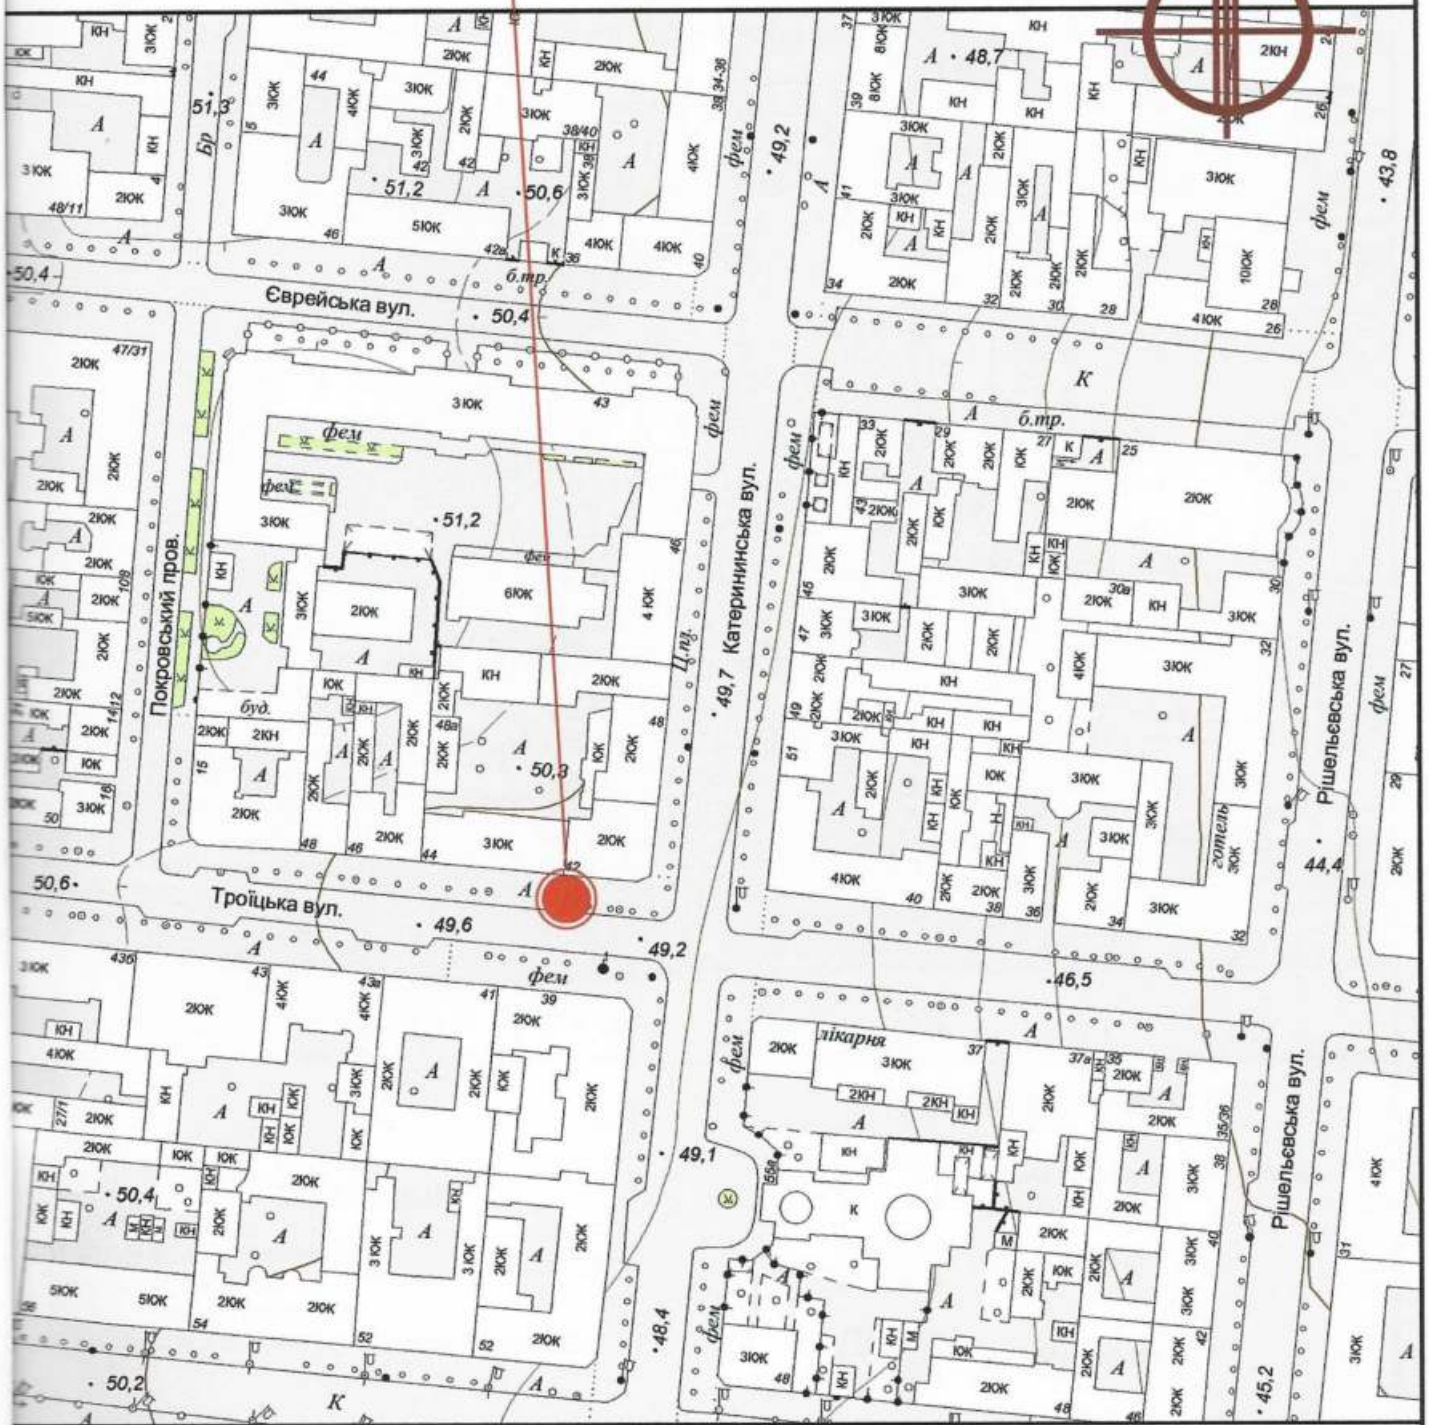

Директор ПП «АРХМАЙСТЕР»

Архітектор

Кваліфікаційний сертифікат серія АР №000262



Горбачова Н.В

Бойцова С.П