

СТИСЛА ПОЯСНЮВАЛЬНА ЗАПИСКА

1. Група стаціонарних тимчасових споруд для здійснення підприємницької діяльності, яка має торговельні приміщення для тимчасового перебування людей.

Ступінь вогнестійкості — IIIa

Павільйони мають неправильну форму,

Габаритні розміри групи у плані — 9.40м x 7.10м x 2.30м x 2.00м x 2.70м x 4.00м x 1.00м x 4.00м x 4.60м x 9.40м x 17.75м.

Площа забудови групи — 135.40м²

Площа твердого покриття групи — 135.40м²

Загальна площа групи — 124.65м²

Загальна висота групи — 4.00м

Внутрішня висота складає — 3.60м.

Ґрунт заснування, до встановлення ТС, ретельно утрамбовується щебенем та укладається тротуарна плитка.

Стіни споруди запроектовані товщиною 100 мм із сертифікованим утеплювачем із мінеральної вати та обшивкою з обох сторін.

Обшивка сторін по каркасу: зовнішня — по металевому каркасу композитні матеріали типу Алюкобонд, внутрішня (стіни та стеля) — пластикова вагонка

Підлога — дерев'яні дошки 40 мм по металевому каркасу з утеплювачем з пенополістерольних плит та покриттям антипіринами та антигрибковими засобами.

Покрівля — по металевим прогонам і решетуванню з покриттям профнастілом, з утеплювачем з мінераловатних плит.

Зовнішня обробка:

поверхні стін — композитні матеріали типу Алюкобонд.

Вікна та двері — металопластикові із вакуумними склопакетами, пофарбовані фарбою для ПФХ.

покрівля — профнастіл.

2. Група ТС підключається до мереж електропостачання згідно з чинними нормами та ТУ. Точка підключення згідно з ТУ.

Опалення - електричне з встановленням навісних електро-конвекторів з регулюванням температури.

Освітлення приміщення виконується світильниками з діодними лампами.

Розподільні мережі виконані проводами із мідними жилами, що прокладені у трубах та приховані в обшивці стін.

Захист мереж від дії струмів, коротких замикань та перевантажень здійснюється автоматичними вимикачами щитка. Передбачене заземлення.

3. Благоустрій прилеглої території виконується згідно з планом благоустрою, Освітлення території передбачене світильниками, що розміщуються на основному фасаді та над входом в ТС.


Директор ТОВ "Архітектурне Бюро "АРКАДІЯ"
Архітектор

Кваліфікаційний сертифікат серія АА №002590




Смаглій Д.П.
Глінін Д.Ю.

ЕСКІЗИ ФАСАДІВ ГРУПИ СТАЦІОНАРНИХ ТС Головний фасад групи стаціонарних ТС М 1:100

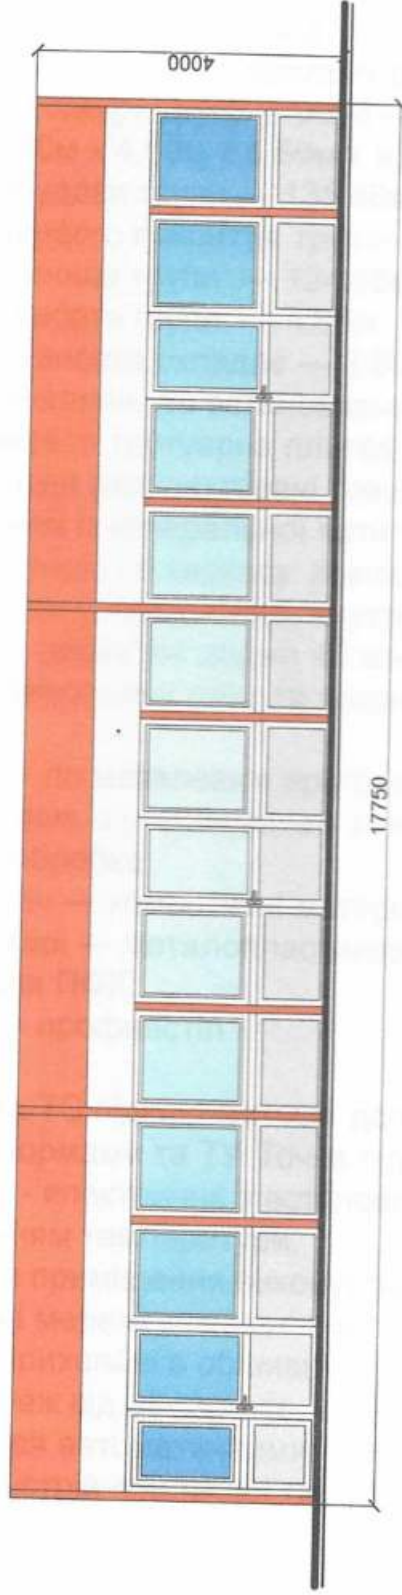

Бічний фасад групи стаціонарних ТС М 1:100

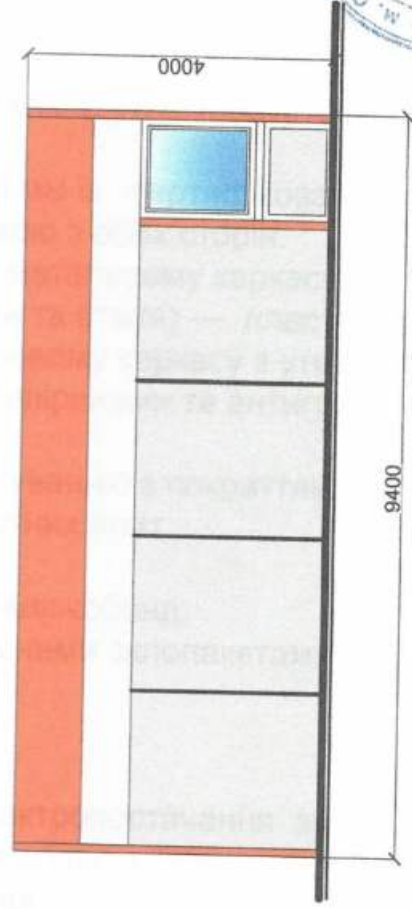

Директор ТОВ "Архітектурне Бюро "Аркадія"

Архітектор

Кваліфікаційний сертифікат серія АА №002560

Смаглій Д.П.

Глінін Д.Ю.

The floor plan shows a building with an overall width of 9400 and a total length of 7100. The plan is divided into several rooms and corridors. Key dimensions and area calculations are as follows:

- Top Left Room:** Dimensions 4650 (width) x 5000 (length). Internal width is 4450. Area: 20,25. Wall thickness is 100. There are two 900 wide openings on the top wall.
- Top Right Room:** Dimensions 6500 (width) x 5200 (length). Area: 26,83. Wall thickness is 100. There are two 900 wide openings on the right wall.
- Bottom Left Room:** Dimensions 6900 (width) x 3500 (length). Internal width is 6300. Area: 21,34. Wall thickness is 100. There is one 900 wide opening on the left wall.
- Bottom Right Room:** Dimensions 5950 (width) x 5200 (length). Area: 27,44. Wall thickness is 100. There are two 900 wide openings on the right wall.
- Central Corridor:** Dimensions 4000 (width) x 4900 (length). Area: 27,00. Wall thickness is 100.
- Overall Dimensions:** Total width is 9400. Total length is 7100.

The plan also includes a circular stamp on the right side with the text "Україна" (Ukraine) and a scale bar indicating 17750.

Смаглій Д.П.

Глінін Д.Ю.

Кваліфікаційний сертифікат серія АА №002590



СХЕМА РОЗМІЩЕННЯ ГРУПИ СТАЦІОНАРНИХ ТС М 1:200

Площа земельної ділянки згідно з документами на
землекористування - землі міста



Умовні позначення:

- | | | | |
|--|------------------------------|--|--|
| | - існуючі газони | | - межа благоустрою ділянки розміщення ТС |
| | - існуюча тротуарна плитка | | - існуюча ТС |
| | - існуюче асфальтне покриття | | - існуючі будівлі |
| | - урна | | - існуючі дороги |
| | - вуличний ліхтар | | |

Директор ТОВ "Архітектурне Бюро "Аркадія"

Архітектор

Кваліфікаційний сертифікат серія АА №002590



"АРХІТЕКТУРНЕ БЮРО "АРКАДІЯ" Смальцій Д.П.

Глінін Д.Ю.

Місце розміщення об'єкту



Кваліфікаційний сертифікат серія АА №002590

"АРХІТЕКТУРНЕ" Смаглій Д.П.

Гелінін Д.Ю.

