

СТИСЛА ПОЯСНЮВАЛЬНА ЗАПИСКА

1. Група стаціонарних тимчасових споруд для здійснення підприємницької діяльності, яка має торговельні приміщення для тимчасового перебування людей.

Ступінь вогнестійкості — IIIa

павільйони мають неправильну форму, наближену до трикутної.

Габаритні розміри групи у плані — 0.70м x 9.40м x 8.40м x 12.20м.

Площа забудови групи — 42.80м²

Площа твердого покриття групи — 42.80м²

Загальна площа групи — 38.70м²

Загальна висота групи — 3.00 м

Внутрішня висота складає — 2.60м.

Ґрунт заснування, до встановлення ТС, ретельно утрамбовується щебенем та укладається тротуарна плитка.

Стіни споруди запроектовані товщиною 100 мм із сертифікованим утеплювачем із мінеральної вати та обшивкою з обох сторін.

Обшивка сторін по каркасу: зовнішня — по металевому каркасу композитні матеріали типу Алюкобонд, внутрішня (стіни та стеля) — пластикова вагонка

Підлога — дерев'яні дошки 40 мм по металевому каркасу з утеплювачем з пенополістерольних плит та покриттям антипіринами та антигрибковими засобами.

Покрівля — по металевим прогонам і решетуванню з покриттям профнастілом, з утеплювачем з мінераловатних плит.

Зовнішня обробка:

поверхні стін — композитні матеріали типу Алюкобонд.

Вікна та двері — металопластикові із вакуумними склопакетами, пофарбовані фарбою для ПФХ.

покрівля — профнастіл.

2. Група ТС підключається до мереж електропостачання згідно з чинними нормами та ТУ. Точка підключення згідно з ТУ.

Опалення - електричне з встановленням навісних електро-конвекторів з регулюванням температури.

Освітлення приміщення виконується світильниками з діодними лампами.

Розподільні мережі виконані проводами із мідними жилами, що прокладені у трубах та приховані в обшивці стін.

Захист мереж від дії струмів, коротких замикань та перевантажень здійснюється автоматичними вимикачами щитка. Передбачене заземлення.

3. Благоустрій прилеглої території виконується згідно з планом благоустрою. Освітлення території передбачене світильниками, що розміщуються на основному фасаді та над входом в ТС.


Директор ТОВ "Архітектурне Бюро "АРКАДІЯ"
Архітектор

Кваліфікаційний сертифікат серія АА №002590




Смаглій Д.П.
Глінін Д.Ю.

ЕСКІЗИ ФАСАДІВ ГРУПИ СТАЦІОНАРНИХ ТС
Головний фасад групи стаціонарних ТС М 1:50

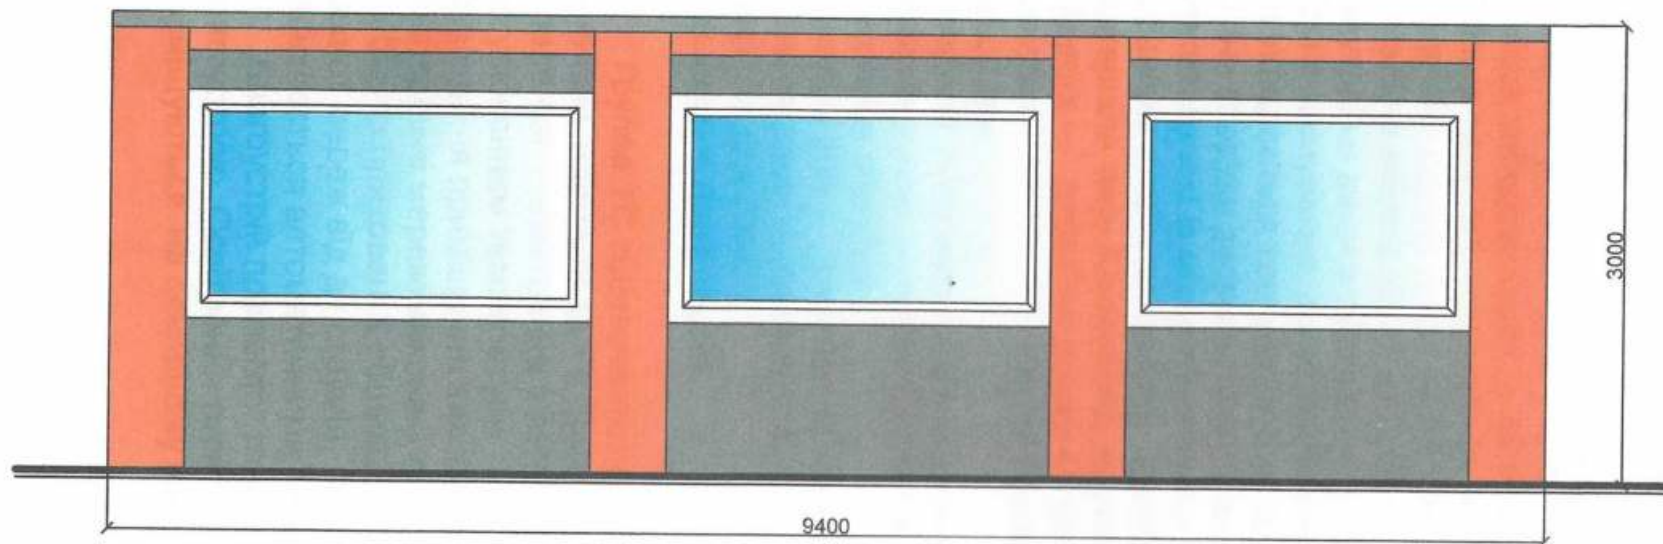

Бічний фасад групи стаціонарних ТС М 1:50

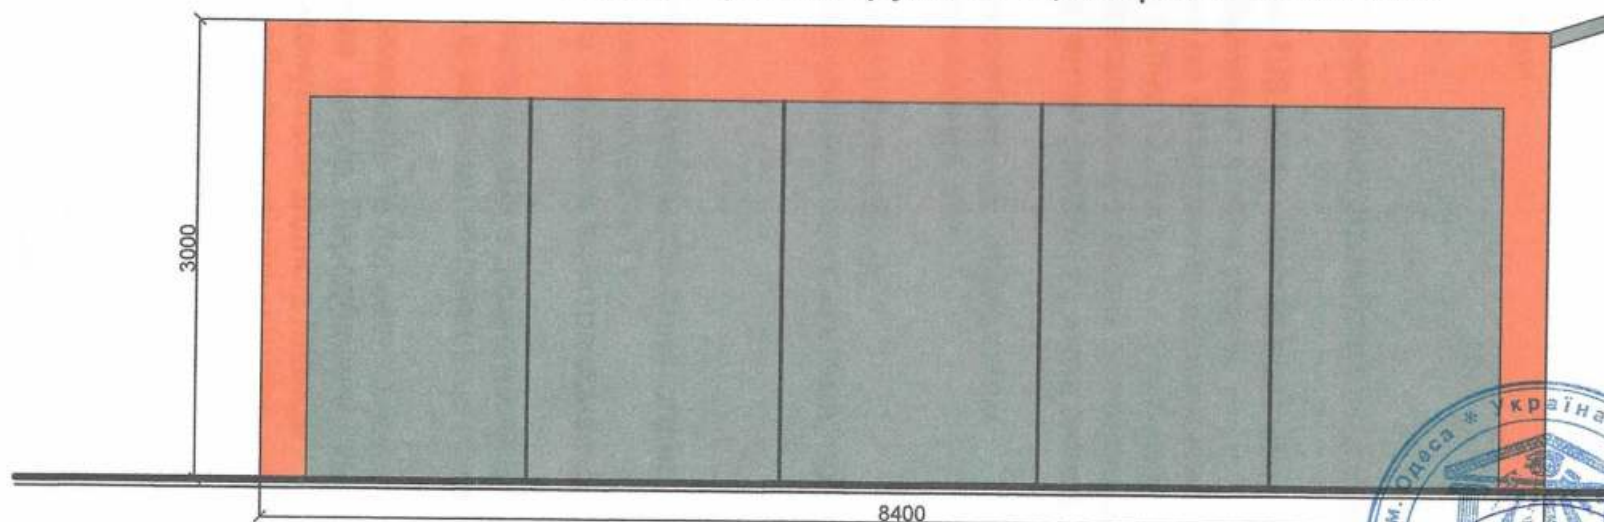

Директор ТОВ "Архітектурне Бюро "Аркадія"

Архітектор

Кваліфікаційний сертифікат серія АА №002590



Смаглій Д.П.

Глінін Д.Ю.

ПЛАНИ УНИ ТАЦІОНАРНИХ ІС М 1:50

700 100 100 4190 9400 100 100 2640 2170 3180 100 100 4790 6925 900 900 12200 100 900 15,60 13,60 9,51

ОВ "Архітектура Бюро " Аркадія"

Ідентифікат серія АА №002590

М. Оdesa * Україна * Товариство

"АРХІТЕКТУРНЕ БЮРО "АРКАДІЯ"

Ідент. код 40175885

Смаглій Д.П.


Глінін Д.Ю.

Кваліфікаційний сертифікат серія АА №002590



Глінін Д.Ю.

Площа земельної ділянки згідно з документами на
землекористування - землі міста

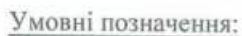


- | | | | |
|---|------------------------------|---|--|
|  | - існуючі газони |  | - межа благоустрою ділянки розміщення ТС |
|  | - існуюча тротуарна плитка |  | - існуюча ТС |
|  | - існуюче асфальтне покриття |  | - існуючі будівлі |
|  | - урна |  | - існуючі дороги |
|  | - вуличний ліхтар | | |

Кваліфікаційний сертифікат серія АА №002490

Глінін Д.Ю.

СИТУАЦІЙНИЙ ПЛАН М 1:2000

Місце розміщення об'єкту

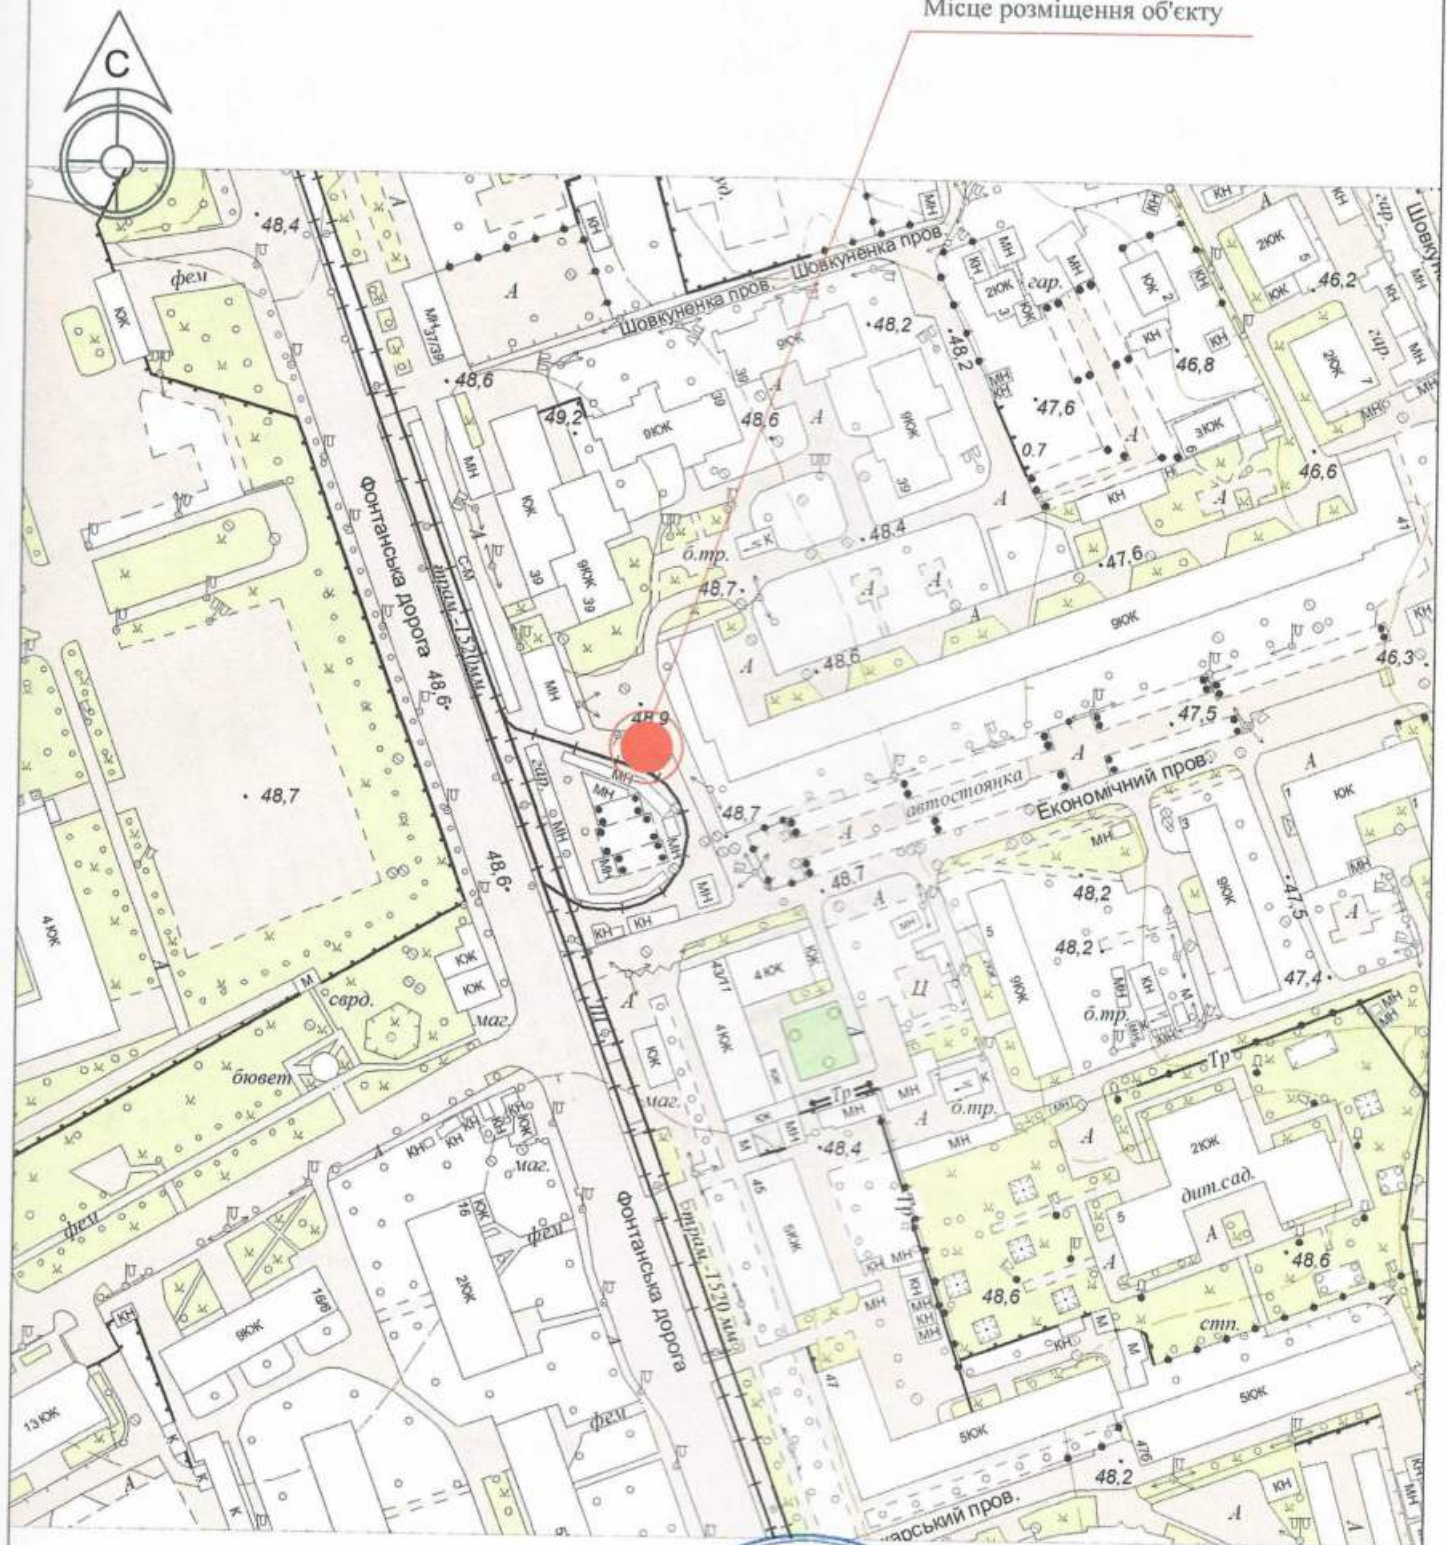

Директор ТОВ "Архітектурне Бюро "Аркадія"

Архітектор

Кваліфікаційний сертифікат серії АА №002590



Смаглій Д.П.

Глінін Д.Ю.