

## СТИСЛА ПОЯСНЮВАЛЬНА ЗАПИСКА

1. Група стаціонарних тимчасових споруд для здійснення підприємницької діяльності має торгівельні приміщення для тимчасового перебування людей. За умовну позначку  $\pm 0.000$  прийнятий рівень чистої підлоги ТС.

Ступень вогнестійкості - Ша.

Габарити павільйона прямокутної форми,  
розміри у плані - 18,0 м x 3,0 м.

Загальна площа ТС - 8,07 м<sup>2</sup>; 8,07 м<sup>2</sup>; 8,07 м<sup>2</sup>; 8,07 м<sup>2</sup>; 8,07 м<sup>2</sup>; 8,07 м<sup>2</sup>.

Площа твердого покриття - 54,0 м<sup>2</sup>.

Внутрішня висота від рівня чистої підлоги складає - 2,6м.

Загальна висота складає - 3,2м.

Грунт заснування, до встановлення ТС, ретельно утрамбовується щебнем та укладається бетонна тротуарна плитка.

Стіни споруди запроектовані товщиною 100 мм із утеплювачем з мінеральної вати та обшивкою з обох сторін.

Обшивка стін по каркасу. Фасадне скління з вакуумними склопакетами, внутрішня обробка (стіни та стеля) - пластикова вагонка.

Підлога - дерев'яні дошки 40 мм по металевому каркасу з утеплювачем з мінераловатних плит та покриттям з негорючого матеріалу.

Покрівля - по металевим прогонам і решетуванню з покриттям листами оцинкованою покрівельною сталлю, з утеплювачем з мінераловатних плит, гідро- і пароізоляцією.

### Зовнішня обробка:

поверхні стін - фасадне скління з вакуумними склопакетами, обшивка металевий лист для зовнішніх робіт,

покрівля - оцинкована покрівельна сталь.

2. Тимчасова споруда підключається до мереж електропостачання згідно з діючими нормами та ТУ. Точка підключення - згідно з ТУ.

Опалення - електричне з встановленням навісних електро-конвекторів з регулюванням температури.

Освітлення приміщення виконується світильниками з люмінесцентними лампами.

Розподільні мережі виконані проводами з мідними жилами, що прокладені у трубах та приховані в обшивці стін.

Захист мереж від дії струмів коротких замикань та перевантажень здійснюється автоматичними вимикачами щитка.

3. Благоустрій прилеглої території виконується згідно з планом благоустрою. Освітлення території передбачене світильником, що розміщується на головному фасаді над входом у ТС.

Директор ПП «АРХМАЙСТЕР»

Архітектор


Кваліфікаційний сертифікат серія АР №002730




Кіслякова О.М

Бойцова С.П

ЕСКІЗИ ФА  
Головний фаса

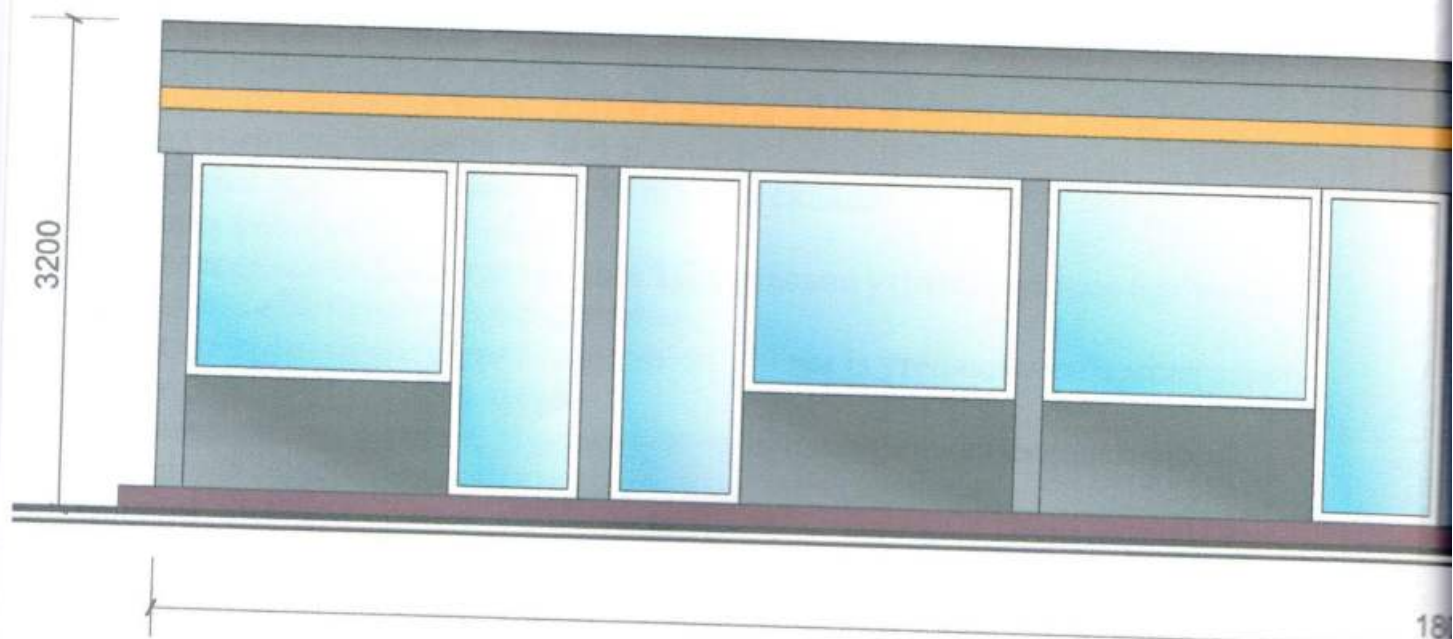


Бічний фасад Т

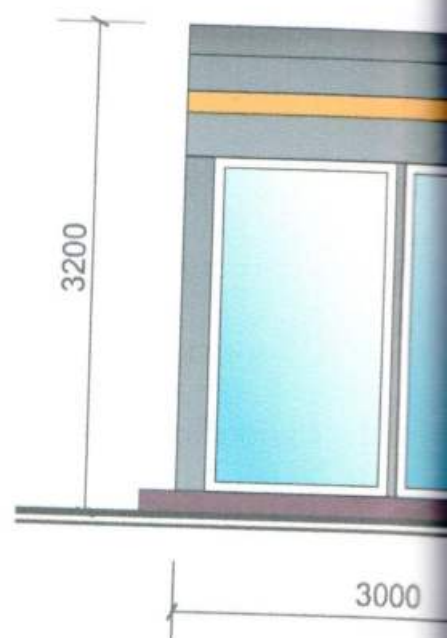

САДІВ ТС

ад ТС М 1:50

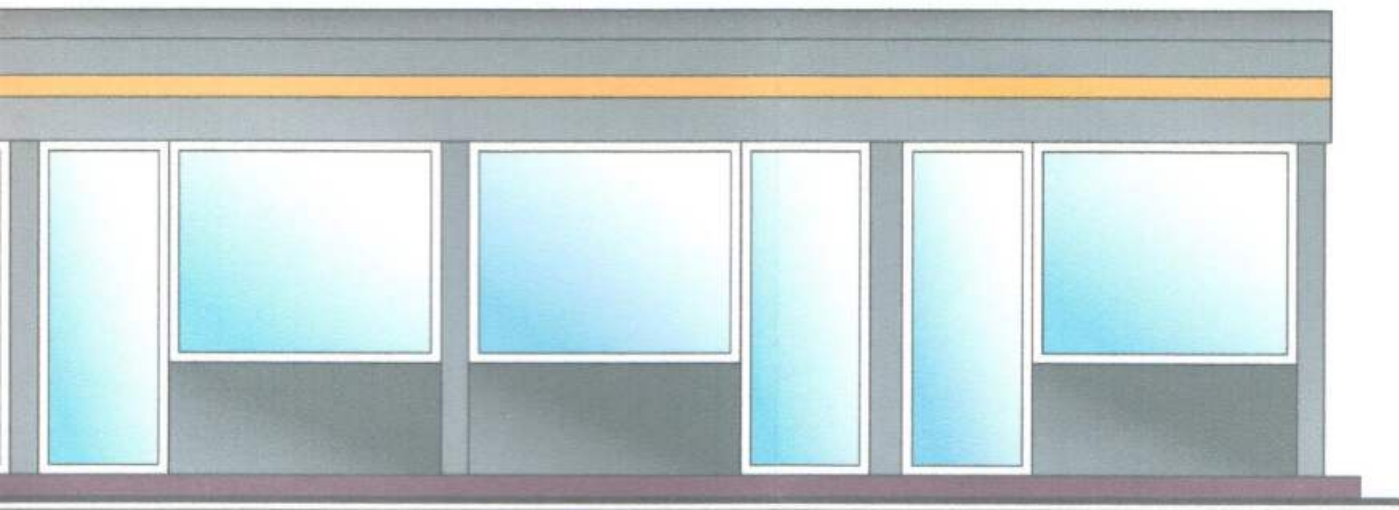

8000

ТС М 1:50



00

Директор ПП «АРХМАЙСТЕР»

Архітектор


Кваліфікаційний сертифікат серія АР №002730



Кіслякова О. М.


Бойцова С.П

План 7

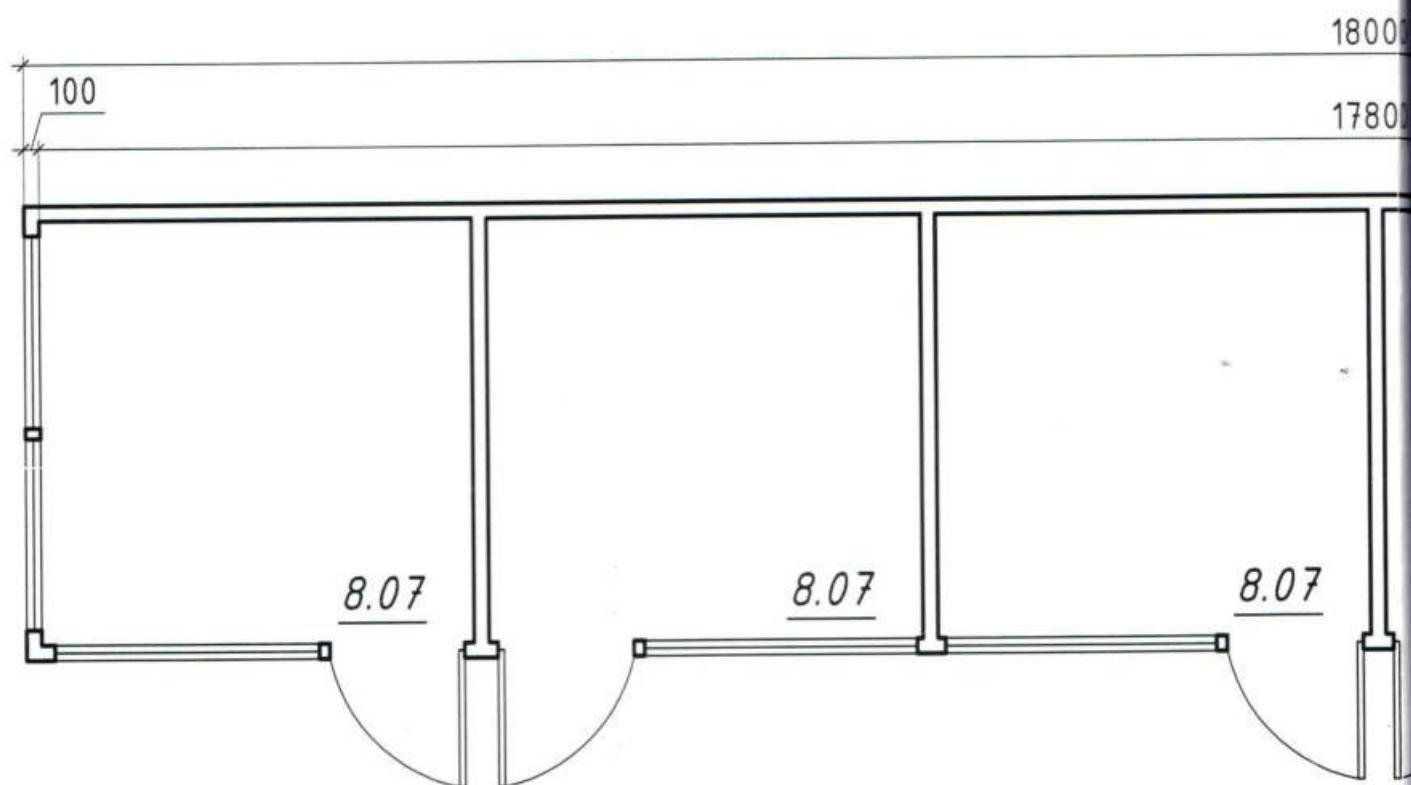



ТС М 1:50

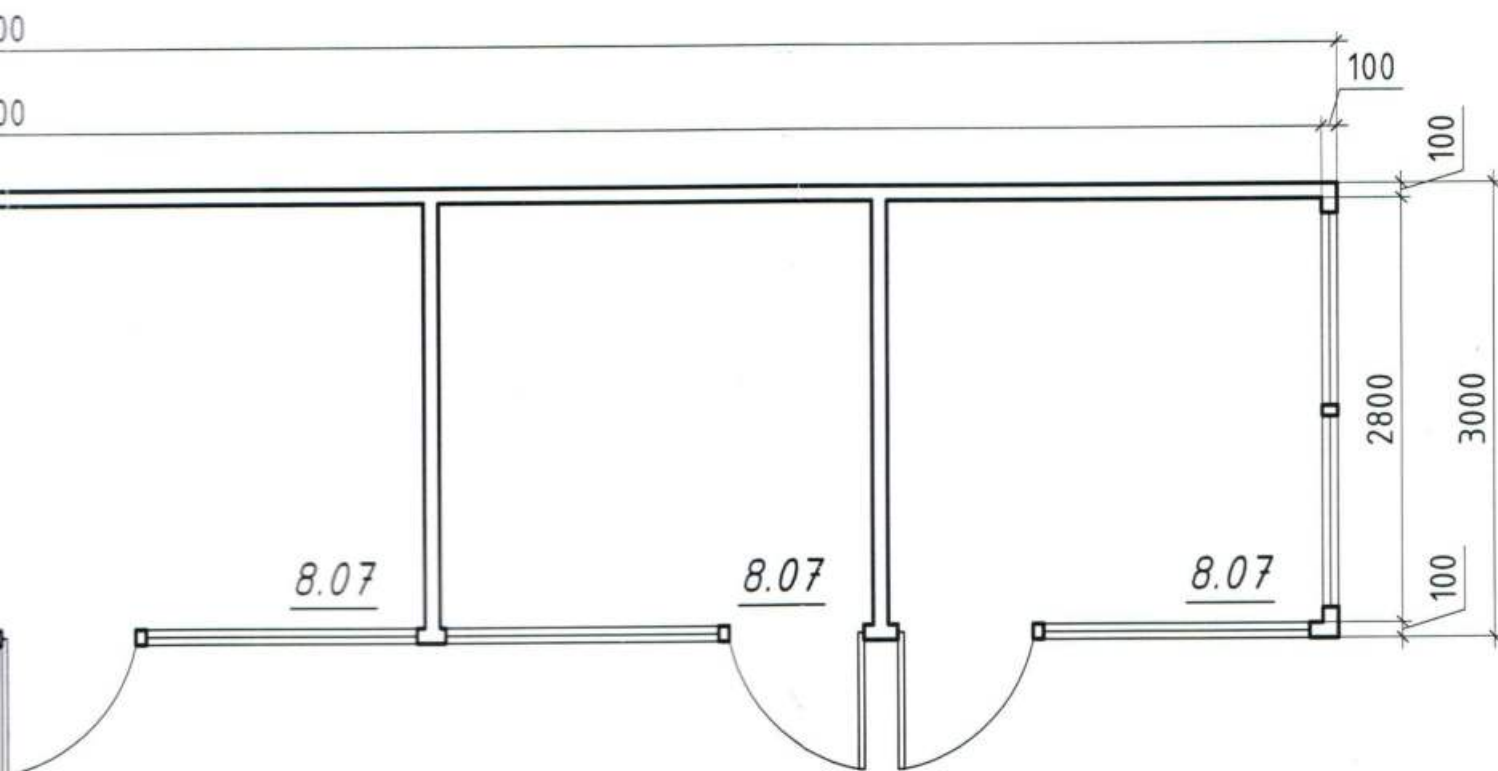

Директор ПП «АРХМАЙСТЕР»

Архітектор

Кваліфікаційний сертифікат серія АР №002730




Кіслякова О.М

Бойцова С.П

# СХЕМА РОЗМІЩЕННЯ ТС М 1:200

Площа земельної ділянки згідно з документами  
на землекористування - землі міста

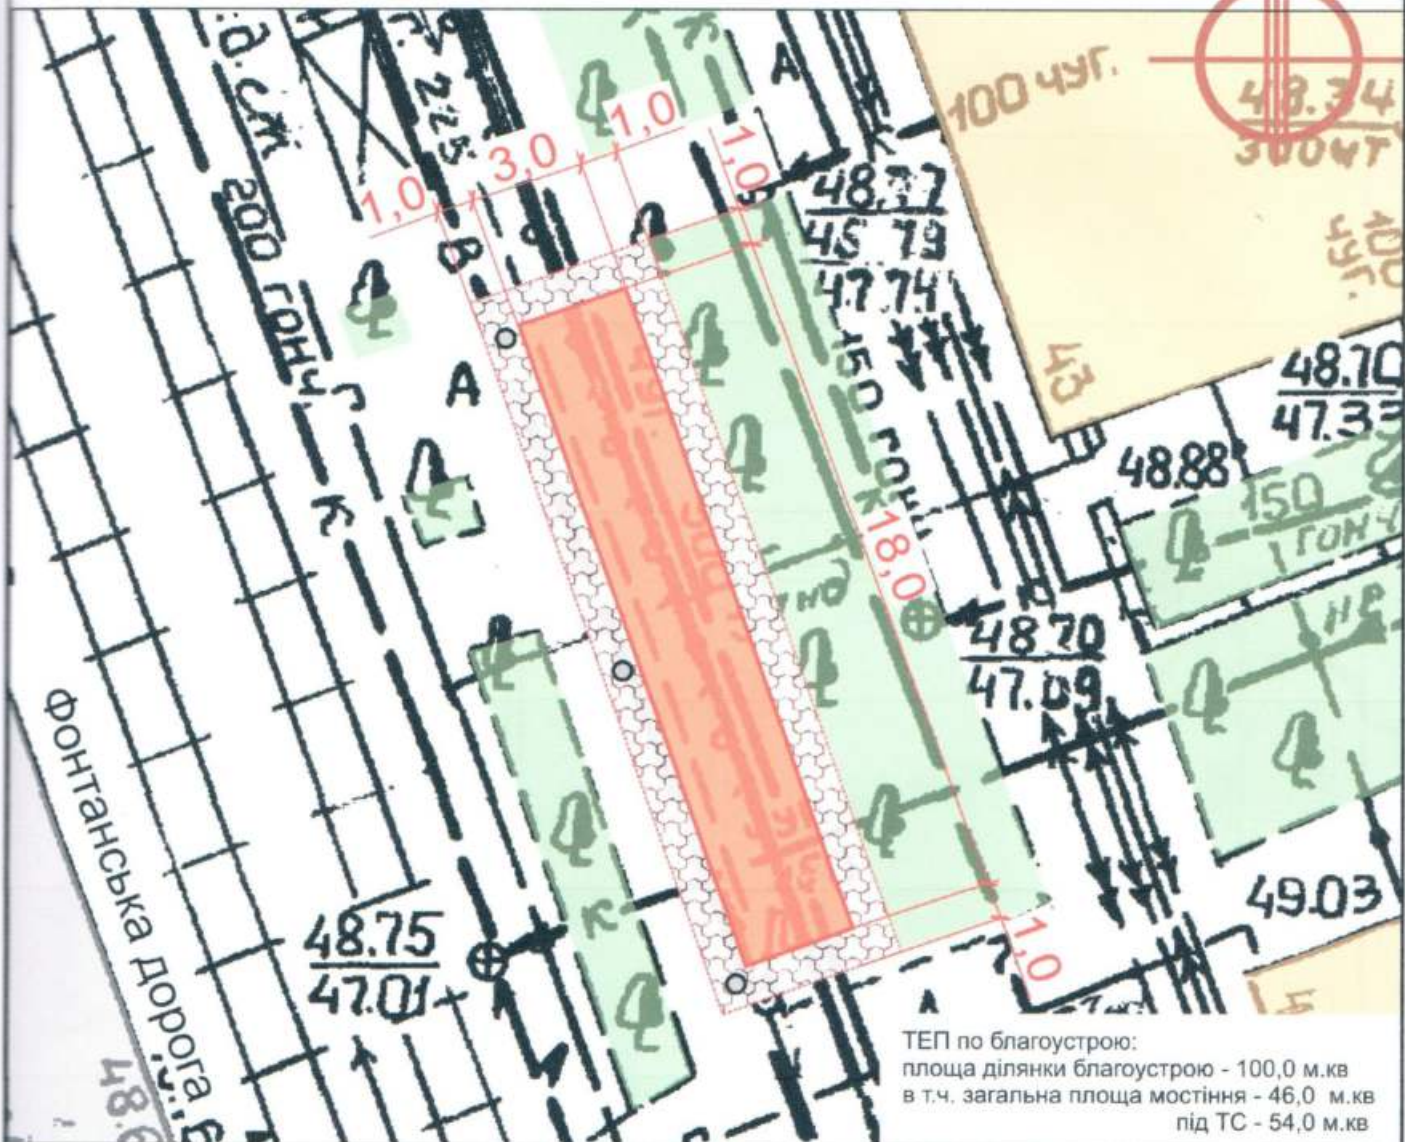

## Умовні позначення:



- озеленення



- тротуарна плитка



- асфальтне покриття




- урна



- межа благоустрою ділянки  
розміщення ТС



- проектна ТС

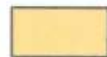

- існуючі будівлі



- існуючі дороги



- підключення до мереж  
електропостачання

Директор ПП «АРХМАЙСТЕР»

Архітектор

Кваліфікаційний сертифікат серія АР №002730



Кіслякова О.М

Бойцова С.П



Місце розміщення об'єкту



Кваліфікаційний сертифікат серія АР №002730



Бойцова С.П