

ПОЯСНЮВАЛЬНА ЗАПИСКА

1. Група тимчасових споруд (ТС) для здійснення підприємницької діяльності має закриті приміщення для тимчасового перебування людей.

За умовну позначку 0.000 прийнятий рівень чистої підлоги ТС.

Ступінь вогнестійкості - IIIа.

Тимчасових споруд - 5 штук.

Площа забудови, всього - 70.80м²

Площа загальна, всього - 63.28м².

Внутрішня висота кіосків від рівня чистої підлоги складає - 2.50м.

Загальна висота - 3.00м.

Стіни споруд запроектовані по типу «Сендвич», товщиною 100мм із утеплювачем з мінеральної вати й обшивкою.

Обшивка стін по каркасу: зовнішня - алюмінієві сендвіч панелі; внутрішня (стіни й стеля) - вагонка.

Підлога з покриттям дошки 40мм і утеплювачем (керамзитовий ґравій - 200мм) та покриття з негорючого матеріала.

Покрівля - по металевим прогонам і решетуванню з покриттям із профільованого сталевих листа, з утеплювачем з мінераловатних плит, гідро- і пароізоляцією.

Зовнішня обробка.

поверхні стін - колірні алюмінієві сендвіч панелі, типа «Алюкобонд».

вікна - металопластикові;

двері - металопластикові;

покрівля - колірний металевий профнастил алюмінієві сендвіч панелі;

цоколь - колірні сендвіч-панелі.

2. Стационарна група тимчасових споруд підключається до мереж електропостачання згідно з діючими нормами та ТУ. Точка підключення - близька опора, що розташована поряд з територією ділянки.

Опалювання - електричне з встановленням навісних електро-конвекторів з регулюванням температури.

Як розподільний щиток у павільонах встановлюється щиток серії NRL-1F6ZS з лічильником активної енергії й автоматичних вимикачів на лініях, що відходять.

Освітлення приміщень виконується стельовими світильниками з люмінесцентними лампами.

Розподільні мережі споруд, виконані проводами з мідними жилами, що прокладні у трубах та приховані в обшивці стін. Мережі обрані по тривалодопустимим струмам навантаження.

Захист мереж від дії струмів коротких замикань і перевантаження здійснюється автоматичними вимикачами щитка.


3. Стационарна тимчасова група підключена до існуючих мереж зовнішнього господарсько-питного водопостачання, згідно ТУ.

Водовідведення господарсько-побутових стоків передбачено відповідно ТУ за погодженням санітарно-епідеміологічної служби міста.


Назва об'єкту, адреса розміщення	Посада виконавця	ІПБ	Підпис
Група стаціонарних тимчасових споруд, вул.Фонтанська дорога, 63	ГАП архітектор	Ігнатова Л.А. Чабан Л.В.	
М.П. 	Кваліфікаційний сертифікат серія АА № 000199		
	Дата складання "22" 10. 2014 року		

ЕСКІЗИ ФАСАДІВ ТС, М 1:50

Головний фасад

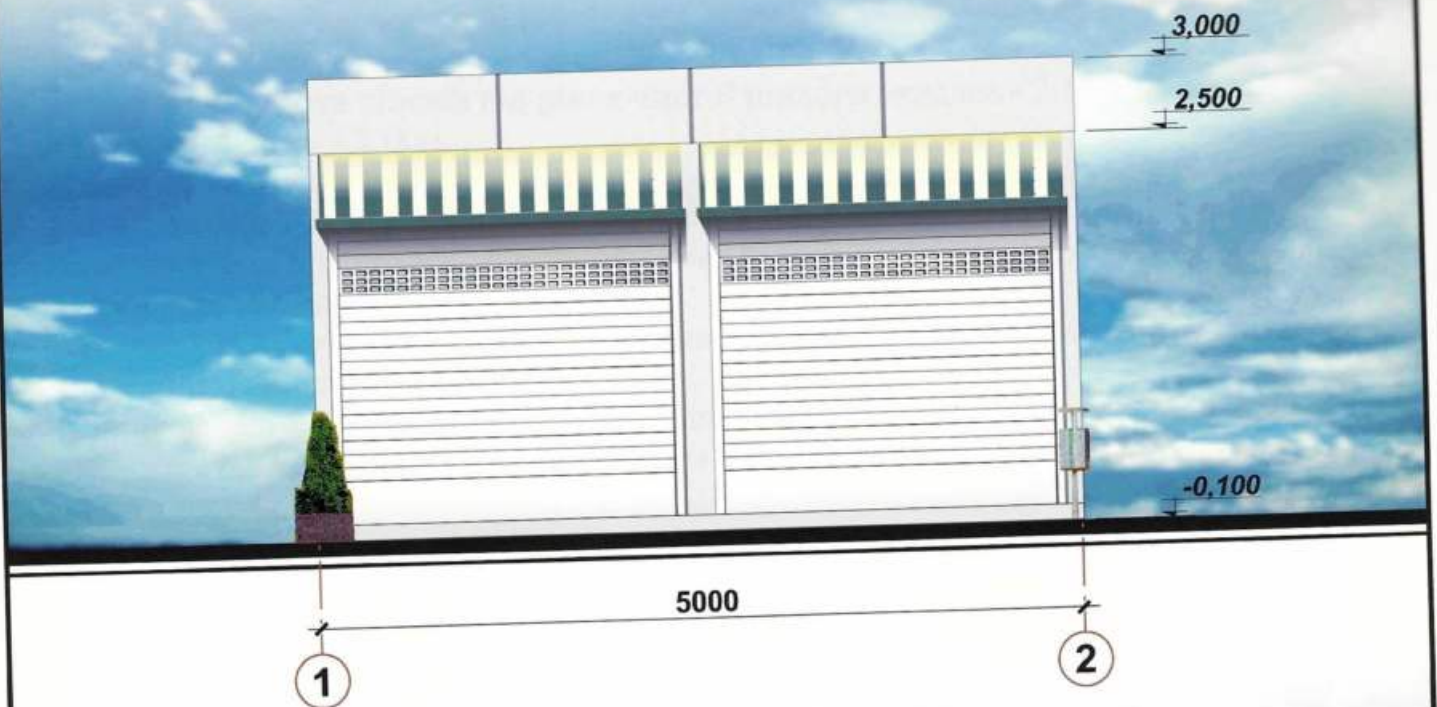


Боковий фасад

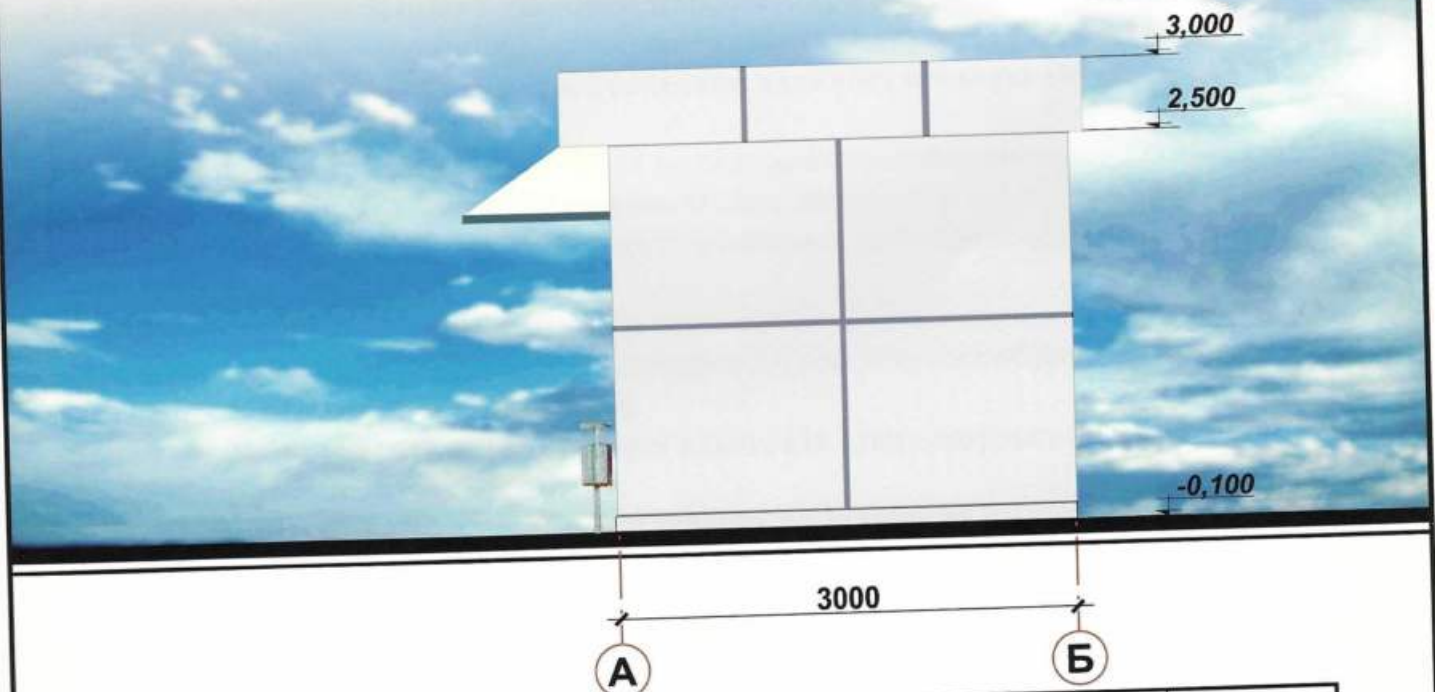

Назва об'єкту, адреса розміщення	Посада виконавця	ПІБ	Підпис
Група стаціонарних тимчасових споруд, вул.Фонтанська дорога, 63	ГАП архітектор	Ігнатова Л.А. Чабан Л.В.	
М.П. 	Кваліфікаційний сертифікат серія АА № 000199 Дата складання "22" 10. 2014 року		

СХЕМА РОЗМІЩЕННЯ ТС М 1:500

Площа земельної ділянки згідно з документами на землекористування
Город земель фонд земля м.Одеси

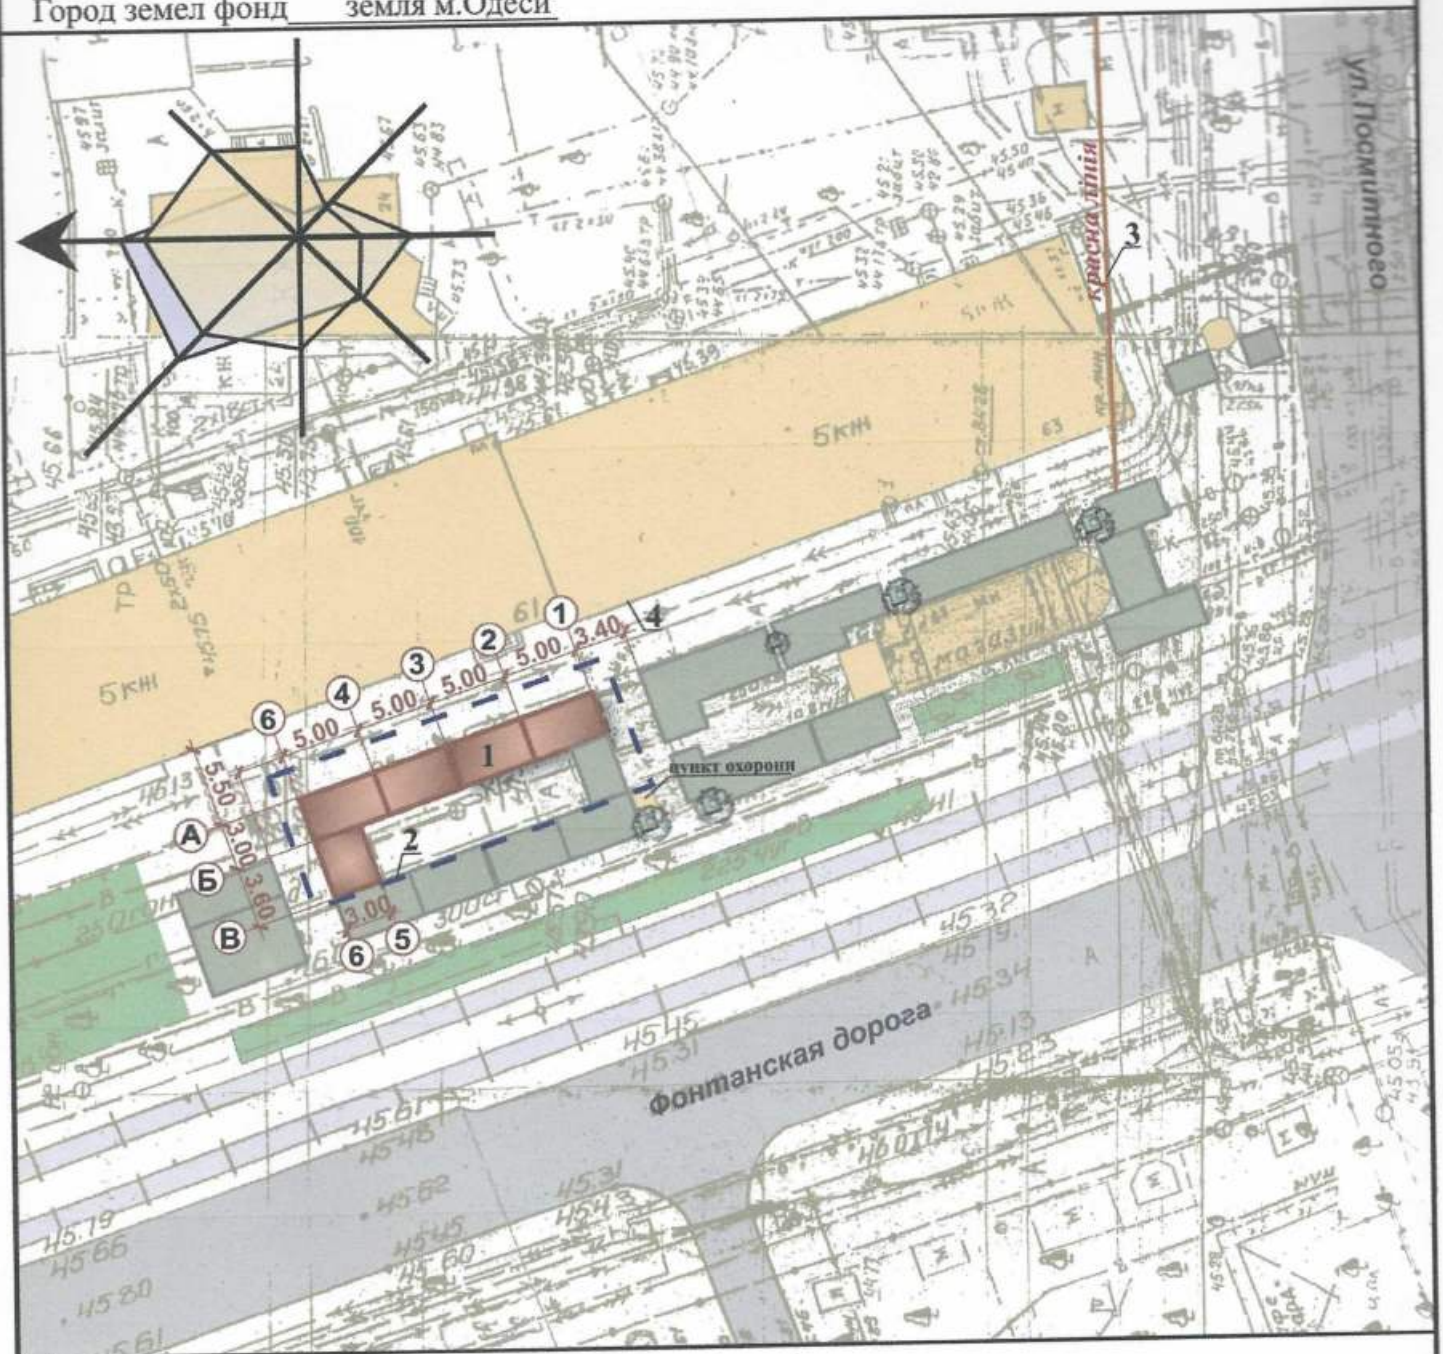

Експлікація:


- 1) місце розташування групи ТС; 3) червоні лінії;
2) лінії регулювання забудови; 4) місця підключення до інженерних мереж.

Умовні позначення:

- об'єкт проектування (ТС)
 - існуючі дороги.
 - територія благоустрою
- існуючі будівлі та споруди.
 - озеленення.
 - існуючі групи ТС ПП «ЮЛІС»

Назва об'єкту, адреса розміщення	Посада виконавця	ПІБ	Підпис
Група стаціонарних тимчасових споруд, вул.Фонтанська дорога, 63	ГАП архітектор	Ігнатова Л.А. Чабан Л.В.	
М.П.			
Кваліфікаційний сертифікат серія АА № 000199			
Дата складання "22" 10. 2014 року			

СИТУАЦІЙНИЙ ПЛАН, М 1:2000

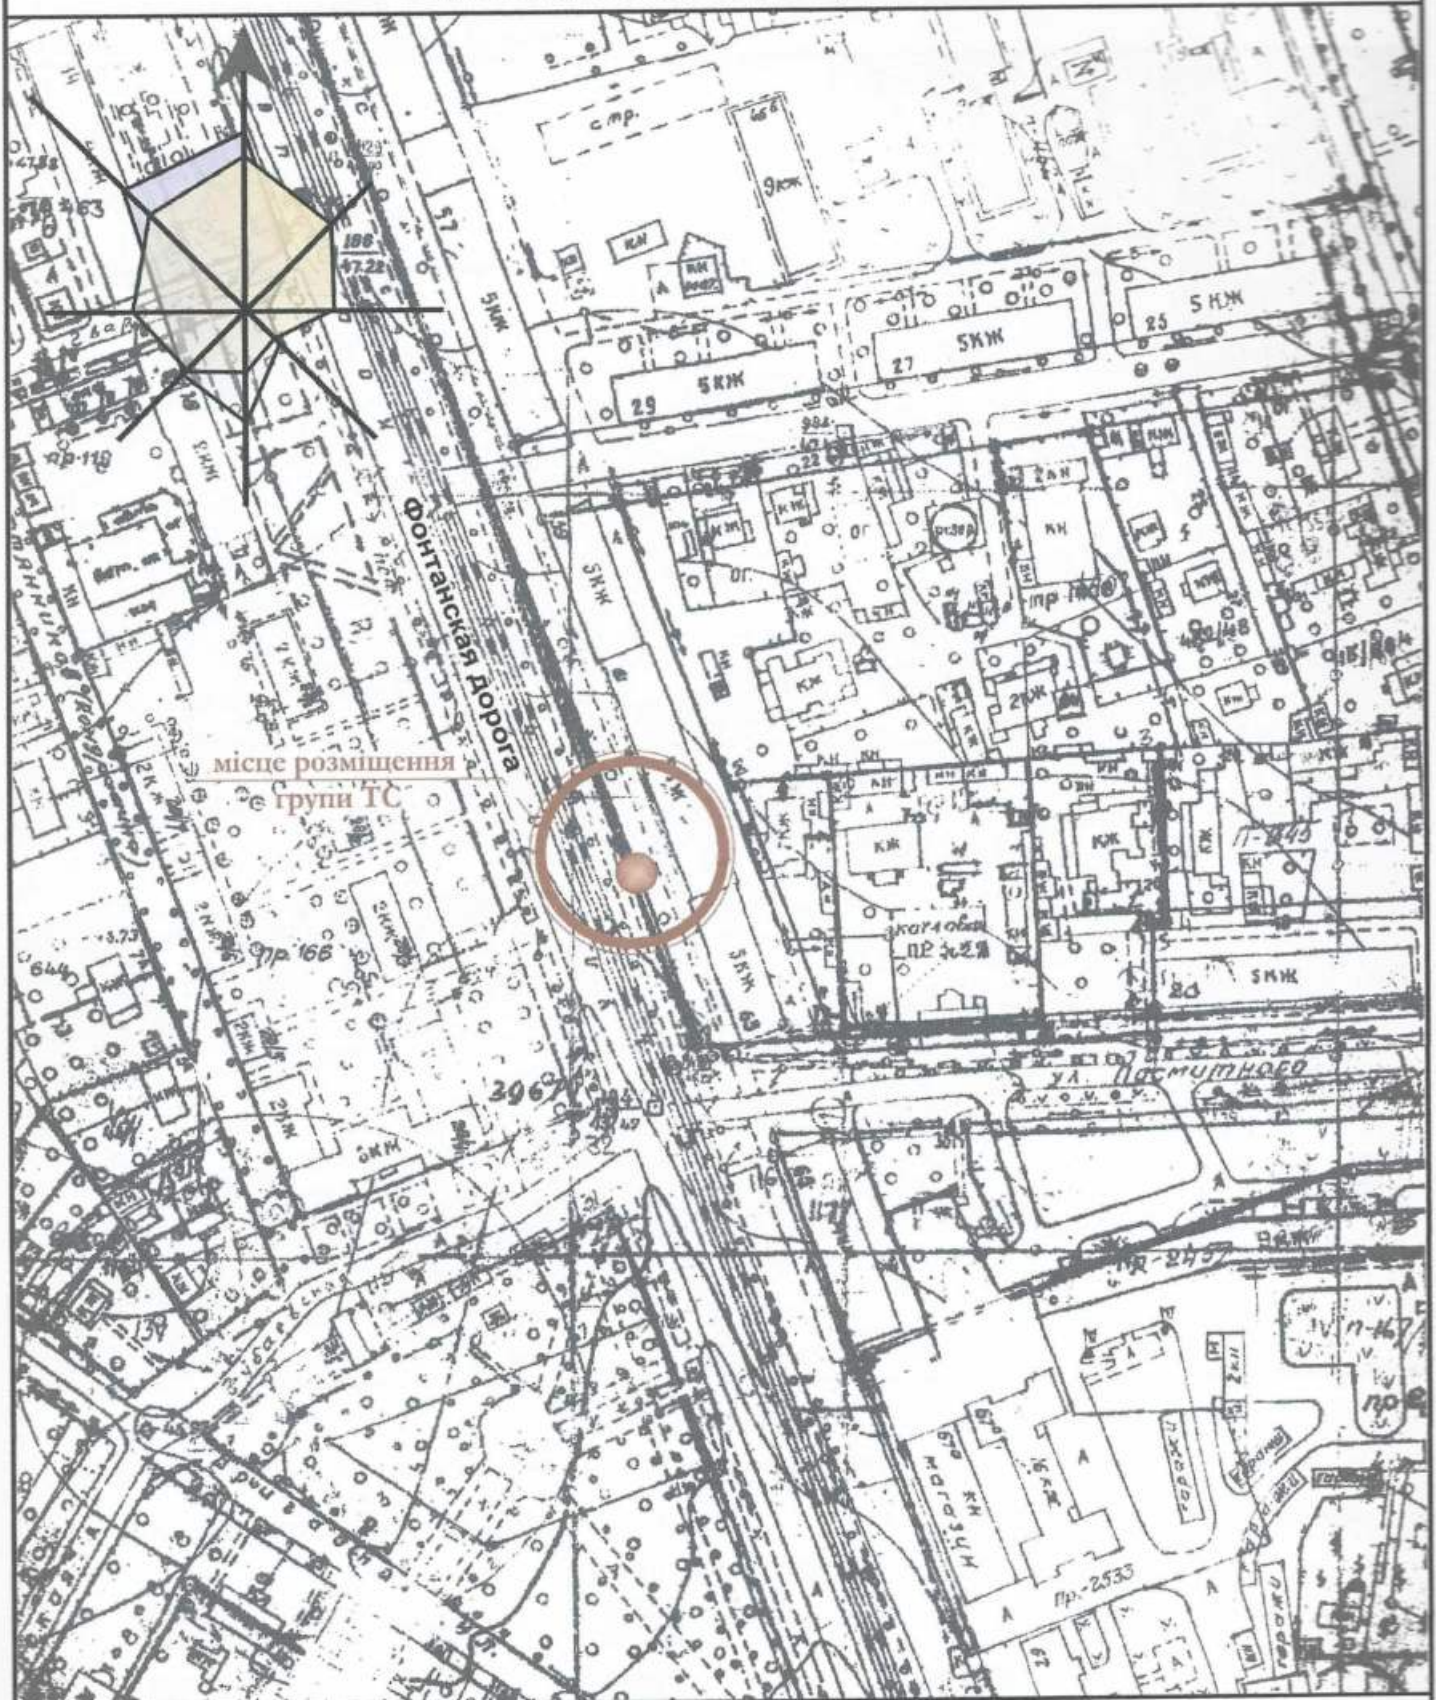

Назва об'єкту, адреса розміщення Група стаціонарних тимчасових споруд, вул.Фонтанська дорога, 63	Посада виконавця ГАП архітектор	ПІБ Ігнатова Л.А. Чабан Л.В.	Підпис 
М.П. 	Кваліфікаційний сертифікат серія АА № 000199 Дата складання "22" 10. 2014 року		