

## ПОЯСНЮВАЛЬНА ЗАПИСКА

1. Група тимчасових споруд (ТС) для здійснення підприємницької діяльності має закриті приміщення для тимчасового перебування людей.

За умовну позначку 0.000 прийнятий рівень чистої підлоги ТС.

Ступінь вогнестійкості - IIIа.

Тимчасових споруд - 5 штук.

Площа забудови, всього - 70.00м<sup>2</sup>

Площа загальна, всього - 62.50м<sup>2</sup>.

Внутрішня висота кіосків від рівня чистої підлоги складає - 2.50м.

Загальна висота - 3.00м.

Стіни споруд запроектовані по типу «Сендвич», товщиною 100мм із утеплювачем з мінеральної вати й обшивкою.

Обшивка стін по каркасу: зовнішня - алюмінієві сендвіч панелі;

внутрішня (стіни й стеля) - вагонка.

Підлога з покриттям дошки 40мм і утеплювачем (керамзитовий гравій - 200мм) та покриття з негорючого матеріала.

Покрівля - по металевим прогонам і решетуванню з покриттям із профільованого сталевих листа, з утеплювачем з мінераловатних плит, гидро- і пароізоляцією.

### Зовнішня обробка.

**поверхні стін** - колірні алюмінієві сендвіч панелі, типа «Алюкобонд».

**вікна** - металопластикові;

**двері** - металопластикові;

**покрівля** - колірний металевий профнастил алюмінієві сендвіч панелі;

**цоколь** - колірні сендвіч-панелі.

2. Стационарна група тимчасових споруд підключається до мереж електропостачання згідно з діючими нормами та ТУ. Точка підключення - близька опора, що розташована поряд з територією ділянки.

Опалювання - електричне з встановленням навісних електро-конвекторів з регулюванням температури.

Як розподільний щиток у павільйонах встановлюється щиток серії NRL-1F6ZS з лічильником активної енергії й автоматичних вимикачів на лініях, що відходять.

Освітлення приміщень виконується стельовими світильниками з люмінесцентними лампами.

Розподільні мережі споруд, виконані проводами з мідними жилами, що прокладні у трубах та приховані в обшивці стін. Мережі обрані по тривалодопустимим струмам навантаження.

Захист мереж від дії струмів коротких замикань і перевантаження здійснюється автоматичними вимикачами щитка.


3. Стационарна тимчасова група підключена до існуючих мереж зовнішнього господарсько-питного водопостачання, згідно ТУ.

Водовідведення господарсько-побутових стоків передбачено відповідно ТУ за погодженням санітарно-епідеміологічної служби міста.


| Назва об'єкту, адреса розміщення                                                         | Посада виконавця  | ПІБ                         | Підпис                                                                                |
|------------------------------------------------------------------------------------------|-------------------|-----------------------------|---------------------------------------------------------------------------------------|
| Група стаціонарних тимчасових споруд,<br>вул.Фонтанська дорога, 63                       | ГАП<br>архітектор | Ігнатова Л.А.<br>Чабан Л.В. |  |
| М.П.  |                   |                             |                                                                                       |
| Кваліфікаційний сертифікат<br>серія АА № 000199                                          |                   |                             |                                                                                       |
| Дата складання "22" 10. 2014 року                                                        |                   |                             |                                                                                       |

# ЕСКІЗИ ФАСАДІВ ТС, М 1:50

## Головний фасад

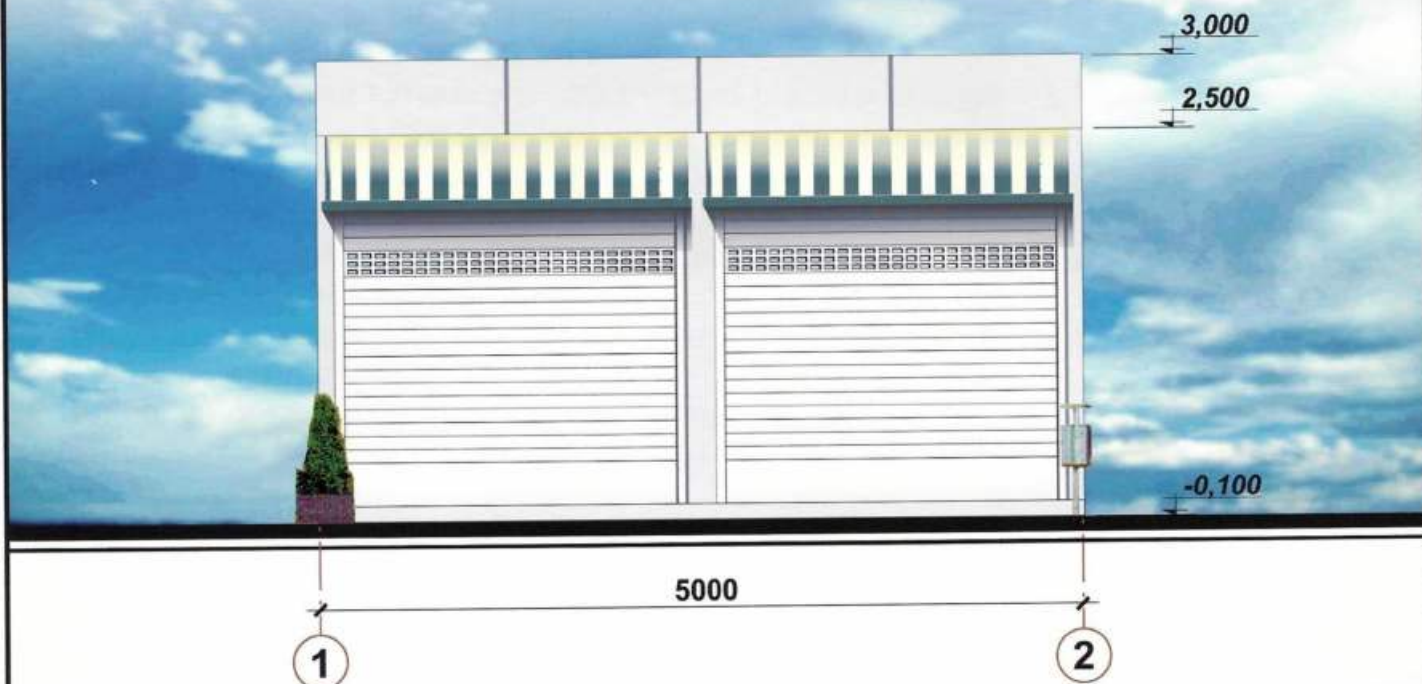

## Боковий фасад

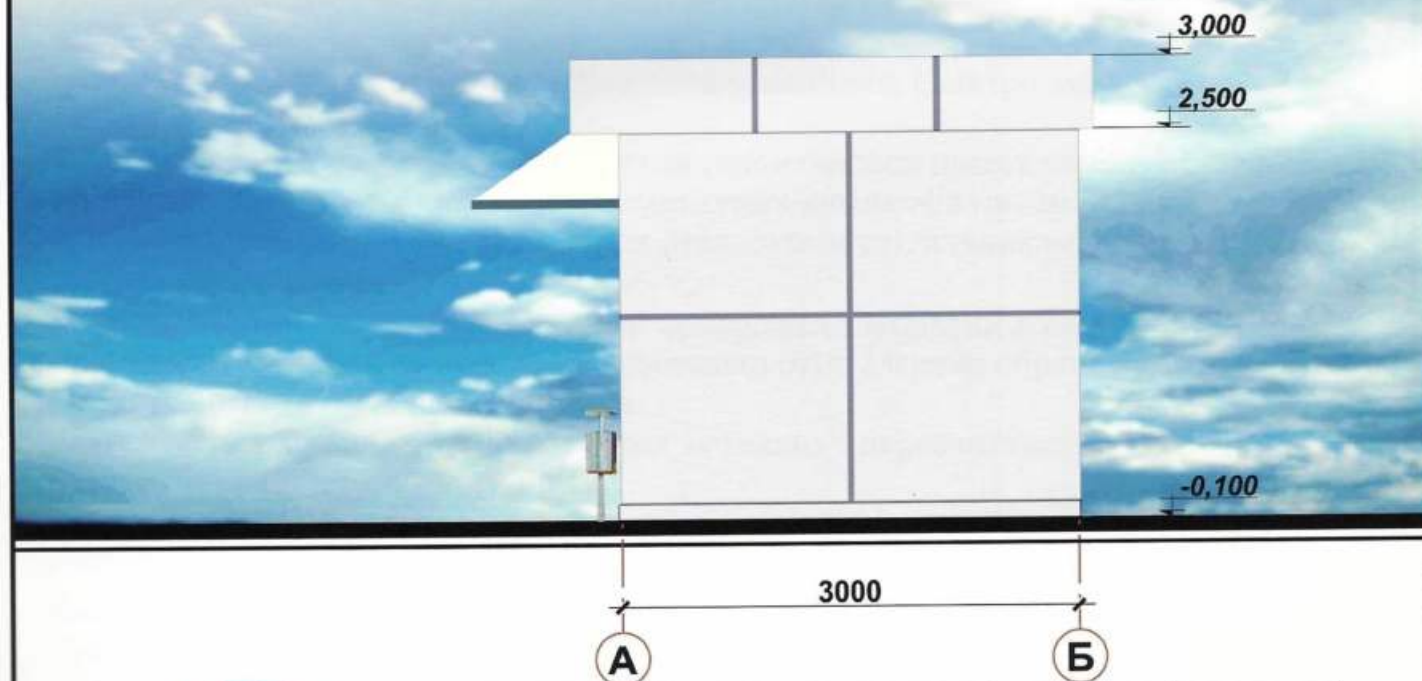


|   |                  |                             |                                                                                       |
|---|------------------|-----------------------------|---------------------------------------------------------------------------------------|
| <p>Назва об'єкту, адреса розміщення</p> <p>Група стаціонарних тимчасових споруд,<br/>вул.Фонтанська дорога, 63</p> <p>М.П. </p> | Посада виконавця | ПІБ                         | Підпис                                                                                |
|   | ГАП архітектор   | Ігнатова Л.А.<br>Чабан Л.В. |  |
| <p>Кваліфікаційний сертифікат<br/>серія АА № 000199</p> <p>Дата складання "22" 10. 2014 року</p>   |                  |                             |                                                                                       |



# СХЕМА РОЗМІЩЕННЯ ТС М 1:500

Площа земельної ділянки згідно з документами на землекористування  
Город земель фонд земля м.Одеси

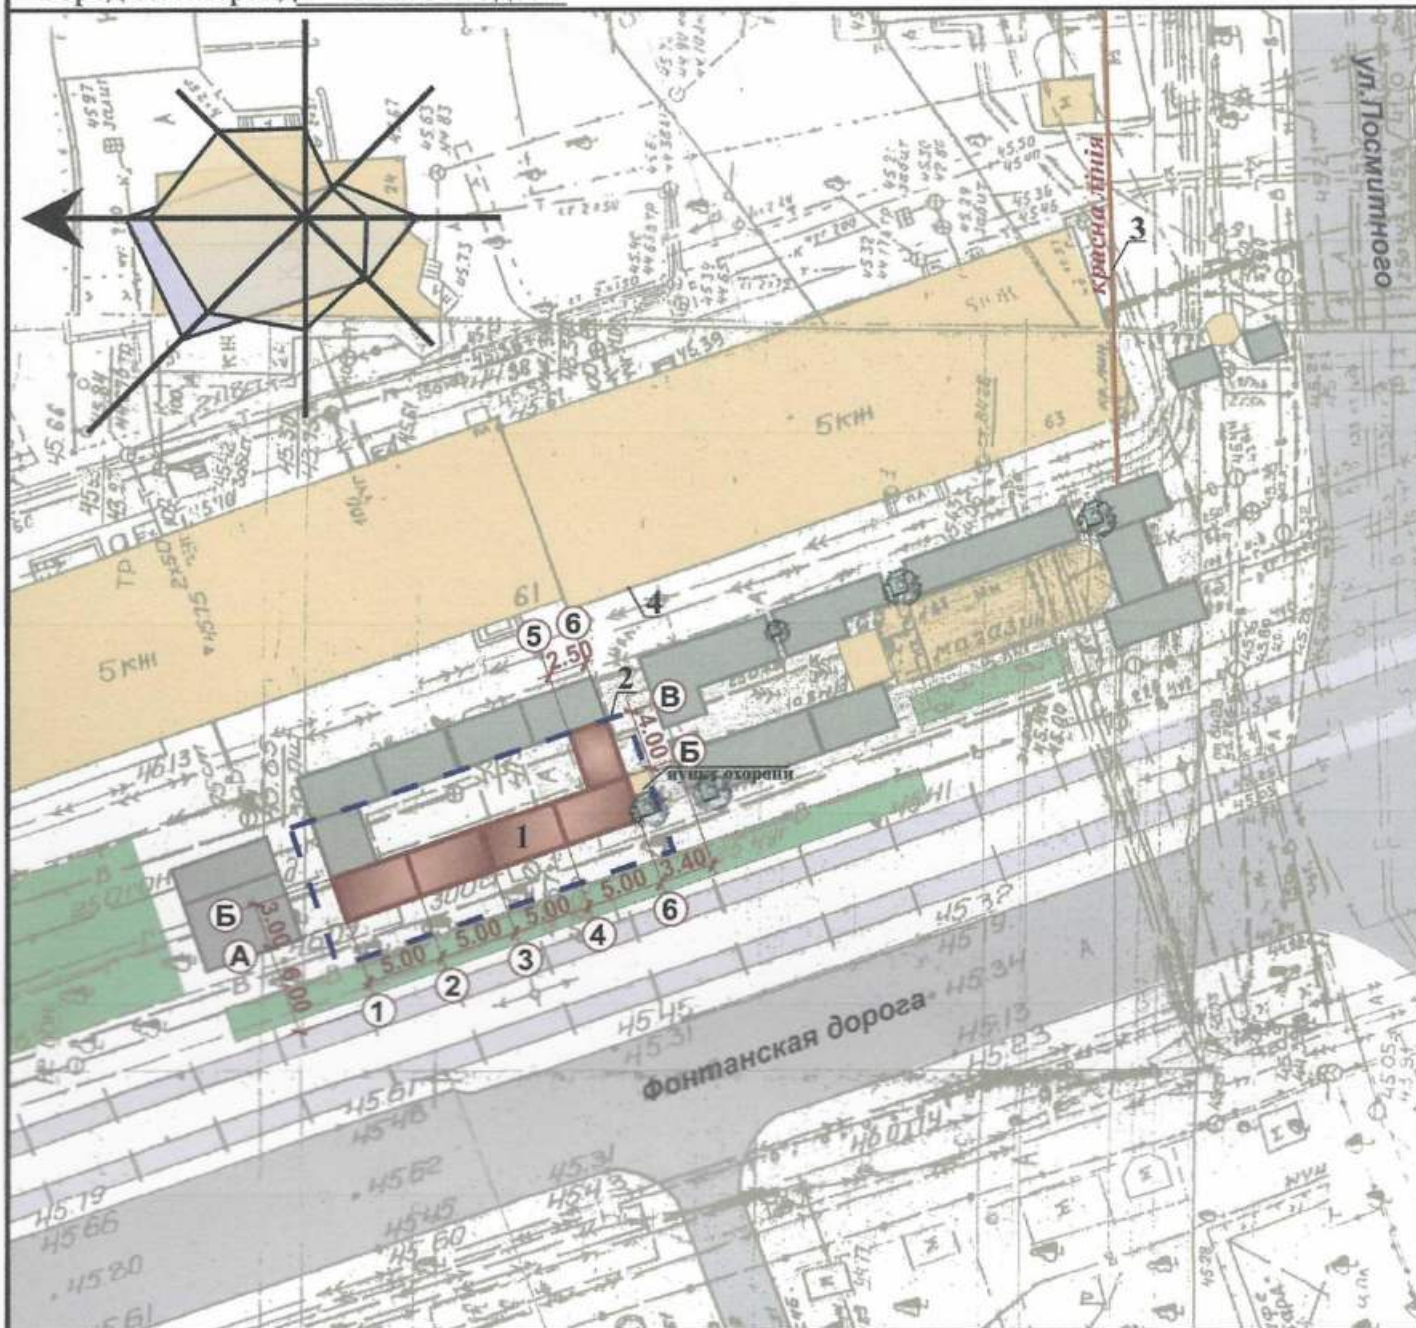

## Експлікація:

- 1) місце розташування групи ТС; 3) червоні лінії;  
2) лінії регулювання забудови; 4) місця підключення до інженерних мереж.

## Умовні позначення:


|  |                               |  |                   |  |                              |
|--|-------------------------------|--|-------------------|--|------------------------------|
|  | - об'єкт проектування (ТС)    |  | - існуючі дороги. |  | - територія благоустрою      |
|  | - існуючі будівлі та споруди. |  | - озеленення.     |  | - існуючі групи ТС ПП «ЮЛІС» |

|   |                  |                             |        |
|---|------------------|-----------------------------|--------|
| <p>Назва об'єкту, адреса розміщення</p> <p>Група стаціонарних тимчасових споруд,<br/>вул.Фонтанська дорога, 63</p> <p>М.П. </p> | Посада виконавця | ПІБ                         | Підпис |
|   | ГАП архітектор   | Ігнатова Л.А.<br>Чабан Л.В. |        |
| <p>Кваліфікаційний сертифікат<br/>серія АА № 000199</p> <p>Дата складання "22" 10. 2014 року</p>                                |                  |                             |        |




Площа земельної ділянки згідно з документами на землекористування  
Город земель фонд земля м.Одеси

Площа земельної ділянки згідно з документами на землекористування  
Город земель фонд земля м.Одеси

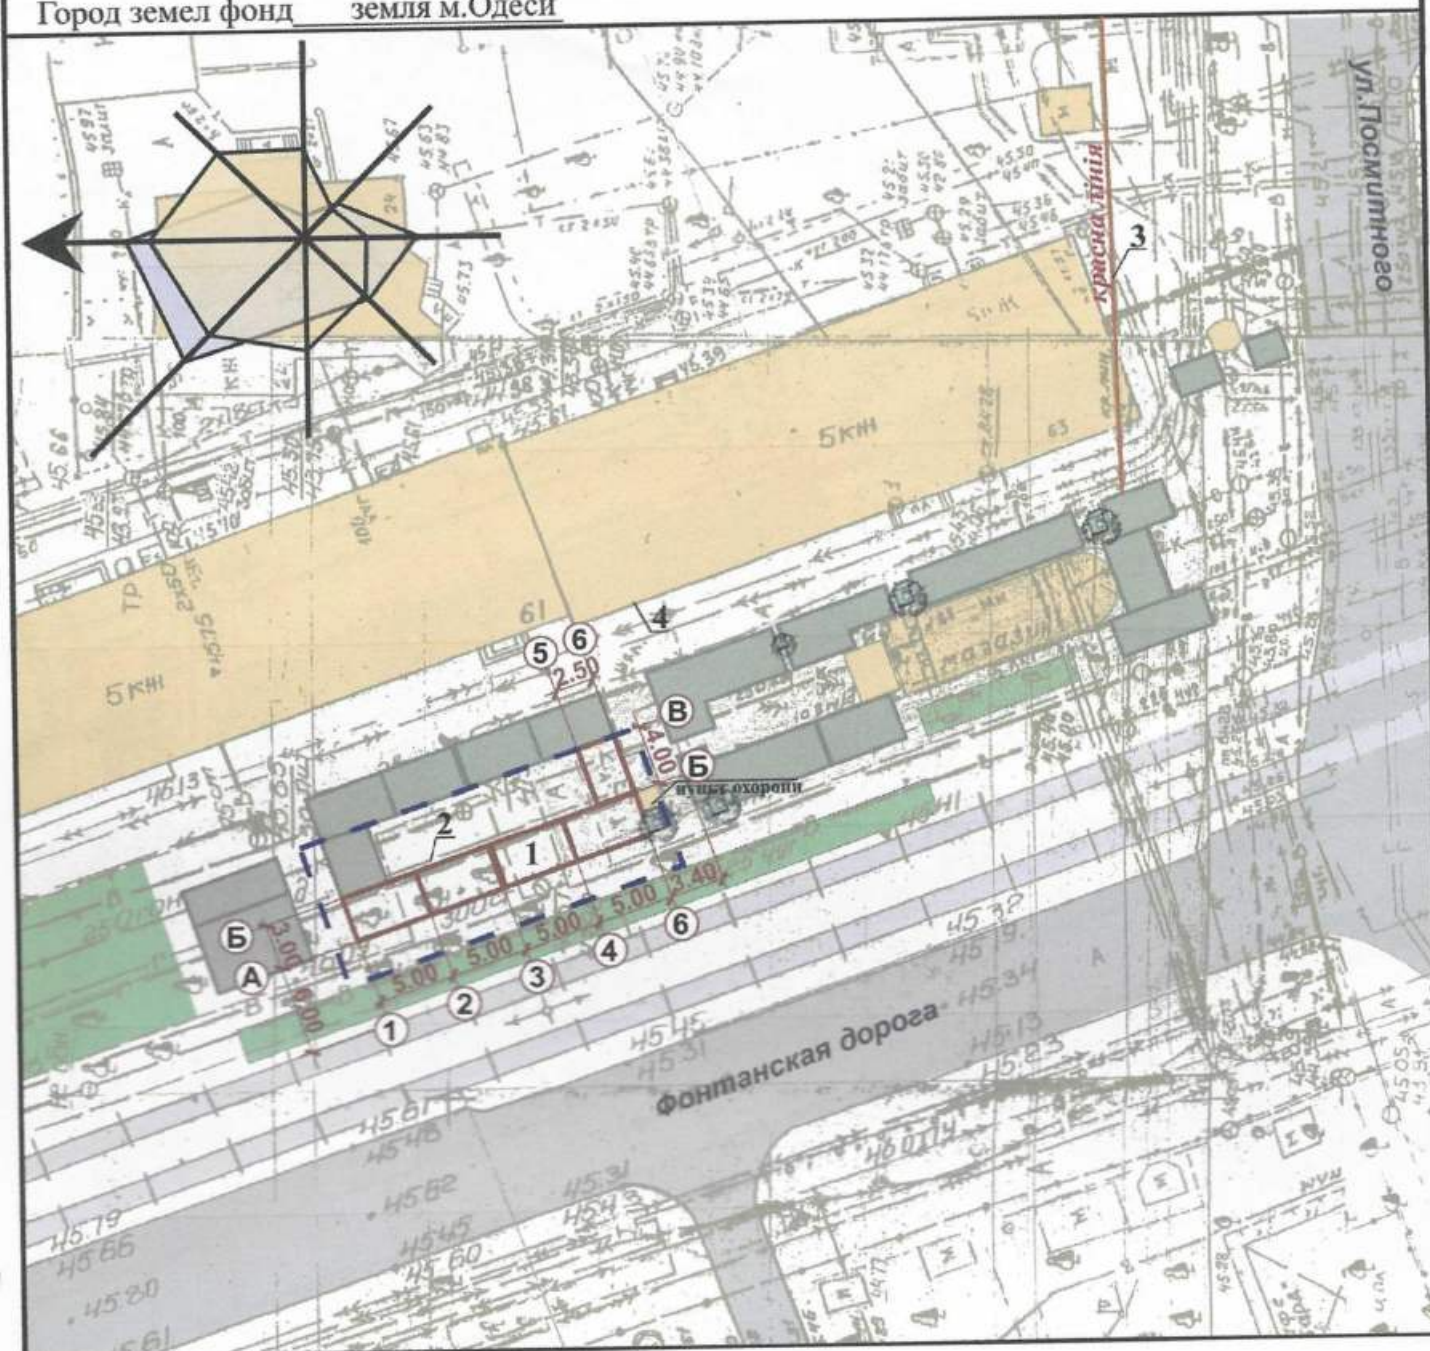


1) місце розташування групи ТС; 3) червоні лінії;  
2) лінії регулювання забудови; 4) місця підключення до інженерних мереж.

 - об'єкт проектування (ТС)    
  - існуючі дороги.    
  - територія благоустрою  
 - існуючі будівлі та споруди.    
 - озеленення.    
 - існуючі групи ТС ПП «ЮЛІС»
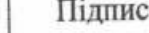
|   |                                                                                                  |                                                              |   |
|---|--------------------------------------------------------------------------------------------------|--------------------------------------------------------------|---|
| <p><u>Назва об'єкту, адреса розміщення</u></p> <p><b>Група стаціонарних тимчасових споруд,<br/>вул.Фонтанська дорога, 63</b></p> | <p><b>Посада<br/>виконавця</b></p> <p><b>ГАП<br/>архітектор</b></p>                              | <p><b>ПІБ</b></p> <p><b>Ігнатова Л.А.<br/>Чабан Л.В.</b></p> | <p><b>Підпис</b></p>  |
| <p><b>М.П.</b></p>                            | <p>Кваліфікаційний сертифікат<br/>серія АА № 000199</p> <p>Дата складання "22" 10. 2014 року</p> |                                                              |   |



# СИТУАЦІЙНИЙ ПЛАН, М 1:2000

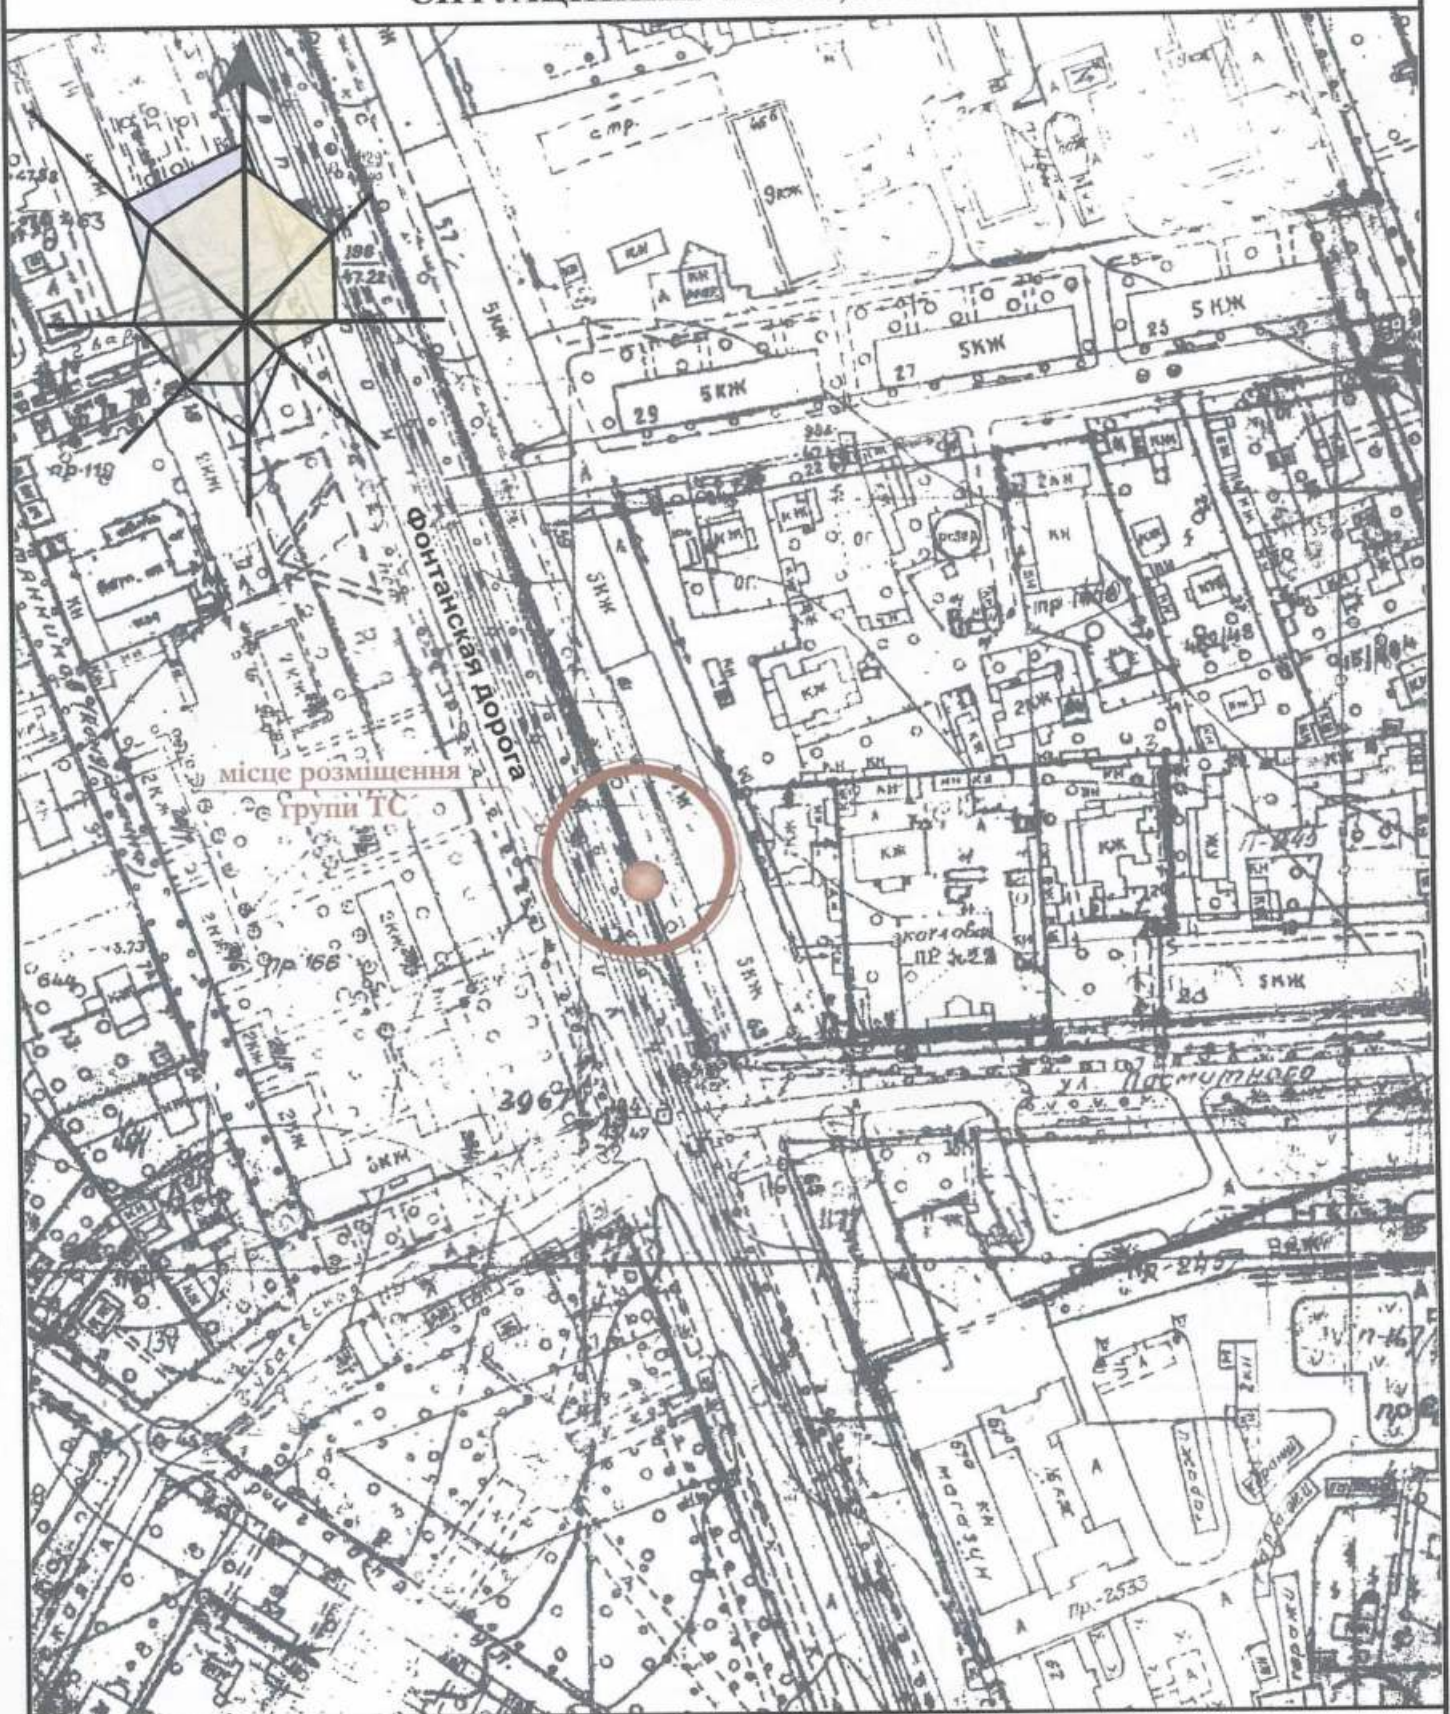

|                                                                                     |                                                                                          |                             |                                                                                       |
|-------------------------------------------------------------------------------------|------------------------------------------------------------------------------------------|-----------------------------|---------------------------------------------------------------------------------------|
| Назва об'єкту, адреса розміщення                                                    | Посада виконавця                                                                         | ПІБ                         | Підпис                                                                                |
| Група стаціонарних тимчасових споруд,<br>вул.Фонтанська дорога, 63                  | ГАП<br>архітектор                                                                        | Ігнатова Л.А.<br>Чабан Л.В. |  |
|  | Кваліфікаційний сертифікат<br>серія АА № 000199<br>Дата складання "22" 10.2014 року      |                             |                                                                                       |
|                                                                                     | М.П.  |                             |                                                                                       |