

ПОЯСНЮВАЛЬНА ЗАПИСКА

1. Тимчасова споруда (ТС) для здійснення підприємницької діяльності має закриті приміщення для тимчасового перебування людей.
За умовну позначку 0.000 прийнятий рівень чистої підлоги ТС.
Ступінь вогнестійкості - Ша.
Габаритні розміри павільйона в плані - 3.00м x 3.00м.
У павільйоні розташоване приміщення, площею - 7.84м².
Внутрішня висота павільйону від рівня чистої підлоги складає - 2.40м.
Загальна висота павільйону - 2.92м.
Ґрунт заснування, до встановлення павільйону, ретельно утрамбован щебнем.
Стіни споруди запроектовані по типу «Сендвич», товщиною 100мм із утеплювачем з мінеральної вати й обшивкою.
Обшивка стін по каркасу: зовнішня - колірний алюмінієві сендвіч панелі; внутрішня (стіни й стеля) - гіпсокартон.
Підлога з покриттям дошки 40мм і утеплювачем (керамзитовий ґравій - 200мм) та покриття з негорючого матеріала.
Покрівля - по металевим прогонам і решетуванню з покриттям із профільованого сталевих листа, з утеплювачем з мінераловатних плит, гідро- і пароізоляцією.

Зовнішня обробка.


поверхні стін - колірні алюмінієві сендвіч панелі.
вікна - металопластикові;
двері - металопластикові;
покрівля - колірний металевий профнастіл, алюмінієві сендвіч панелі;
цоколь - колірні сендвіч-панелі.

2. Стационарна тимчасова споруда підключена до мереж електропостачання згідно з діючими нормами та ТУ. Точка підключення - близька опора, що розташована поряд з територією ділянки.
Опалювання - електричне з встановленням навісних електро-конвекторів з регулюванням температури.
Як розподільний щиток у павільйоні встановлено щиток серії NRL-1F6ZS з лічильником активної енергії й автоматичних вимикачів на лініях, що відходять.
Освітлення приміщення виконане стельовими світильниками з люмінесцентними лампами.
Розподільні мережі павільйону, виконані проводами з мідними жилами, що прокладені у трубах та приховані в обшивці стін. Мережі обрані по тривалодопустимим струмам навантаження.
Захист мереж від дії струмів коротких замикань і перевантаження здійснюється автоматичними вимикачами щитка.


Назва об'єкту, адреса розміщення Стационарна тимчасова споруда, вул. Французький бульвар, 22	Посада виконавця	ПІБ	Підпис
	ГАП архітектор	Ігнатова Л.А. Чабан Л.В.	
 М.П.	Кваліфікаційний сертифікат серія АА № 000199		
	Дата складання "07" 11. 2014 року		

ЕСКІЗИ ФАСАДІВ ТС, М 1:50

Головний фасад

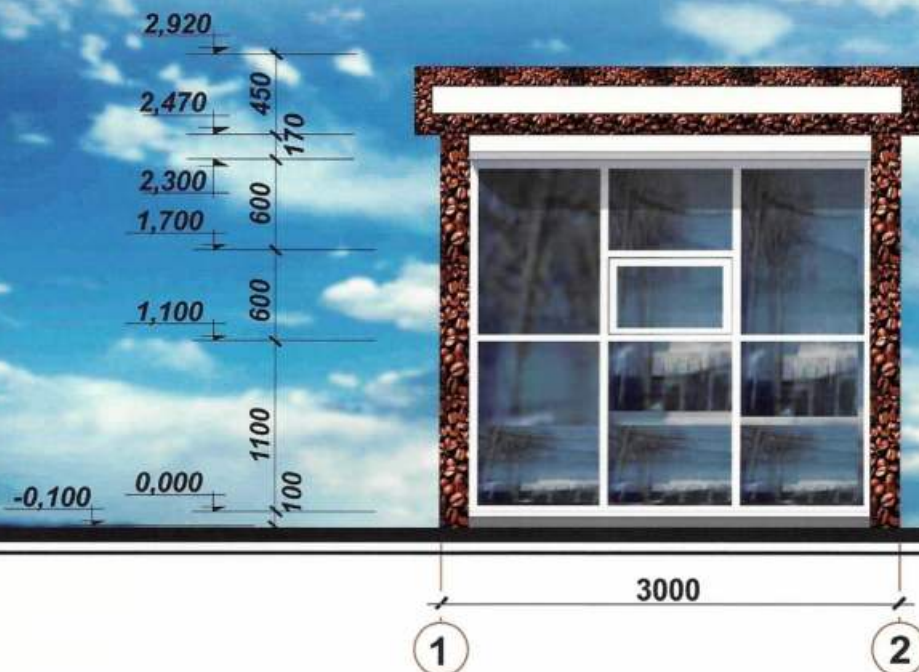

Боковий фасад

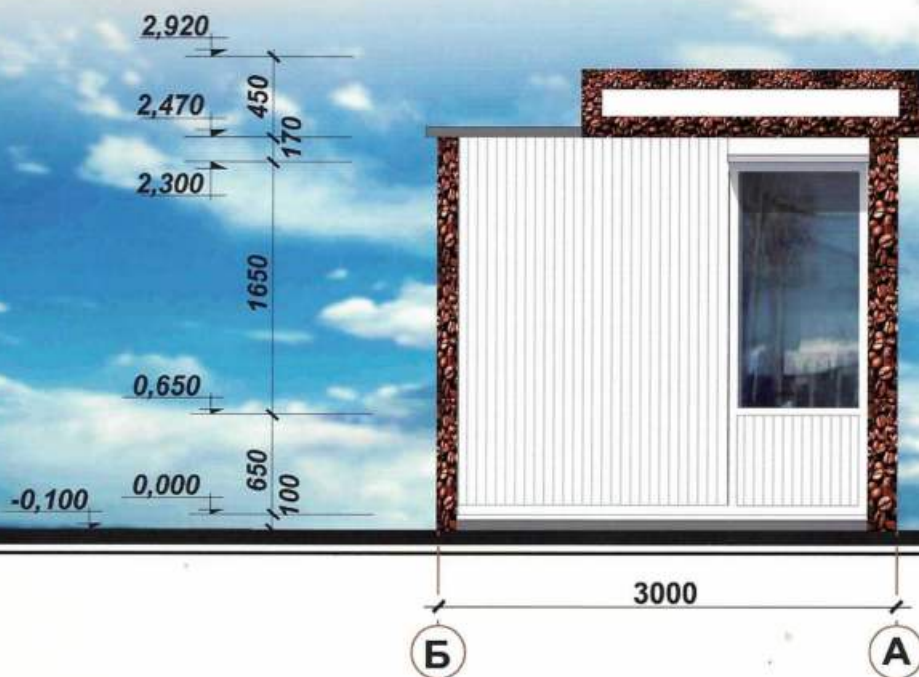


 Назва об'єкту, адреса розміщення Станційна тимчасова споруда, вул. Французький бульвар, 22	Посада виконавця	ПІБ	Підпис
	ГАП архітектор	Ігнатова Л.А. Чабан Л.В.	
Кваліфікаційний сертифікат серія АА № 000199 Дата складання "07" 11. 2014 року			

СХЕМА РОЗМІЩЕННЯ ТС М 1:500

Площа земельної ділянки згідно з документами на землекористування

Город земель фонд земля м.Одеси

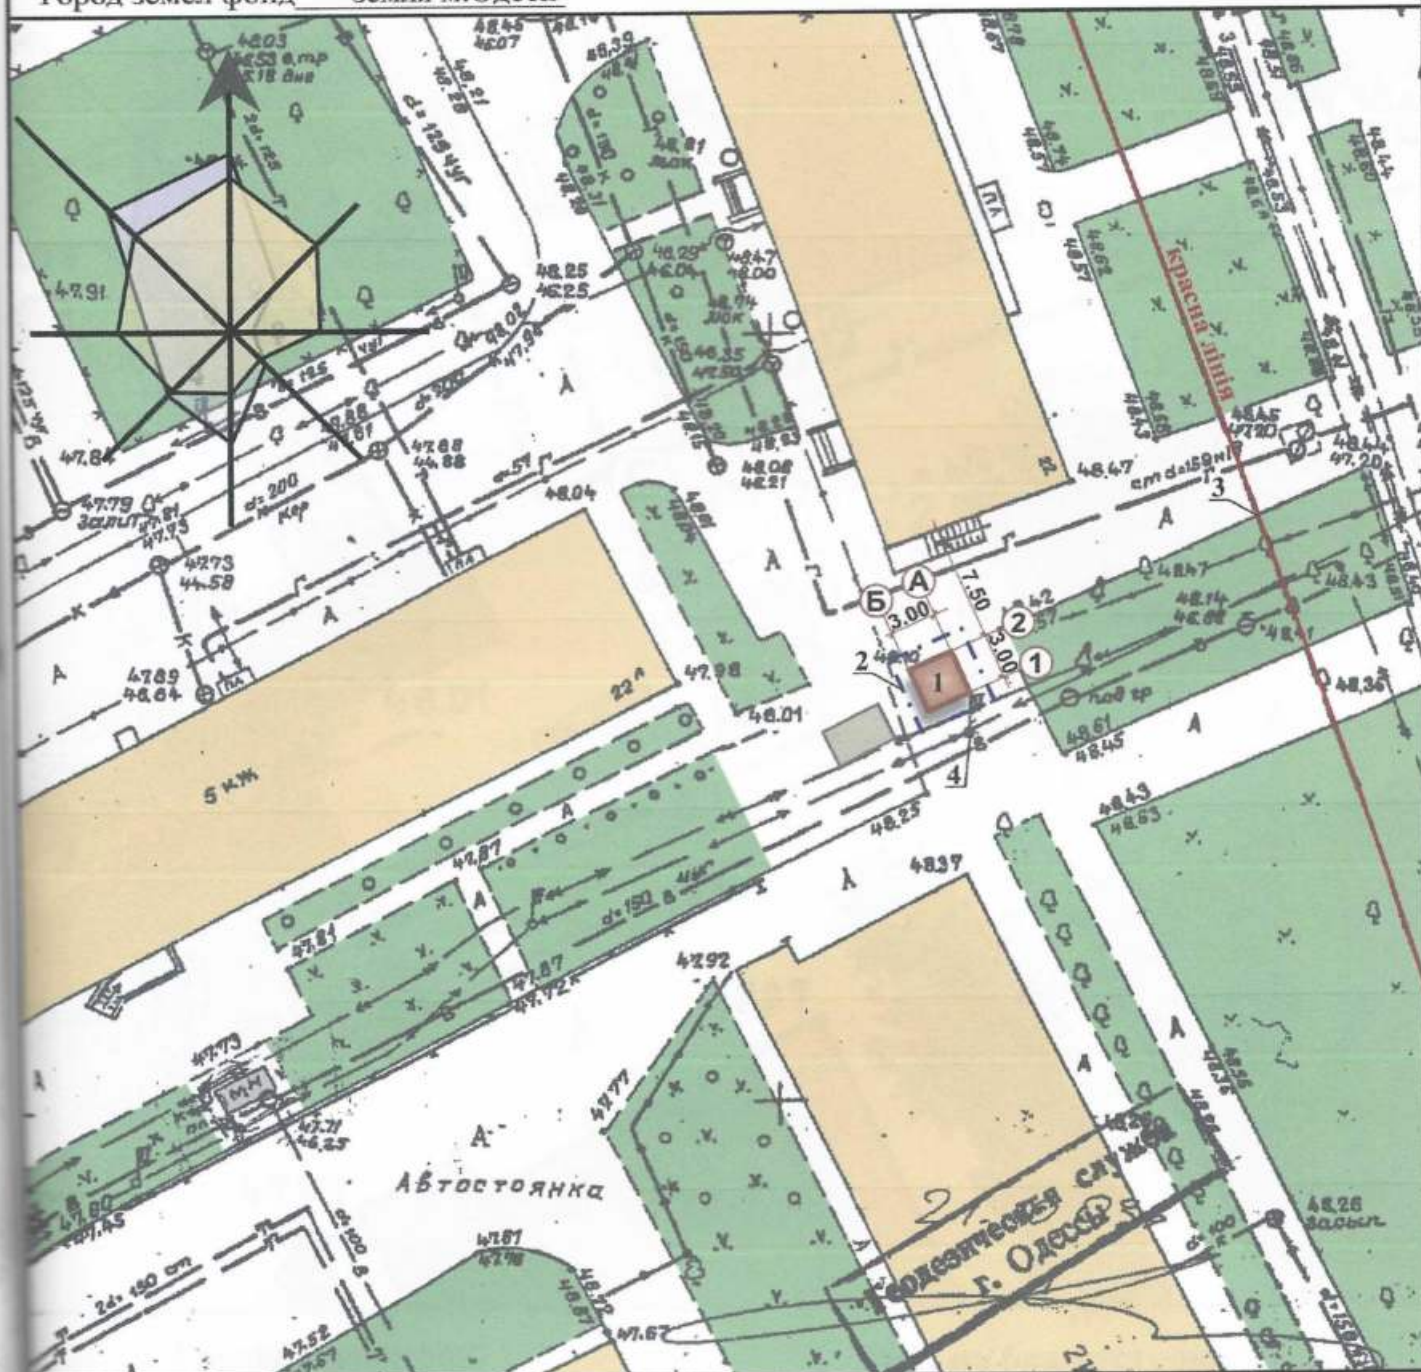

Експлікація:

- 1) місце розташування ТС;
- 2) лінії регулювання забудови;
- 3) червоні лінії;
- 4) місця підключення до інженерних мереж.

Умовні позначення:

 - об'єкт проектування (ТС)

 - територія благоустрою

 - існуючі будівлі та споруди.

 - озеленення.

 - існуючі ТС

Назва об'єкту, адреса розміщення Станційна тимчасова споруда, вул. Французький бульвар, 22 Архітектор М.П. № 199 ЛЕНА ОЛЕКСІЕНА	Посада виконавця	ПІБ	Підпис
	ГАП архітектор	Ігнатова Л.А. Чабан Л.В.	
Кваліфікаційний сертифікат серія АА № 000199 Дата складання "07" 11. 2014 року			

місце розміщення ТС

Французький бульвар

пер. Чумакова

Назва об'єкту адреси: **Станційна тимчасова в'їжджаюча митниця в м. Французький Мад.**

[Signature]

Дата складання "07" 11.2014 року