

СТИСЛА ПОЯСНЮВАЛЬНА ЗАПИСКА


1. Тимчасова споруда ФОП Ліщенко А.А, розташована за адресою: вул. Вільямса, 50а/1, має закриті приміщення для тимчасового перебування людей.
За умовну позначку 0.000 прийнятий рівень чистої підлоги ТС.
Ступінь вогнестійкості – Ша.
Тимчасова споруда являє собою павільйон прямокутної форми в плані, з габаритними розмірами – 5,0м х 6,0м.
Загальна висота ТС – 2,60м.
Площа забудови групи ТС – 30,0м²
Загальна площа групи ТС – 27,8м²
ТС встановлюється без закладання фундаменту. Грунт основи, до встановлення ТС, ретельно утрамбовується щебнем та укладається бетонна тротуарна плитка.
Основні конструкції виконані по металевому каркасу.
Стіни споруди виконані по типу «Сендвич», товщиною 100мм з утеплювачем та обшивкою з обох сторін.
Утеплювач – «Ізовер» по розрахунку.
Внутрішня обробка: стіни – листи ламінованого ДСП, стеля – гіпсокартон.
Підлога в приміщенні – дерев'яні дошки 40мм по металевому каркасу з утеплювачем з мінераловатних плит та покриттям з негорючого матеріалу.

Зовнішня обробка:
поверхні стін – фасадні композитні панелі типу «Alucobond».
Віконні та дверні отвори заповнені металопластиковими блоками.
Покрівля – оцинкована покрівна сталь.
2. Тимчасову споруду забезпечено електроенергією з підключенням к існуючим внутрішньо квартальним мережам. Точка підключення – опора, що розташована поряд з ТС.
Освітлення приміщень виконане стельовими світильниками з люмінесцентними лампами.
Для урахування електроенергії на вводі встановлено ввідно-лічильний ящик типу ПВУ.
Захист мереж від дії струмів коротких замикань і перевантаження здійснюється автоматичними вимикачами щитка.
Опалювання - електричне з встановленням навісних електро-конвекторів з регулюванням температури.
Електропостачання – згідно договору про користування електроенергією з ВАТ «Одесаобленерго», та відповідно ТУ.
3. Благоустрій прилеглої території виконується згідно з планом благоустрою. Освітлення території передбачене світильниками, що розміщуються на головному фасаді ТС.




ЕСКІЗИ ФАСАДІВ ТС М 1:50

Задній фасад М 1:50

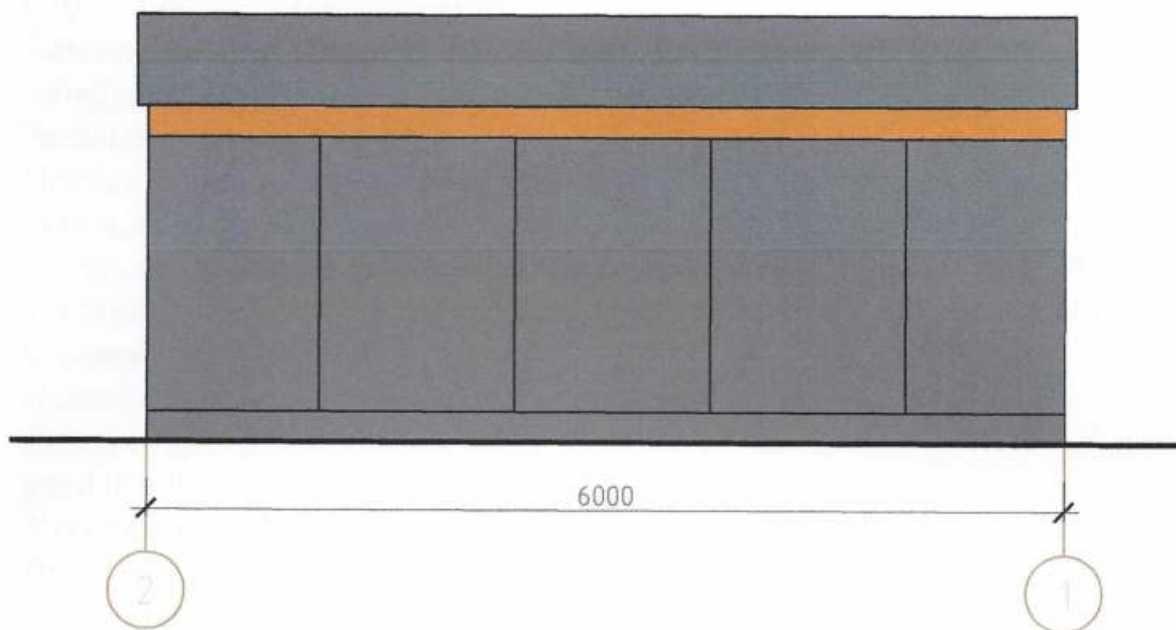

Бічний фасад М 1:50

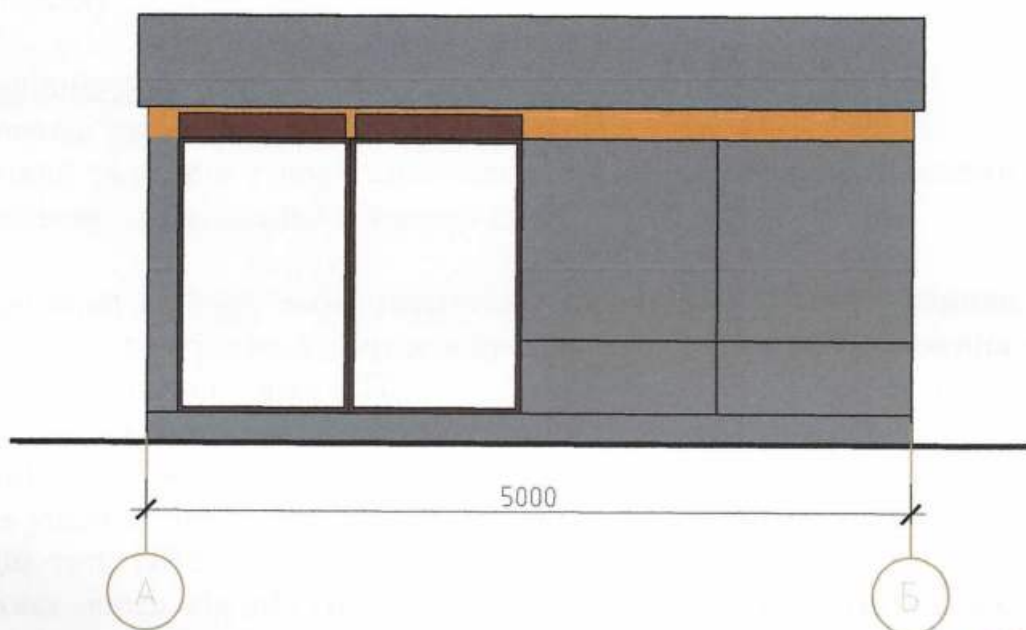

Назва об'єкту, адреса розміщення	Посада виконавця	ШБ	
тимчасова споруда (павільон)	ГАП архітектор	Найденов І.В. Найденов І.В.	
м. Одеса. вул.Академіка Вільямса,50а/1.			

Кваліфікаційний сертифікат
Серія АА 001218


Дата складання "19" 07 2019

ЕСКІЗИ ФАСАДІВ ТС М 1:50

Головний фасад М 1:50



Бічний фасад М 1:50

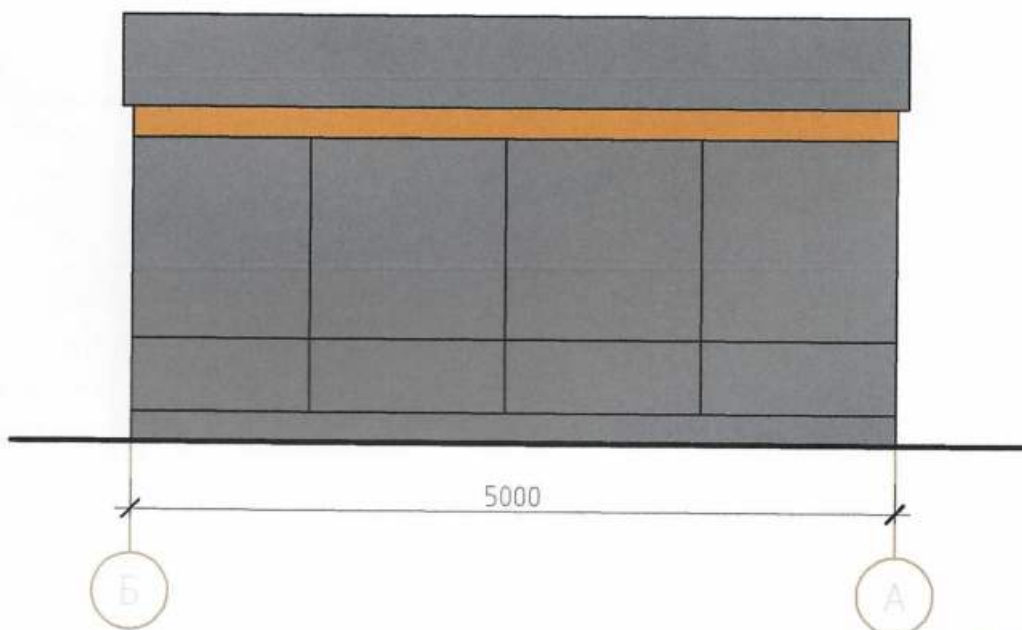


Назва об'єкту, адреса розміщення	Посада виконавця	ШБ	
тимчасова споруда (павільон)	ГАП архітектор	Найденов І.В. Найденов І.В.	
м. Одеса. вул.Академіка Вільямса,50а/1.			

Кваліфікаційний сертифікат
Серія АА 001218

Дата складання "19" 07 2019

ПЛАН ТС М 1:50

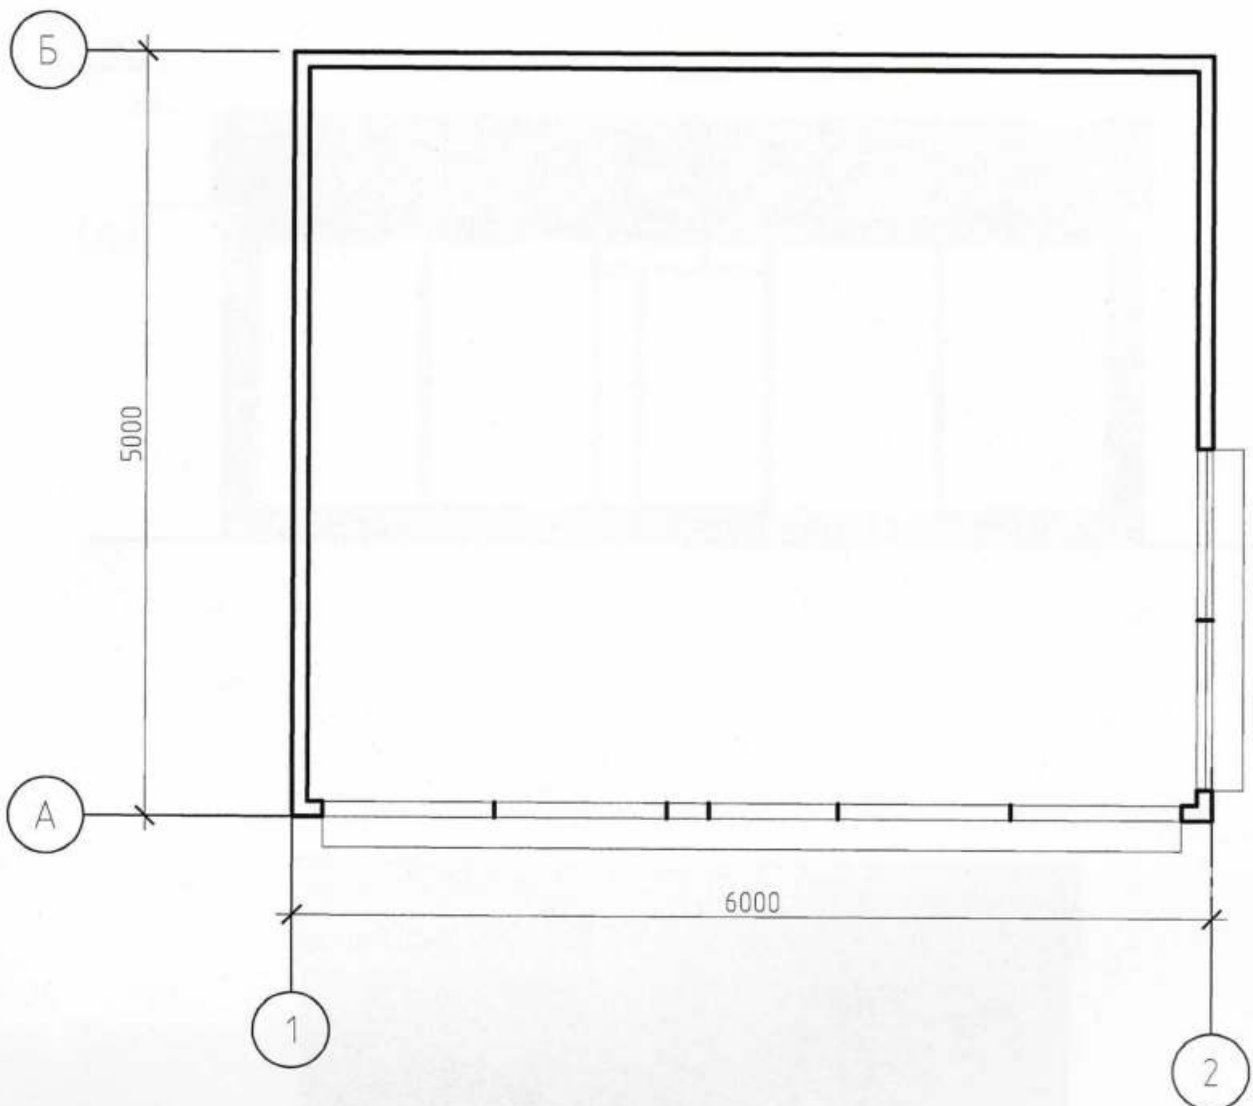

ТЕХНИКО-ЭКОНОМИЧЕСКИЕ ПОКАЗАТЕЛИ

- 1 Загальна площа павільона – 27.8 м.кв.
- 2 Площа забудови – 30.0 м.кв.


Назва об'єкту, адреса розміщення тимчасова споруда (павільон) м. Одеса. вул.Академіка Вільямса,50а/1.	Посада виконавця	ШБ	
	ГАП архітектор	Найденов І.В Найденов І.В	

Кваліфікаційний сертифікат
Серія АА 001218

Дата складання "19" 07 2019

СХЕМА РОЗМІЩЕННЯ ТС М 1:500

Площа земельної ділянки згідно з документами
на землекористування землі міста

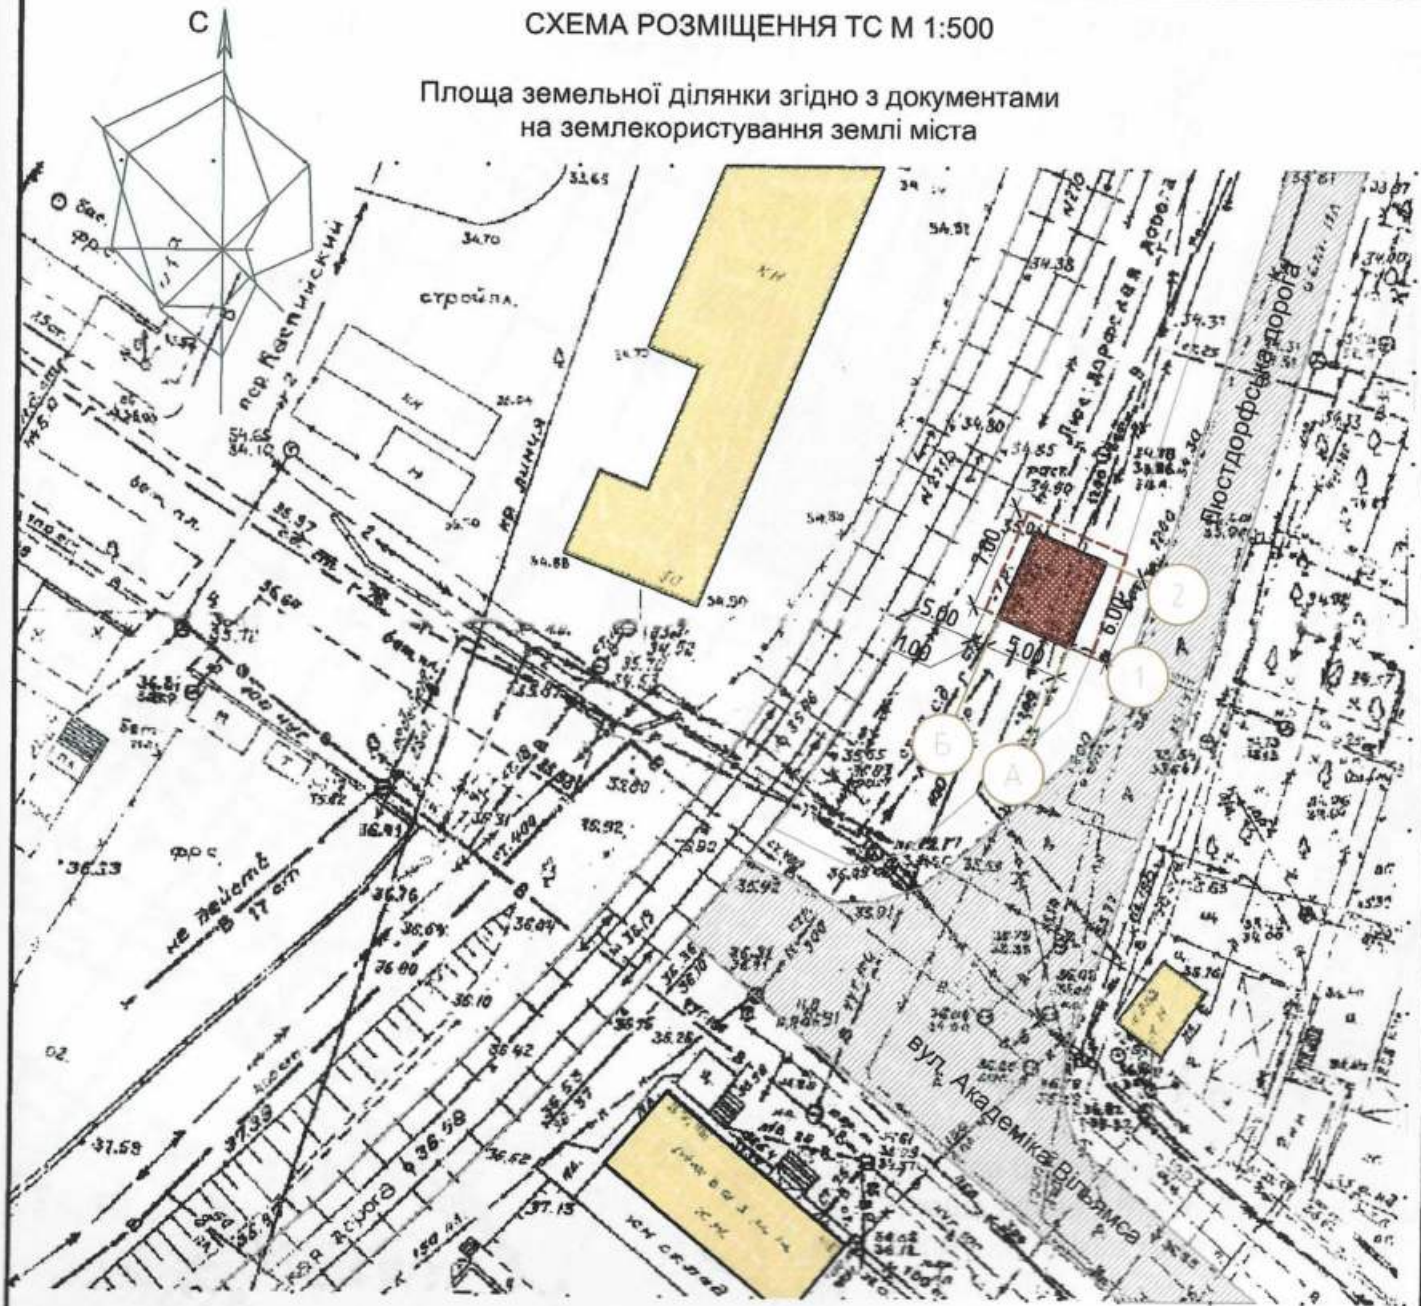

Експлікація:

- 1) місце розташування ТС;
- 2) червоні лінії;
- 3) лінії регулювання забудови;
- 4) місця підключення до інженерних мереж.

Умовні позначення:

- об'єкт проектування (ТС)
- існуючі будівлі та споруди
- існуючі дороги
- межа благоустрою ділянки розміщення ТС
- озеленення

Назва об'єкту, адреса розміщення
тимчасова споруда
(павільйон)

м. Одеса.
вул.Академіка Вільямса,50а/1.

Посада
виконавця

ГАП
архітектор

ШБ

Найденів І.В.
Найденів І.В.



Кваліфікаційний
сертифікат
Серія АА 001218

Дата складання "19" 07 2019



Місце розміщення об'єкту

Назва об'єкту, адреса розміщення

тимчасова споруда
(павільон)

м. Одеса.
вул.Академіка Вільямса,50а/1.

Посада
виконавця

ГАП
архітектор

ШБ

Найденов І.В
Найденов І.В



Кваліфікаційний сертифікат
Серія АА 001218

Дата складання "19" 07 2019