

СТИСЛА ПОЯСНЮВАЛЬНА ЗАПИСКА

1. Стаціонарна тимчасова споруда являє собою павільон для здійснення підприємницької діяльності, має торгівельне приміщення для тимчасового перебування людей.

За умовну позначку ± 0.000 прийнятий рівень чистої підлоги ТС.

Ступень вогнестійкості - Ша.

ТС має прямокутну форму у плані, габаритні розміри - 3,37 x 3,37 м.

Загальна площа ТС - 11,36 м².

Внутрішня висота від рівня чистої підлоги складає - 2,72 м.

Загальна висота складає - 3,21 м.

Грунт заснування, до встановлення ТС, ретельно утрамбовується щебнем та укладається тротуарна плитка.

ТС встановлюється на існуюче покриття без влаштування фундаменту.

Стіни споруд запроектовані товщиною 100 мм із утеплювачем з мінеральної вати та обшивкою з обох сторін.

Обшивка стін по каркасу: зовнішня - металеві листи композитного матеріалу типу "Алюкобонд"; внутрішня: стіни - ламіноване ДСП, стеля - вагонка.

Підлога - дерев'яні дошки 40 мм по металевому каркасу з утеплювачем з мінераловатних плит та покриттям з негорючого матеріалу (плитка).

Покрівля - по металевим прогонам і риштуванню з покриттям із металочерепиці, з утеплювачем з мінераловатних плит, гідро- і пароізоляцією.

Зовнішня обробка:

поверхні стін- металеві листи композитні матеріали типу "Алюкобонд";

вікна, двері - металопластикові з вакуумними склопакетами;

покрівля - металочерепиця.

2. Тимчасова споруда підключається до мереж електропостачання згідно з діючими нормами та ТУ. Точка підключення - згідно з ТУ.

Опалення - електричне з встановленням навісних електро-конвекторів з регулюванням температури.

Освітлення приміщення виконується світильниками з люмінісцентними лампами.

Розподільні мережі виконані проводами з мідними жилами, що прокладені у трубах та приховані в обшивці стін.

Захист мереж від дії струмів коротких замикань та перевантажень здійснюється автоматичними вимикачами щитка.

3. Благоустрій прилеглої території виконується згідно з планом благоустрою.

Освітлення території передбачене світильниками, що розміщуються на головному фасаді ТС.

В.о.директора ТОВ "АРХІ-ТЕКСТУРЦЯ"

Головний інженер

Кваліфікаційний сертифікат серія АР № 012191




В.В. Спіченко

Т.І. Свеченко



ЕСКІЗИ ФАСАДІВ ТС

Головний фасад ТС М 1:50

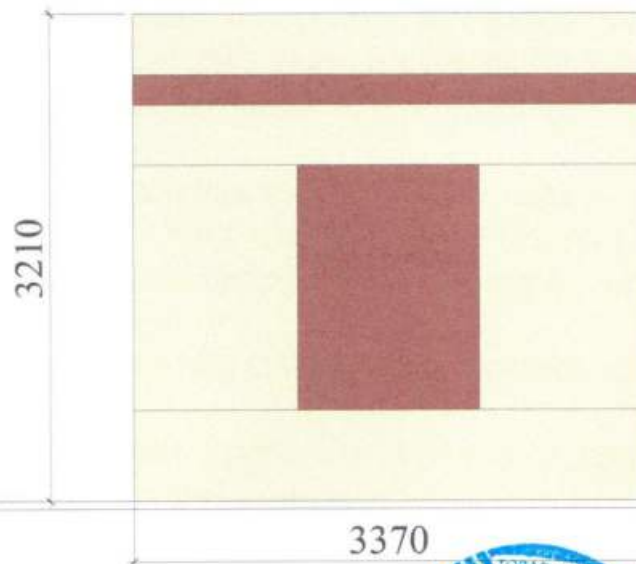


В.о.директора ТОВ "АРХІ-ТЕКСТУРЦЯ"

Головний інженер

Кваліфікаційний сертифікат серія АР № 012191



План ТС М 1:50

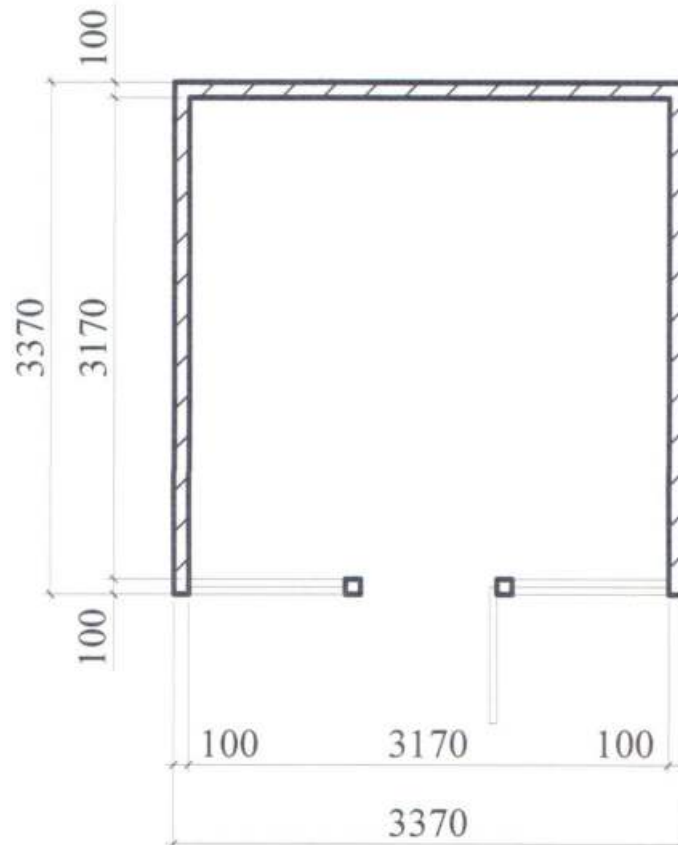

В.о.директора ТОВ "АРХІ-ТЕКСТУРИЦЯ"


Головний інженер

Кваліфікаційний сертифікат серія АР № 012191

В.В. Євченко



Площа земельної ділянки згідно з документами
на землекористування - землі міста

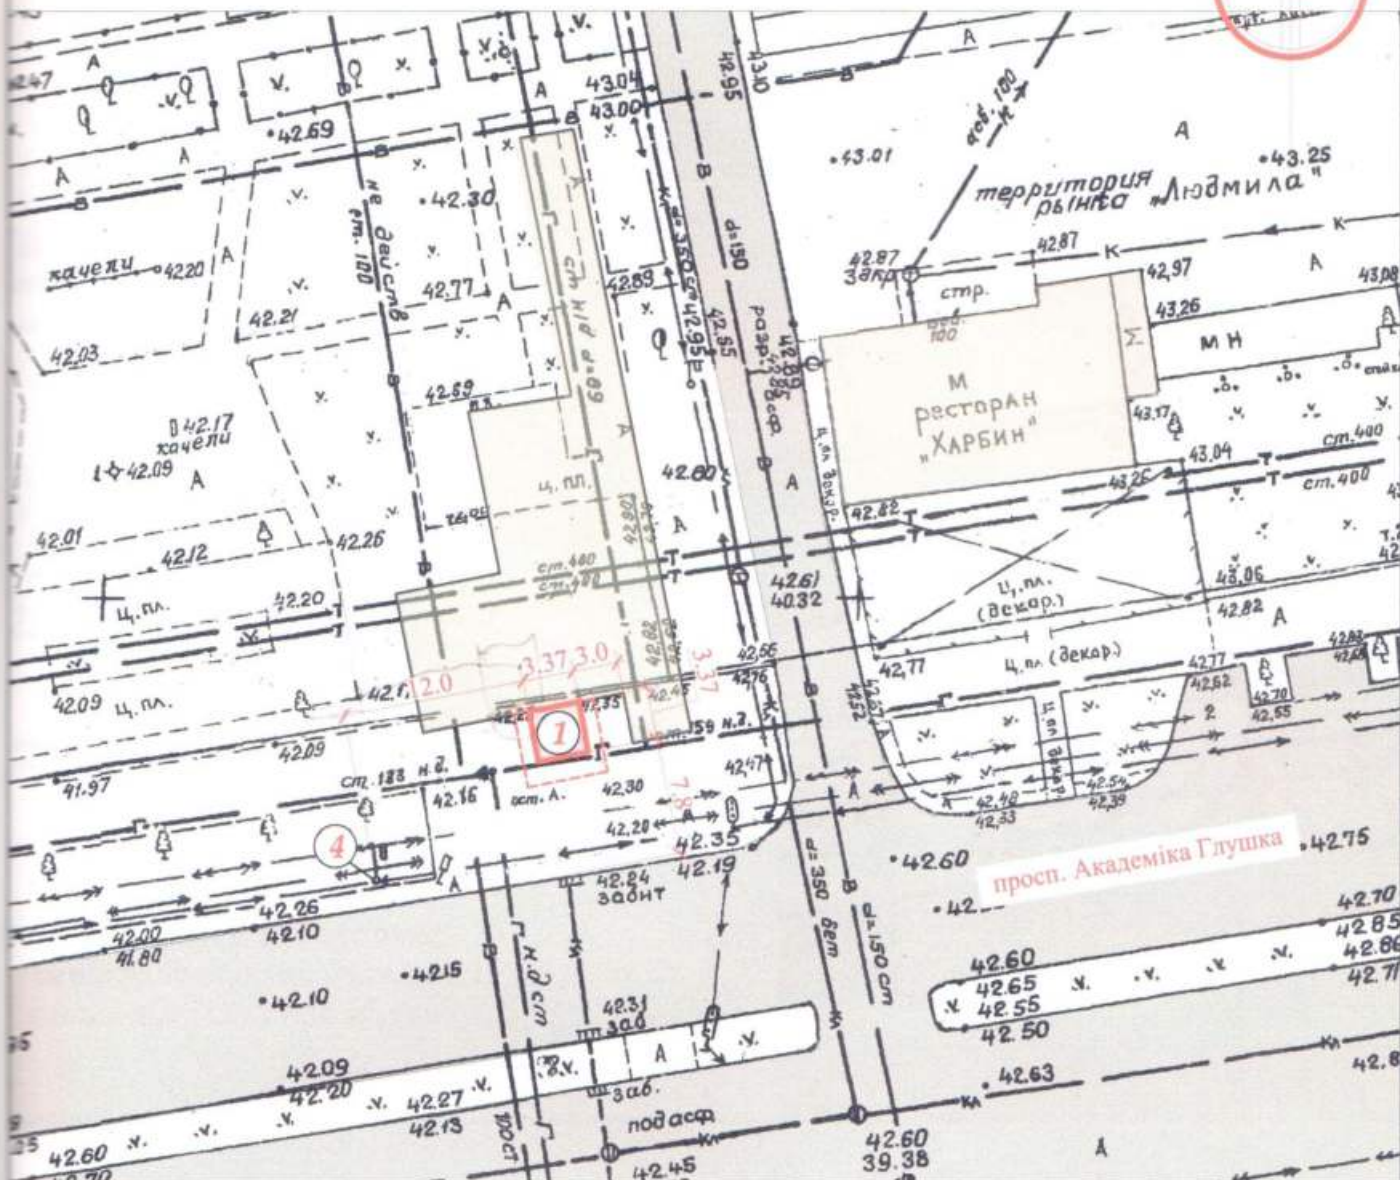

- 1) місце розташування ТС;
- 2) червоні лінії;
- 3) лінії регулювання забудови;
- 4) місця підключення до інженерних мереж.

-  - межа благоустрою ділянки розміщення ТС
-  - проектна ТС
-  - існуючі будівлі


підключення до мереж електропостачання

Кваліфікаційний сертифікат серія АР № 012191

Т. Г. Євченко

Ситуаційний план М 1:2000

Місце розміщення об'єкту

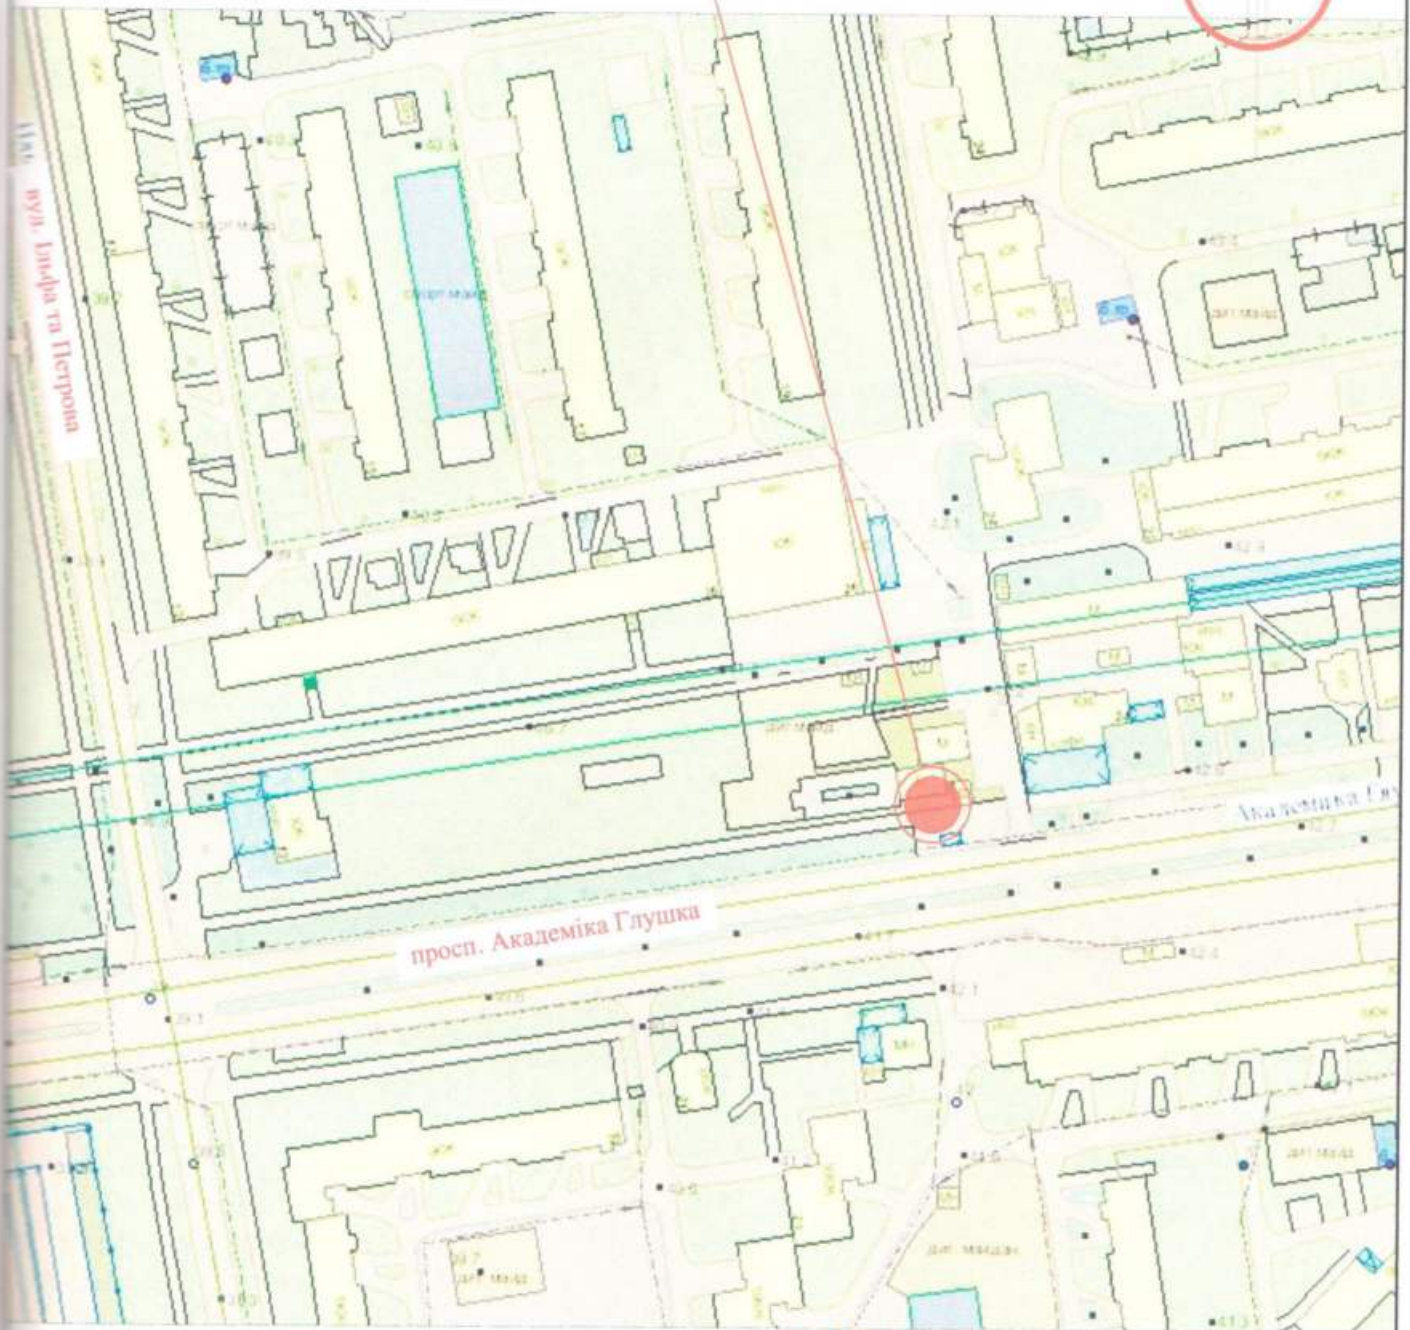

В.о.директора ТОВ "АРХІ-ТЕКСТУРЦЯ"

Головний інженер

Кваліфікаційний сертифікат серія АР № 012191

В.В. Сидченко
Т.Т. Євченко

