

ПОЯСНЮВАЛЬНА ЗАПИСКА

1. Стационарних тимчасових споруд для здійснення підприємницької діяльності має горгівельні приміщення для тимчасового перебування людей.

Ступінь вогнестійкості - III а.

Кіоск має прямокутну форму.

Габаритні розміри у плані - 2,7 м X 2,7 м

Площа забудови - 7,3 м²

Загальна площа тимчасової споруди – 6,25 м²

Площа твердого покриття - 7,3 м²

Загальна висота – 2,50 м

Внутрішня висота складає – 2,30 м

ґрунт заснування, до встановлення ТС, ретельно утрамбовується щебенем такладається бетонна тротуарна плитка.

Стіни групи споруд запроектовані товщиною 100 мм із сертифікованим утеплювачем із мінеральної вати та обшивкою з обох сторін.

Обшивка стін по каркасу: зовнішня – колірний металевий профіль; внутрішня (стіни й теля) – пластикова вагонка.

Підлога – дерев'яні дошки 40 мм по металевому каркасу з утеплювачем енополістерольних плит та покриттям з негорючого матеріалу.

Покрівля – по металевих прогонах і решетуванню з покриттям із профільованого галевого листа, з утеплювачем з мінераловатних плит, гідро- і пароізоляцією.

Зовнішня обробка:

Верхні стін – колірний металевий профіль;

Вікна – металопластикові;

Вері – металопластикові;

Покрівля – профільований сталевий лист;

ТС підключається до мереж електропостачання згідно з чинними нормами та ТУ. точка підключення згідно з ТУ. Опалення - електричне з встановленням навісних електро - конвекторів з регулюванням температури. Освітлення приміщення виконується ітильниками з діодними лампами. Розподільні мережі виконані проводами із мідними лами, що прокладені у трубах та приховані в обшивці стін. Захист мереж від дії румів, коротких замикань та перевантажень здійснюється автоматичними вимикачами ттка. Передбачене заземлення.

Благоустрій прилеглої території виконується згідно з планом благоустрою, освітлення отирії передбачене світильниками, що розміщуються на основному фасаді та над одом в ТС.

хітектор


ліфікаційний сертифікат, серія АА № 002057




Давидова В.В.

ЕСКІЗИ ФАСАДІВ ТС М 1:50

Фасад в осях 1-2

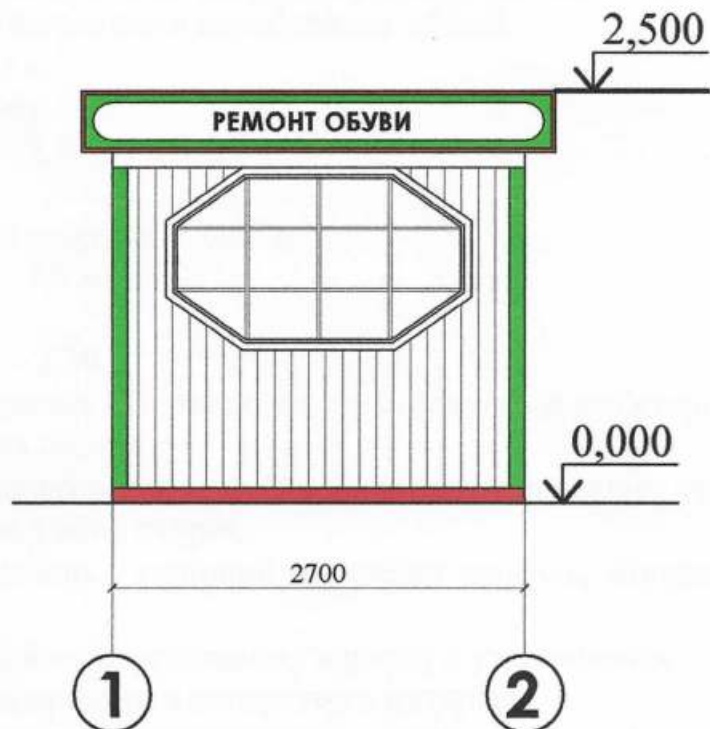

Фасад в осях А-Б

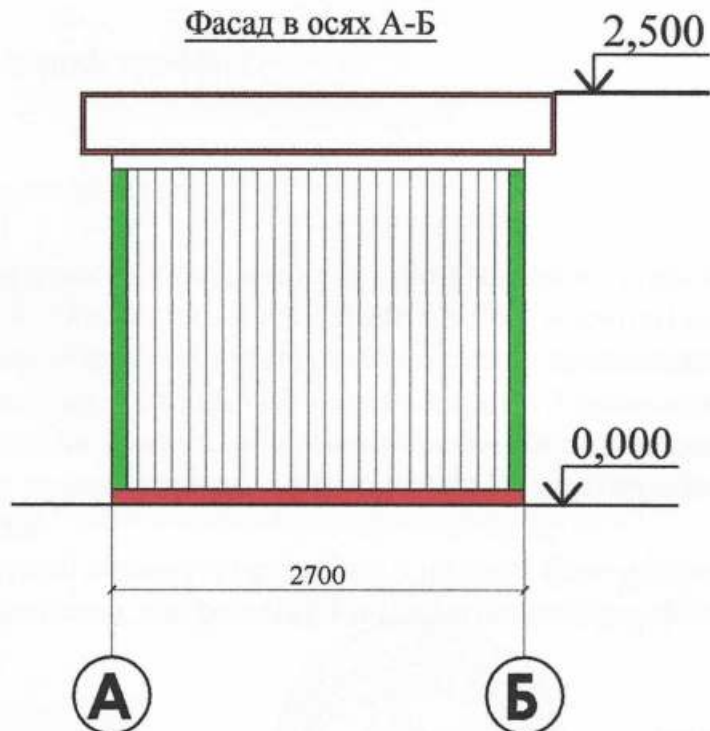


Архітектор
Кваліфікаційний сертифікат, серія АА № 002057



Давидова В.В.

ПЛАН ТС М 1:50

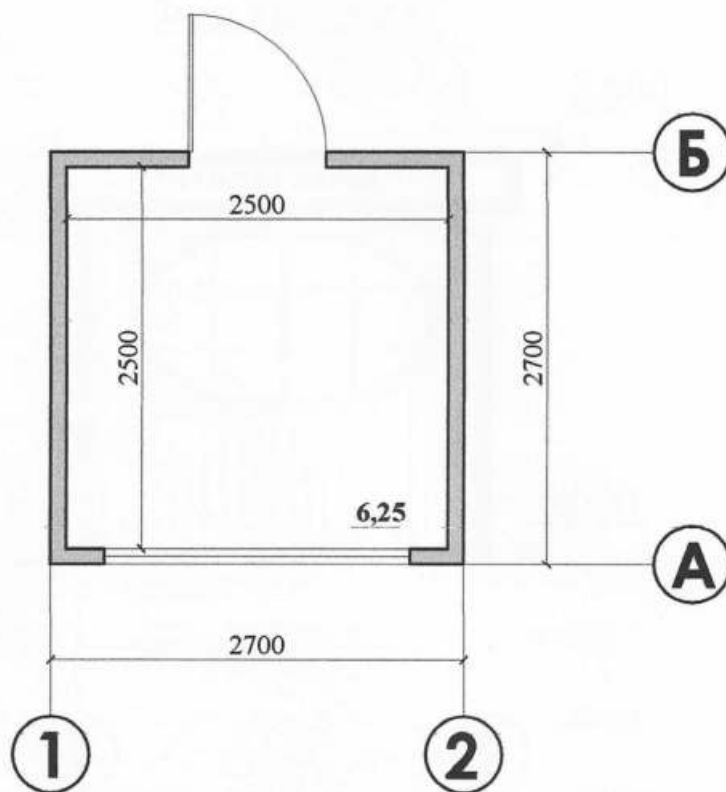

Архітектор


Кваліфікаційний сертифікат, серія АА № 00215



Давидова В.В.

СХЕМА РОЗМІЩЕННЯ ТС М 1:500



Площа земельної ділянки згідно з документами на землекористування - землі міста

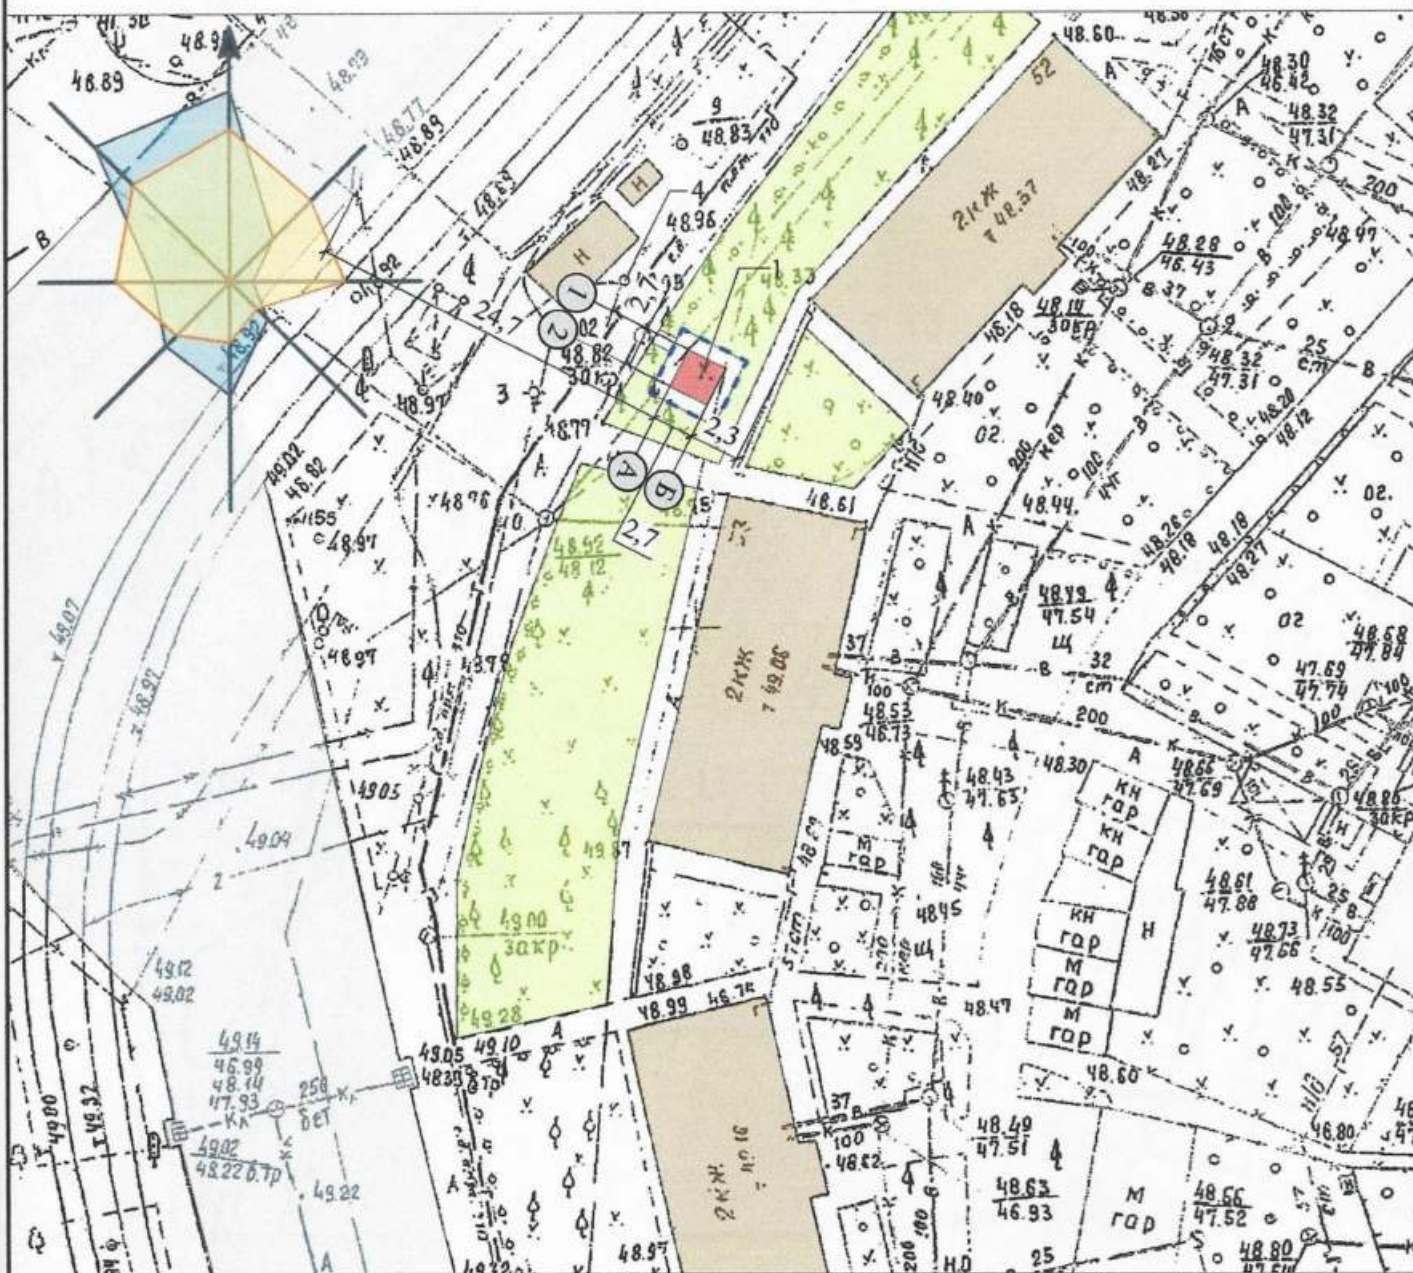

Експлікація:

- 1) місце розташування ТС;
- 2) червоні лінії;
- 3) лінії регулювання забудови;
- 4) місця підключення до інженерних мереж.

Умовні позначення

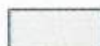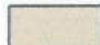-  Існуюча дорога
-  Існуючі споруди
-  Існуюче озеленення
-  Тимчасова споруда
-  Територія, що підлягає благоустрою


Архітектор

Кваліфікаційний сертифікат, серія АА № 002057



Давидова В.В.

Місце розміщення об'єкта

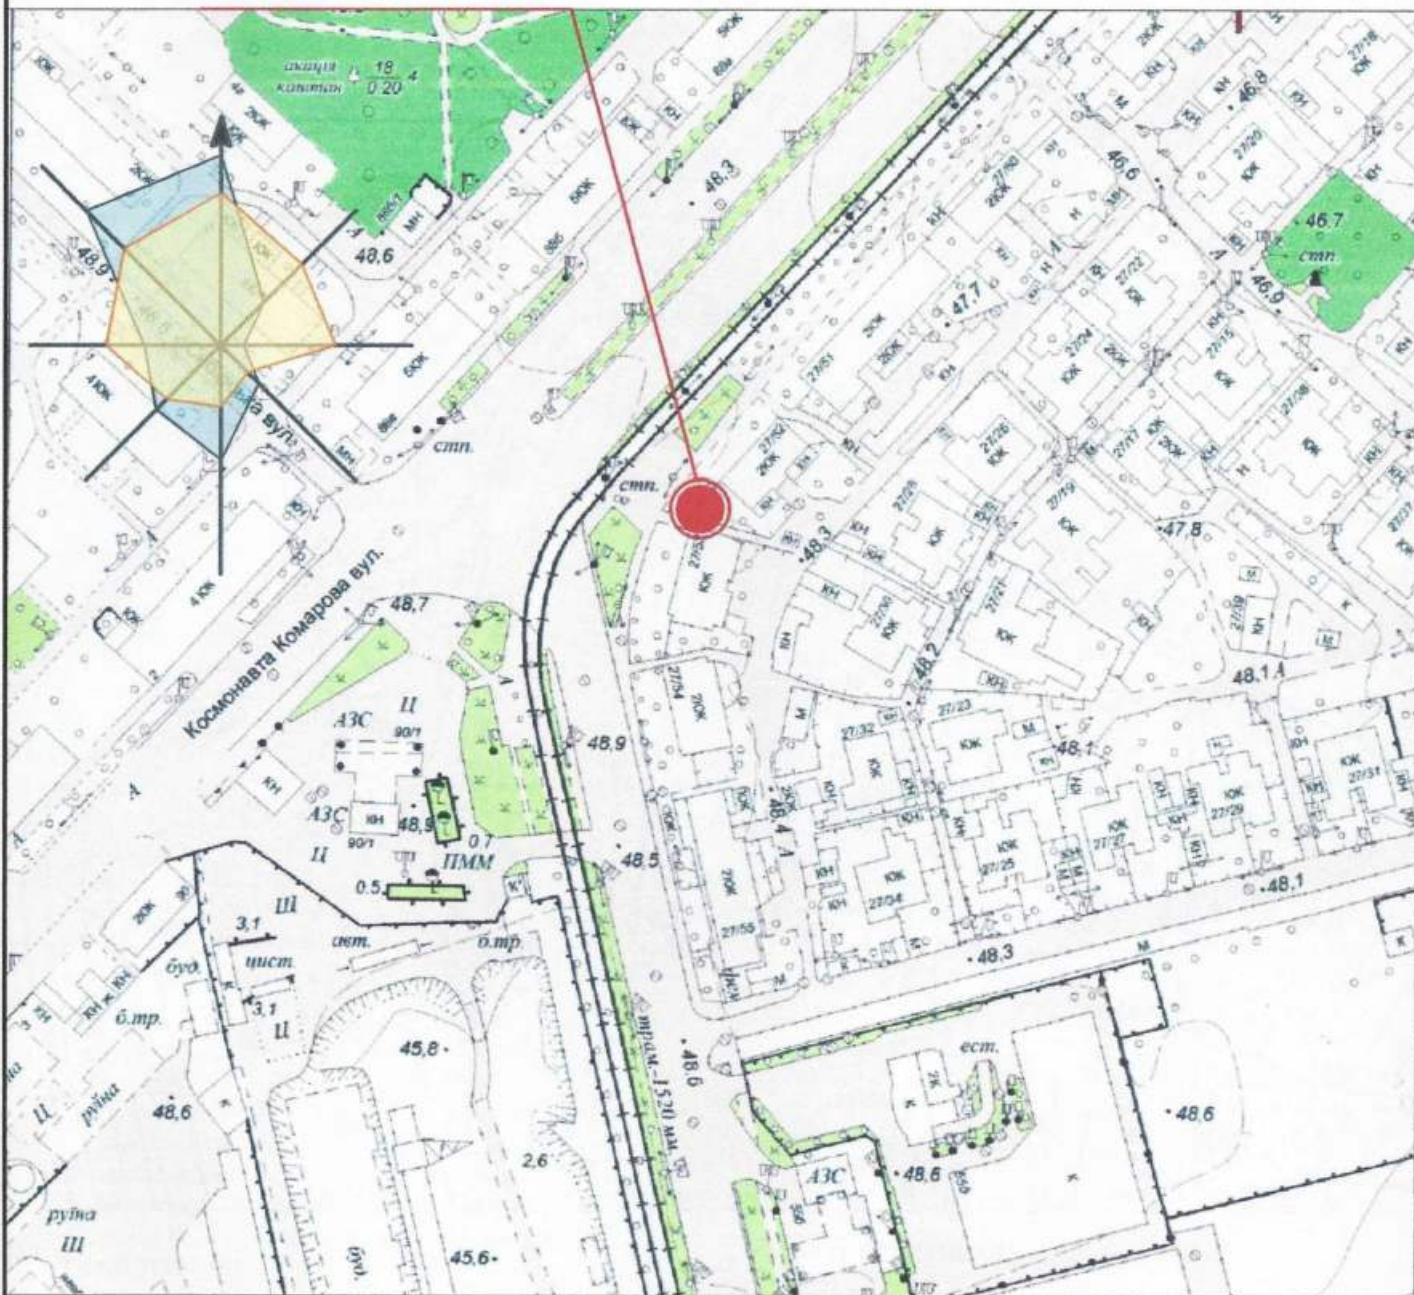

Давидова В.В.