

СТИСЛА ПОЯСНЮВАЛЬНА ЗАПИСКА

1. Група стаціонарних тимчасових споруд для здійснення підприємницької діяльності, яка має торговельні приміщення для тимчасового перебування людей.

Ступінь вогнестійкості — IIIa

Павільйони мають прямокутну форму.

Габаритні розміри групи у плані — 11.00м x 6.00м.

Площа забудови групи — 66.00м²

Площа твердого покриття групи — 66.00м²

Загальна площа групи — 61.63м²

Загальна висота групи — 3.00,м

Внутрішня висота складає — 2.70м.

Ґрунт заснування, до встановлення ТС, ретельно утрамбовується щебенем, без улаштування фундаменту та укладається тротуарна плитка.

Стіни споруди запроектовані товщиною 100 мм із сертифікованим утеплювачем із мінеральної вати та обшивкою з обох сторін.

Обшивка сторін по каркасу: зовнішня — по металевому каркасу композитні матеріали типу Алюкобонд., внутрішня (стіни та стеля) — пластикова вагонка.

Підлога — дерев'яні дошки 40 мм по металевому каркасу з утеплювачем з пенополістерольних плит та покриттям антипіринами та антигрибковими засобами.

Покрівля — по металевим прогонам і решетуванню з покриттям профнастілом, з утеплювачем з мінераловатних плит.

Зовнішня обробка:

поверхні стін — композитні матеріали типу Алюкобонд.

Вікна та двері — металопластикові із вакуумними склопакетами, пофарбовані фарбою для ПФХ.

покрівля — профнастіл.

2. Група ТС підключається до мереж електропостачання згідно з чинними нормами та ТУ. Точка підключення згідно з ТУ.

Опалення - електричне з встановленням навісних електро-конвекторів з регулюванням температури.

Освітлення приміщення виконується світильниками з діодними лампами.

Розподільні мережі виконані проводами із мідними жилами, що прокладені у трубах та приховані в обшивці стін.

Захист мереж від дії струмів, коротких замикань та перевантажень здійснюється автоматичними вимикачами щитка. Передбачене заземлення.

3. Благоустрій прилеглої території виконується згідно з планом благоустрою, Освітлення території передбачене світильниками, що розміщуються на основному фасаді та над входом в ТС.

Директор ТОВ "Архітектурне Бюро "АРКАДІЯ"
Архітектор


Кваліфікаційний сертифікат серія АА №002590




Смаглій Д.П.
Глінін Д.Ю.

Ескізи Фасадів групи ТС

Головний фасад групи ТС 1:100

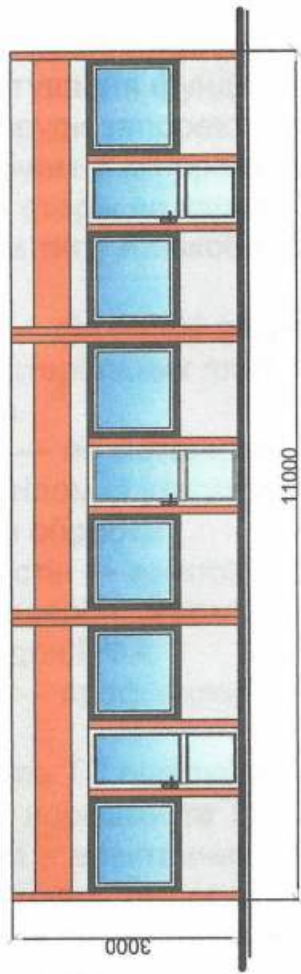

Бічний фасад групи ТС М 1:100

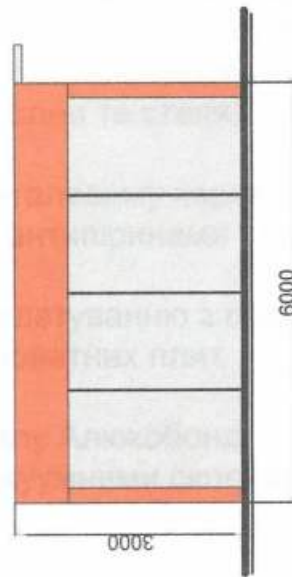

Директор ТОВ "Архітектурне Бюро "Аркада" С. Маглій Д.П.


Архітектор

Кваліфікаційний сертифікат серія АА №002590



П. І. Маглій Д.Ю.

ПЛАН ГРУПИ ТС М 1:100

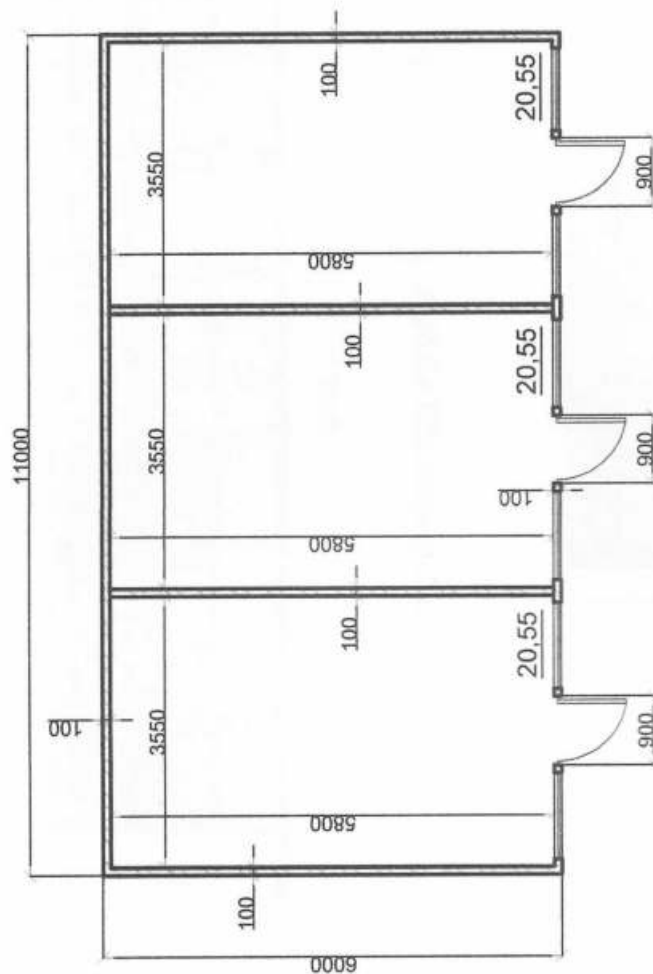

Директор ТОВ "Архітектурне Бюро "Аркадія" Смальдій Д.П.
 Архітектор Глінін Д.Ю.
 Кваліфікаційний сертифікат серія АА №002560



Площа земельної ділянки згідно з документами на
землекористування - землі міста



- 1) місце розташування ТС;
- 2) червона лінія;
- 3) регулювання забудови;
- 4) місця підключення до інженерних мереж

Умовні позначення:

-  - межа благоустрою ділянки розміщення ТС
-  - існуюча ТС
-  - існуючі дороги
-  - існуючі будівлі

Директор ТОВ "Архітектурне Бюро "Аркан" _____

Архітектор

Кваліфікаційний сертифікат серія АА №002590

АРХІТЕКТУРНЕ


Блісін Д.Ю.

Идент. код
40175885



СИТУАЦІЙНИЙ ПЛАН М 1:2000

Місце розміщення об'єкту

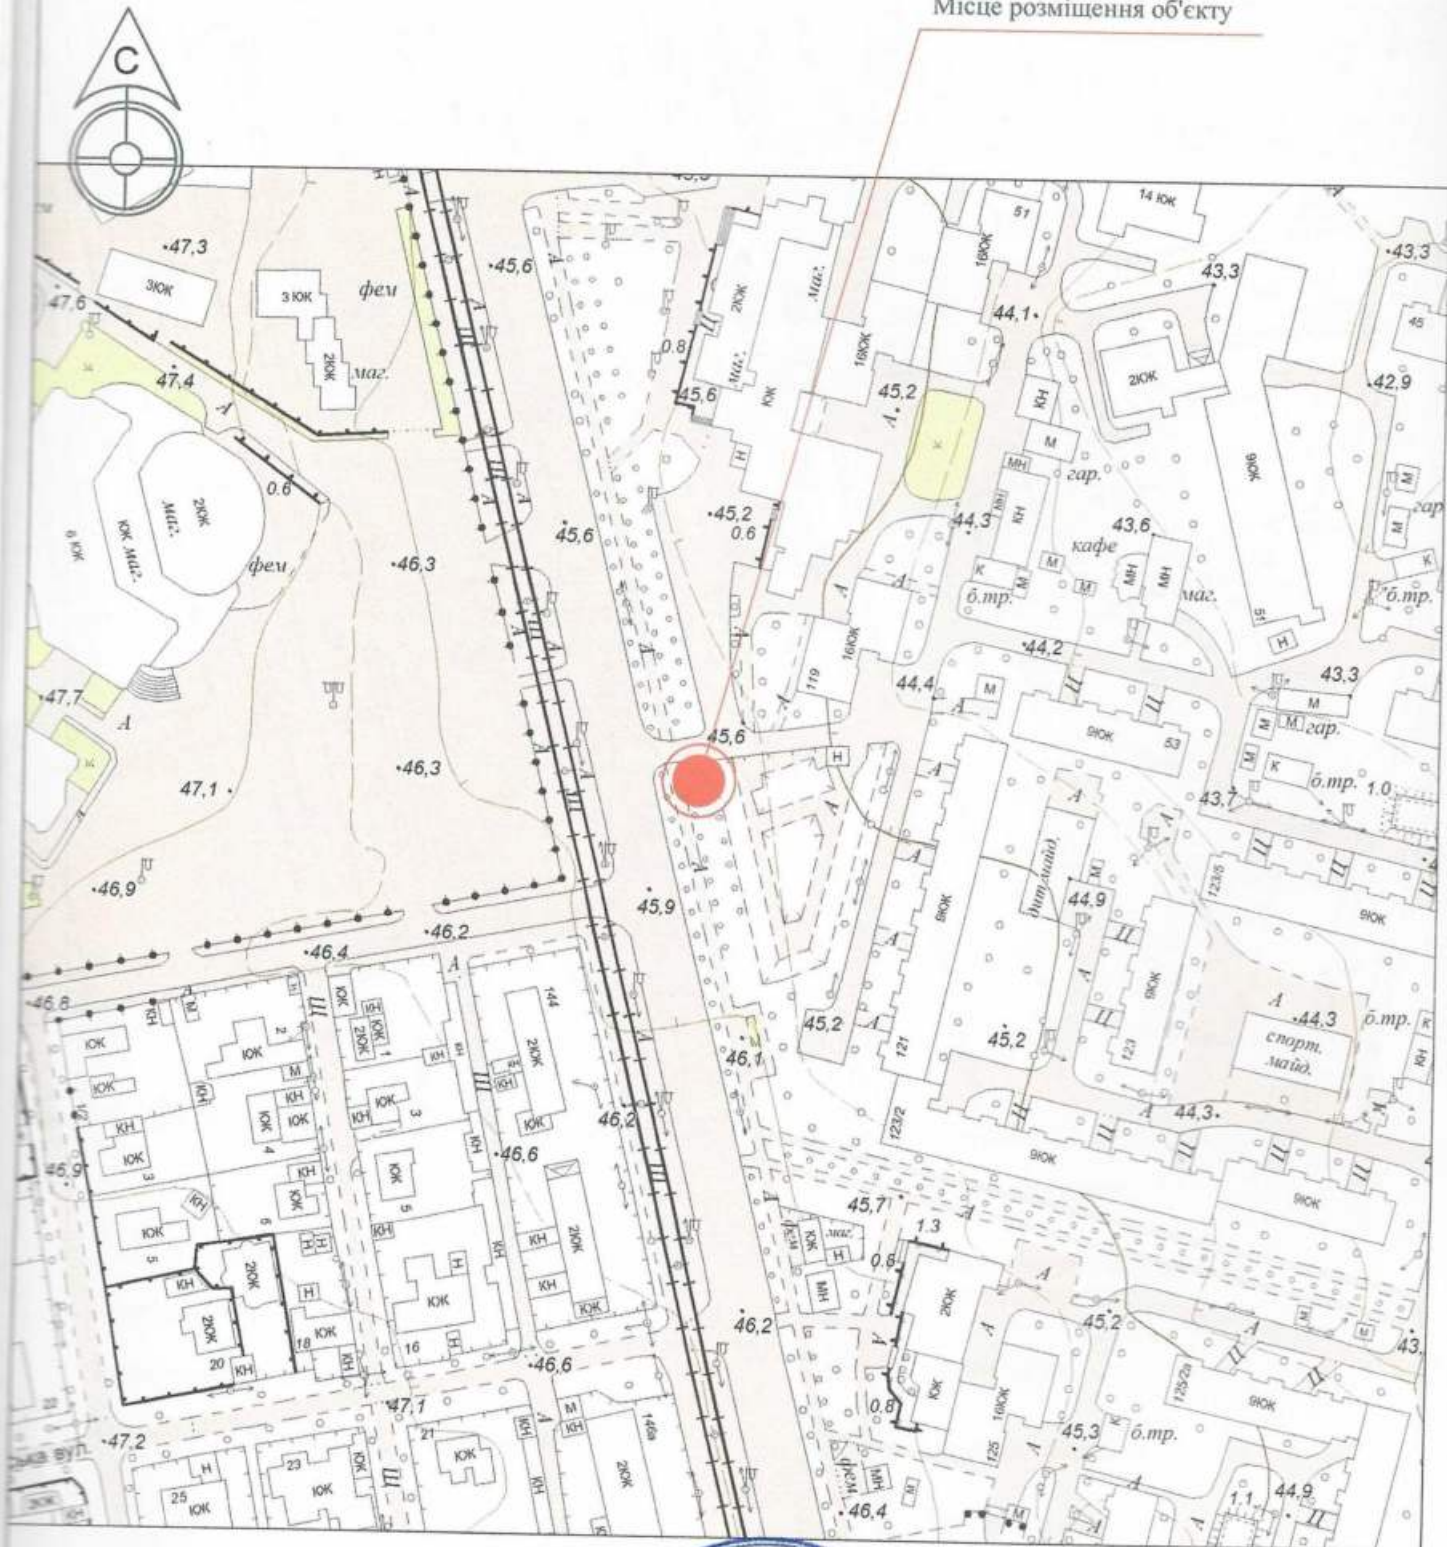

Директор ТОВ "Архітектурне Бюро "Аркадія" * Україна * Товариство з обмеженою відповідальністю * Маглій Д.П.

Архітектор

Кваліфікаційний сертифікат серія АА №002590



ліній Д.Ю.