

ПОЯСНЮВАЛЬНА ЗАПИСКА

Тимчасова споруда являє собою одноповерхову споруду, яка виконується зі збірних металевих конструкцій та встановлюється безпосередньо на існуюче покриття. За умовну позначку 0,000 прийнятий рівень чистої підлоги ТС.

Грунт вогнестійкості тимчасової споруди III а.

Баритні розміри в плані – 4,8 X 2,8 м.

Висота павільйону від рівня землі – 3,30 м.

Запроектований ТС має вхід з головного фасаду. Торгівля передбачається в приміщенні відкритого типу.

Стіни споруди запроектовані по типу "Сендвич" товщиною 100 мм із утеплювачем з каптової вати й обшивкою. Обшивка стін по каркасу: зовнішня – алюмінієві сандвіч панелі; внутрішня (стіни й стеля) – металопластикові вагонки.

Підлоги передбачені з покриттям дошки 40 мм і утеплювачу та покриттям з деревного матеріалу.

Заповнення прорізів з метало пластикового профілю та рольгратами.

Покрівля – по металевих прогонах і решетуванню з покриттям із профільованого листового листа, з утеплювачем з мінераловатних плит, гідро- і пароізоляцією.

Водостік передбачити зовнішній організований по жолобах і риннам.

Зовнішня обробка:

Зовнішня стін – колірні алюмінієві сандвіч панелі, типа «Алюкобонд»;

Зовнішня – металопластикові;

Зовнішня – металопластикові;

Покрівля – профільований сталевий лист;

Зовнішня – колірні алюмінієві сандвіч панелі

Підрозробка вирішення фасадів дивись графічний додаток.

Внутрішню обробку виконати згідно індивідуального дизайну-проекту із застосуванням негорючих оздоблювальних матеріалів, з підтвердженням сертифікатом.

2. Підключення до інженерних мереж:- тимчасова споруда підключається до місцевої електромережі, згідно договору про постачання електричної енергії.

Опалювання – електричне з встановленням навісних електро - конвекторів з регулюванням температури.




Вітлення приміщення виконане стельовими світильниками з люмінесцентними лампами.

Назва об'єкта, адреса розміщення Тимчасова споруда (стаціонарна) вул. Варненська, 15 (згідно схеми посадки)	Посада виконавця	ПІБ	Підпис
	Архітектор	Давидова В.В.	
М.П.	Кваліфікаційний сертифікат, серія АА № 002057		




ФАСАДИ В ОСЯХ 1-2
М 1:50

ФАСАДИ В ОСЯХ А-Б
М 1:50

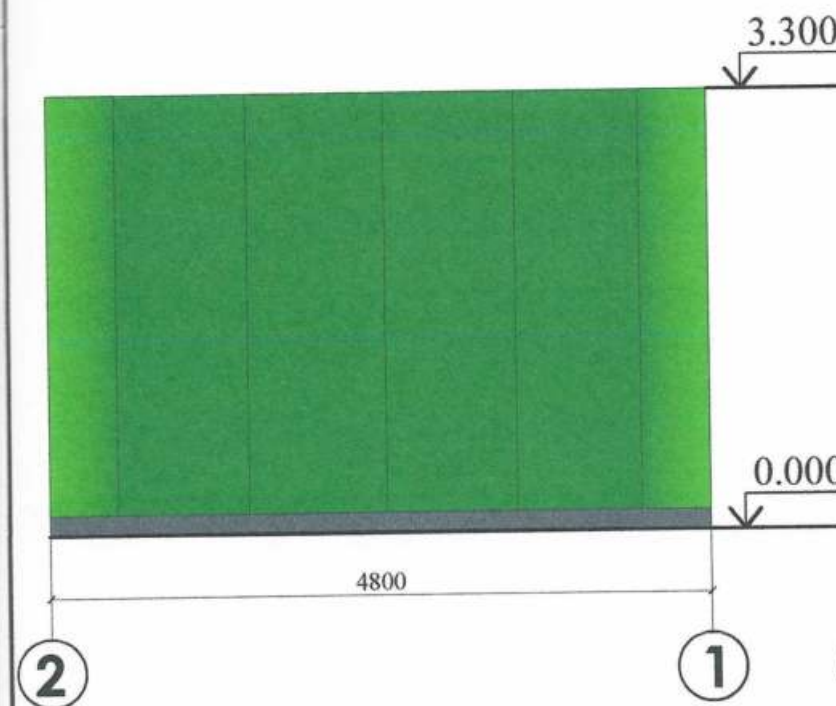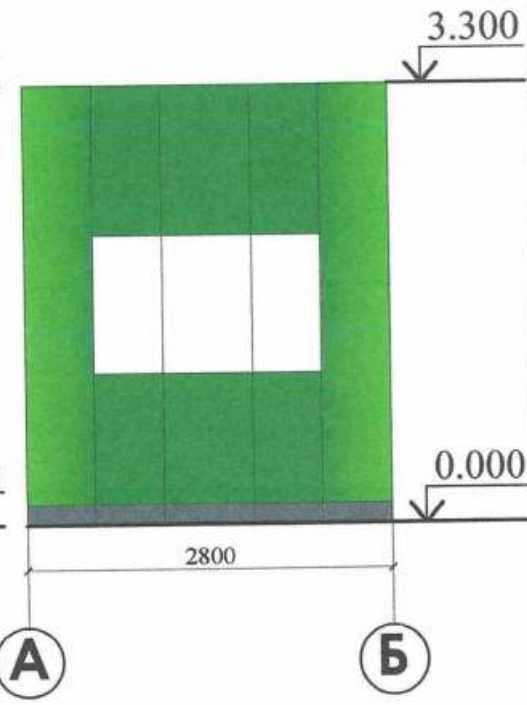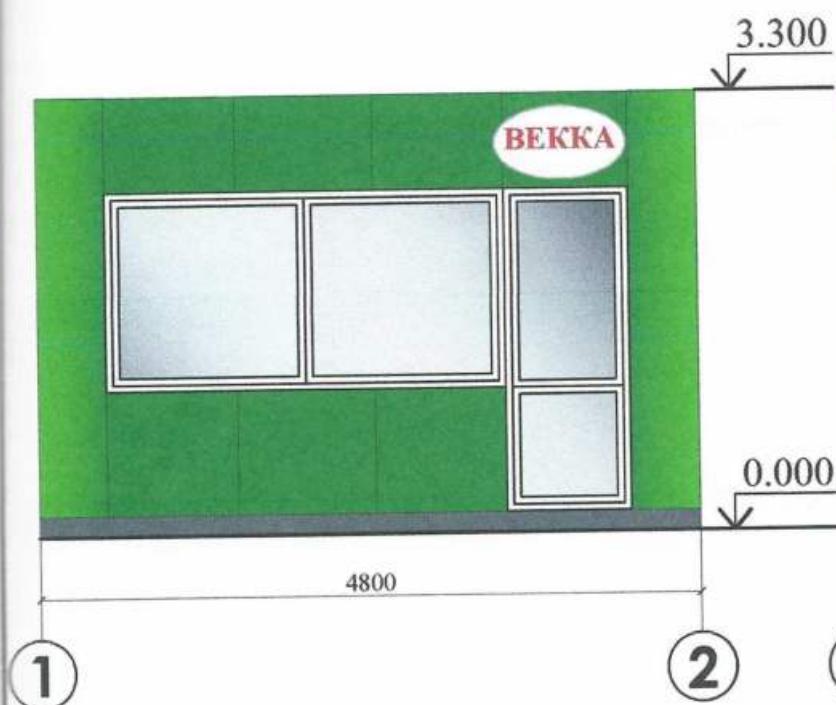

Тимчасова споруда - (заг. площею 13,44 кв.м.) по продажу товарів змішаної групи за адресою: м. Одеса, вул. Варненська, 15	Посада виконавця	ПІБ
	Архітектор	Давидова В.В.
М.П.	Кваліфікаційний сертифікат, серія АА № 002057	
	Дата складання ____ 20__ року	

ПЛАН НА ОТМ. 0.000

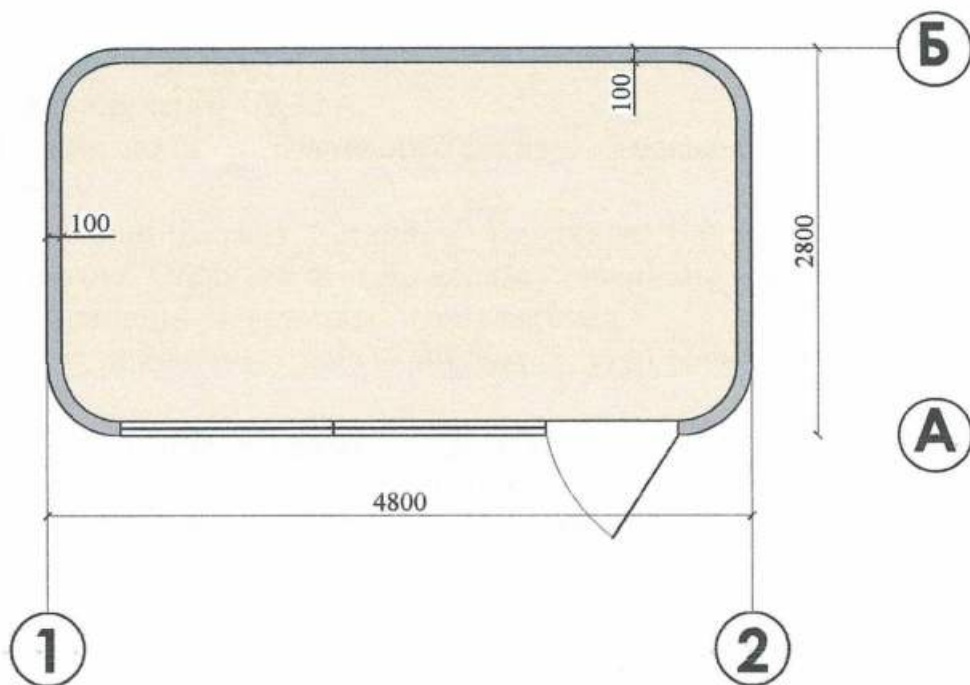

Тимчасова споруда - (заг. площею 13,44 кв.м.) по
продажу товарів зм'яганої групи за адресою:
М.Одеса, вул. Барненська, 15

М.П.

Посада виконавця

ПБ

Підпис

Архітектор


Давидова В.В.

Кваліфікаційний сертифікат, серія АА № 002057

Дата складання ____ 20__ року

СХЕМА РОЗМІЩЕННЯ ТС М 1:500

Документи на землекористування відсутні

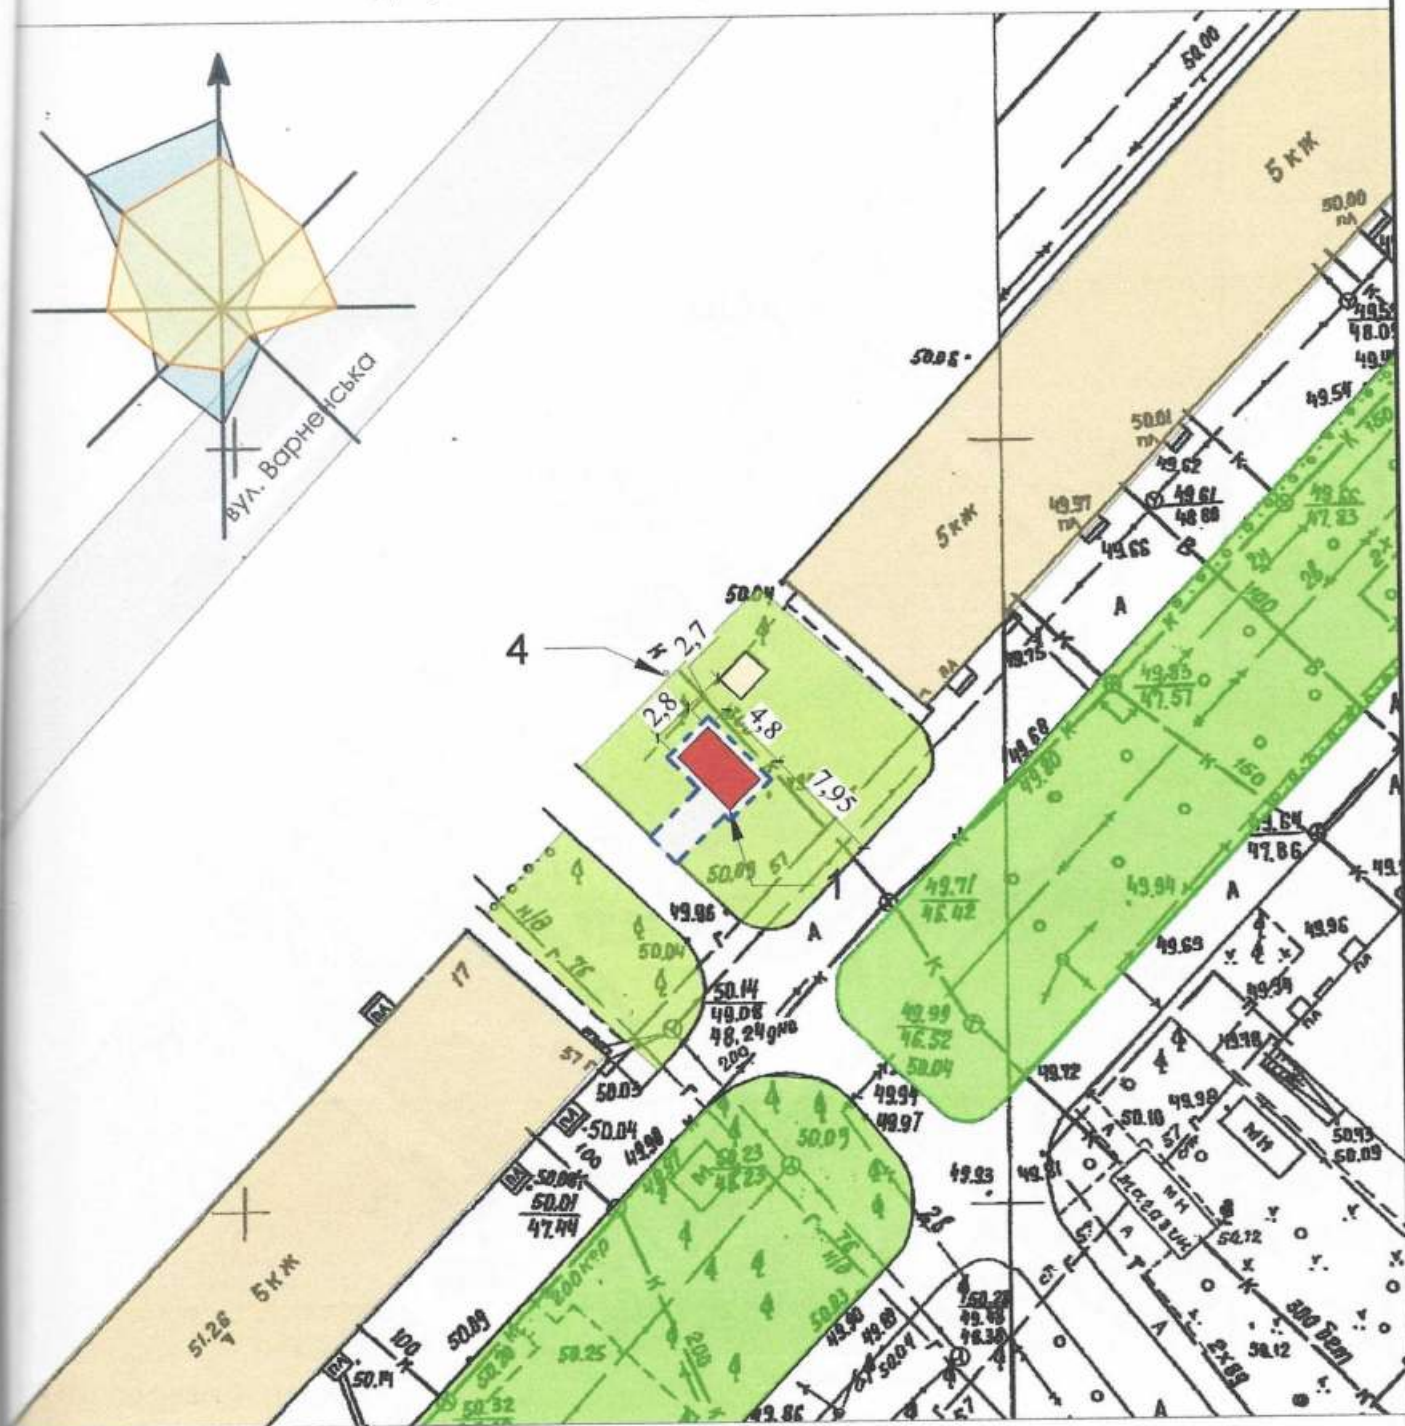

Експлікація:

- 1) місце розташування ТС;
- 2) червоні лінії;
- 3) лінії регулювання забудови;
- 4) місця підключення до інженерних мереж.

Умовні позначення

- Існуючі споруди
- Озеленення
- Тимчасова споруда
- Територія, що підлягає благоустрою

Тимчасова споруда - (заг. площею 13,44 кв.м.) по продажу товарів змішаної групи за адресою: м. Одеса, вул. Варненська, 15

М.П.

Посада виконавця

ПІБ

Підпис

Архітектор


Давидова В.В.

Кваліфікаційний сертифікат, серія АА № 002057

Дата складання _____ 20__ року

СИТУАЦІЙНИЙ ПЛАН


М 1:2000

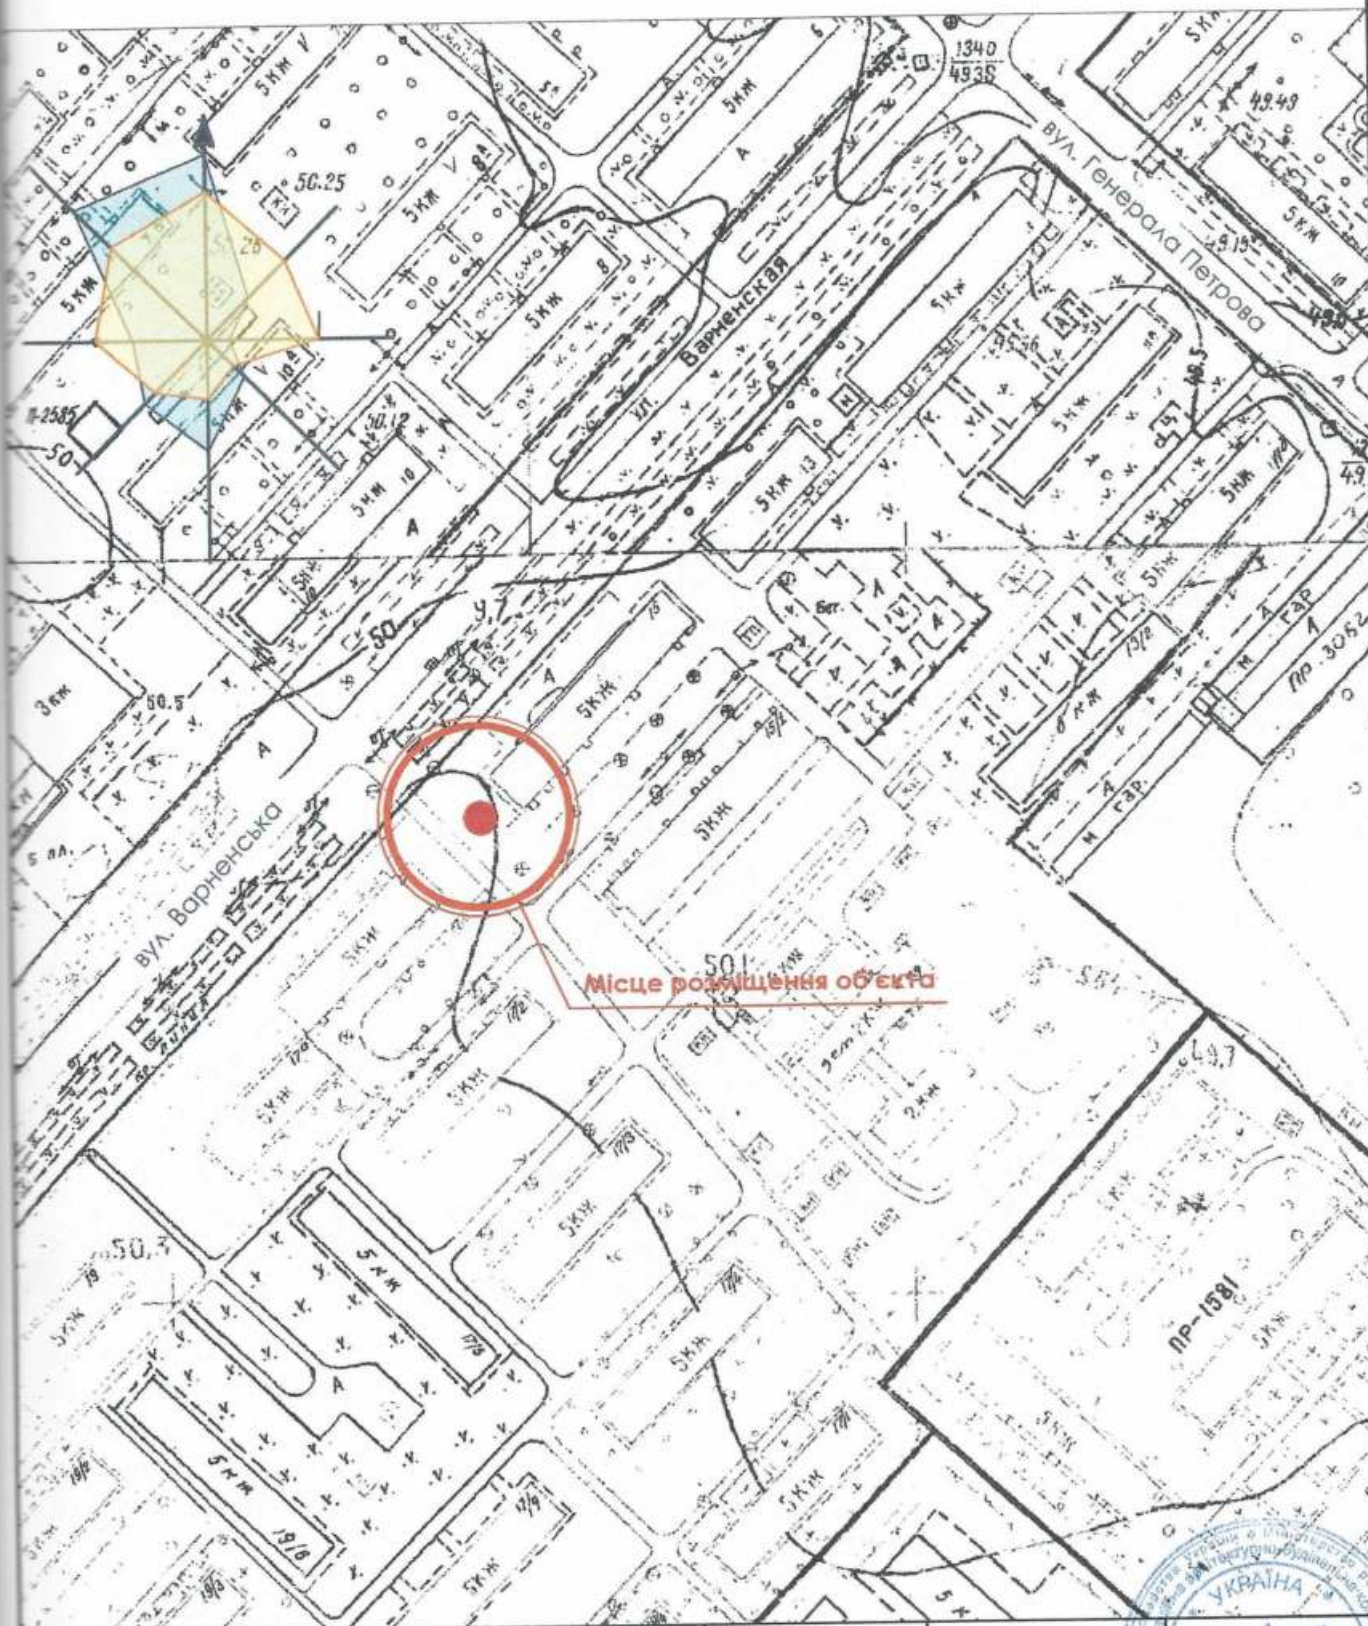

Тимчасова споруда - (заг. площею 13,44 кв.м.) по продажу товарів змішаної групи за адресою: м. Одеса, вул. Варненська, 15	Посада виконавця	ГПБ
	Архітектор	Давидова В.В.
М.П.	Кваліфікаційний сертифікат, серія АА № 002057	
	Дата складання ____ 20 ____ року	



Ситуаційний план, М1:2000

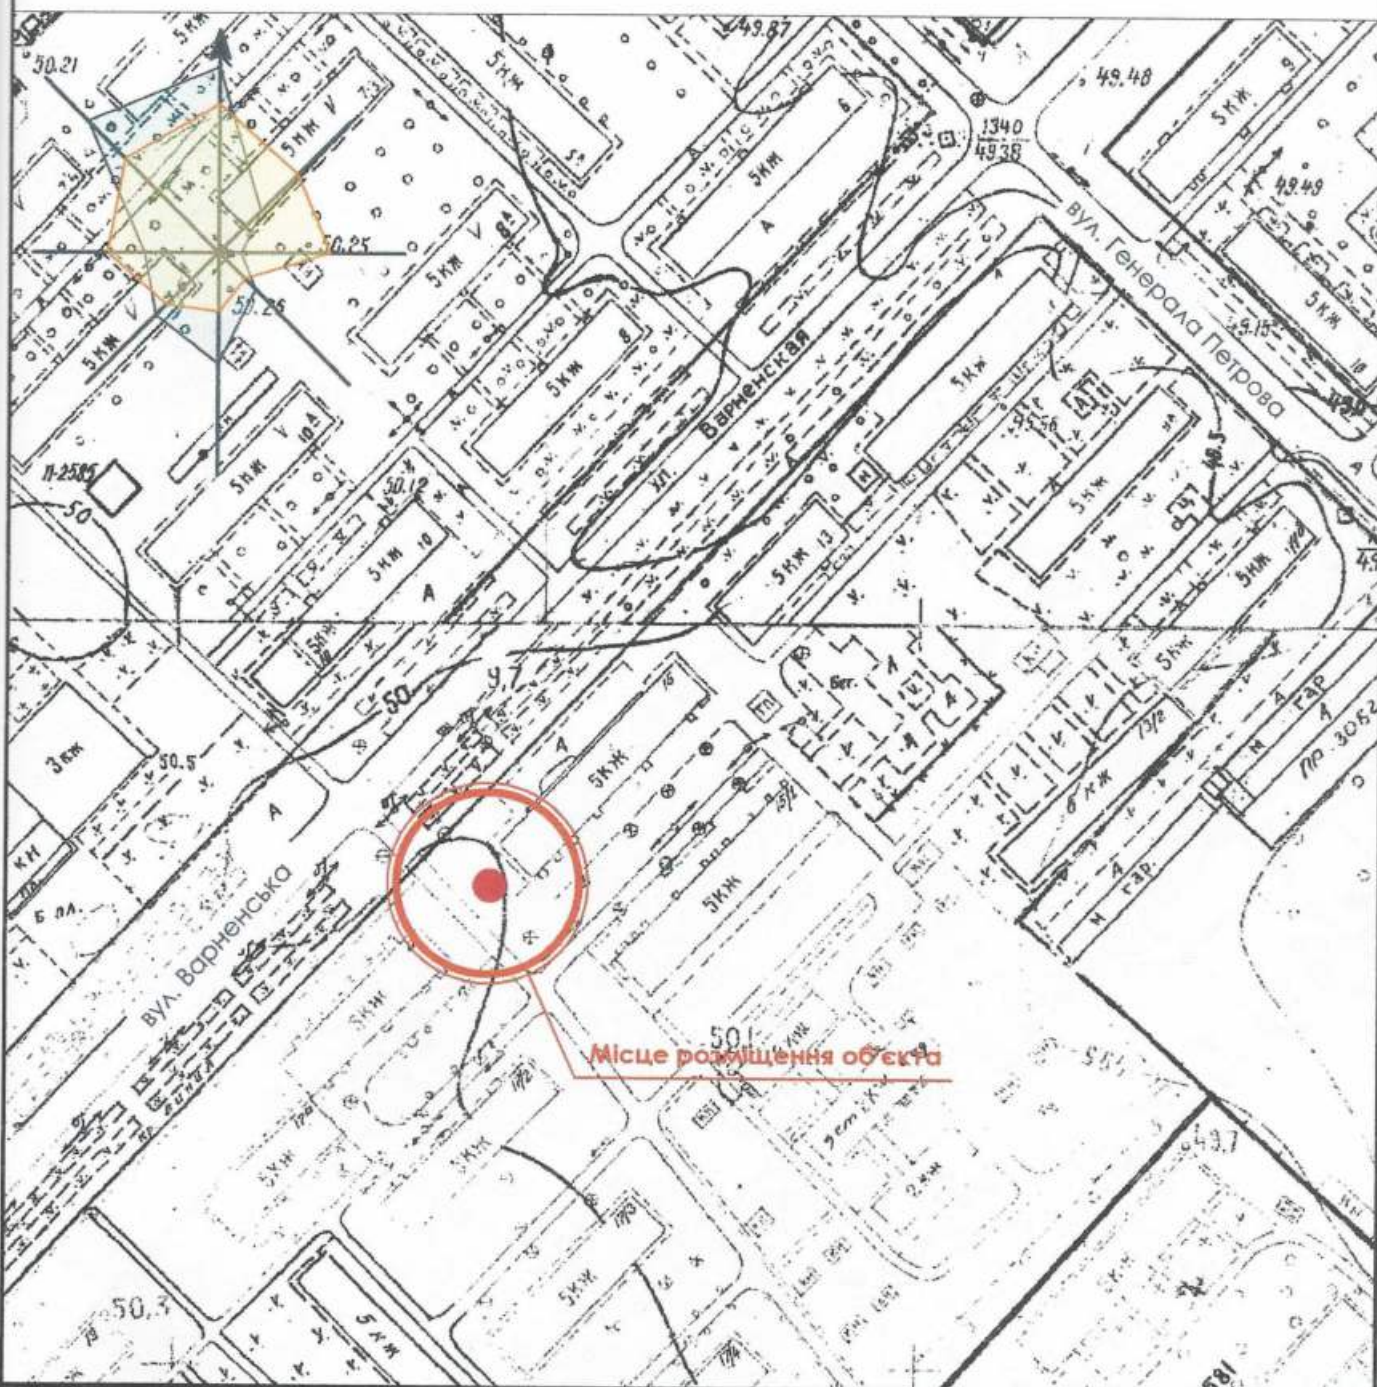

601-12-2014

Замовник: ТОВ "ВЕККА"

Посада ПІБ Підпис Дата

архітектор

Давидова В.В.

01.12.2014

Тимчасова споруда - (заг. площею 13,44 кв.м.) по продажу товарів змішаної групи за адресою:
м. Одеса, вул. Варненська, 15

Стадія

Лист

Листов

2


Ситуаційний план, М1:2000

архітектор Давидова В.В.
кваліфікаційний сертифікат
серія АА № 002057

Генеральний план, М 1:500

Умовні позначення

- Існуючі клумби, газони
- Проїздна частина вулиць
- Існуюча забудова
- Тимчасова споруда

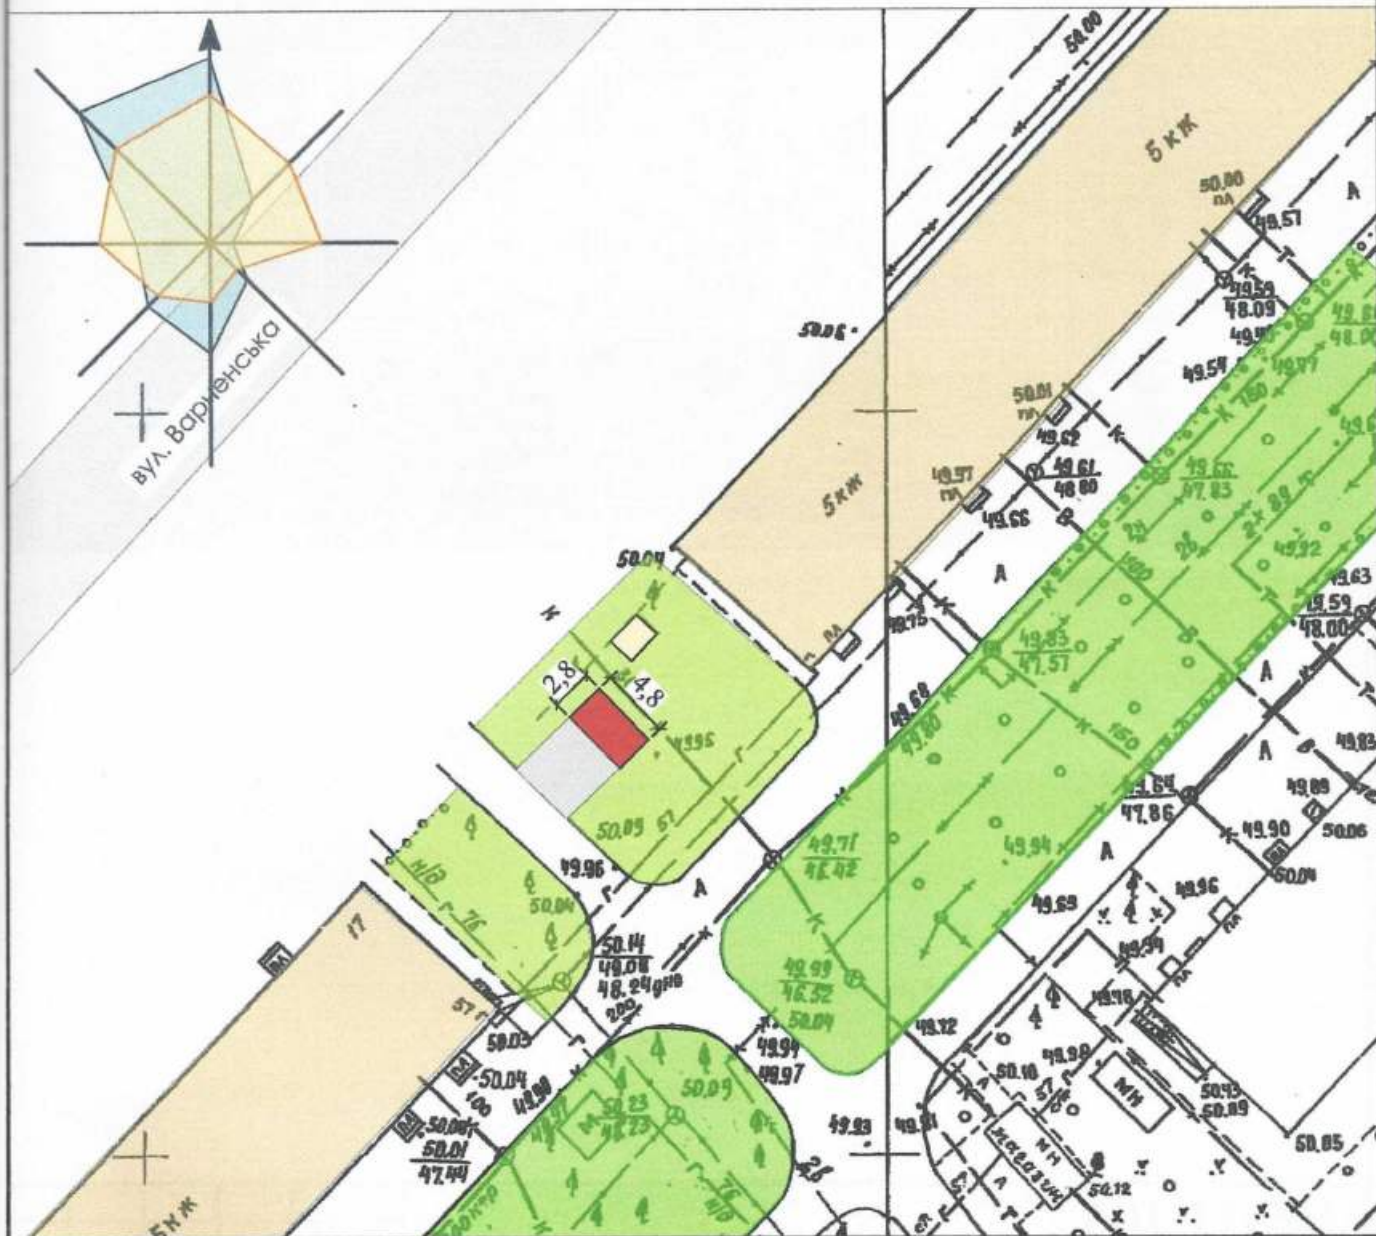

601-12-2014

Замовник: ТОВ "ВЕККА"

Посада	ПІБ	Підпис	Дата	Тимчасова споруда - (заг. площею 13,44 кв.м.) по продажу товарів змішаної групи за адресою: м. Одеса, вул. Варненська, 15			Стадія	Лист	Листов
архітектор	Давидова В.В.		01.12.2014					3	
Генеральний план, М1:500				архітектор Давидова В.В. кваліфікаційний сертифікат серія АА № 002057					