

ПОЯСНЮВАЛЬНА ЗАПИСКА

1. Тимчасова споруда являє собою одноповерхову споруду, яка виконується зі збірно-розбірних металевих конструкцій та встановлюється безпосередньо на існуюче покриття.

За умовну позначку 0,000 прийнятий рівень чистої підлоги ТС.

Ступінь вогнестійкості тимчасової споруди III а.

Габаритні розміри в плані – 4,8 X 2,8 м.

Висота павільйону від рівня землі – 3,30 м.

Запроектований ТС має вхід з головного фасаду. Торгівля передбачається в приміщенні відкритого типу.

Стіни споруди запроектовані по типу “Сендвич” товщиною 100 мм із утеплювачем з мінеральної вати й обшивкою. Обшивка стін по каркасу: зовнішня – алюмінієві сандвіч панелі; внутрішня (стіни й стеля) – металопластикові вагонки.

Підлоги передбачені з покриттям дошки 40 мм і утеплювачу та покриттям з негорючого матеріалу.

Заповнення прорізів з метало пластикового профілю та рольгратами.

Покрівля – по металевих прогонах і решетуванню з покриттям із профільованого сталевих листа, з утеплювачем з мінераловатних плит, гідро- і пароізоляцією.

Водостік передбачити зовнішній організований по жолобах і ринвам.

Зовнішня обробка:

Поверхні стін – колірні алюмінієві сандвіч панелі, типа «Алюкобонд»;

Вікна – металопластикові;

Двері – металопластикові;

Покрівля – профільований сталевий лист;

Доколь – колірні алюмінієві сандвіч панелі

Колірне вирішення фасадів дивись графічний додаток.

Внутрішню обробку виконати згідно індивідуального дизайну-проекту із застосуванням негорючих оздоблювальних матеріалів, з підтвердженням сертифікатом.

2. Підключення до інженерних мереж:- тимчасова споруда підключається до існуючої електромережі, згідно договору про постачання електричної енергії.


Опалювання – електричне з встановленням навісних електро - конвекторів з регулюванням температури.

Освітлення приміщення виконане стельовими світильниками з люмінесцентними лампами.




Назва об'єкта, адреса розміщення Тимчасова споруда (стаціонарна) вул. Корольова, 37 кут Ак. Глушка, 12 (згідно схеми посадки)	Посада виконавця	ПІБ	Підпис
	Архітектор	Давидова В.В.	
М.П.	Кваліфікаційний сертифікат, серія АА № 002057		



ФАСАДИ В ОСЯХ 1-2
М 1:50

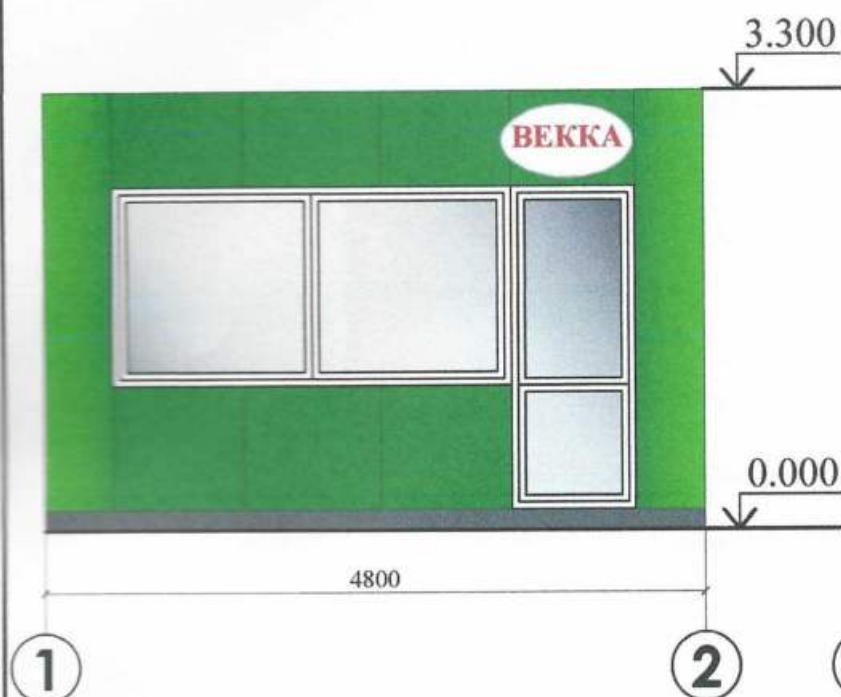

ФАСАДИ В ОСЯХ А-Б
М 1:50

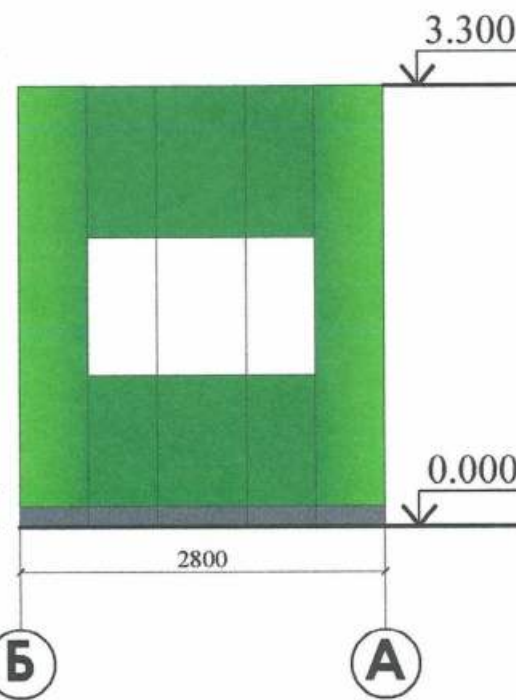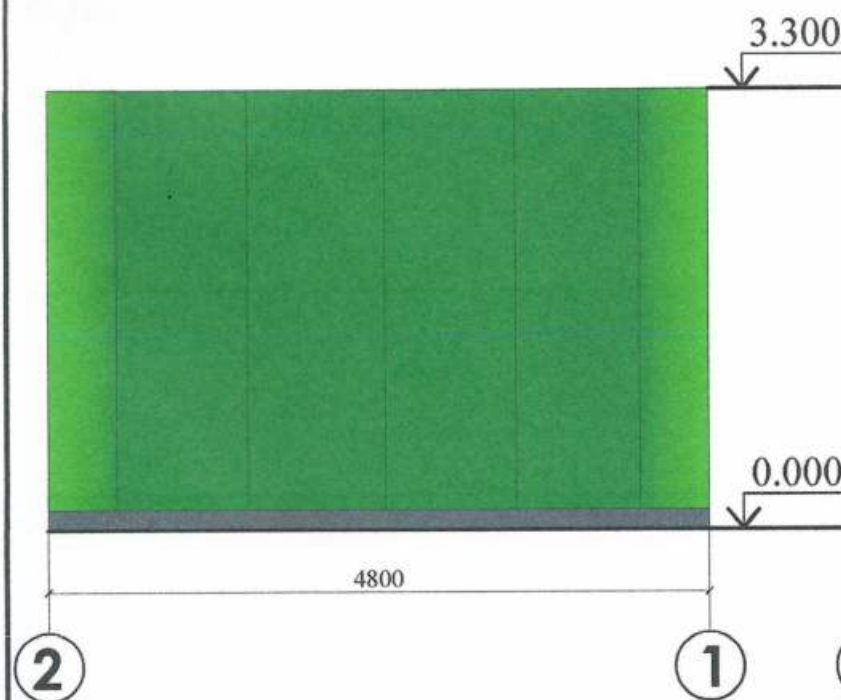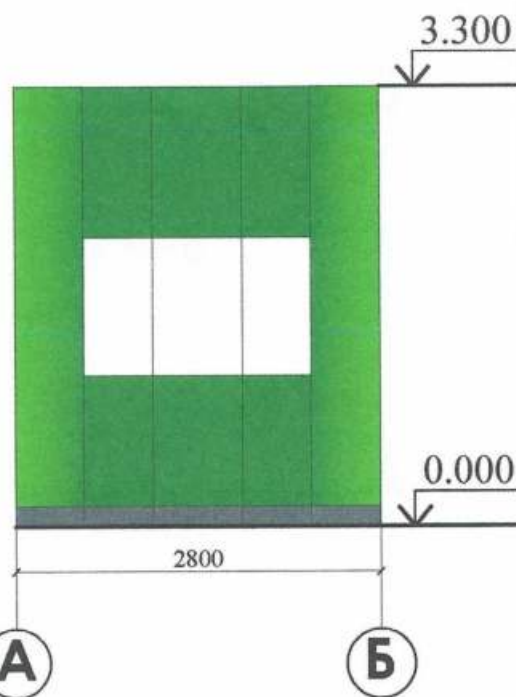

Тимчасова споруда - (заг. площею 13,44 кв.м.) по
продажу товарів змішаної групи за адресою:
м. Одеса, вул. Корольова, 37 кут Ак. Глушка, 12

М.П.

Посада виконавця

ГПБ

Архітектор


Давидова В.В.

Кваліфікаційний сертифікат, серія АА № 002057

Дата складання ____ 20__ року



ПЛАН НА ОТМ. 0.000

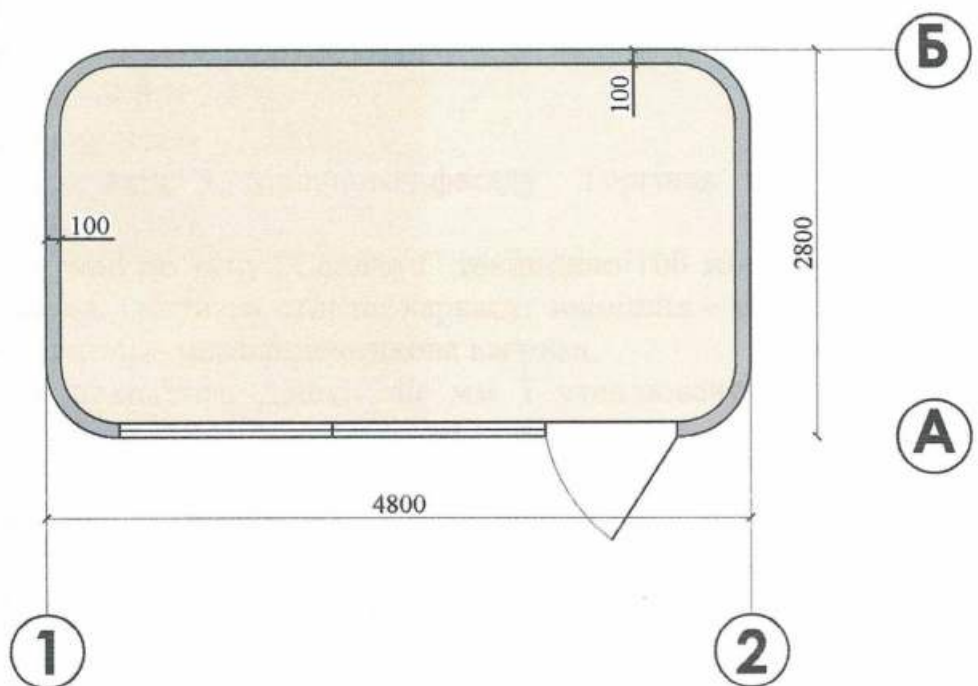

Тимчасова споруда - (заг. площею 13,44 кв.м.) по
введенню в експлуатацію згідно з проектною групою за адресою:
м. Одеса, вул. Королева, 37 кут Ак. Глушка, 12

М.П.

Посада виконавця

ПІБ

Підпис

Архітектор


Давидова В.В.

Кваліфікаційний сертифікат, серія АА № 002057

Дата складання _____ 20____ року

СХЕМА РОЗМІЩЕННЯ ТС М 1:500

Документи на землекористування відсутні

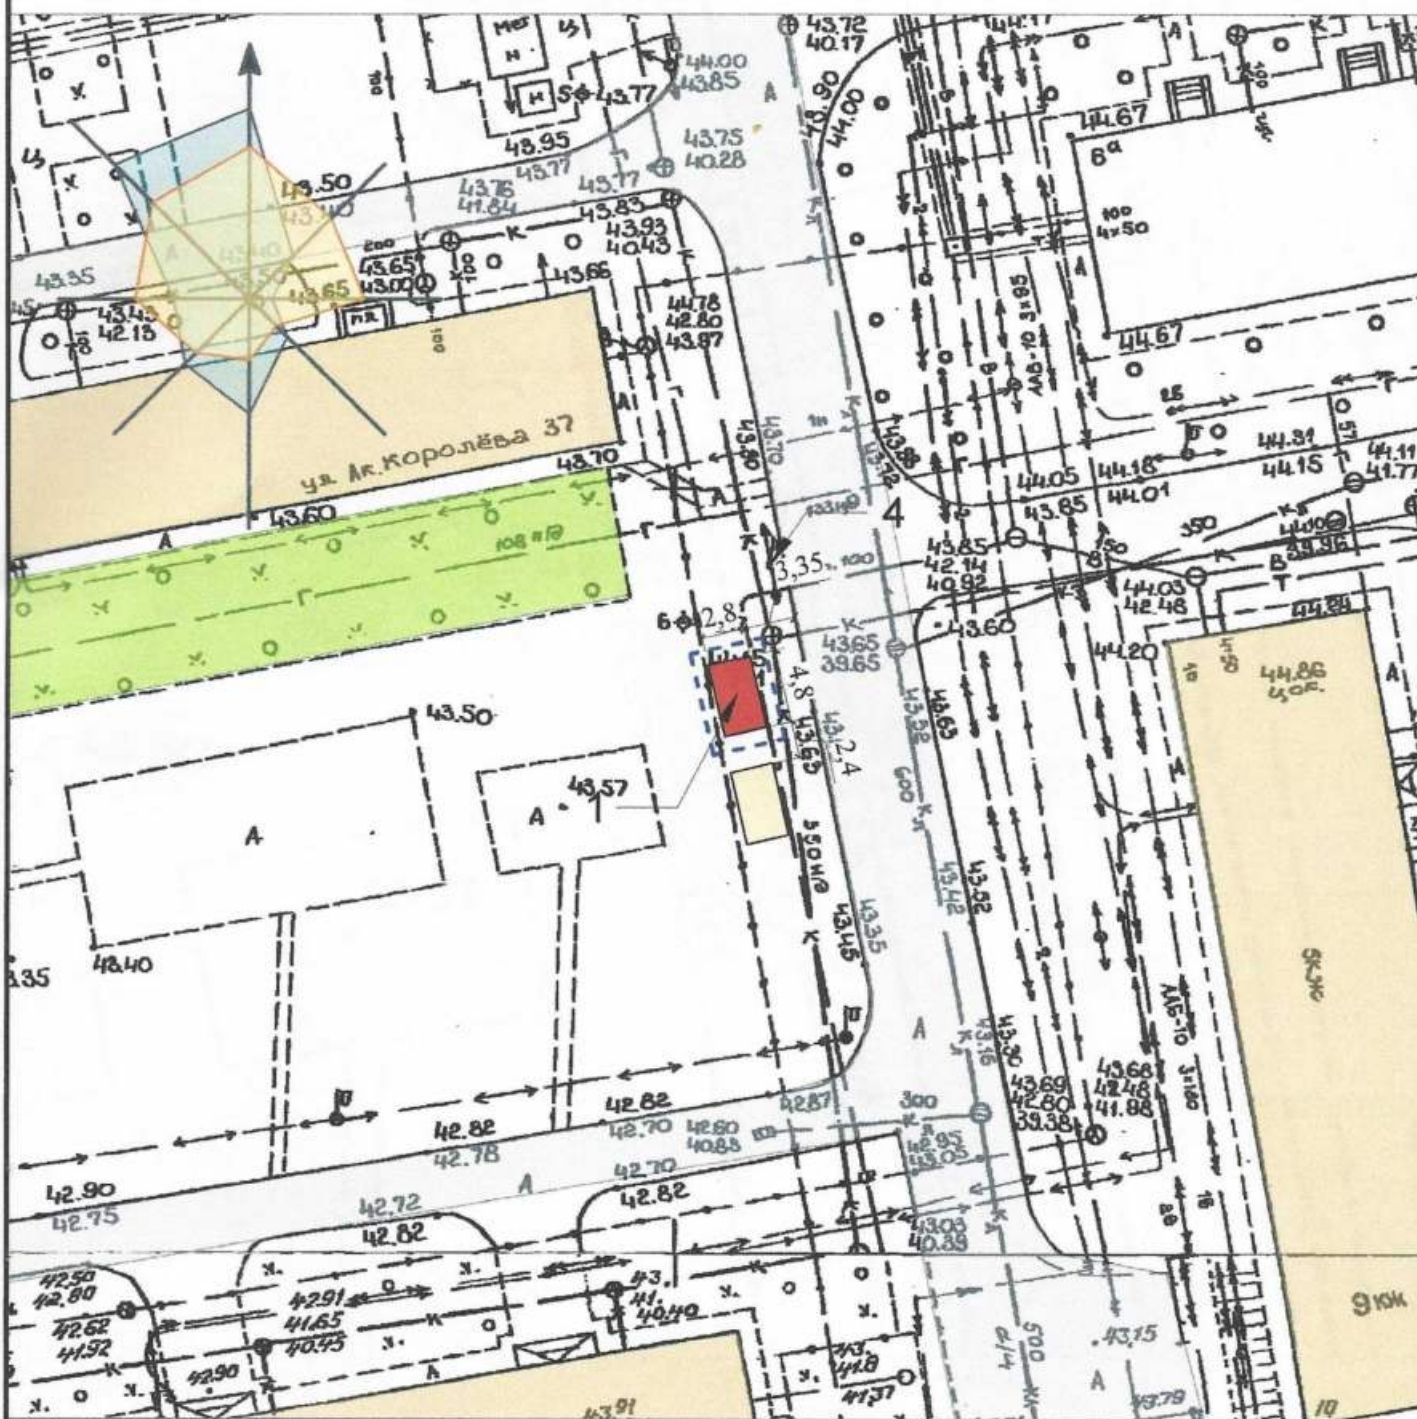

Експлікація:

- 1) місце розташування ТС;
- 2) червоні лінії;
- 3) лінії регулювання забудови;
- 4) місця підключення до інженерних мереж.

Умовні позначення

- Існуючі споруди
- Озеленення
- Тимчасова споруда
- Територія, що підлягає благоустрою

Тимчасова споруда - (заг. площею 13,44 кв.м.) по
продажу товарів змінної групи за адресою:
м. Одеса, вул. Корольова 37, кут А. Глушка, 12

М.П.

Посада виконавця

ПІБ

Підпис

Архітектор


Давидова В.В.

Кваліфікаційний сертифікат, серія АА № 002057

Дата складання _____ 20__ року

СИТУАЦІЙНИЙ ПЛАН

М 1:2000

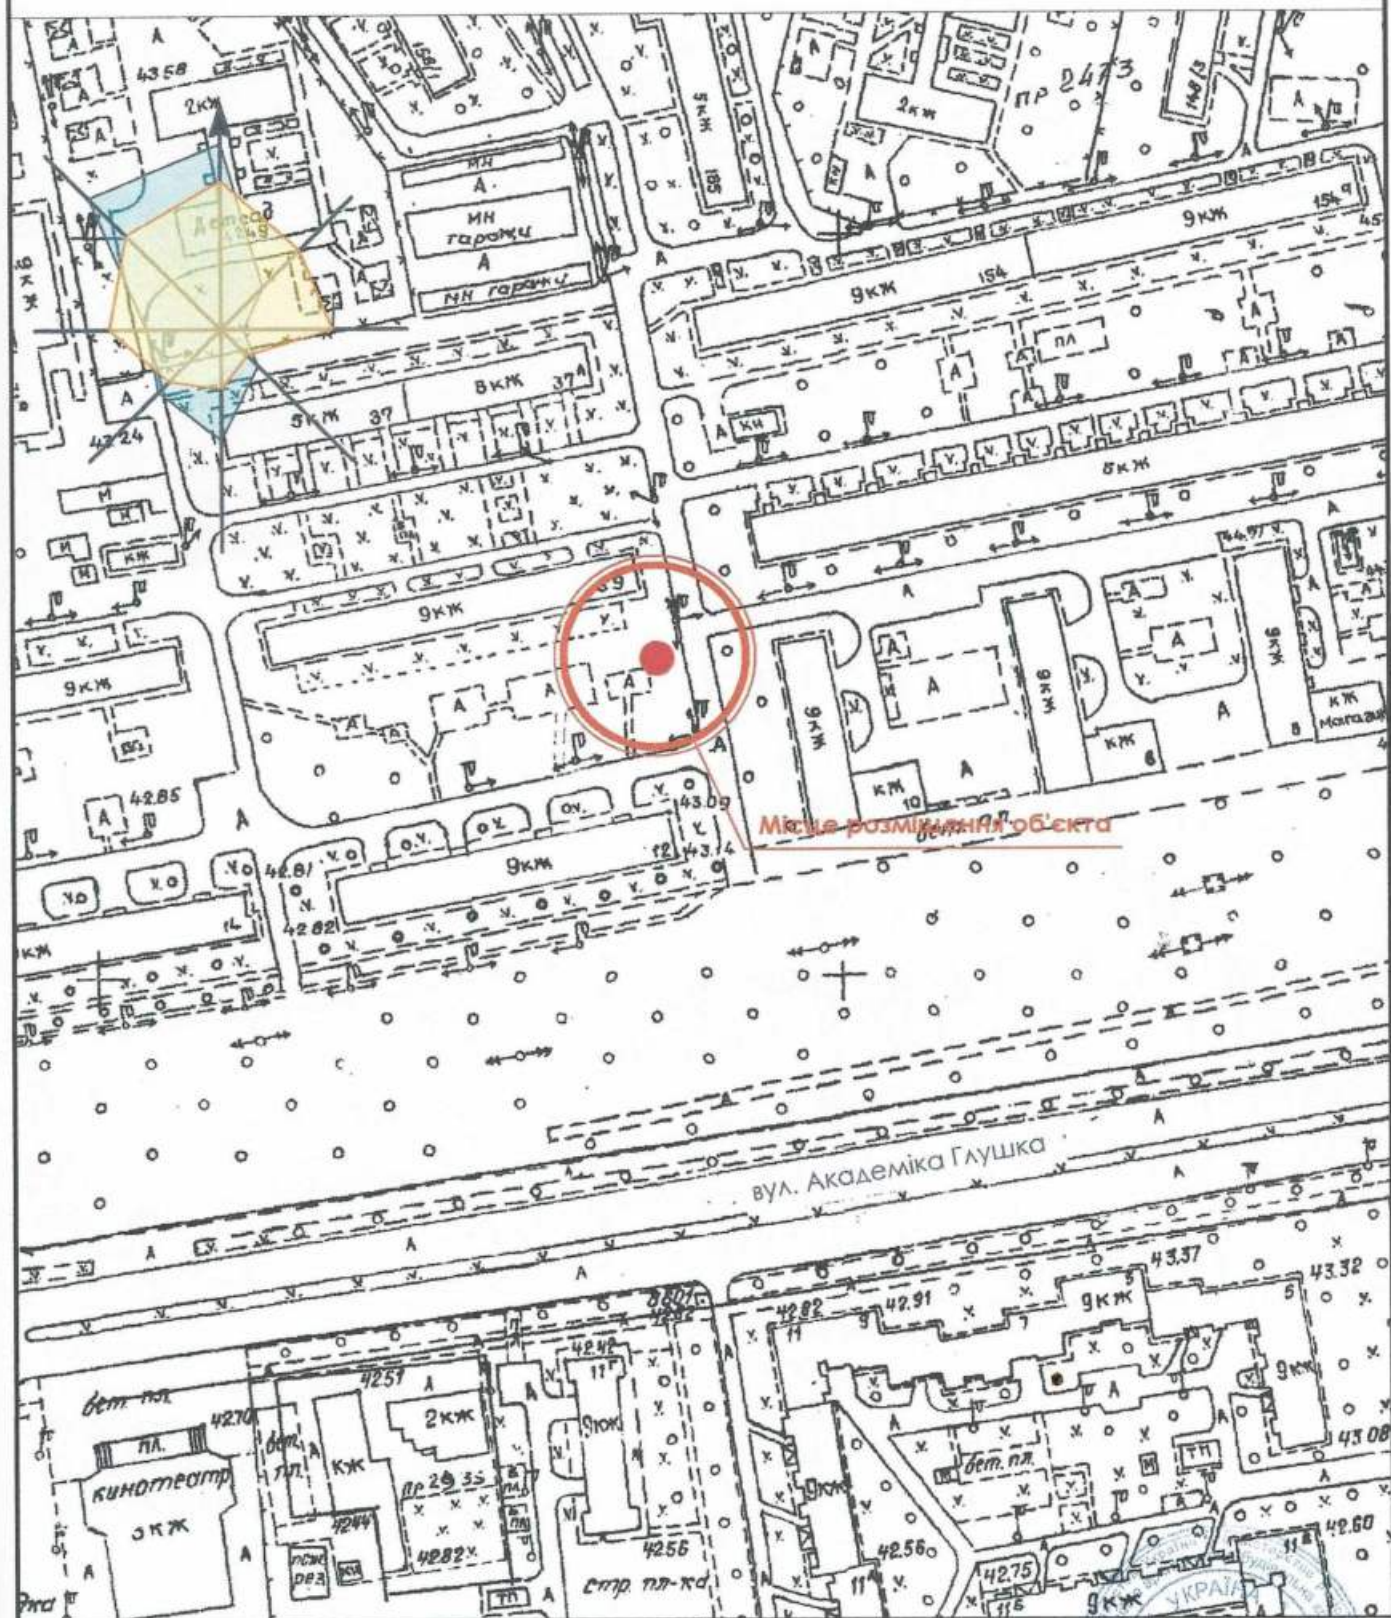

Тимчасова споруда - (заг. площею 13,44 кв.м.) по
продажу товарів змішаної групи за адресою:
м. Одеса, вул. Корольова, 37 кут Ак. Глушка, 12

Посада виконавця

ПІБ

Архітектор Підпис

Архітектор

Давидова В.В.

М.П.

Кваліфікаційний сертифікат, серія АА № 002057

Дата складання _____ 20__ року