

СТИСЛА ПОЯСНЮВАЛЬНА ЗАПИСКА

1. Стационарна тимчасова споруда для здійснення підприємницької діяльності має торговельне приміщення для тимчасового перебування людей.

За умовну позначку +0.000 прийнятий рівень чистої підлоги ТС.

Ступінь вогнестійкості – IIIб

Стационарна тимчасова споруда являє собою кіоск прямокутної форми в плані, максимальні габаритні розміри – 3,5 м x 7,0 м.

Загальна площа ТС – 24,5 м².

Внутрішня висота кіоска від рівня чистої підлоги складає – 2,50 м.

Загальна висота складає – 3,0 м.

Тимчасова споруда встановлюється без влаштування фундаменту на існуючу тротуарну плитку.

Стіни споруд запроектовані товщиною 100 мм із утеплювачем із мінеральної вати та обшивкою з обох сторін.

Обшивка стін по каркасу: зовнішня – дерев'яні дошки з імітацією зрубу; внутрішня (стіни та стеля) – гіпсокартонні листи.

Підлога – дерев'яні дошки 40 мм по металевому каркасу з утеплювачем з мінераловатних плит та покриттям з негорючого матеріалу.

Покрівля – по металевим прогонам і решитуванню з покриттям профільованими листами, з утеплювачем з мінераловатних плит, гідро- і пароізоляцією.

Зовнішня обробка:

стіни – композитні матеріали типу «Алюкобонд»;

вікна – металопластикові з вакуумними склопакетами;

двері – металеві;

покрівля – покрівельні профільовані металеві листи.

2. Стационарна тимчасова споруда підключається до мереж електропостачання згідно з діючими нормами та ТУ. Точка підключення – згідно з ТУ. ТУ на підключення об'єкту до інженерних мереж замовник отримує самостійно.

Опалення – електричне з встановленням навісних електро-конвекторів з регулюванням температури.

Освітлення приміщення виконується світильниками з люмінесцентними лампами.

Розподільні мережі виконані проводами з мідними жилами, що прокладені у трубах та приховані в обшивці стін.

Захист мереж від дії струмів коротких замикань та перевантажень здійснюється автоматичними вимикачами щитка.

3. Благоустрій прилеглої території виконується згідно з планом благоустрою.

Освітлення території передбачене світильниками, що розміщуються на головному фасаді під покрівлею тимчасової споруди.

ФОП (201035000000013361)

Архітектор

Кваліфікаційний сертифікат серія АА №002647



Громова О.Р.


Громова О.Р.

ЕСКІЗИ ФАСАДІВ ТС М 1:50

Головний фасад



Бічний фасад

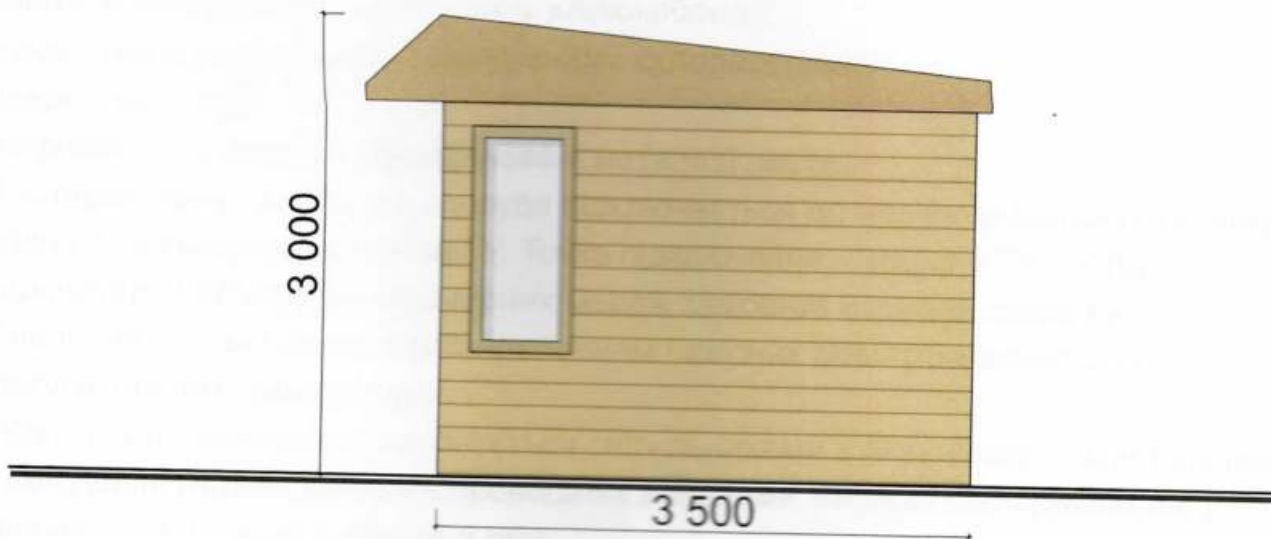

ФОП (2010350000000013361)

Архітектор


Кваліфікаційний сертифікат серія АА №002647



Громова О.Р.

Громова О.Р.

ПЛАН ТС М 1:50

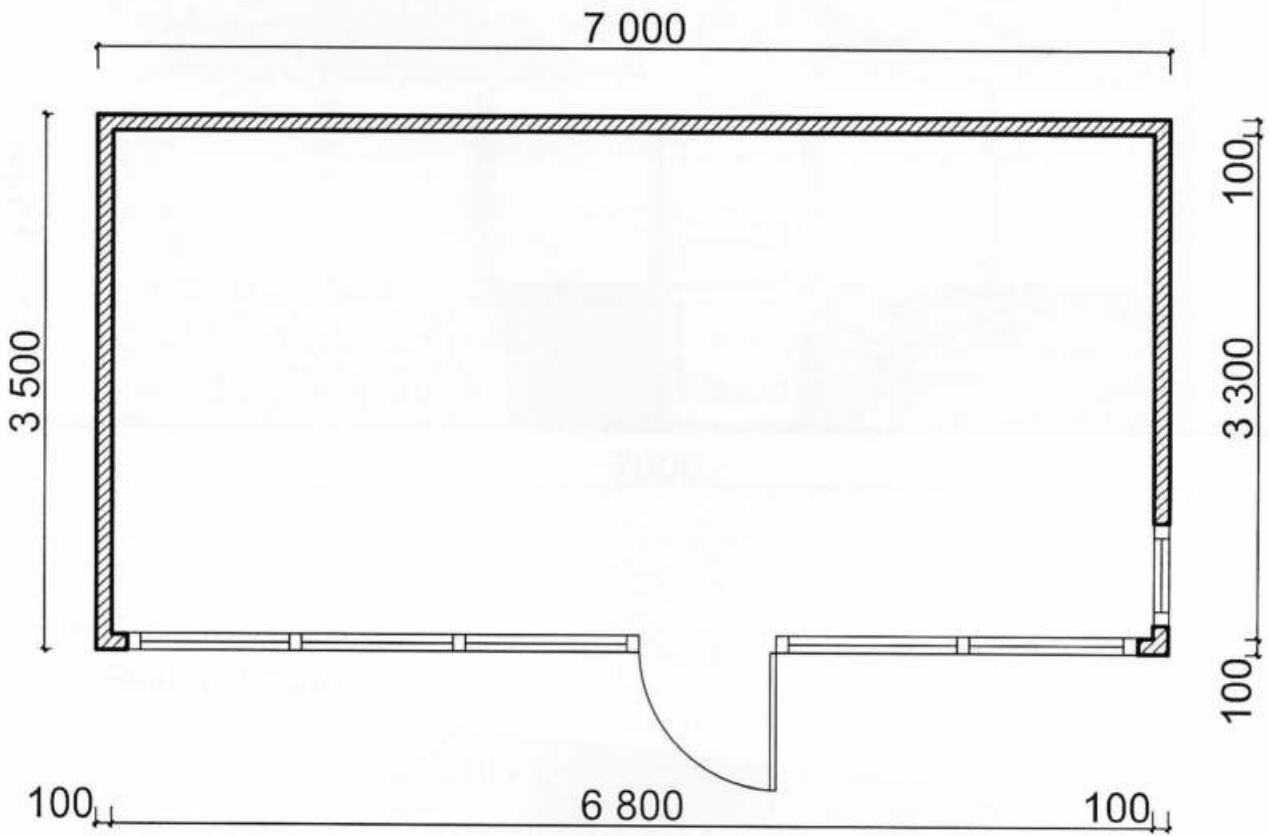

ФАП (2010350000000013361)

Архітектор

Кваліфікаційний сертифікат серія АА №002647



Громова О.Р.

Громова О.Р.

СХЕМА РОЗМІЩЕННЯ ТС М 1:500

Площа земельної ділянки згідно з документами на землекористування - землі міста Одеси



ЕКСПЛІКАЦІЯ:

- 1) Місце розташування ТС
- 2) Червоні лінії
- 3) Лінії регулювання забудови
- 4) Місця підключення до інженерних мереж

УМОВНІ ПОЗНАЧЕННЯ:

- | | |
|---|--|
|  | Межа благоустрою ділянки розміщення ТС |
|  | Тимчасова споруда |
|  | Існуючі будівлі та споруди |
|  | Існуючі дороги |

Підключення до інженерних мереж

ФОРМ (2010350000000013361)

Архітектор

Кваліфікаційний сертифікат серія АА №002647

Дата складання: «09» 07 2021 року




Громова О.Р.

Громова О.Р.

СИТУАЦІЙНИЙ ПЛАН М 1:2000

Місце розміщення об'єкту

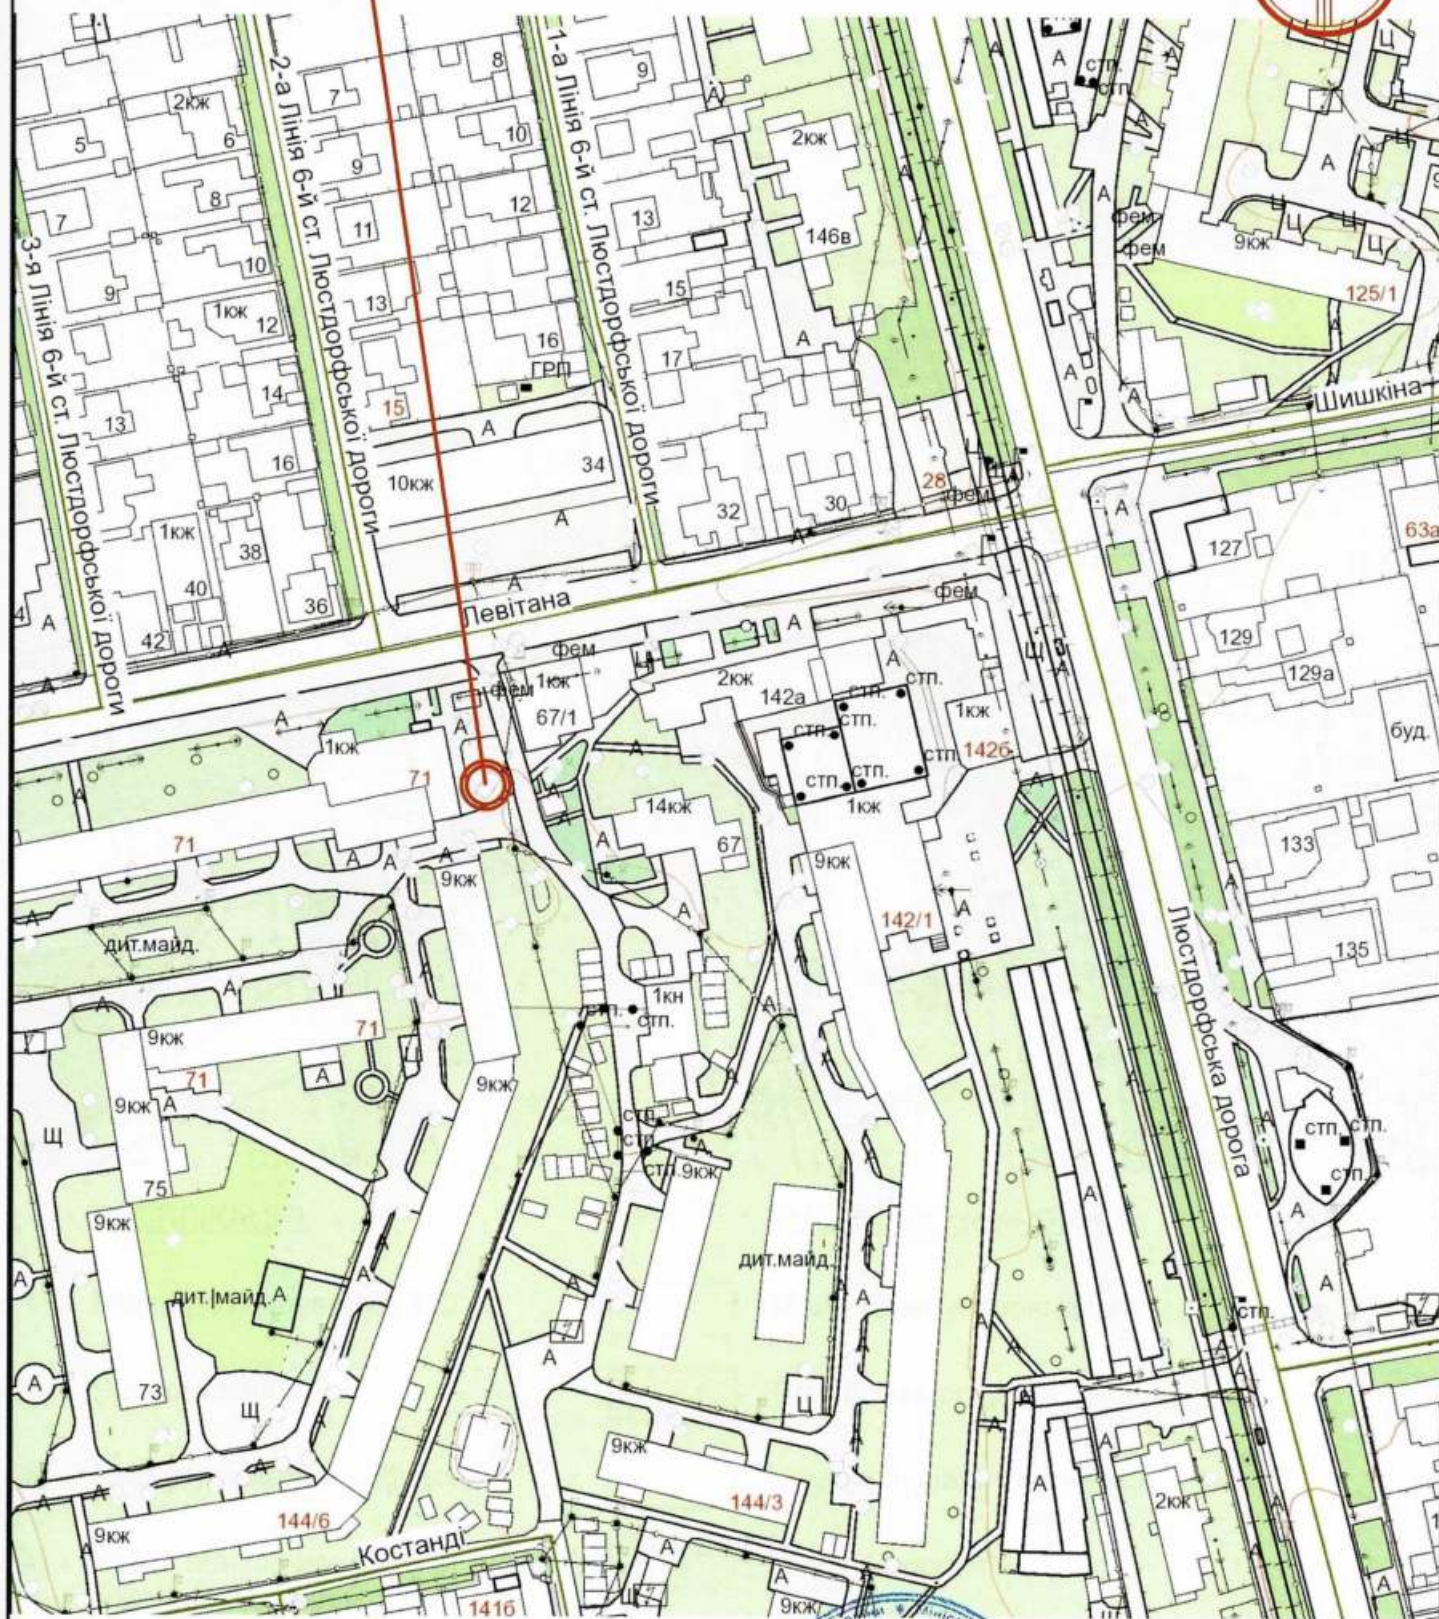

ФОП (201035000000013361)

Архітектор

Кваліфікаційний сертифікат серія АА №002647



Громова О.Р.

Громова О.Р.