

СТИСЛА ПОЯСНЮВАЛЬНА ЗАПИСКА

1. Стаціонарна тимчасова споруда для здійснення підприємницької діяльності має торговельне приміщення для тимчасового перебування людей.

За умовну позначку ± 0.000 прийнятий рівень чистої підлоги ТС.

Ступень вогнестійкості - IIIа.

Стаціонарна тимчасова споруда являє собою павільйон Г-подібної форми у плані з максимальними габаритними розмірами - 4,7 x 6,16 м. Загальна площа ТС - 23,7 м².

Внутрішня висота павільйону від рівня чистої підлоги складає - 3,3 м.

Загальна висота складає - 3,7 м.

Ґрунт заснування, до встановлення ТС, ретельно утрамбовується щебнем та укладається бетонна тротуарна плитка.

Стіни споруди запроектовані товщиною 100 мм із утеплювачем з мінеральної вати та обшивкою з обох сторін.

Обшивка стін по каркасу: зовнішня - композитні матеріали типу "Алюкобонд"; внутрішня (стіни та стеля) - гіпсокартонні листи.

Підлога - дерев'яні дошки 40 мм по металевому каркасу з утеплювачем з мінераловатних плит та покриттям з негорючого матеріалу.

Покрівля - по металевим прогонам і решетуванню з покриттям оцинкованою покрівельною сталлю, з утеплювачем з мінераловатних плит, гідро- і пароізоляцією.

Зовнішня обробка:

поверхні стін - композитні матеріали типу "Алюкобонд";

вікна та двері - металопластикові з вакуумними склопакетами;

покрівля - оцинкована покрівельна сталь.

2. Стаціонарна тимчасова споруда підключається до мереж електропостачання згідно з діючими нормами та ТУ. Точка підключення - згідно з ТУ.

Опалення - електричне з встановленням навісних електро-конвекторів з регулюванням температури.

Освітлення приміщення виконується світильниками з люмінесцентними лампами.

Розподільні мережі виконані проводами з мідними жилами, що прокладені у трубах та приховані в обшивці стін.

Захист мереж від дії струмів коротких замикань та перевантажень здійснюється автоматичними вимикачами щитка.

3. Благоустрій прилеглої території виконується згідно з планом благоустрою.

Освітлення території передбачене світильниками, що розміщуються на головному фасаді під покрівлею ТС.

Директор ТОВ "Вікторіанський стиль"

Архітектор

Кваліфікаційний сертифікат серія АА № 002874



О.М. Кондратюк

К.М. Багріна

ЕСКІЗИ ФАСАДІВ ТС
Головний фасад ТС М 1:50



Бічний фасад ТС М 1:50



Директор ТОВ "Вікторіанський стиль"

Архітектор


Кваліфікаційний сертифікат серія АА № 002874



О.М. Кондратюк

К.М. Багріна

ПЛАН ТС М 1:50

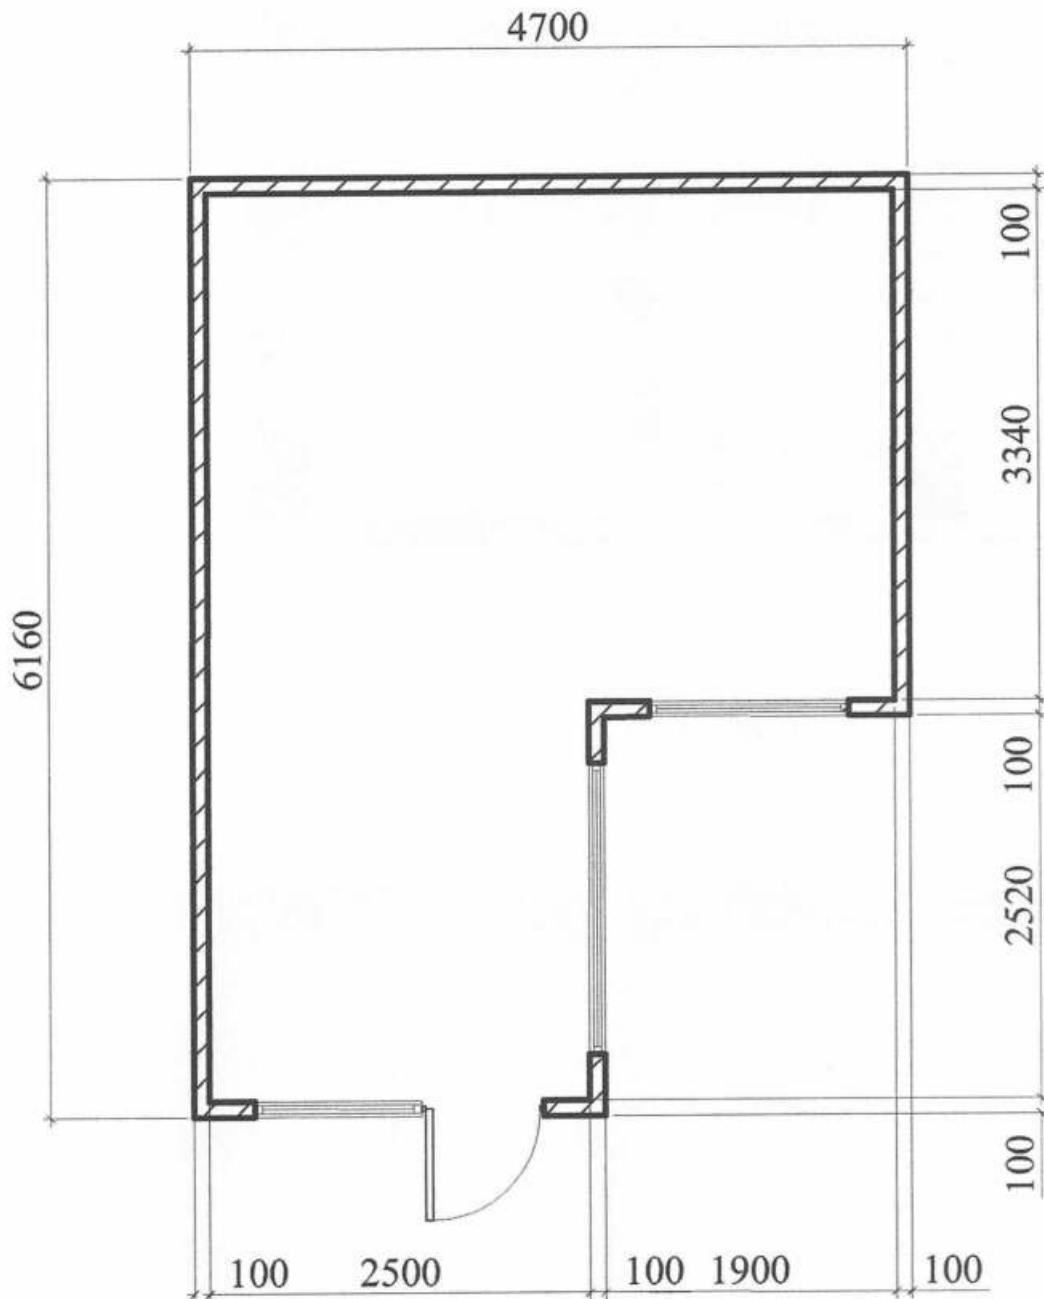

Директор ТОВ "Вікторіанський стиль"

Архітектор


Кваліфікаційний сертифікат серія АА № 002874



О.М. Кондратюк


К.М. Багріна

Площа земельної ділянки згідно з документами
на землекористування - землі міста

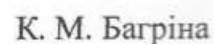

Ситуаційний план М 1:2000

Місце розміщення об'єкту

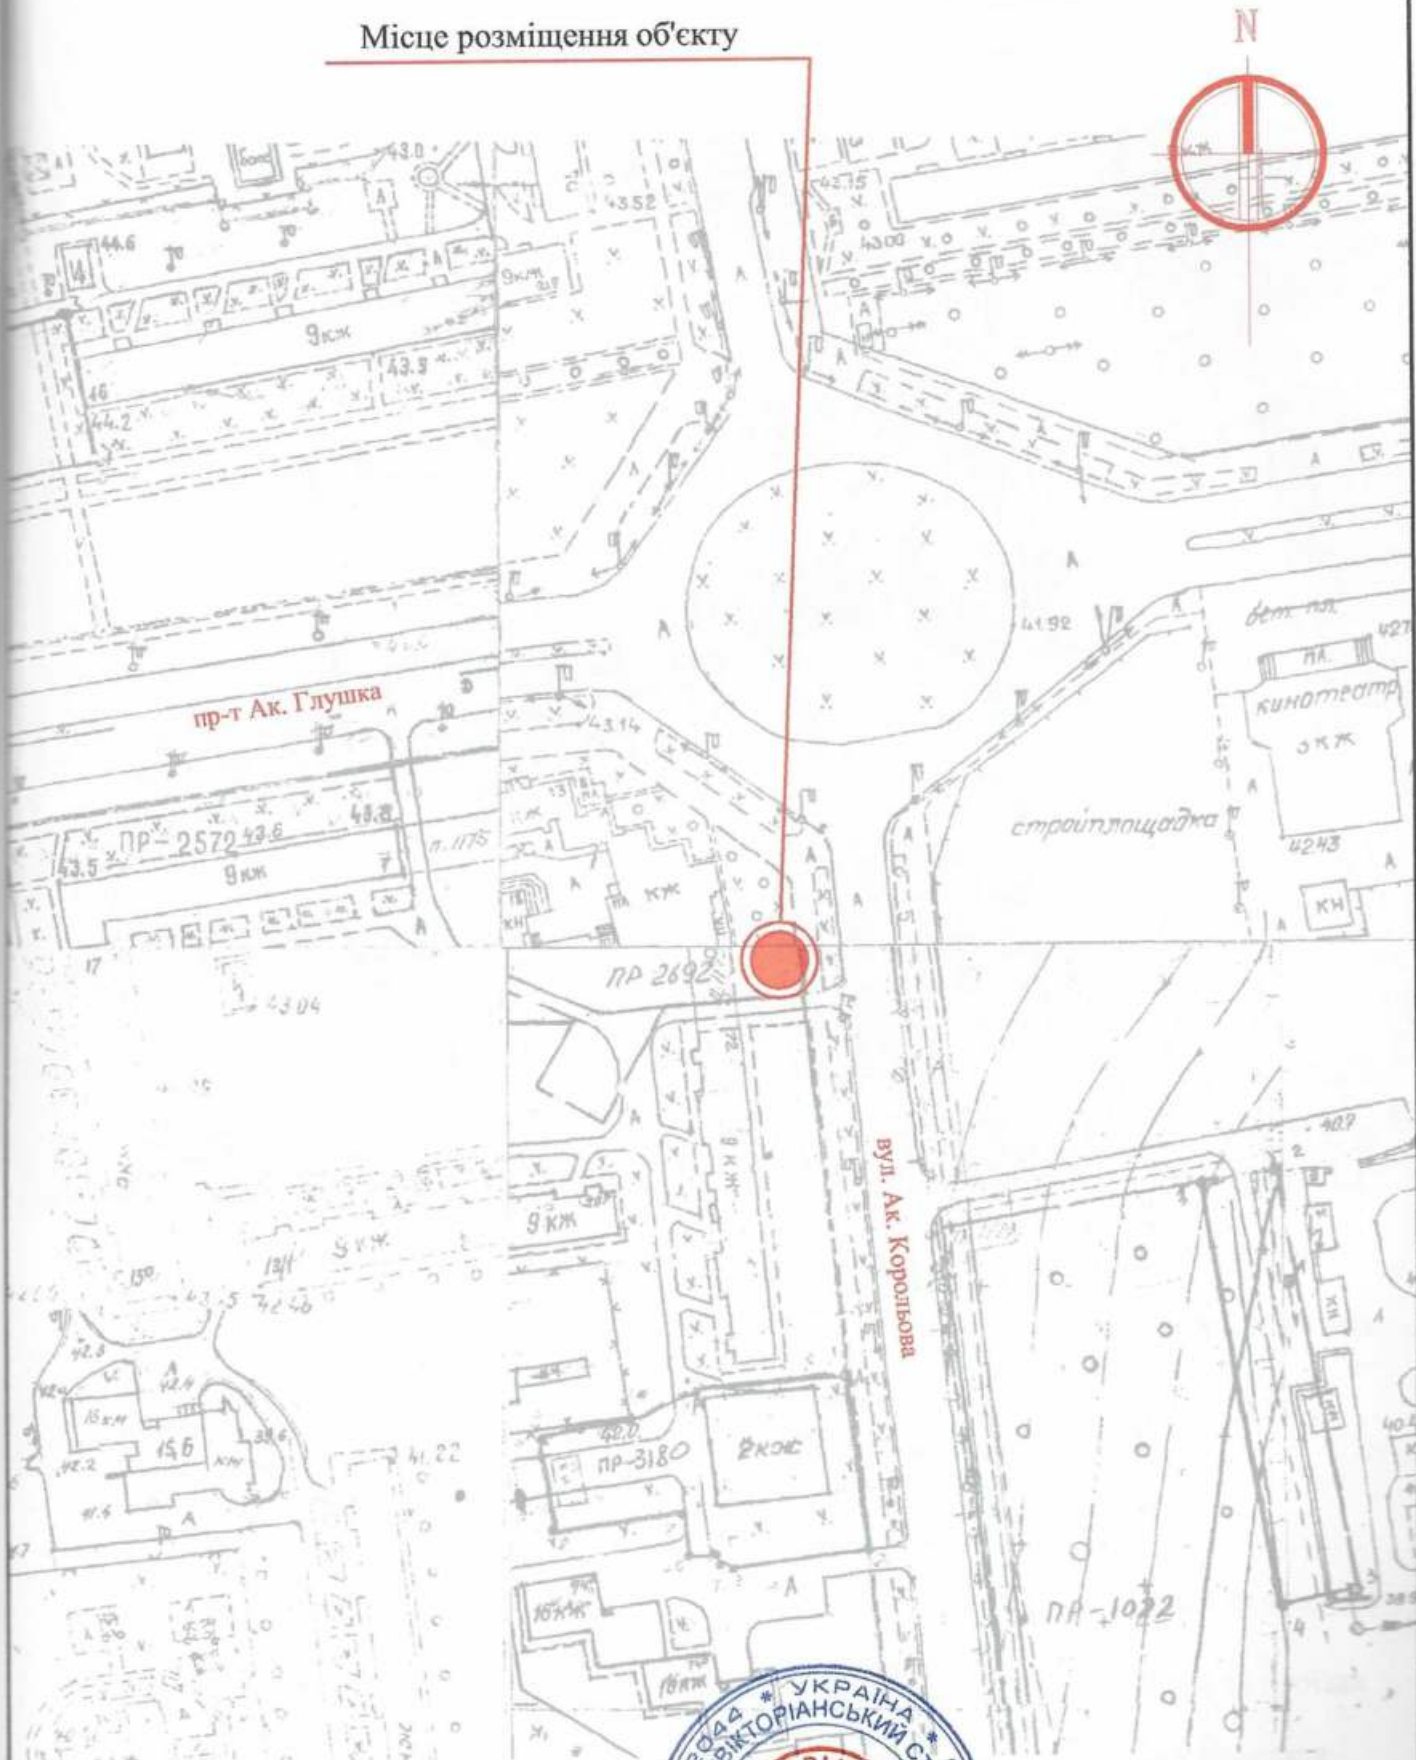

Директор ТОВ "Вікторіанський стиль"

О.М. Кондратюк

Архітектор

К. М. Багіна

Кваліфікаційний сертифікат серія АА № 002874

