

ПОЯСНЮВАЛЬНА ЗАПИСКА

1. Тимчасова споруда (ТС) для здійснення підприємницької діяльності має закриті приміщення для тимчасового перебування людей.

За умовну позначку 0.000 прийнятий рівень чистої підлоги ТС.

Ступінь вогнестійкості - IIIа.

Габаритні розміри павільйона в плані - 6.00м x 4.35м.

Площа забудови складає - 26.10м².

У павільйоні розташоване приміщення загальною площею - 24.07м².

Внутрішня висота павільйону від рівня чистої підлоги складає - 2.7м.

Загальна висота павільйону - 3.35м.

Грунт заснування, до встановлення павільйону, ретельно утрамбован щебнем та покладена тротуарна плитка. ТС встановлена без улаштування фундаментів.

Стіни споруди запроектовані по типу «Сендвич», товщиною 100мм із утеплювачем з мінеральної вати й обшивкою.

Обшивка стін по каркасу: зовнішня - кольорові алюмінієві сендвич панелі, типа «Алюкобонд»; внутрішня (стіни й стеля) - вагонка.

Підлога з покриттям дошки 40мм і утеплювачем (керамзитовий гравій - 200мм) та покриття з негорючого матеріала.

Покрівля - по металевим прогонам і решетуванню з покриттям із профільованого сталевго листа, з утеплювачем з мінераловатних плит, гидро- і пароізоляцією.

Зовнішня обробка.

поверхні стін - кольорові алюмінієві сендвич панелі, типа «Алюкобонд» ;

вікна - металопластикові;

двері - металопластикові;

покрівля - кольоровий металевий профнастіл; алюмінієві сендвич панелі;

цоколь - кольорові сендвич-панелі.

2. Стационарна тимчасова споруда підключена до мереж електропостачання згідно з діючими нормами та ТУ. Точка підключення - близька опора, що розташована поряд з територією ділянки.

Опалювання - електричне з встановленням навісних електро-конвекторів з регулюванням температури.

Як розподільний щиток у павільйоні встановлено щиток серії NRL-1F6ZS з лічильником активної енергії й автоматичних вимикачів на лініях, що відходять.

Освітлення приміщення виконане стельовими світильниками з люмінесцентними лампами.

Розподільні мережі павільйону, виконані проводами з мідними жилами, що прокладені у трубах та приховані в обшивці стін. Мережі обрані по тривалодопустимим струмам навантаження.

Захист мереж від дії струмів коротких замикань і перевантаження здійснюється автоматичними вимикачами щитка.

Назва об'єкту, адреса розміщення Стационарна тимчасова споруда, площа Незалежності, пр.Ак.Глушко, 13	Посада виконавця	ПІБ	Підпис
	ГАП архітектор	Ігнатова Л.А. Чабан Л.В.	
 М.П.	Кваліфікаційний сертифікат серія АА № 000199		
	Дата складання "19" 02. 2015 року		

ЕСКІЗИ ФАСАДІВ ТС М 1:50

Головний фасад



Боковий фасад




Назва об'єкту, адреса розміщення Станіонарна тимчасова споруда, площа Незалежності, пр.Ак.Глушко, 13	Посада виконавця	ПІБ	Підпис
	ГАП архітектор	Ігнатова Л.А. Чабан Л.В.	
М.П. 	Кваліфікаційний сертифікат серія АА № 000199		
	Дата складання "19" 02. 2015 року		

СХЕМА РОЗМІЩЕННЯ ТС М 1:500

Площа земельної ділянки згідно з документами на землекористування

Город земель фонд земля м.Одеси

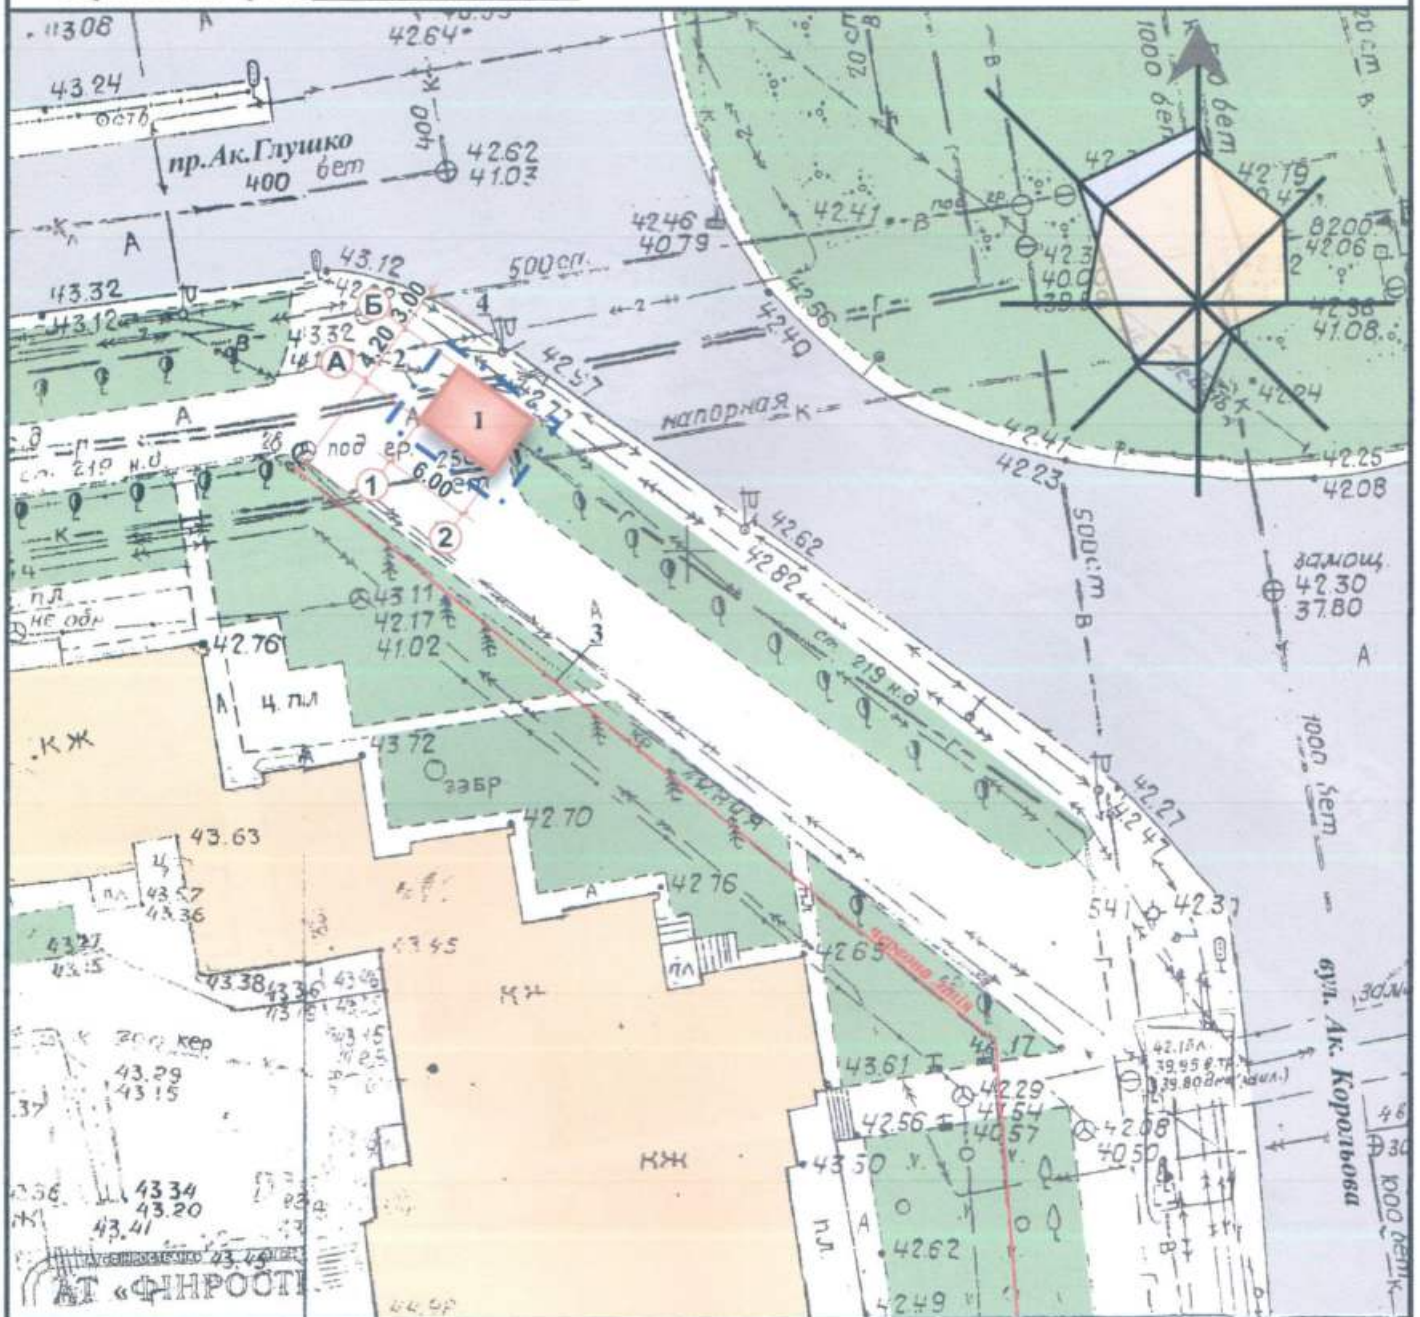

Експлікація:


- 1) місце розташування ТС;
- 2) лінії регулювання забудови;
- 3) червоні лінії;
- 4) місця підключення до інженерних мереж.

Умовні позначення:

- об'єкт проектування (ТС)
- існуючі дороги.
- існуючі будівлі та споруди.
- озеленення.
- територія, що підлягає благоустрою

Назва об'єкту, адреса розміщення Станіонарна тимчасова споруда, площа Незалежності, пр.Ак.Глушко, 13	Посада виконавця	ПІБ	Підпис
	ГАП архітектор	Ігнатова Л.А. Чабан Л.В.	
Кваліфікаційний сертифікат серія АА № 000199			
Дата складання "19" 02. 2015 року			

СИТУАЦІЙНИЙ ПЛАН, М 1:2000

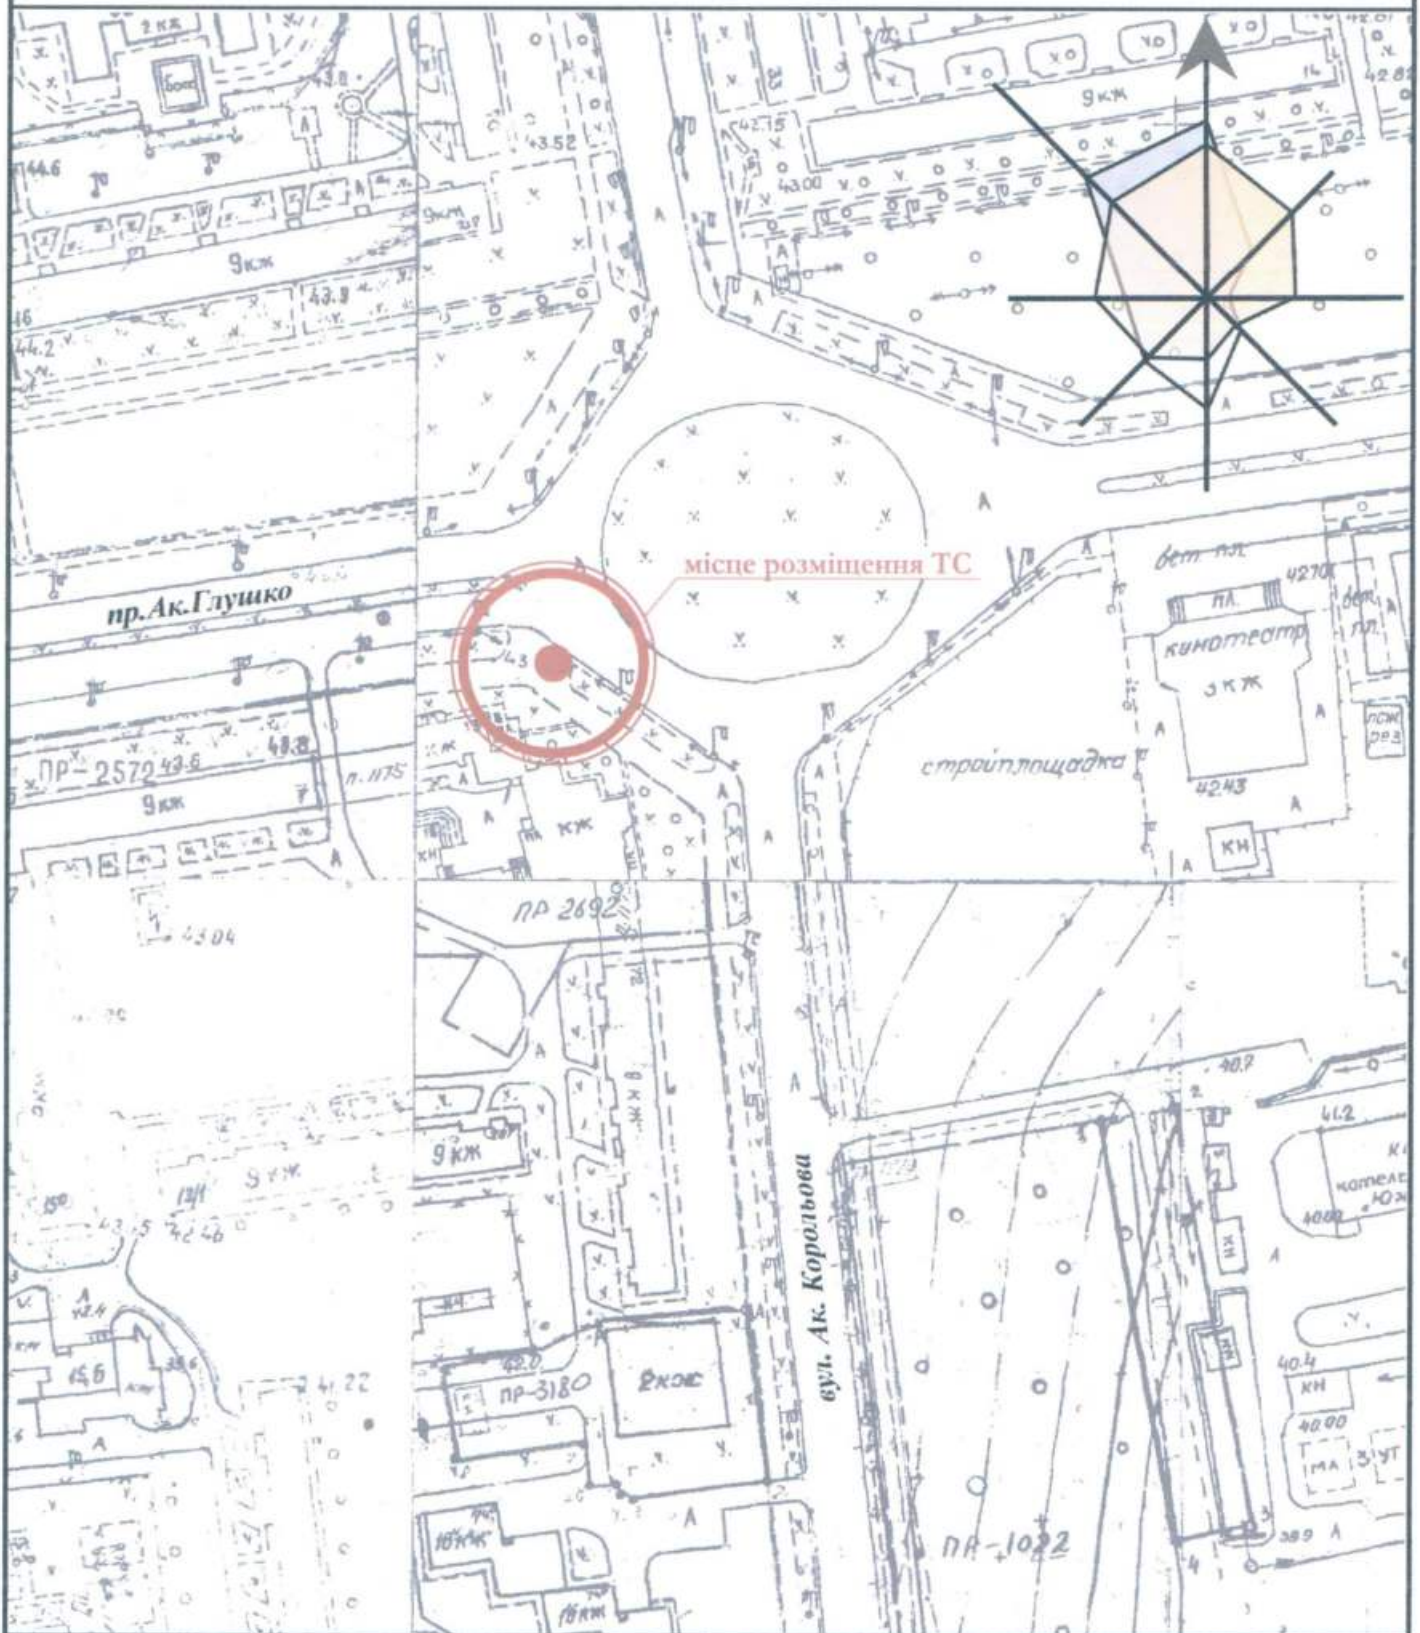

Назва об'єкту, адреса розміщення Станційна тимчасова споруда, площа Незалежності, пр. Ак. Глушко, 13	Посада виконавця ГАП архітектор	ПІБ Ігнатова Л.А. Чабан Л.В.	Підпис 
М.П. 	Кваліфікаційний сертифікат серія АА № 000199 Дата складання "19" 02. 2015 року		