

ПОЯСНЮВАЛЬНА ЗАПИСКА

1. Тимчасова споруда (ТС) для здійснення підприємницької діяльності має закриті приміщення для тимчасового перебування людей.

За умовну позначку 0.000 прийнятий рівень чистої підлоги ТС.

Ступінь вогнестійкості - IIIа.

Габаритні розміри павільйона в плані - 4.00м x 2.00м.

Площа забудови складає - 8.00м².

У павільйоні розташоване приміщення загальною площею - 6.84м².

Внутрішня висота павільйону від рівня чистої підлоги складає - 2.7м.

Загальна висота павільйону - 3.35м.

Ґрунт заснування, до встановлення павільйону, ретельно утрамбован щебнем та покладена тротуарна плитка. ТС встановлена без улаштування фундаментів.

Стіни споруди запроектовані по типу «Сендвич», товщиною 100мм із утеплювачем з мінеральної вати й обшивкою.

Обшивка стін по каркасу: зовнішня - кольорові алюмінієві сендвіч панелі, типа «Алюкобонд»; внутрішня (стіни й стеля) - вагонка.

Підлога з покриттям дошки 40мм і утеплювачем (керамзитовий ґравій - 200мм) та покриття з негорючого матеріала.

Покрівля - по металевим прогонам і решетуванню з покриттям із профільованого сталевих листа, з утеплювачем з мінераловатних плит, гідро- і пароізоляцією.

Зовнішня обробка.

поверхні стін - кольорові алюмінієві сендвіч панелі, типа «Алюкобонд» ;

вікна - металопластикові;

двері - металопластикові;

покрівля - кольоровий металевий профнастил; алюмінієві сендвіч панелі;

цоколь - кольорові сендвіч-панелі.

2. Стационарна тимчасова споруда підключена до мереж електропостачання згідно з діючими нормами та ТУ. Точка підключення - близька опора, що розташована поряд з територією ділянки.


Опалювання - електричне з встановленням навісних електро-конвекторів з регулюванням температури.

Як розподільний щиток у павільйоні встановлено щиток серії NRL-1F6ZS з лічильником активної енергії й автоматичних вимикачів на лініях, що відходять.


Освітлення приміщення виконане стельовими світильниками з люмінесцентними лампами.

Розподільні мережі павільйону, виконані проводами з мідними жилами, що прокладені у трубах та приховані в обшивці стін. Мережі обрані по тривалодопустимим струмам навантаження.


Захист мереж від дії струмів коротких замикань і перевантаження здійснюється автоматичними вимикачами щитка.

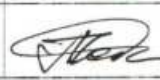 Назва об'єкту, адреса розміщення Стационарна тимчасова споруда, площа Незалежності, пр.Ак.Глушко, 13	Посада виконавця	ПІБ	Підпис
	ГАП архітектор	Ігнатова Л.А. Чабан Л.В.	
Кваліфікаційний сертифікат серія АА № 000199			
Дата складання "19" 02. 2015 року			

Головний фасад

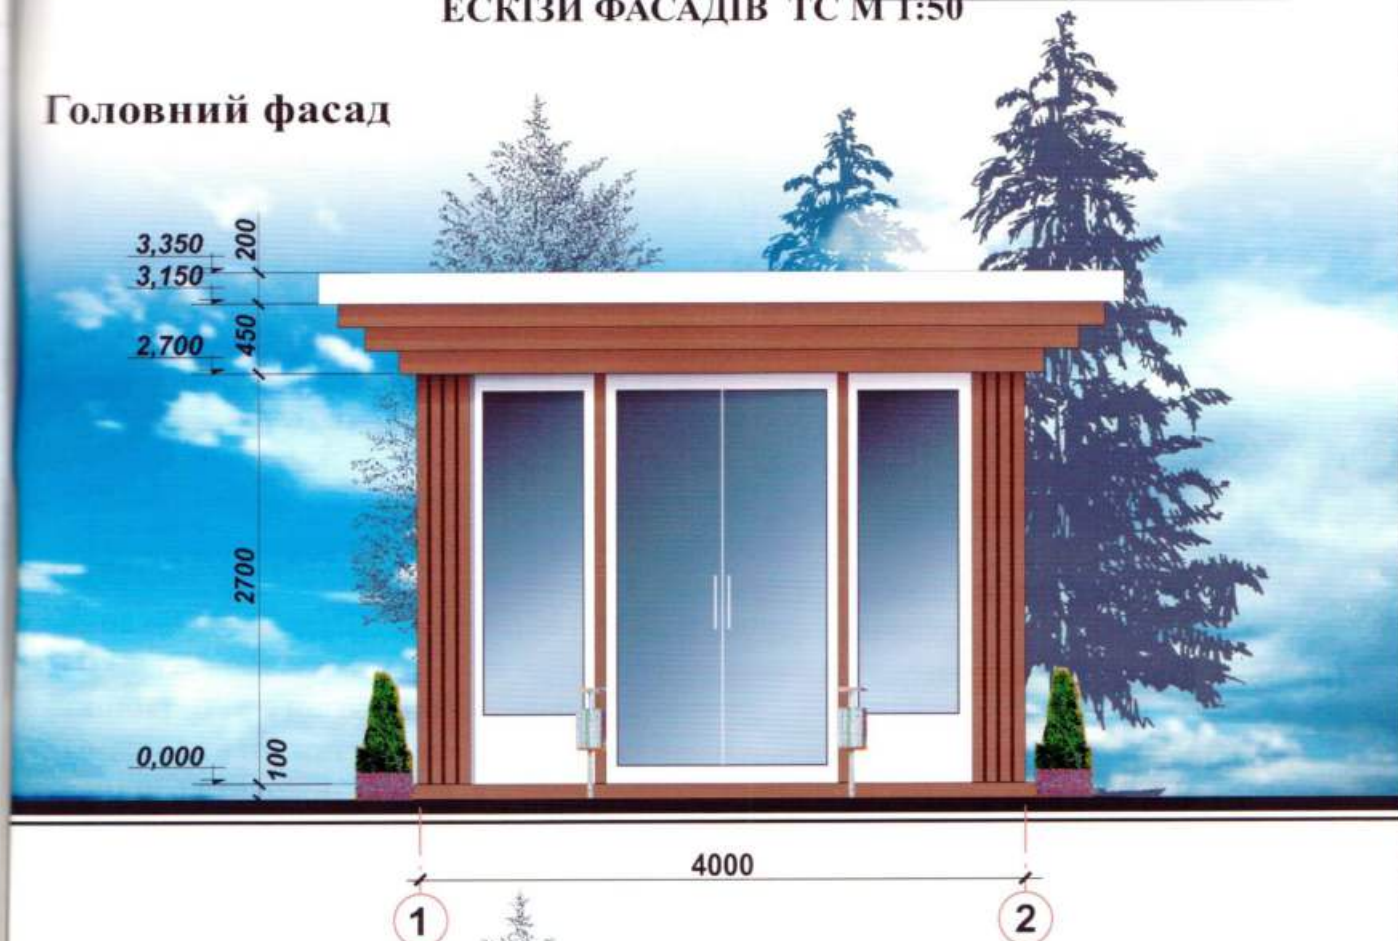

Боковий фасад

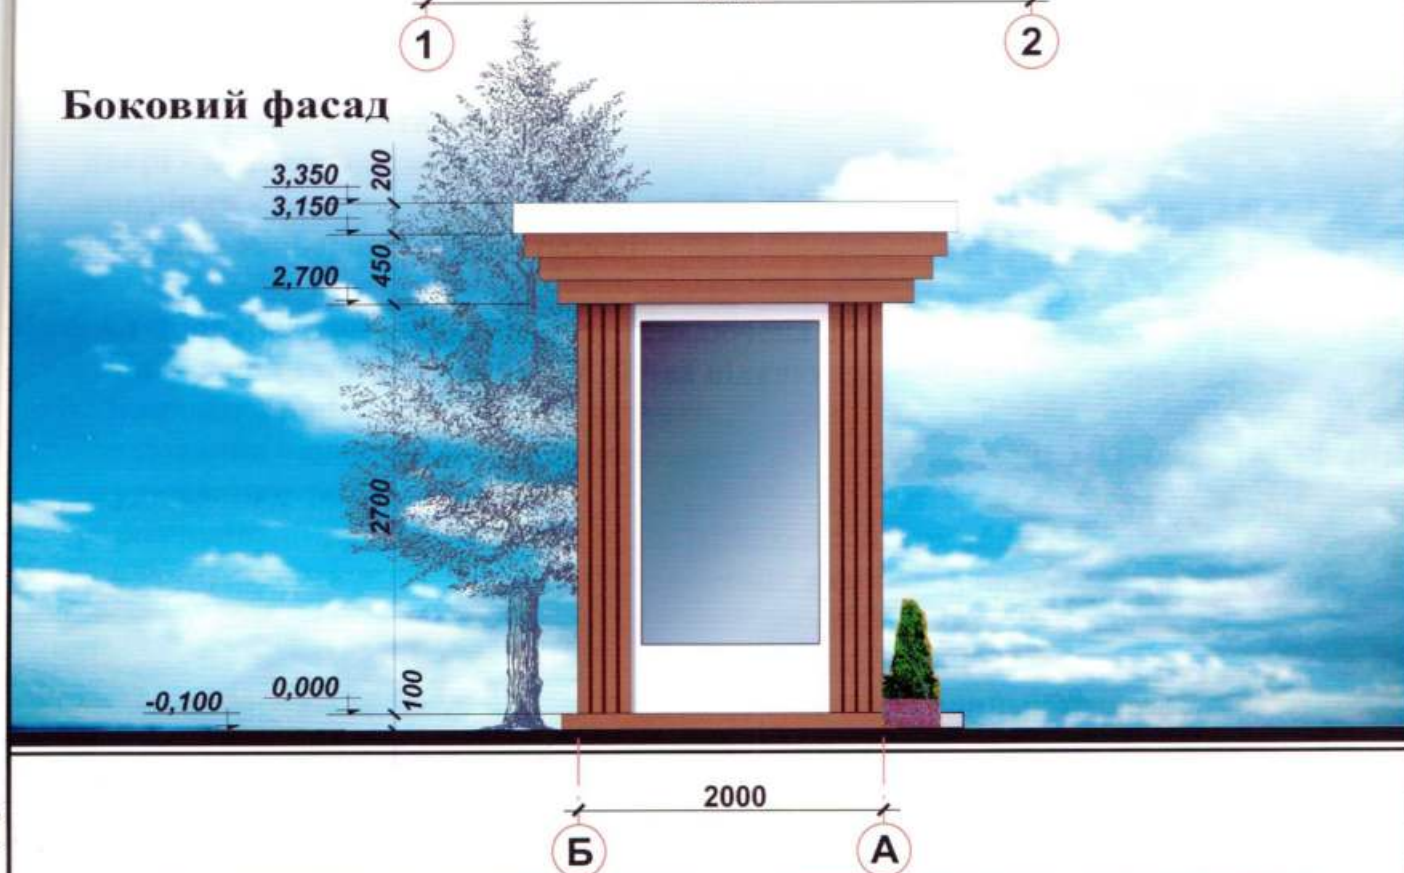


Назва об'єкту, адреса розміщення Станіонарна тимчасова споруда, площа Незалежності, пр.Ак.Глушко, 13	Посада виконавця	ПІБ	Підпис
	ГАП архітектор	Ігнатова Л.А. Чабан Л.В.	
М.П. 	Кваліфікаційний сертифікат серія АА № 000199		
	Дата складання "19" 02. 2015 року		

СХЕМА РОЗМІЩЕННЯ ТС М 1:500

Площа земельної ділянки згідно з документами на землекористування

Город земель фонд земля м.Одеси

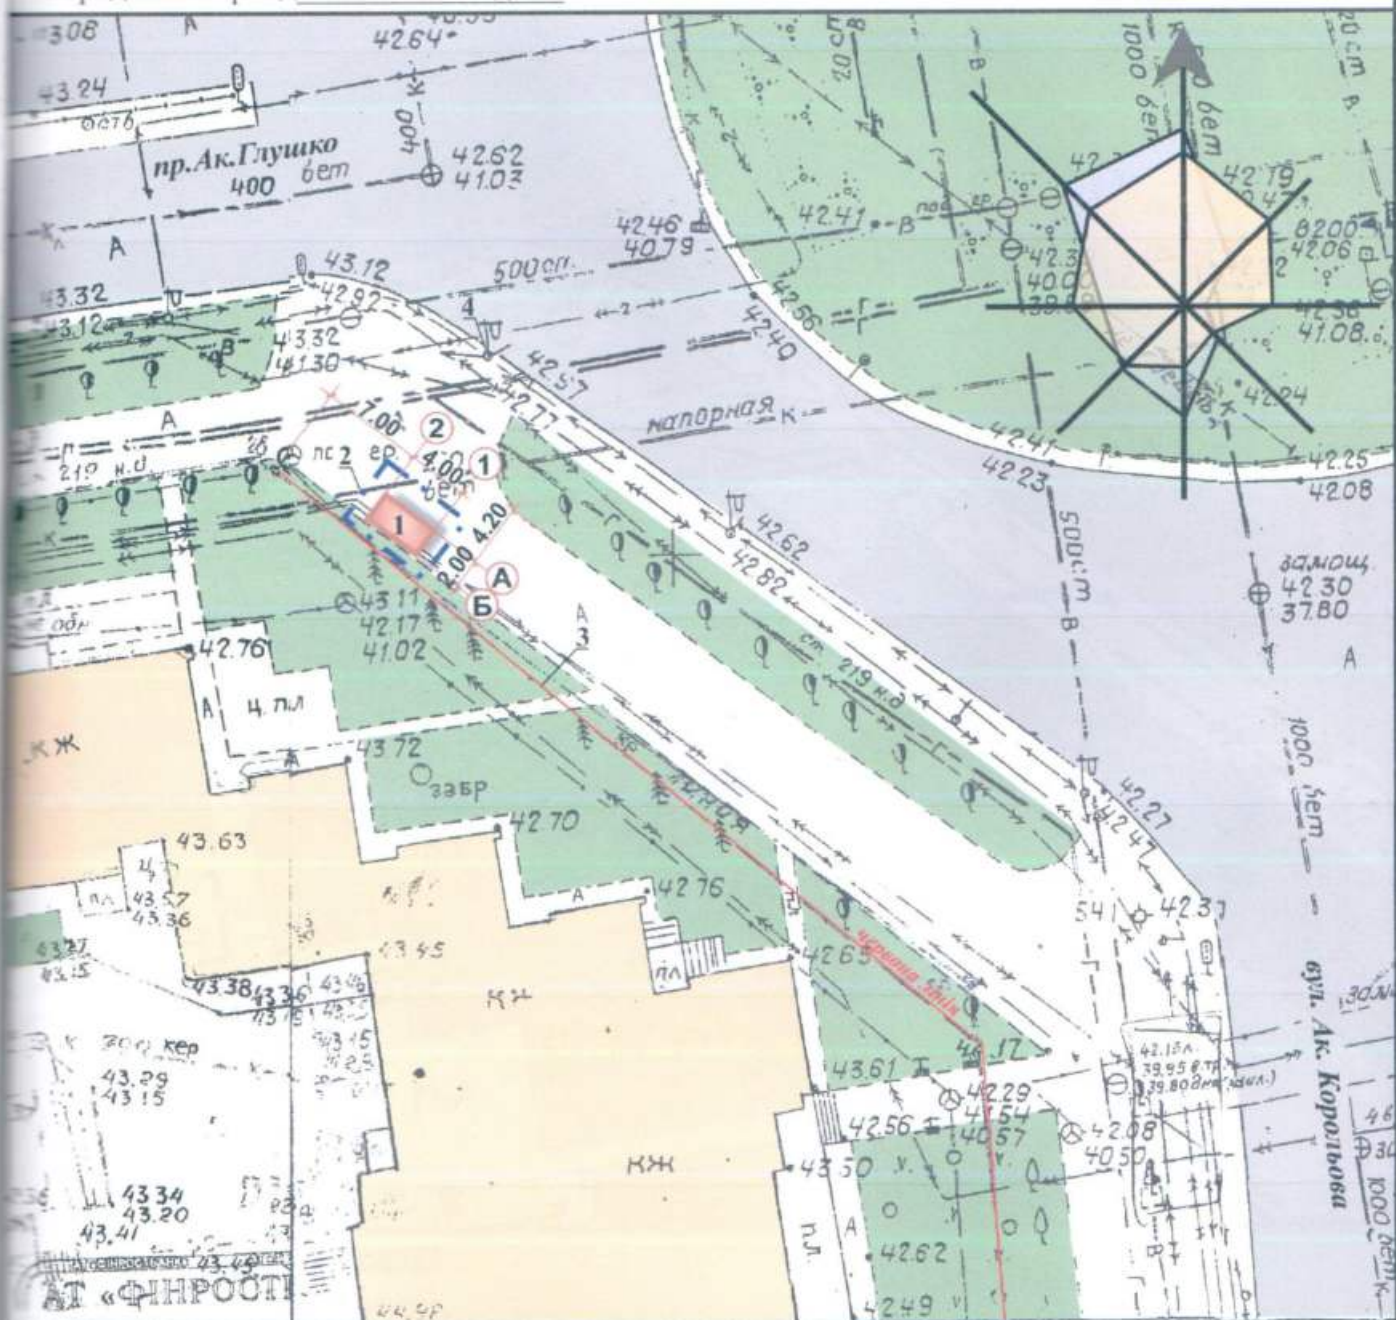

Експлікація:

- 1) місце розташування ТС;
- 2) лінії регулювання забудови;
- 3) червоні лінії;
- 4) місця підключення до інженерних мереж.


Умовні позначення:

- об'єкт проектування (ТС)
- існуючі дороги.
- існуючі будівлі та споруди.
- озеленення.
- територія, що підлягає благоустрою

Назва об'єкту, адреса розміщення Станіонарна тимчасова споруда, площа Незалежності, пр.Ак.Глушко, 13	Посада виконавця	ПІБ	Підпис
	ГАП архітектор	Ігнатова Л.А. Чабан Л.В.	
Кваліфікаційний сертифікат серія АА № 000199			
Дата складання "19" 02. 2015 року			



СИТУАЦІЙНИЙ ПЛАН, М 1:2000

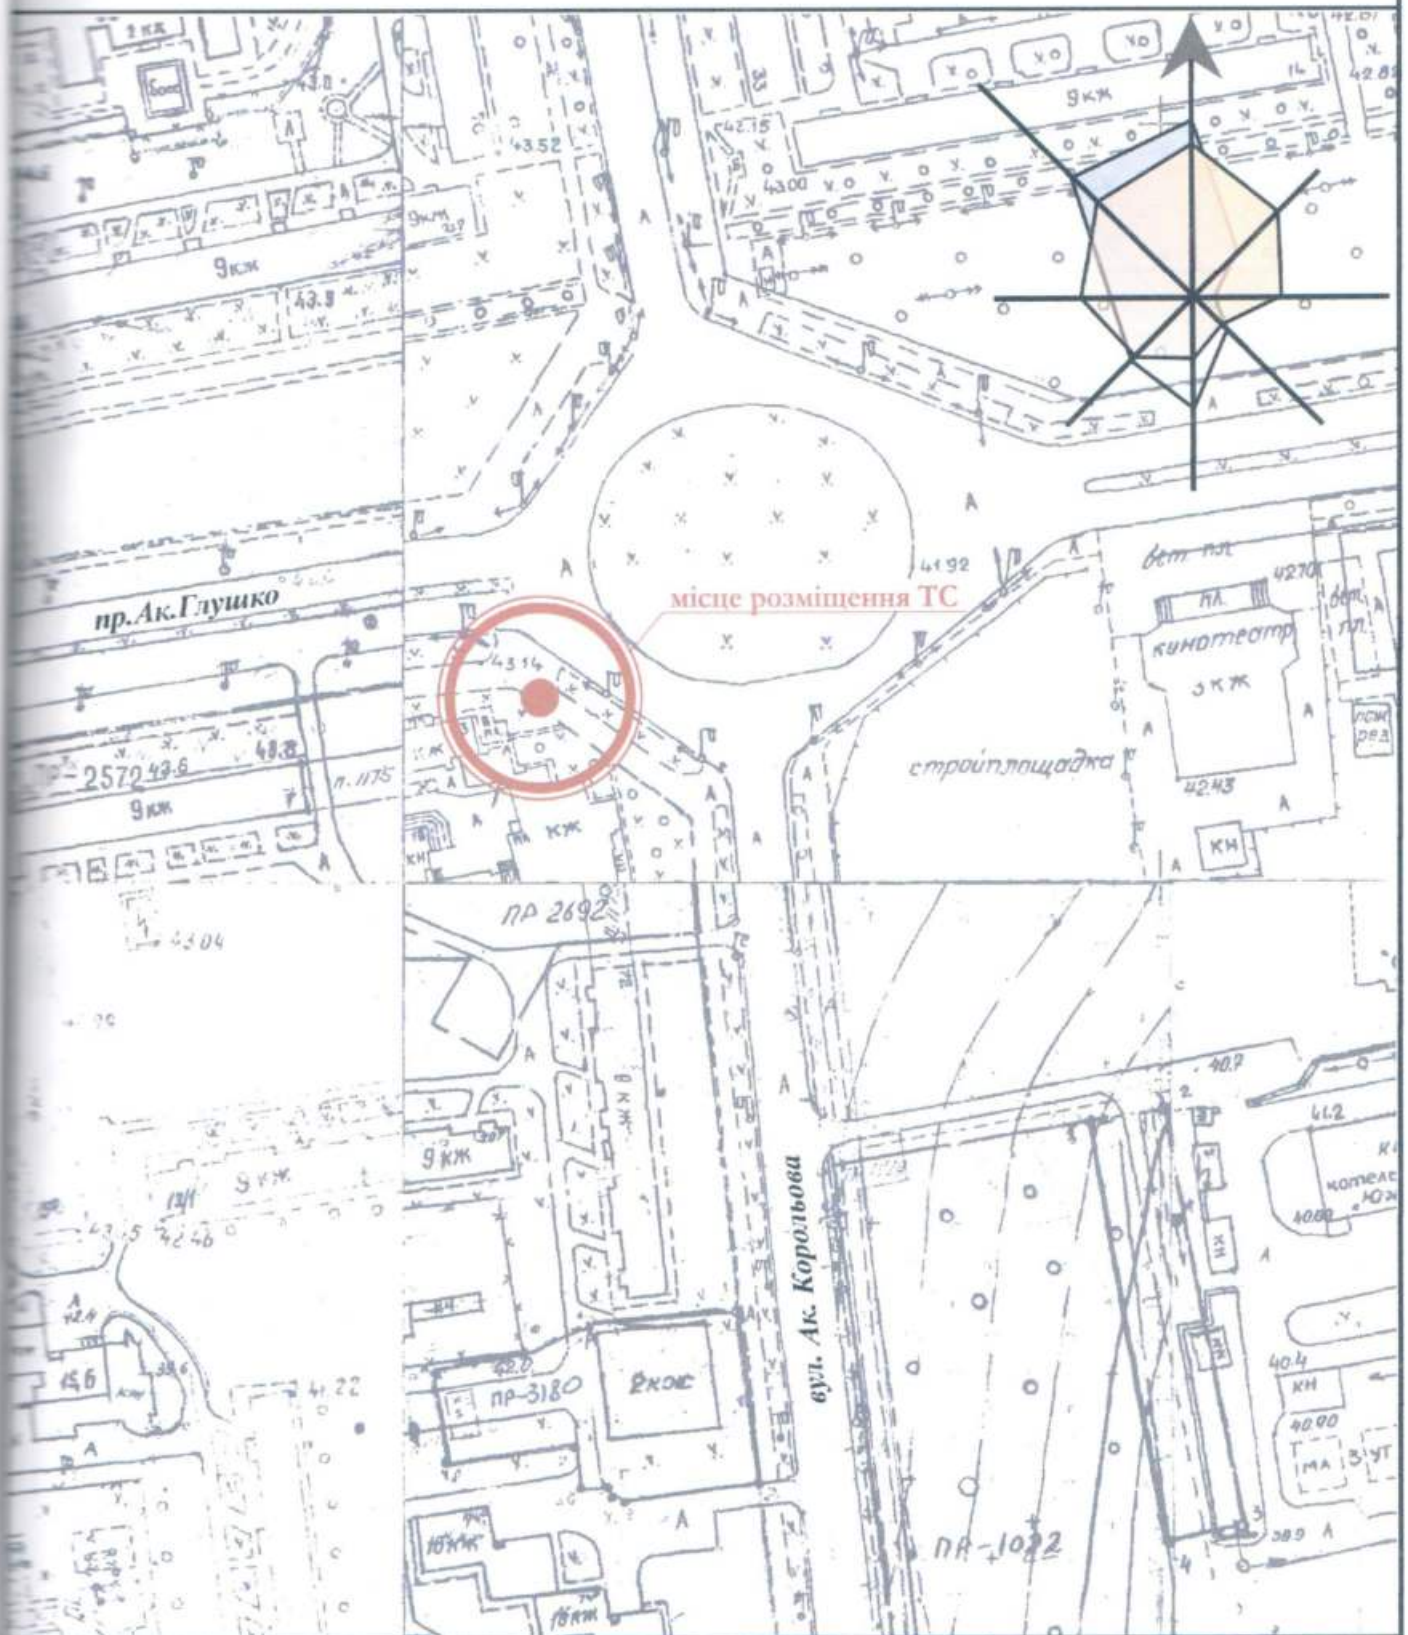

Назва об'єкту, адреса розміщення Станіонарна тимчасова споруда, площа Незалежності, пр.Ак.Глушко, 13 М.П.	Посада виконавця	ПІБ	Підпис
	ГАП архітектор	Ігнатова Л.А. Чабан Л.В.	
Кваліфікаційний сертифікат серія АА № 000199 Дата складання "19" 02. 2015 року			