

ПОЯСНЮВАЛЬНА ЗАПИСКА

1. Тимчасова споруда (ТС) для здійснення підприємницької діяльності має закриті приміщення для тимчасового перебування людей.

За умовну позначку 0.000 прийнятий рівень чистої підлоги ТС.

Ступінь вогнестійкості - IIIа.

Габаритні розміри павільйону в плані - 3.00м x 6.00м.

Площа забудови ТС - 18.00м².

У павільйоні розташовані приміщення, загальною площею - 15.68м².

Внутрішня висота ТС від рівня чистої підлоги складає - 2.40м.

Загальна висота ТС - 3.17м.

Грунт заснування, до встановлення ТС, ретельно утрамбован щебнем та покладена тротуарна плитка.

ТС встановлена без улаштування фундаментів.

Стіни споруди запроектовані по типу «Сендвич», товщиною 100мм із утеплювачем з мінеральної вати та обшивкою з обох сторін.

Обшивка стін по каркасу: зовнішня - кольорові сендвич панелі, внутрішня (стіни й стеля) - пластикова вагонка.

Підлога - дерев'яні дошки 40мм по металевому каркасу з утеплювачем із мінераловатних плит та покриттям з негорючого матеріалу.

Покрівля - по металевим прогонам і решетуванню з покриттям із профільованого сталевго листа, з утеплювачем із мінераловатних плит, гидро- і пароізоляцією.

Зовнішня обробка.

поверхні стін - кольорові сендвич панелі;

вікна - металопластикові з вакуумними склопакетами;

двері - металопластикові з вакуумними склопакетами;

покрівля - профільований сталевий лист;

козирок - полікарбонат.

2. Стационарна тимчасова споруда не підключена до мереж електропостачання.

3. Протипожежні заходи виконані відповідно до вимог Будівельних Норм України «Пожежна безпека об'єктів будівництва» ДБН В.1.1-7-2016 і є обов'язковим для виконання:

- мінімальна ширина дверних прорізів на шляхах евакуації становить не менш 0.8м;

- відкривання дверей запроектоване у бік виходу з павільйону;

- передбачено негорючий утеплювач стін і покрівлі;

- оснащення ТС первинними засобами пожежогасіння;

- внутрішня обробка передбачена із застосуванням негорючих оздоблювальних матеріалів, з підтвердженням сертифікатом;

- всі дерев'яні елементи, просочити антипиренами, металеві елементи погрунтувати потім покрити вогнезахистними фарбами з підтвердженням сертифікатом до досягнення межі вогнестійкості конструкцій 1.0 години.

4. При проведенні всіх видів будівельних і спеціальних робіт виконувати вимоги ДБН А.3.2-2-2009 «Охорона праці і промислова безпека в будівництві».

5. Благоустрій прилеглої території виконується згідно з планом благоустрою.

Поряд со спорудою встановлюються дві урни.

ГАП

Кваліфікаційний сертифікат серія АА №000199

Архітектор

Дата складання "28" 03. 2019 року




Ігнатова Л.А.


Чабан Л.В.

ЕСКІЗИ ФАСАДІВ ТС М 1:50

Головний фасад

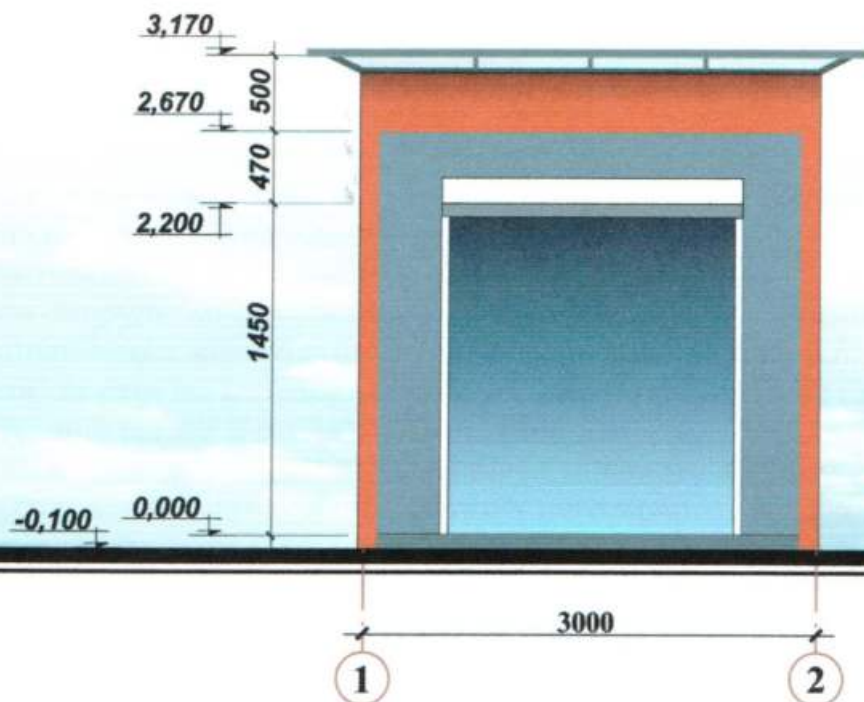

Бічний фасад

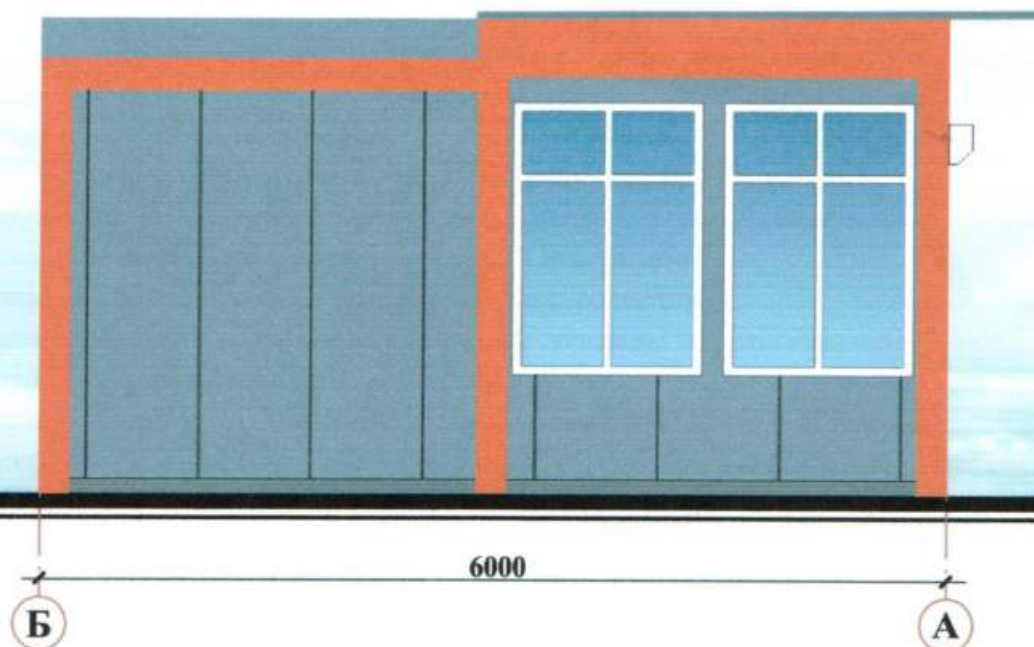

ГАП
Кваліфікаційний сертифікат серія АА №000199

Архітектор


Дата складання "28" 03. 2019 року

Ігнатова Л.А.

Чабан Л.В.



ПЛАН ТС, М 1:50

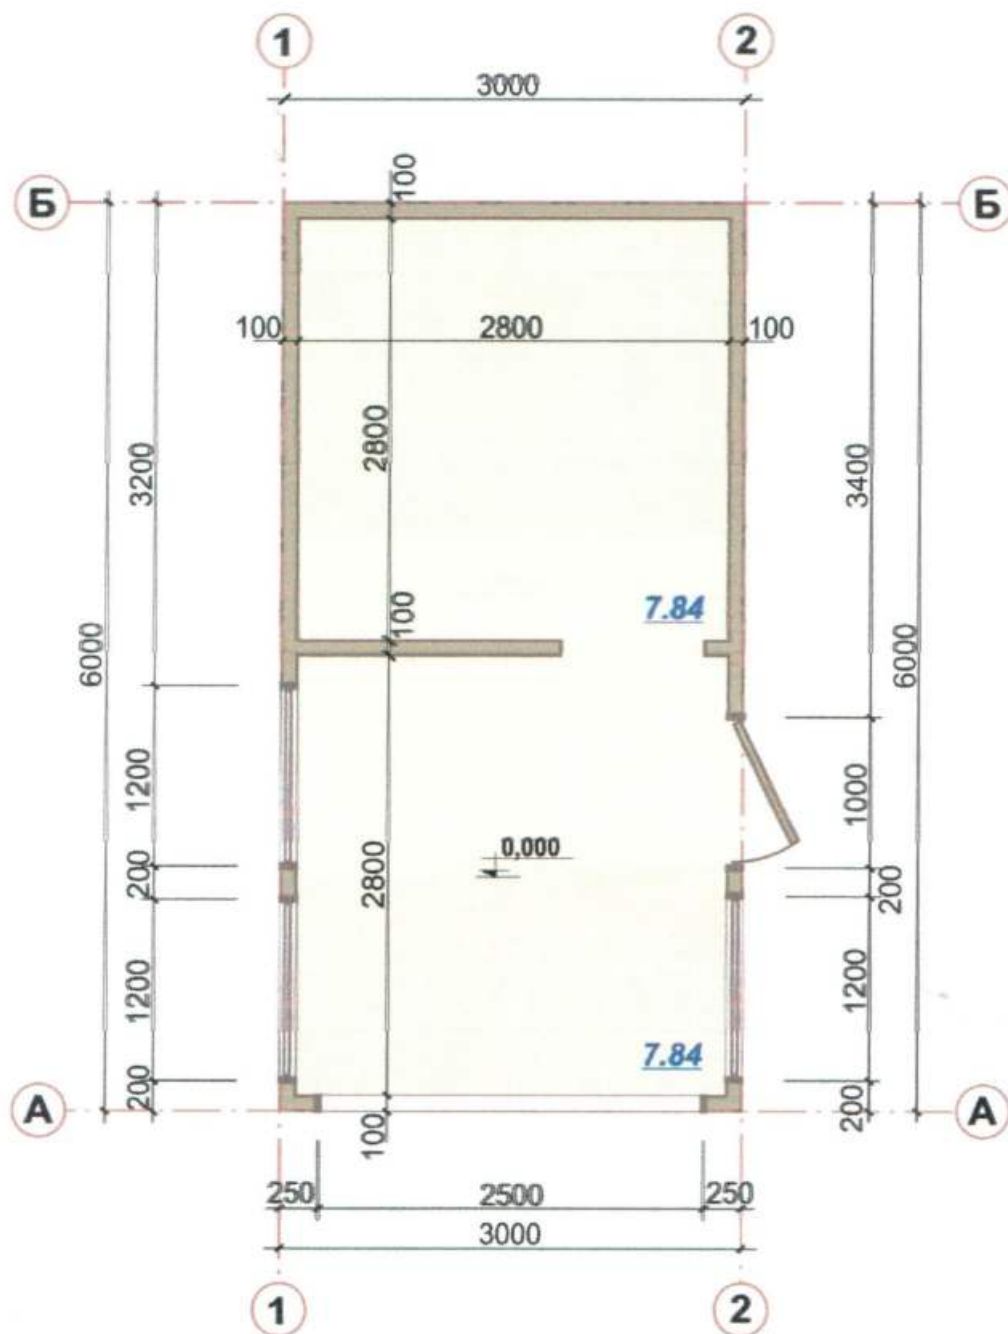

ГАП
Кваліфікаційний сертифікат серія АА №000199

Архітектор

Дата складання "28" 03. 2019 року



Ігнатова Л.А.

Чабан Л.В.

Площа земельної ділянки згідно з документами на землекористування
Город земель фонд земля м.Одеси



- Експлікація:**

- 1) місце розташування ТС;
- 2) лінії регулювання забудови;
- 3) червоні лінії;
- 4) місця підключення до інженерних мереж.


Архітектор

Дата складання "28" 03. 2019 року

Ігнатова Л.А.

Чабан Л.В.

СИТУАЦІЙНИЙ ПЛАН, М 1:2000

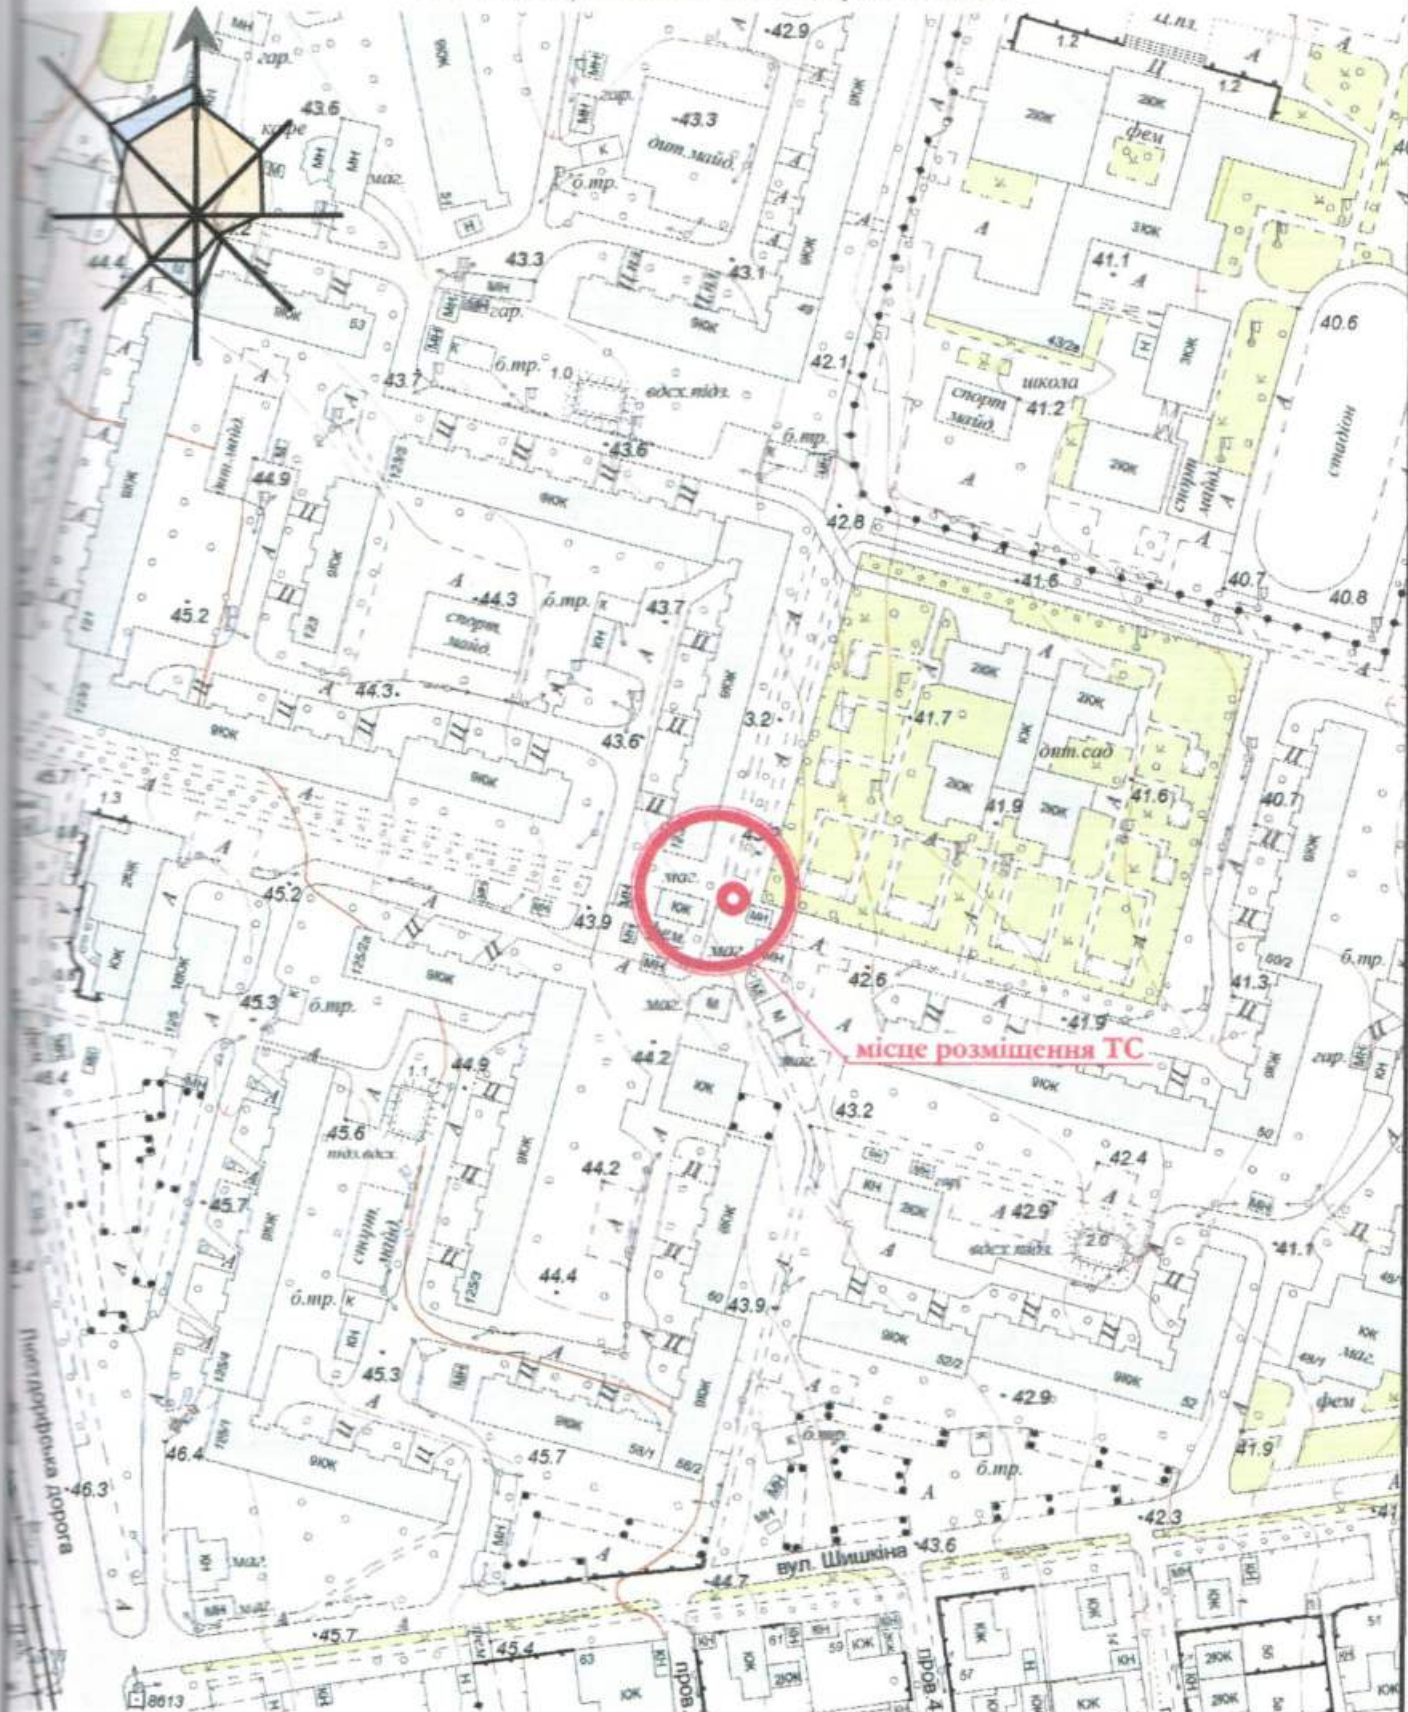

ГАП
Кваліфікаційний сертифікат серія АА №000199

Архітектор

Дата складання "28" 03. 2019 року

Ігнатова Л.А.

Чабан Л.В.



This hand-drawn site plan illustrates the layout of several buildings and their relative positions. The plan includes various annotations such as building numbers (e.g., 17, 18), dimensions (e.g., 6.0, 3.0, 1.0), and labels like "МН" and "ДР.". A central area is highlighted with a red outline and labeled "А". The drawing also shows utility lines and a compass rose indicating orientation.

Чабан Л.В.

