

ПОЯСНЮВАЛЬНА ЗАПИСКА

1. Стационарна тимчасова споруда (ТС) призначена для здійснення підприємницької діяльності та має торговельне приміщення для тимчасового перебування людей.
За умовну позначку ± 0.000 прийнятий рівень чистої підлоги ТС.
Ступень вогнестійкості - III
Габаритні розміри в плані ТС - 3.99 м. x 2.40 м. ;
У павільоні розташоване приміщення площею - 8.33 кв.м.;
Внутрішня висота павільону від рівня чистої підлоги складає - 2.45 м.
Загальна висота павільону складає - 2.55 м.
Грунт заснування, до встановлення павільону, ретельно утрамбован щебнем та укладається бетонна тротуарна плитка.
Стіни споруди запроектовані по типу "Сендвич", товщиною 100 мм. із утеплювачем з мінеральної вати й обшивкою.
Обшивка стін по каркасу: зовнішня - металеві профільовані листи; внутрішня (стіни та стеля) - пластикова вагонка.
Підлога з покриттям дошки 40 мм. і утеплювачем (керамзитовий гравій) -200мм.
та покриття з негорючого матеріала.
Покрівля - по металевим прогонам і решетуванню з покриттям із профільованого сталевих листа, з утеплювачем з мінераловатних плит, гідро і пароізоляцією.

Зовнішня обробка:

- поверхні стін - колірний металевий профіль;
- вікна - металопластикові;
- двері - металопластикові;
- покрівля - профільований сталевий лист;


2. ТС підключене до мереж електропостачання згідно з діючими нормами та ТУ. Точка підключення - близька опора, що розташована поряд з територією ділянки.
Опалювання здійснюється від електричного обогрівача.
Освітлення приміщення виконане стельовими світильниками з люмінесцентними лампами.
Розподільні мережі павільонів, виконані проводами з мідними жилами, що прокладені у трубах то приховані в обшивці стін. Мережі обрані по тривалодопустимим струмам навантаження.
Захист мереж від дії струмів коротких замикань та перевантажень здійснюється автоматичними вимикачами щитка.
3. Благоустрій прилеглої території виконується згідно з планом благоустрою. Освітлення території передбачене світильниками, що розміщуються на головному фасаді над входом у ТС.

Директор ООО "Альфа"
Гослицензія АД № 030757

Архітектор



План на отм. 0.000, М 1:50

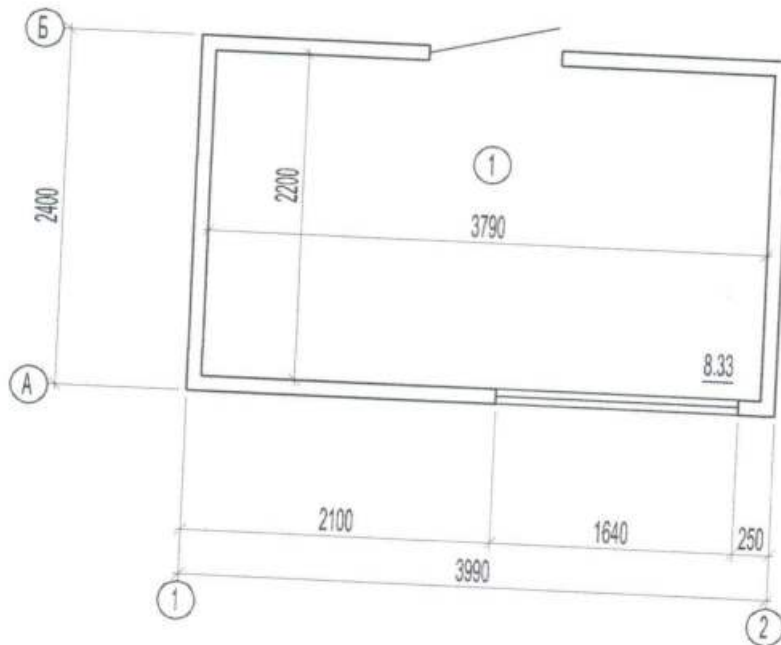

Експлікація


№/№ по плану	Найменування	Площа м2
1	Торгівельне приміщення	8.33
	Загальна площа	8.33
	Площа застройки	9.57

Директор ООО "Альфа"
Госпідприємство АД № 030757

Архітектор



Площа земельної ділянки згідно з документами
на землекористування - землі міста.

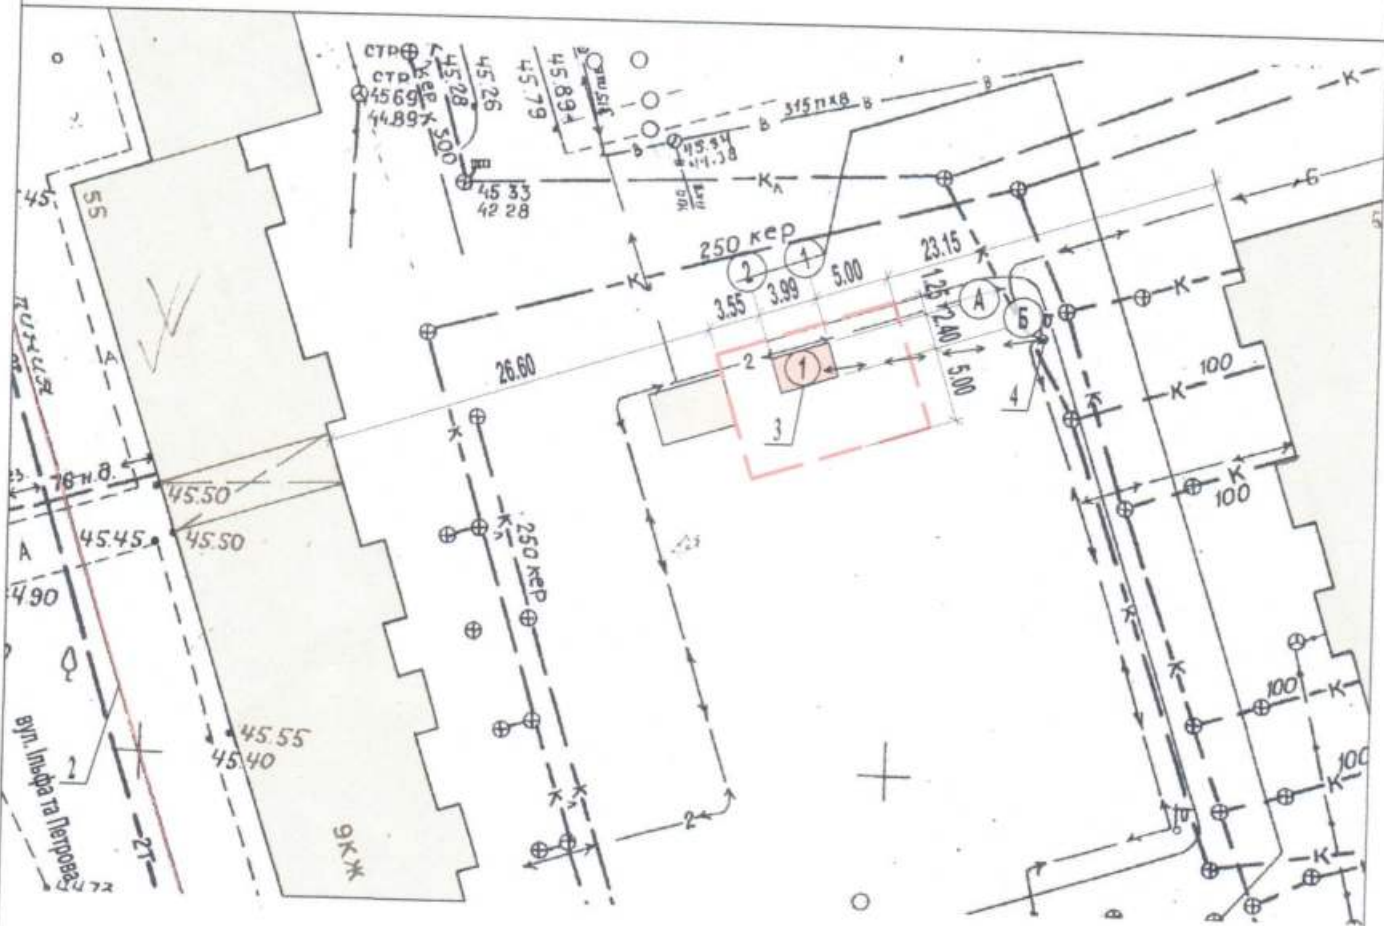

- 1) місце розташування ТС;
- 2) червоні лінії;
- 3) лінії регулювання забудови;
- 4) місця підключення до інженерних мереж;


- - межа благоустрою ділянки розміщення ТС
- - проектна ТС
- - існуючі будівлі
- - підключення до мереж електропостачання

Архітектор



Ситуаційний план, М 1:2000

місце розміщення об'єкту

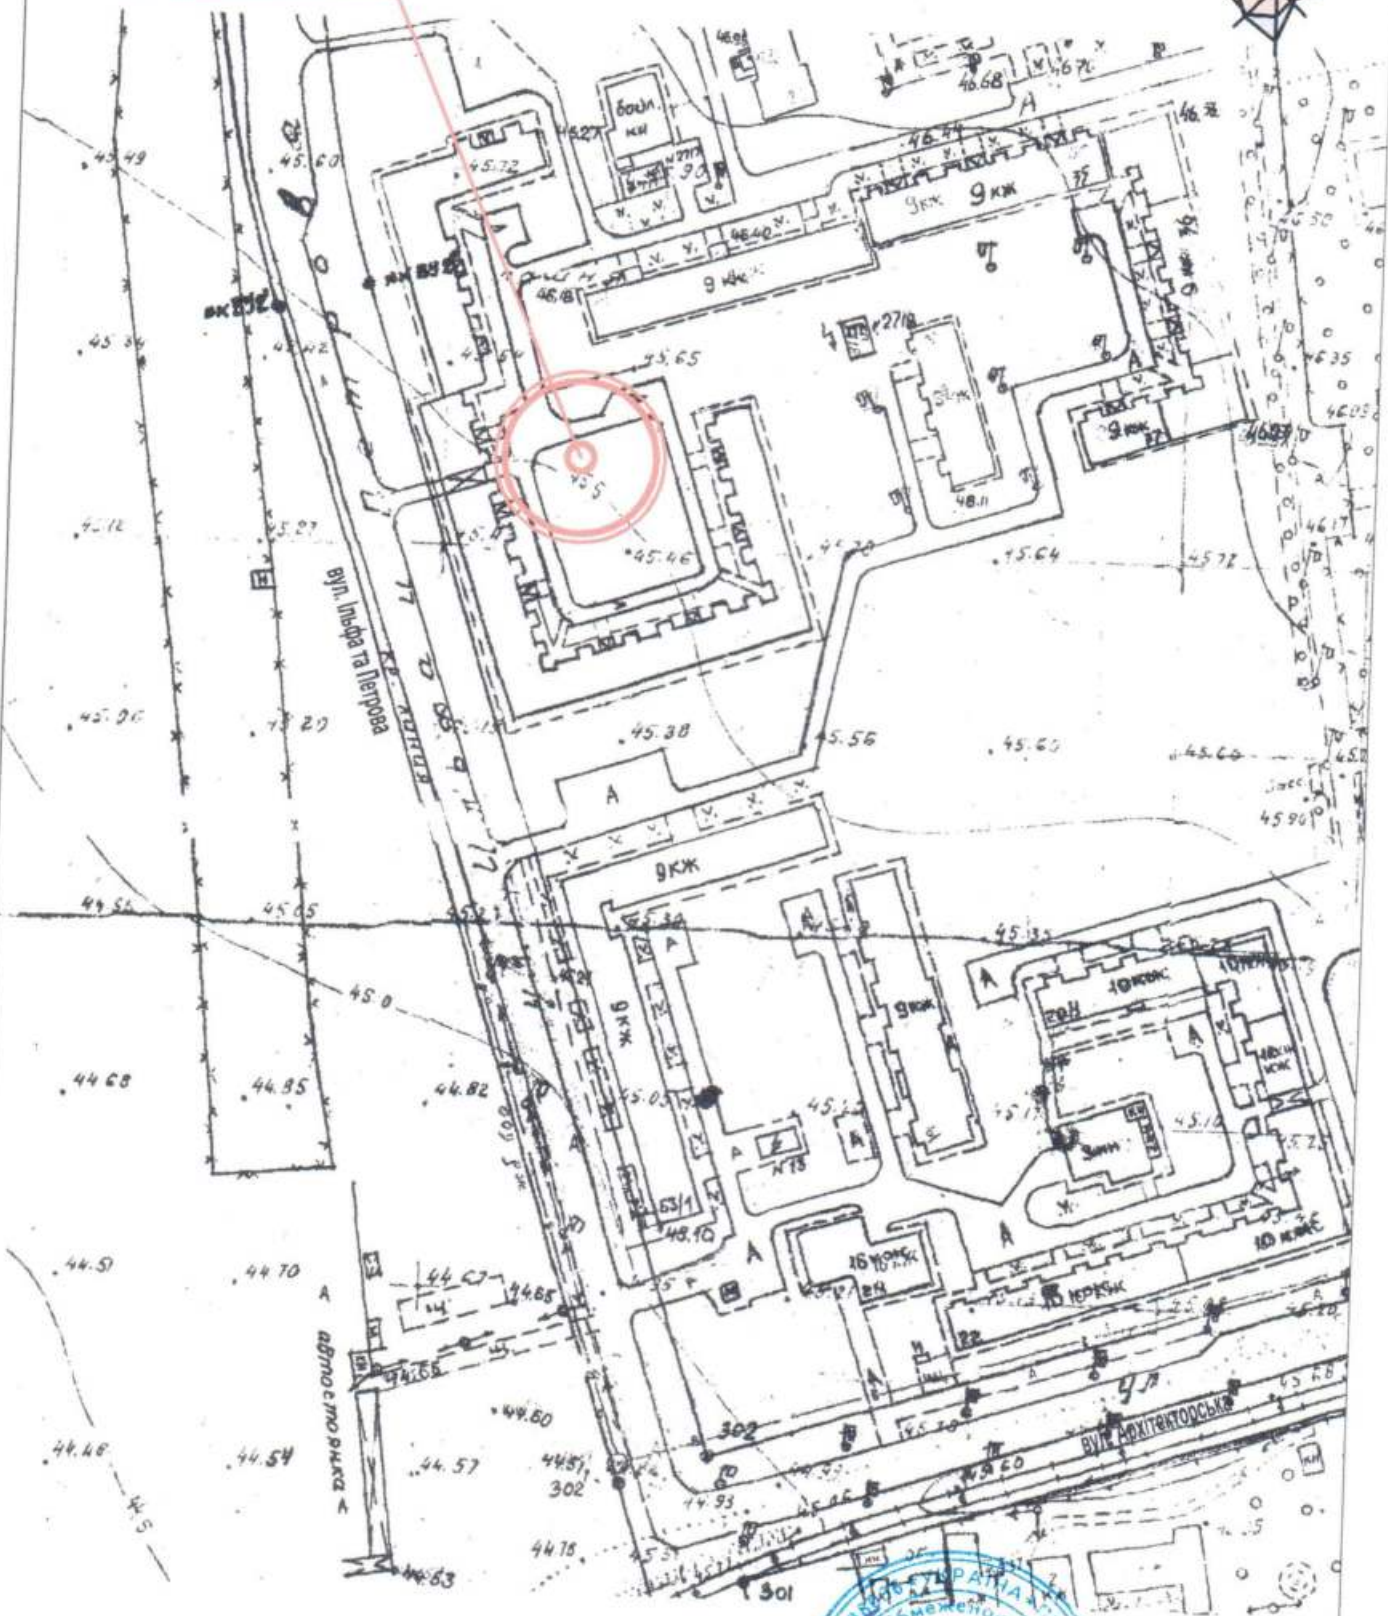

Директор ООО "Альфа"
Гослицензия АД № 030757

Архітектор

