

СТИСЛА ПОЯСНЮВАЛЬНА ЗАПИСКА

1. Група стаціонарних тимчасових споруд для здійснення підприємницької діяльності має торгівельні приміщення для тимчасового перебування людей. За умовну позначку ± 0.000 прийнятий рівень чистої підлоги ТС.
Ступінь вогнестійкості - Ша.
Група стаціонарних тимчасових споруд являє собою 5 павільйонів прямокутної форми.
Габаритні розміри ТС 1, ТС 2, ТС 3, ТС 4, ТС 5 - 5,5 x 4,2 м у плані.
Загальна площа групи ТС - 115,5 м².
Внутрішня висота павільйонів від рівня чистої підлоги складає - 2,70 м.
Загальна висота складає - 3,05 м.
Грунт основи, до встановлення ТС, ретельно утрамбовується щебнем та укладається бетонна тротуарна плитка.
Стіни споруд запроектовані товщиною 100 мм із сертифікованим утеплювачем з мінеральної вати та обшивкою з обох сторін.
Обшивка стін по каркасу: зовнішня - по металевому каркасу композитні матеріали типу "Алюкобонд"; внутрішня (стіни та стеля) - пластикова вагонка.
Підлога - дерев'яні дошки 40 мм по металевому каркасу з утеплювачем з пенополістерольних плит та покриттям антипіринами та антигрибковими засобами.
Покрівля - по металевим прогонам і риштуванню з покриттям профнастілом, з утеплювачем з мінераловатних плит.

Зовнішня обробка:
поверхні стін - композитні матеріали типу "Алюкобонд";
вікна та двері - металопластикові з вакуумними склопакетами;
покрівля - профнастіл.
2. Група стаціонарних тимчасових споруд підключається до мереж електропостачання згідно з діючими нормами та ТУ. Точка підключення - згідно з ТУ.
Опалення - електричне з встановленням навісних електро-конвекторів з регулюванням температури.
Освітлення приміщення виконується світильниками з діодними лампами.
Розподільні мережі виконані проводами з мідними жилами, що прокладені у трубах та приховані в обшивці стін.
Захист мереж від дії струмів, коротких замикань та перевантажень здійснюється автоматичними вимикачами щитка. Передбачене заземлення.
3. Благоустрій прилеглої території виконується згідно з планом благоустрою.
Освітлення території передбачене світильниками, що розміщуються на головних фасадах та над входами в ТС.

Директор ТОВ "ГРАДБУД-ГБ" 


Архітектор

Кваліфікаційний сертифікат серія АА № 002874



ЕСКІЗИ ФАСАДІВ ТС

Головний фасад групи ТС М 1:100

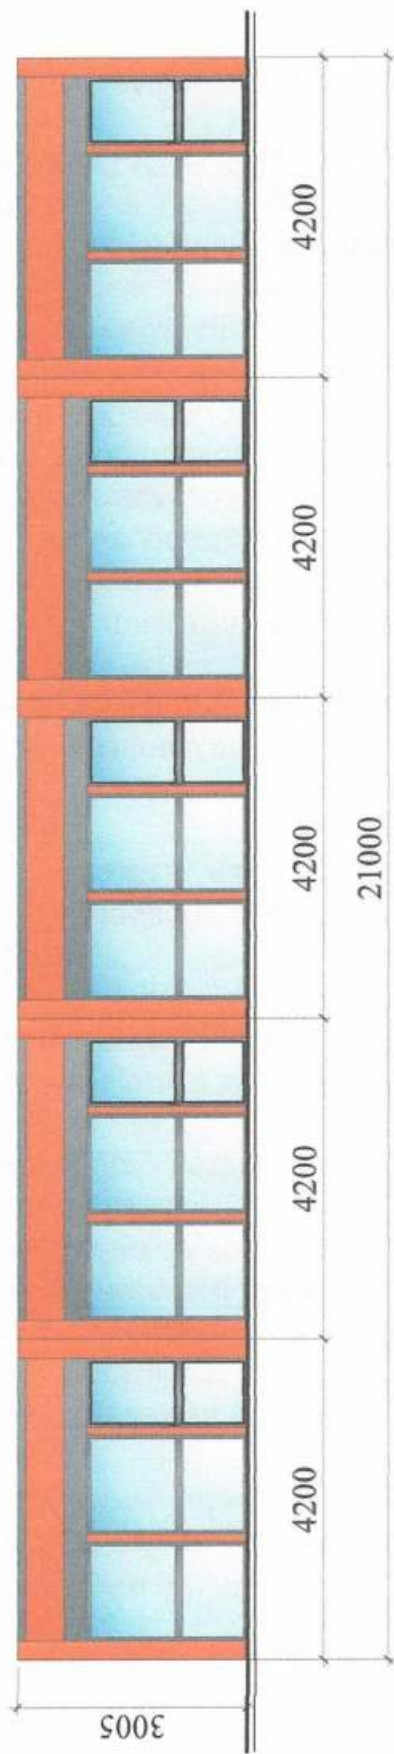

Бічний фасад групи ТС М 1:100



Директор ТОВ "ГРАДБУД-ГБ"
О.В. Кльоб


Архітектор

К.М. Багіріна

Кваліфікаційний сертифікат серії АХ № 002874



План групи ТС М 1:100

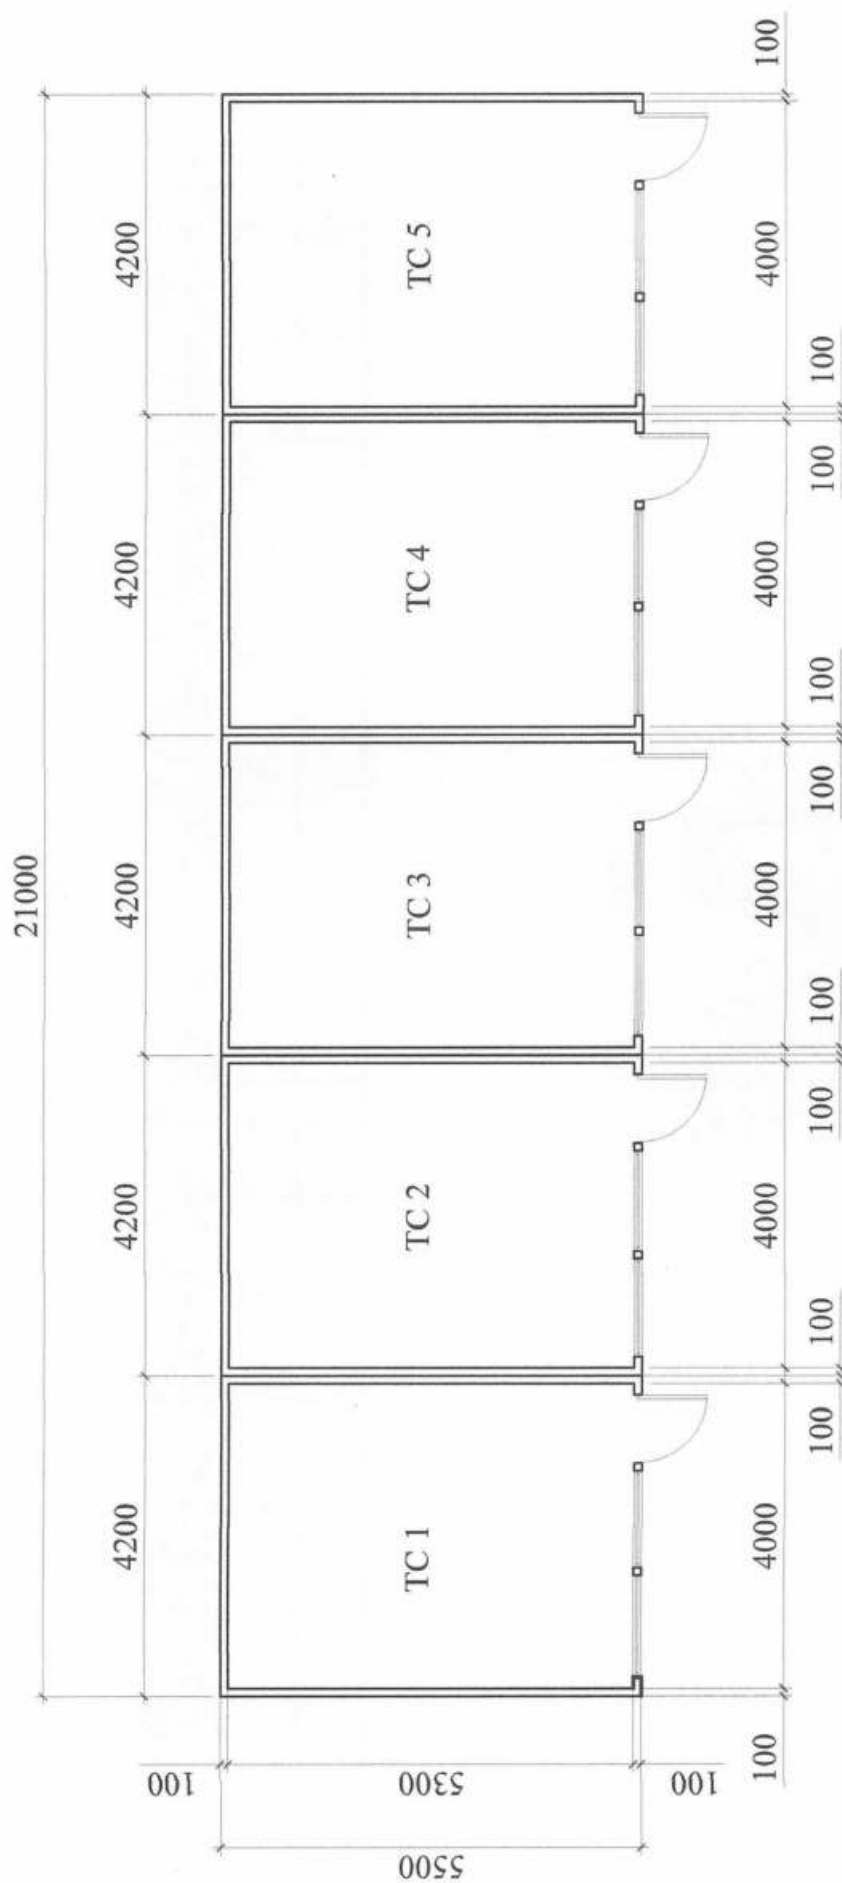


Архітектор
К.М. Багіна
Кваліфікаційний сертифікат серія АА № 002874



Директор ТОВ "ГРАДБУД-ГБ"
О.В. Кльоб

СХЕМА РОЗМІЩЕННЯ ГРУПИ ТС М 1:500

Площа земельної ділянки згідно з документами
на землекористування - землі міста

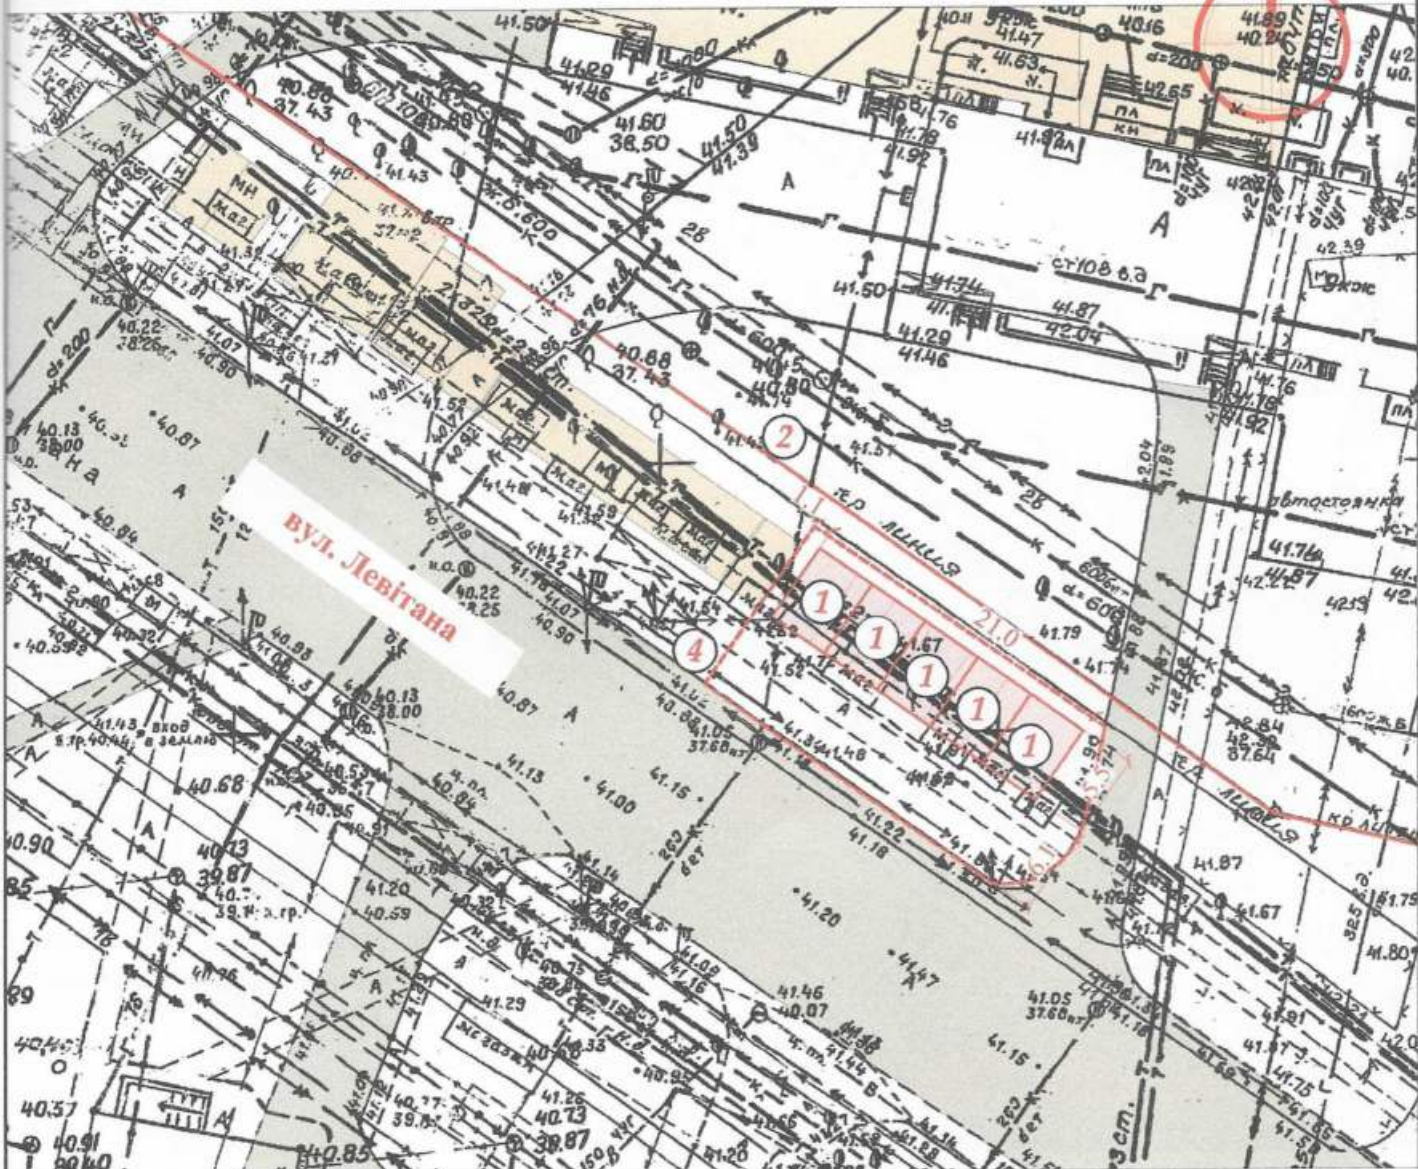

Експлікація:

- 1) місце розташування ТС;
- 2) червоні лінії;
- 3) лінії регулювання забудови;
- 4) місця підключення до інженерних мереж.

Умовні позначення:

- межа благоустрою ділянки розміщення ТС
- проектна ТС
- існуючі будівлі та споруди
- існуючі дороги та проїзди
- підключення до мереж електропостачання

Директор ТОВ "ГРАДБУДІГБ"

Архітектор

Кваліфікаційний сертифікат серія АА № 002874


О.В. Кльоб

Архітектор
Регістраційний № 2874
К.М. Багіра

Ситуаційний план М 1:2000

Місце розміщення об'єкту

N

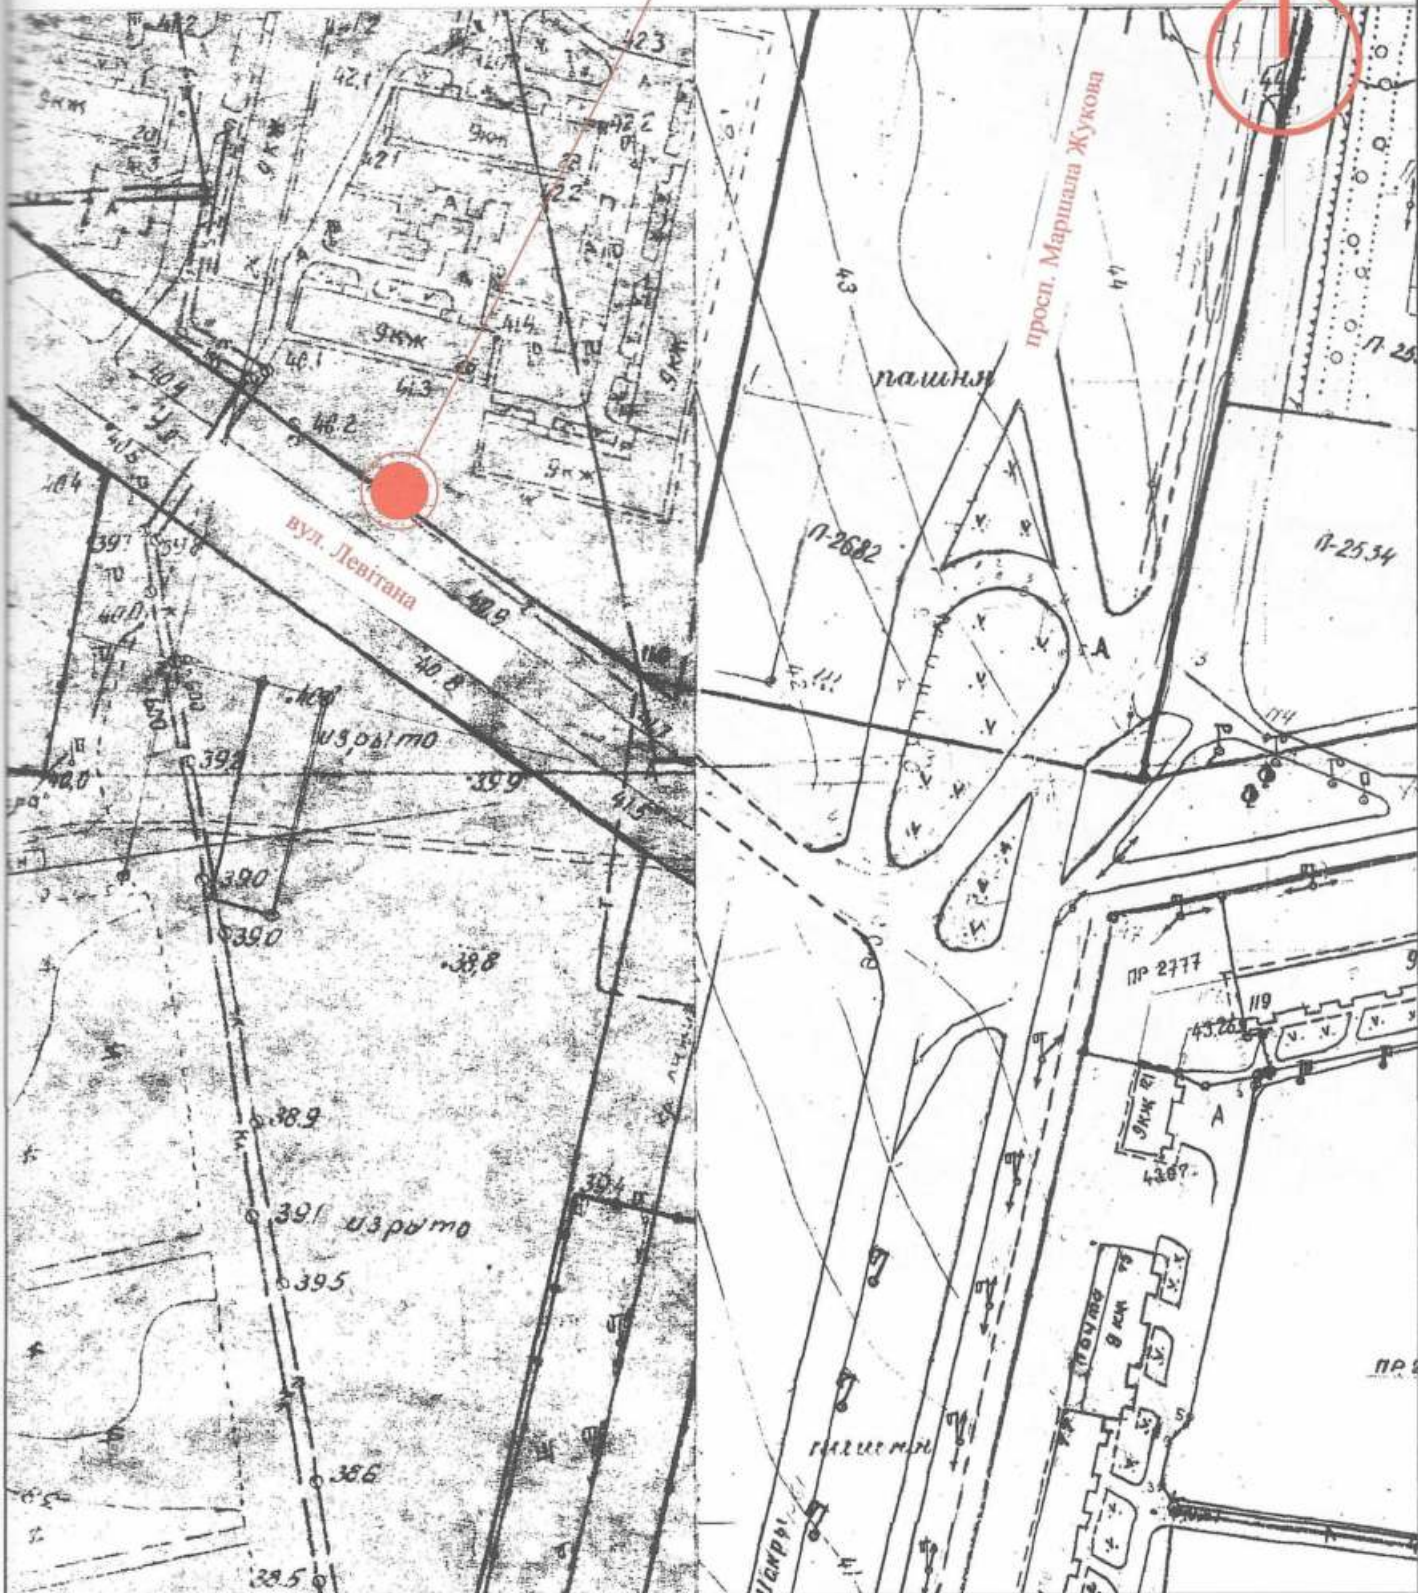

Директор ТОВ "ГРАДБУД-ГБ"

Архітектор

Кваліфікаційний сертифікат серія АА № 002874

О.В. Кльоб

К.М. Багріна

