

СТИСЛА ПОЯСНЮВАЛЬНА ЗАПИСКА

1. Група стаціонарних тимчасових споруд для здійснення підприємницької діяльності, яка має торговельні приміщення для тимчасового перебування людей.
Ступінь вогнестійкості — IIIа
Павільйони неправильної форми.
Габаритні розміри групи у плані — 8.70м x 4.00м x 5.00м x 2.00м x 3.70м x 6.00м
Площа забудови групи — 42.20м²
Площа твердого покриття групи — 42.20м²
Загальна площа групи — 39.82м²
Загальна висота групи — 3.10м
Внутрішня висота складає — 2.60м.
Ґрунт заснування, до встановлення ТС, ретельно утрамбовується щебенем та укладається тротуарна плитка.
Стіни споруди запроектовані товщиною 100 мм із сертифікованим утеплювачем із мінеральної вати та обшивкою з обох сторін.
Обшивка сторін по каркасу: зовнішня — по металевому каркасу профільовані металеві листи, внутрішня (стіни та стеля) — пластикова вагонка
Підлога — дерев'яні дошки 40 мм по металевому каркасу з утеплювачем з пенополістерольних плит та покриттям антипірінами та антигрибковими засобами.
Покрівля — по металевим прогонам і решетуванню з покриттям профнастілом, з утеплювачем з мінераловатних плит.
Зовнішня обробка:
поверхні стін — профільовані металеві листи.
Вікна та двері — металопластикові із вакуумними склопакетами, покрівля — профнавістіл.

2. Група ТС підключається до мереж електропостачання згідно з чинними нормами та ТУ. Точка підключення згідно з ТУ.
Опалення - електричне з встановленням навісних електро-конвекторів з регулюванням температури.
Освітлення приміщення виконується світильниками з діодними лампами.
Розподільні мережі виконані проводами із мідними жилами, що прокладені у трубах та приховані в обшивці стін.
Захист мереж від дії струмів, коротких замикань та перевантажень здійснюється автоматичними вимикачами щитка. Передбачене заземлення.

3. Благоустрій прилеглої території виконується згідно з планом благоустрою. Освітлення території передбачене світильниками, що розміщуються на основному фасаді та над входом в ТС.

Директор ТОВ "Архітектурне Бюро "АРКАДІЯ"
Архітектор

Кваліфікаційний сертифікат серія АА №002590




Смаглій Д.П.
Глінін Д.Ю.

Technical drawing of a building facade elevation. The drawing shows a vertical section with horizontal siding. The overall width is 3100, and the overall height is 8700. The main section has a width of 2900 and a height of 8700. The side section has a width of 200. The facade features five windows: three large square windows and two smaller windows. The windows are arranged vertically, with the two smaller windows at the top and bottom, and the three large square windows in the middle. The windows are shown in a perspective view, with the glass panes colored blue. The drawing includes dimension lines and labels for the width and height of the various sections.

Technical drawing of a rectangular object with dimensions 3100 (width) and 6000 (height). The object features a blue vertical strip on the left and a red horizontal strip at the top. A circular stamp is visible in the bottom right corner.

Кваліфікаційний сертифікат серія АА №002690

ПЛАН ГРУПИ СТАЦІОНАРНИХ ТС М 1:50

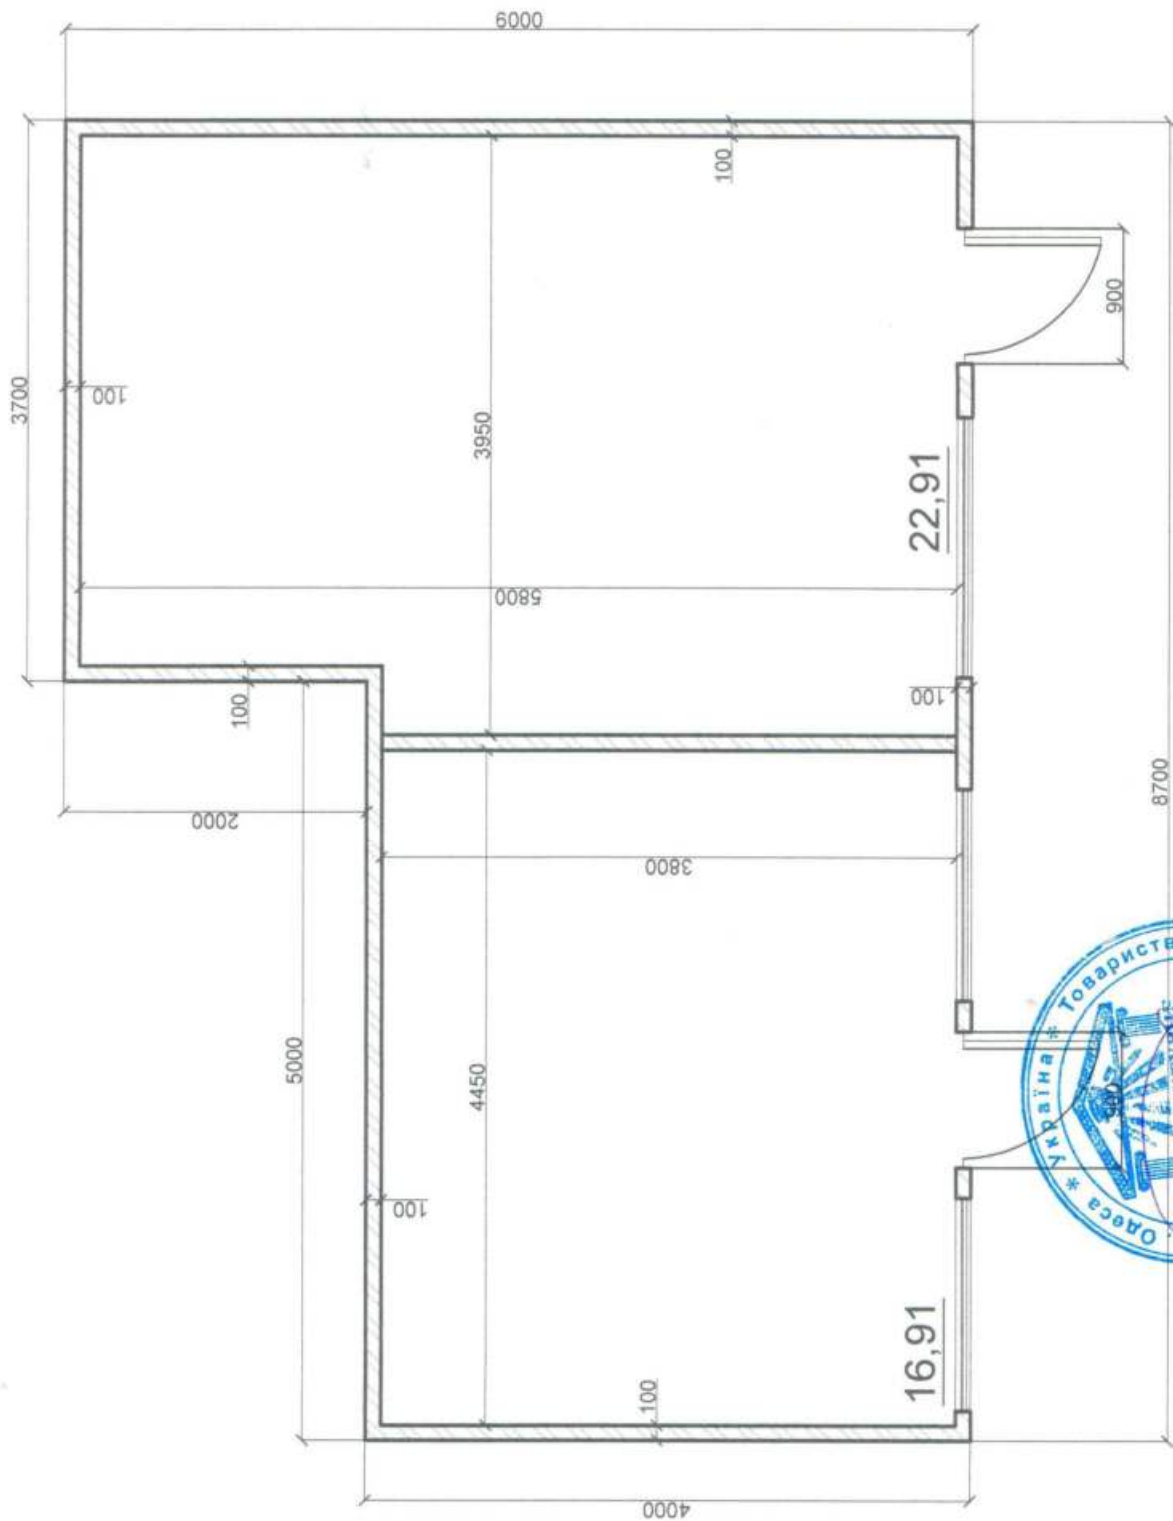

Директор ТОВ "Архітектуре Бюро " Аркадій Смага Д.П.

Архітектор

Кваліфікаційний сертифікат серія АА №002590

СХЕМА РОЗМІЩЕННЯ ГРУПИ СТАЦІОНАРНИХ ТС М 1:200

Площа земельної ділянки згідно з документами на
землекористування - землі міста



ТЕП по благоустрою:

Площа ділянки благоустрою-66.9м2
Загальна площа мостіння -24.7м2
в т.ч. під ТС -42.2м2
Урна - 2шт.
Вуличний ліхтар -2шт.

Умовні позначення:

- | | | | |
|---|------------------------------|---|--|
|  | - існуючі газони |  | - межа благоустрою ділянки розміщення ТС |
|  | - тротуарна плитка |  | - існуюча ТС |
|  | - існуюче асфальтне покриття |  | - існуючі будівлі |
|  | - урна |  | - існуючі дороги |
|  | - вуличний ліхтар | | |

Директор ТОВ "Архітектурне Бюро "Аркадія"

Архітектор

Кваліфікаційний сертифікат серія АА №002590




Савлій Д.П.

Гринін Д.Ю.

СИТУАЦІЙНИЙ ПЛАН М 1:2000

Місце розміщення об'єкту

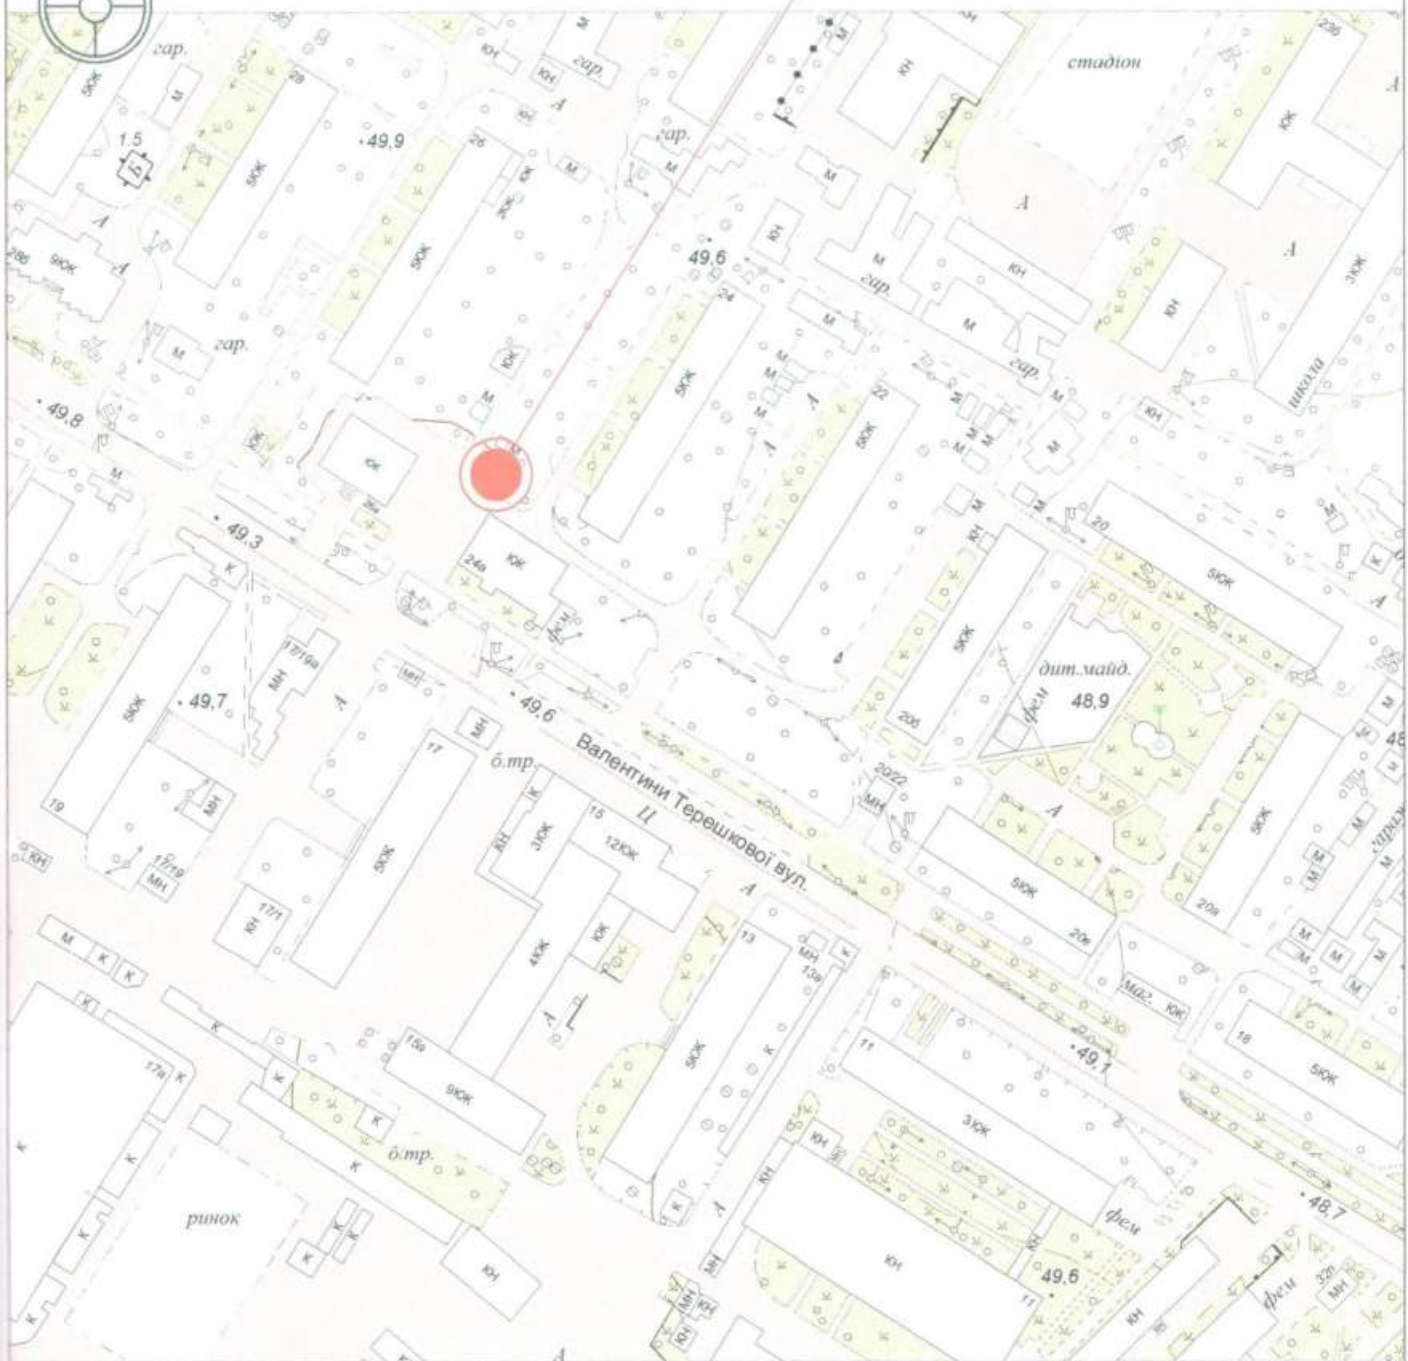

Директор ТОВ "Архітектурне Бюро "Аркадія"

Архітектор

Кваліфікаційний сертифікат серія АА №002590



Д.П. Д.П.

Д.Ю. Д.Ю.