


СТИСЛА ПОЯСНЮВАЛЬНА ЗАПИСКА

1. Стационарних тимчасових споруд ФОП Сирота В.П., розташована за адресою: вул. Крайня, 1, має закриті приміщення для тимчасового перебування людей.
Ступінь вогнестійкості – IIIа.
Габаритні розміри ТС – 3,80м x 2,6м.
Загальна висота ТС – 3,10м.
Площа забудови групи ТС – 9,88 м².
Загальна площа групи ТС – 8,04м².
ТС встановлюється без закладення фундаменту на існуючому асфальтобетонному покритті.
Основні конструкції виконані по металевому каркасу.
Стіни споруди виконані по типу «Сендвич», товщиною 100мм з утеплювачем та обшивкою.
Зовнішня обробка – фасадні панелі типу «Alucobond».
Утеплювач - «Ізовер» по розрахунку.
Внутрішня обробка: стіни - листи ламінованого ДСП, стеля - гіпсокартон.
Підлога в приміщенні - утеплений лінолеум.
Покрівля – по металевим прогонам і решетуванню з покриттям із профільованого сталевих листа, з утеплювачем з мінераловатних плит, гідро- та пароізоляцією.
Віконні та дверні отвори заповнені металопластиковими блоками.
Несучі конструкції покриття - металеві ферми.
2. Стационарну тимчасову споруду забезпечено електроенергією з підключенням к існуючим внутрішньоквартальним мережам. Точка підключення – опора, що розташована поряд з ТС.
Освітлення приміщень виконане стельовими світильниками з люмінесцентними лампами.
Для урахування електроенергії на вводі встановлено вводно-лічильний ящик типу ПВУ.
Захист мереж від дії струмів коротких замикань і перенавантаження здійснюється автоматичними вимикачами щитка.
Електропостачання – згідно договору про користування електричною енергією з ВАТ «Одесаобленерго», та відповідно ТУ.
3. Благоустрій прилеглої території виконується згідно з планом благоустрою. Освітлення території передбачене світильниками, що розміщуються на головному фасаді ТС.

ЕСКІЗИ ФАСАДІВ ТС М 1:50

в осях 1-2

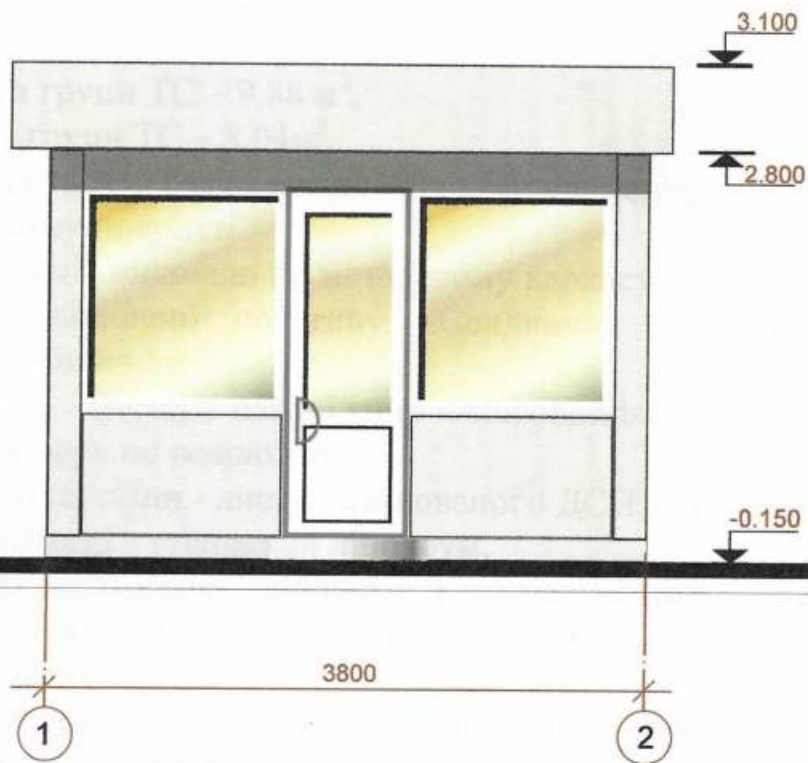

Директор ТОВ "ЕКО Містобудівельник"
Державна ліцензія АВ №515924

Архітектор




Л.І. Графова

Е.В. Урсол

СХЕМА РОЗМІЩЕННЯ ТС М 1:500

Площа земельної ділянки згідно з документами на землекористування землі міста Одеси

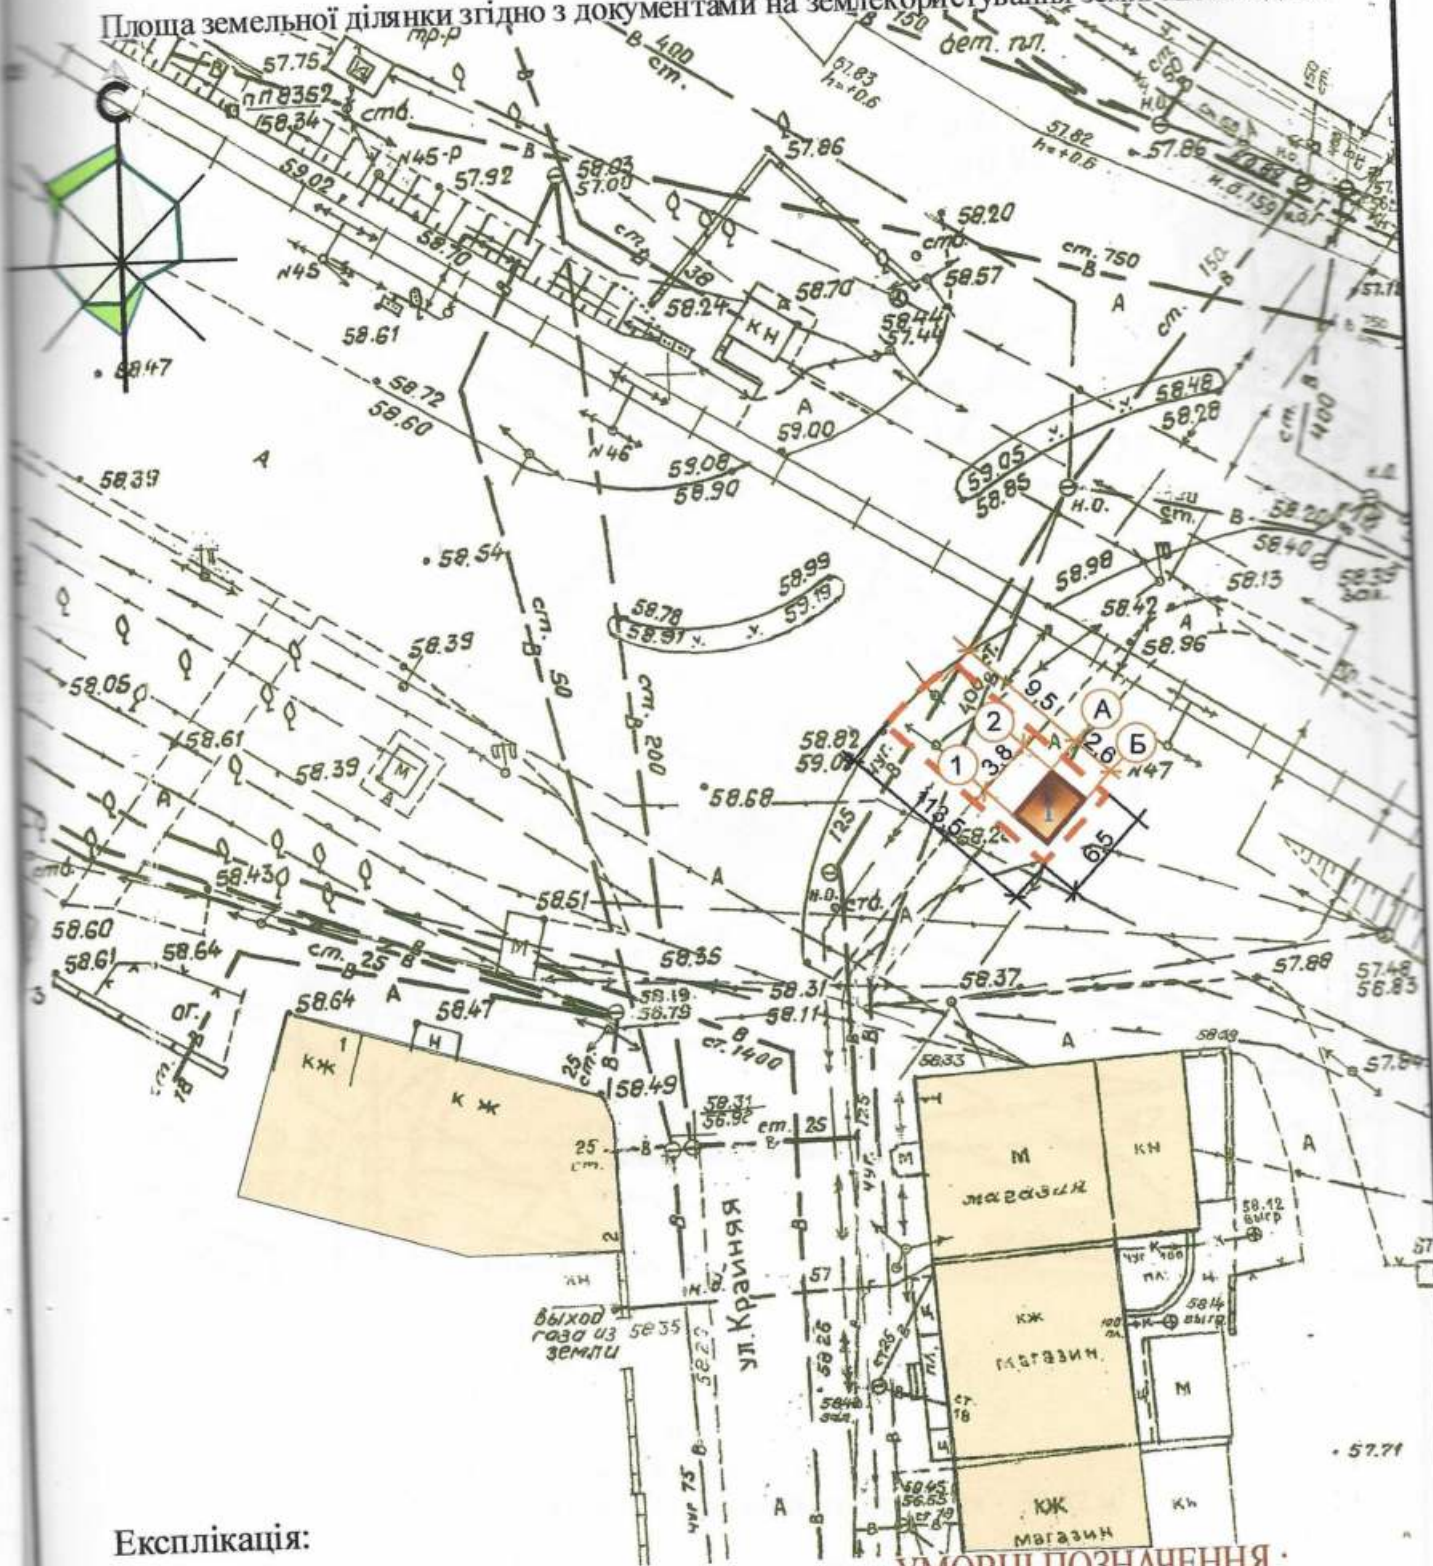

Експлікація:

- 1) місце розташування ТС;
- 2) червоні лінії;
- 3) лінії регулювання забудови;
- 4) місця підключення до інженерних мереж.

Директор ТОВ "ЕКО Містобудівельник"
Державна ліцензія АВ №515924

Архітектор

УМОВНІ ПОЗНАЧЕННЯ:



ТС ФОП Сирота В.П.



межа благоустрою




Існуюча забудова

Л.И. Графова

Е.В. Урсол

СИТУАЦІЙНИЙ ПЛАН М 1:2000

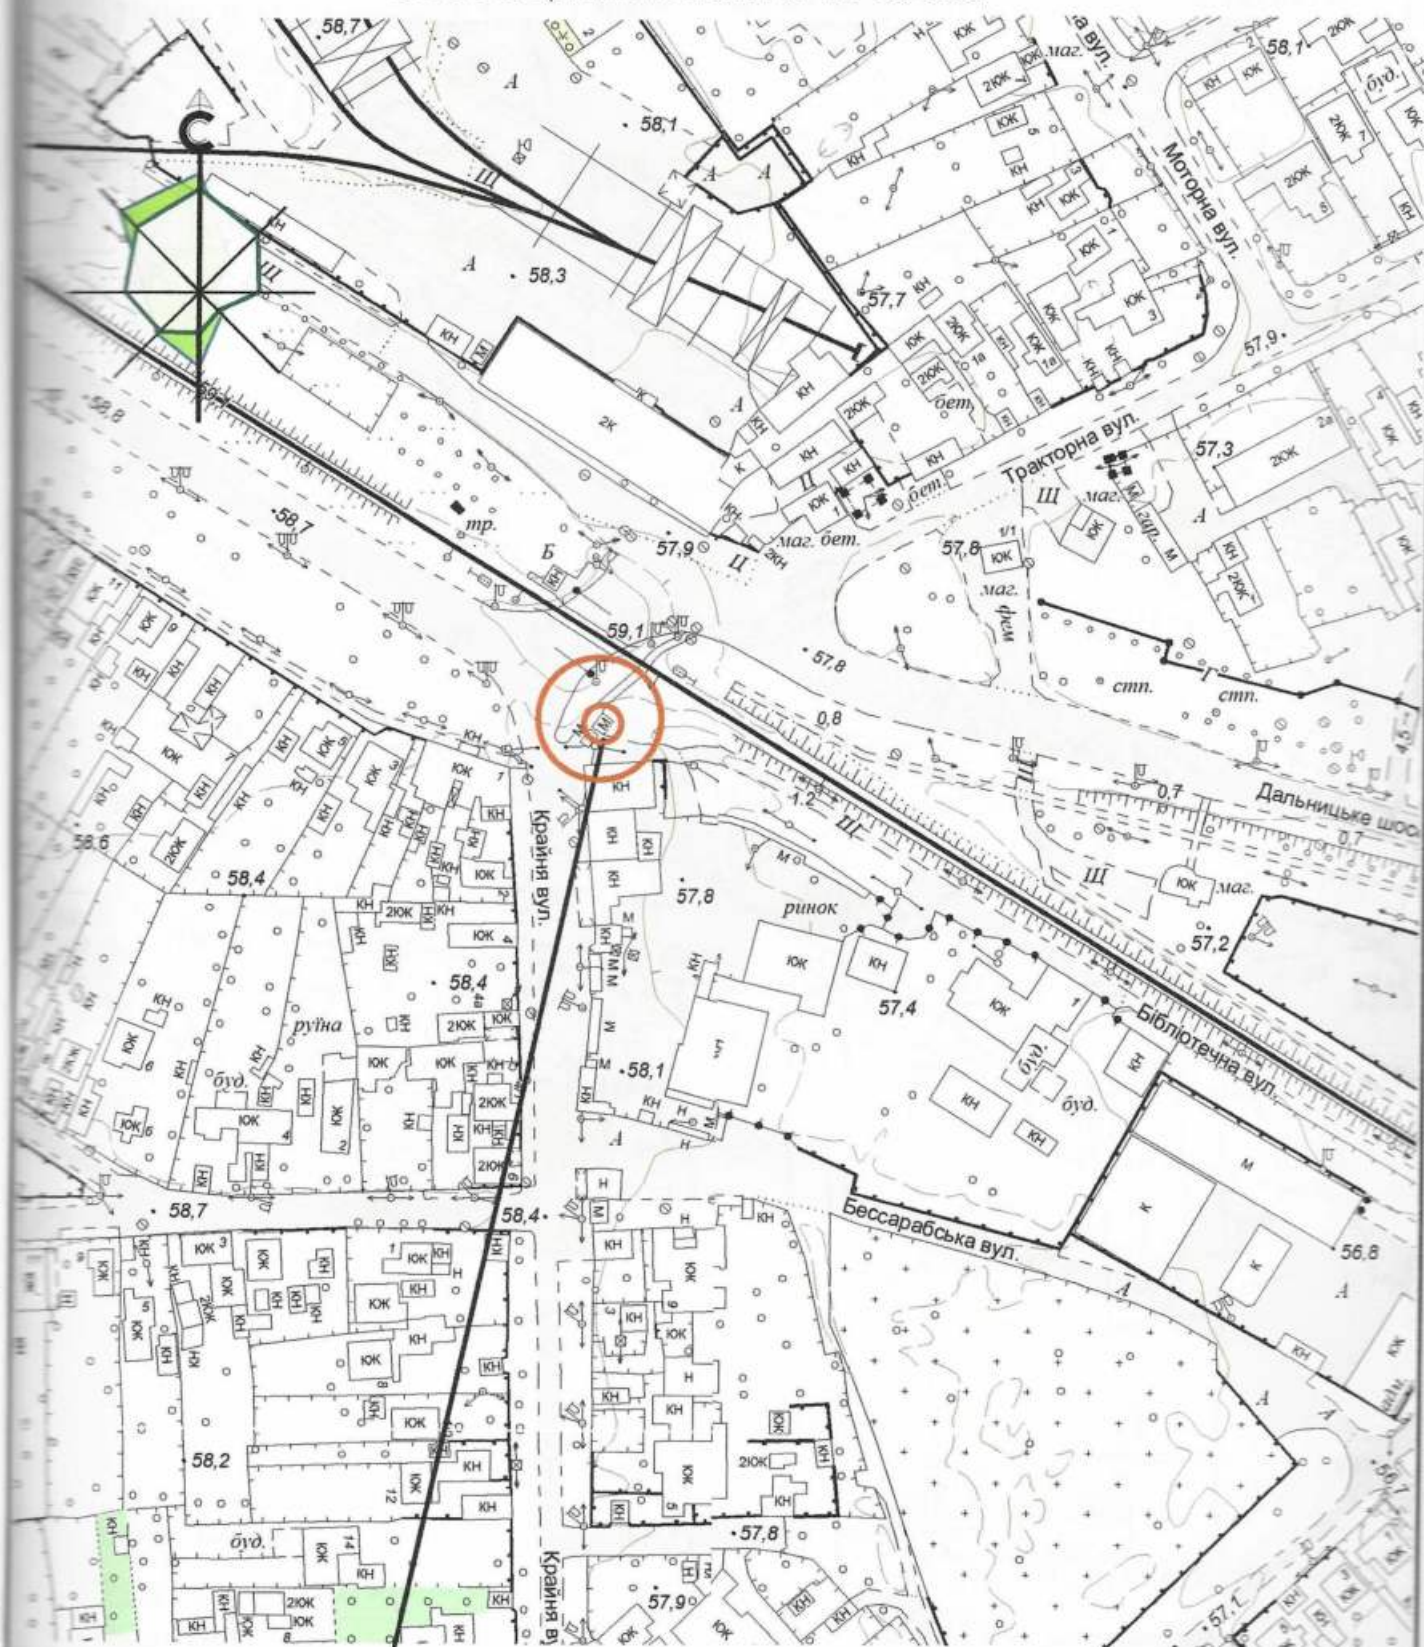

місце розміщення ТС

Директор ТОВ "ЕКО Містобудівельник"
Державна ліцензія АВ №515924

Архітектор

Л.І. Графова

Е.В. Урсол