

СТИСЛА ПОЯСНЮВАЛЬНА ЗАПИСКА

1. Група стаціонарних тимчасових споруд ТОВ «Наташа», розташована за адресою: вул. Житомирська, 2 (напроти), має закриті приміщення для тимчасового перебування людей, включає в себе дві ТС.

Ступінь вогнестійкості – IIIа.

Габаритні розміри групи ТС – 9,6м x 5,0м.

Загальна висота торгового ряду – 3,5м.

Площа забудови групи ТС – 48,0 м².

Загальна площа ТС 1 – 28,8 м².

Загальна площа ТС 2 – 17,4 м².

Загальна площа групи ТС – 46,2м².

Група ТС встановлюється без закладення фундаменту на існуючому асфальтобетонному покритті.

Основні конструкції виконані по металевому каркасу.

Стіни споруди виконані по типу «Сендвич», товщиною 100мм з утеплювачем та обшивкою.

Зовнішня обробка – фасадні панелі типу «Alucobond».

Утеплювач - «Ізовер» по розрахунку.

Внутрішня обробка: стіни - листи ламінованого ДСП, стеля - гіпсокартон.

Підлога в приміщенні - утеплений лінолеум.

Покрівля – по металевим прогонам і решетуванню з покриттям із профільованого сталевих листа, з утеплювачем з мінераловатних плит, гідро- та пароізоляцією.

Віконні та дверні отвори заповнені металопластиковими блоками.

Несучі конструкції покриття - металеві ферми.

2. Група стаціонарних тимчасових споруд забезпечено електроенергією з підключенням к існуючим внутрішньоквартальним мережам. Точка підключення – опора, що розташована поряд з ТС.

Освітлення приміщень виконане стельовими світильниками з люмінесцентними лампами.

Для урахування електроенергії на вводі встановлено ввідно-лічильний ящик типу ПВУ.

Захист мереж від дії струмів коротких замикань і перенавантаження здійснюється автоматичними вимикачами щитка.

Електропостачання – згідно договору про користування електричною енергією з ВАТ «Одесаобленерго», та відповідно ТУ.

3. Благоустрій прилеглої території виконується згідно з планом благоустрою. Освітлення території передбачене світильниками, що розміщуються на головному фасаді ТС.

ЕСКІЗИ ФАСАДІВ групи ТС в осях 1-2



Директор ТОВ "ЕКО Містобудівельник"


Л.І. Графова

Архітектор

О.А. Спінул

ПЛАН НА 0 М. 0.000
масштаб 1:50

100 4800 5000 100 А В

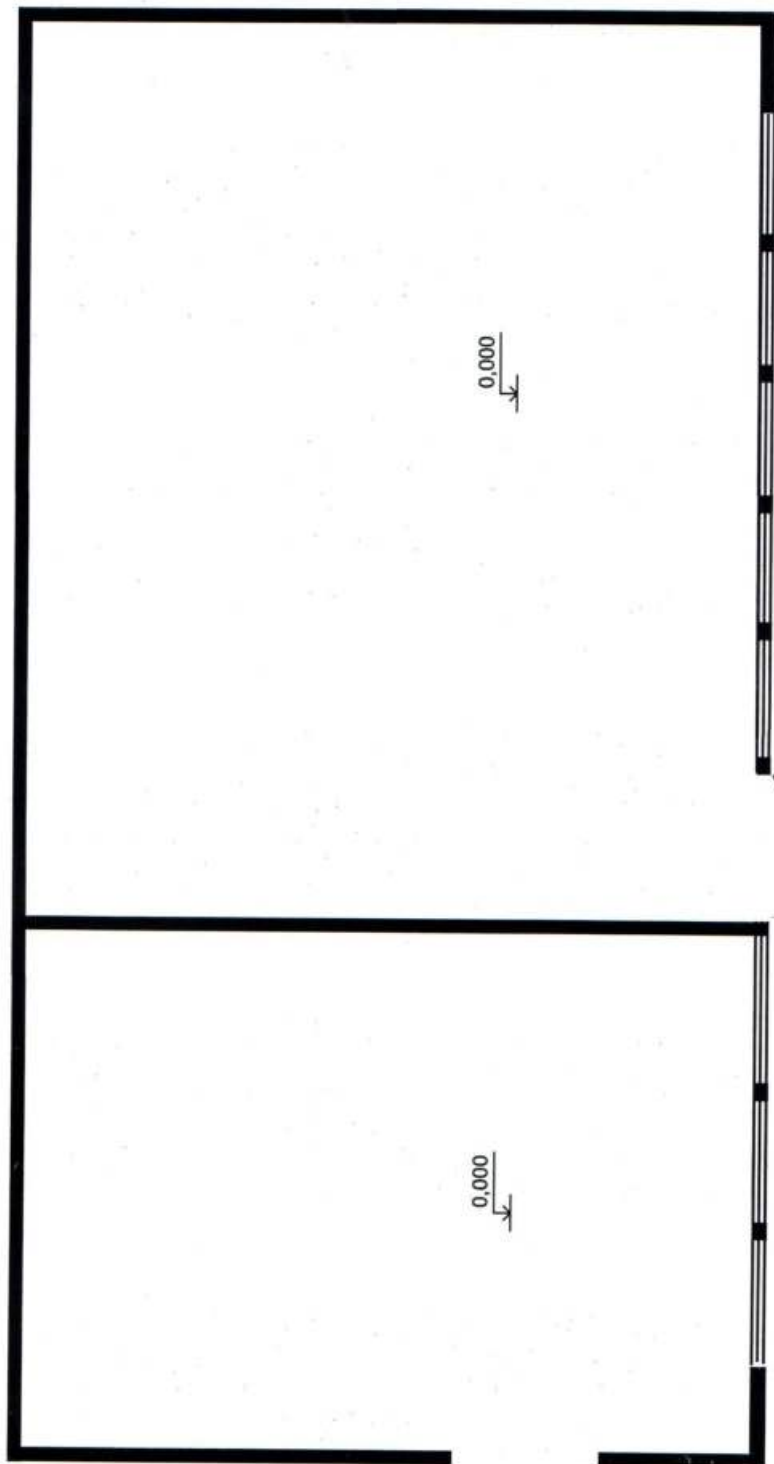

0.000

0.000

100 3400 3600 100 1 2 3 9600 5900 6000 100



Директор ТОВ "ЕКО Містобудівельник"


Архітектор

Л.І. Графова

О.А. Спінул

СХЕМА РОЗМІЩЕННЯ групи ТС М 1:500

Площа земельної ділянки згідно з документами на землекористування - землі міста

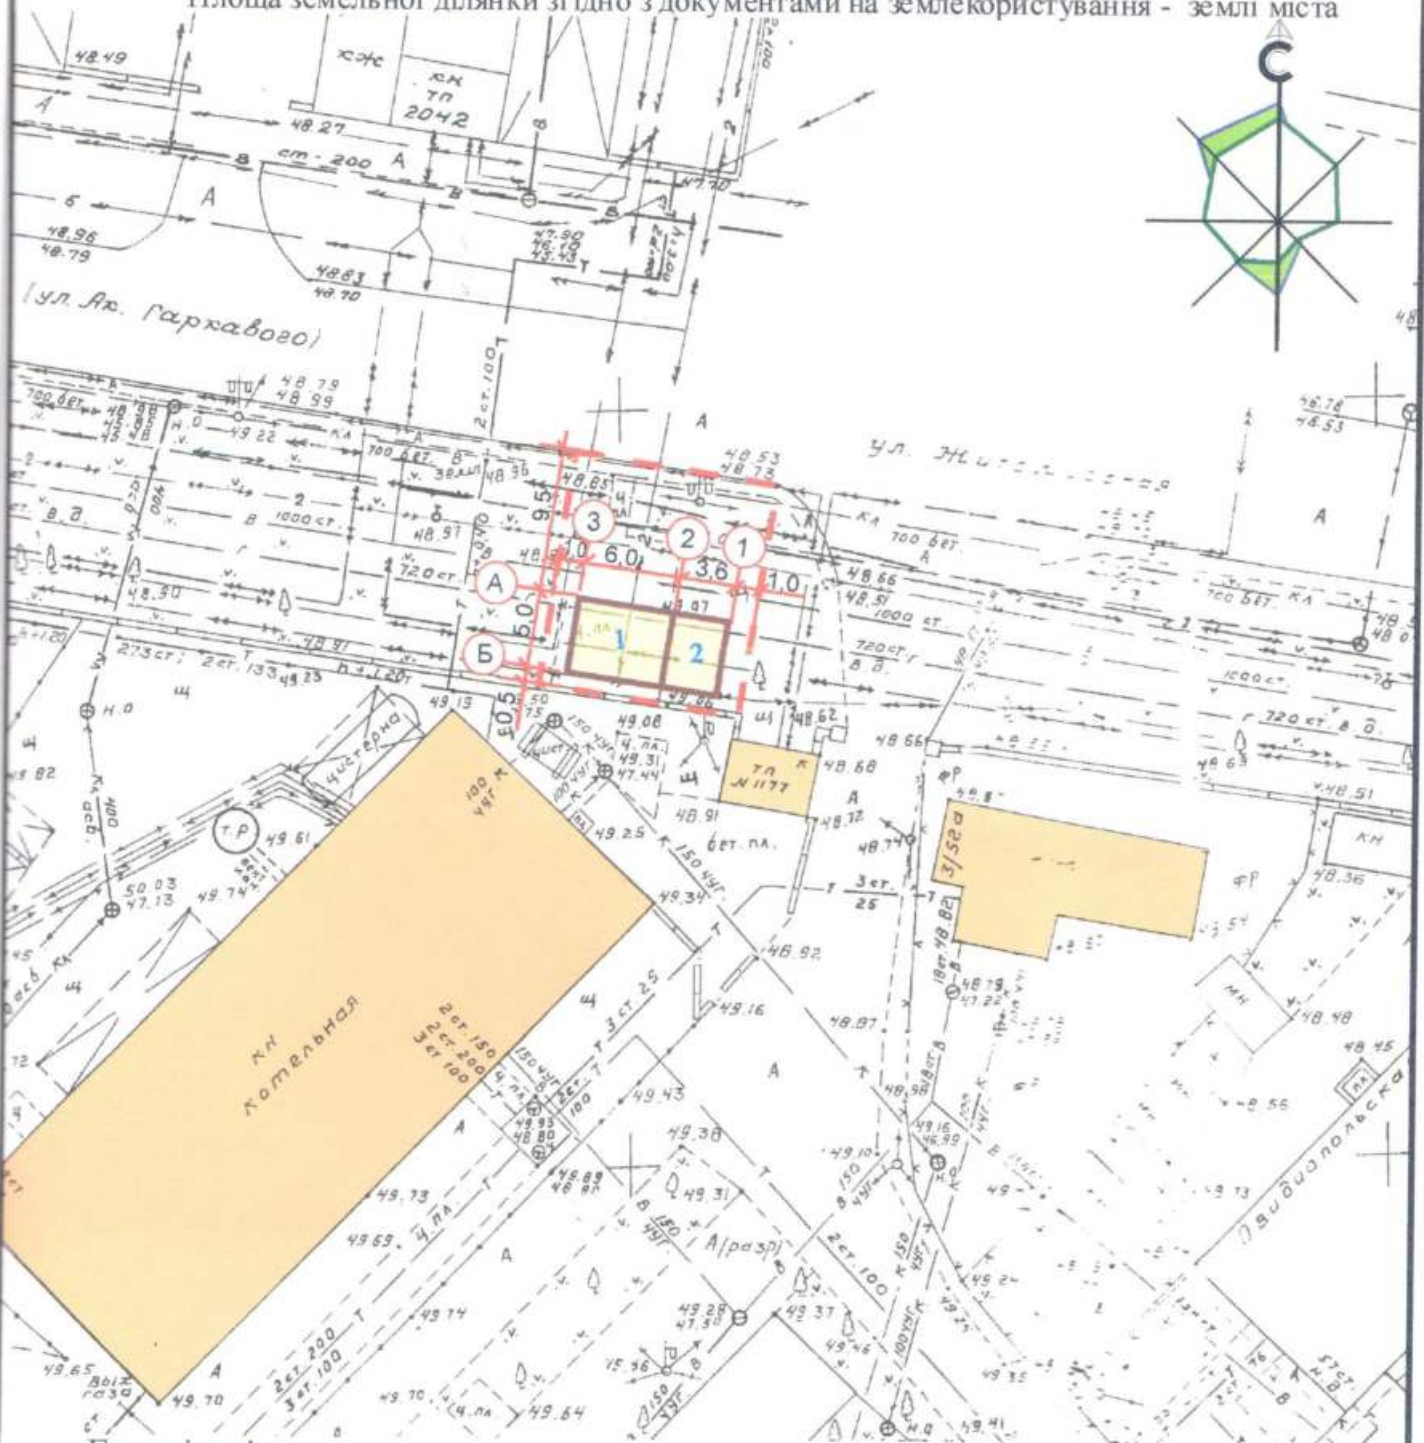

Експлікація:

- 1) місце розташування ТС;
- 2) червоні лінії;
- 3) лінії регулювання забудови;
- 4) місця підключення до інженерних мереж.

Директор ТОВ "ЕКО Містобудівельник"

Архітектор

УМОВНІ ПОЗНАЧЕННЯ:


- Група ТС ТОВ "Наташа"
межа благоустрою
Існуюча забудова



Л.И. Графова

О.А. Спінул

СИТУАЦІЙНИЙ ПЛАН М 1:2000

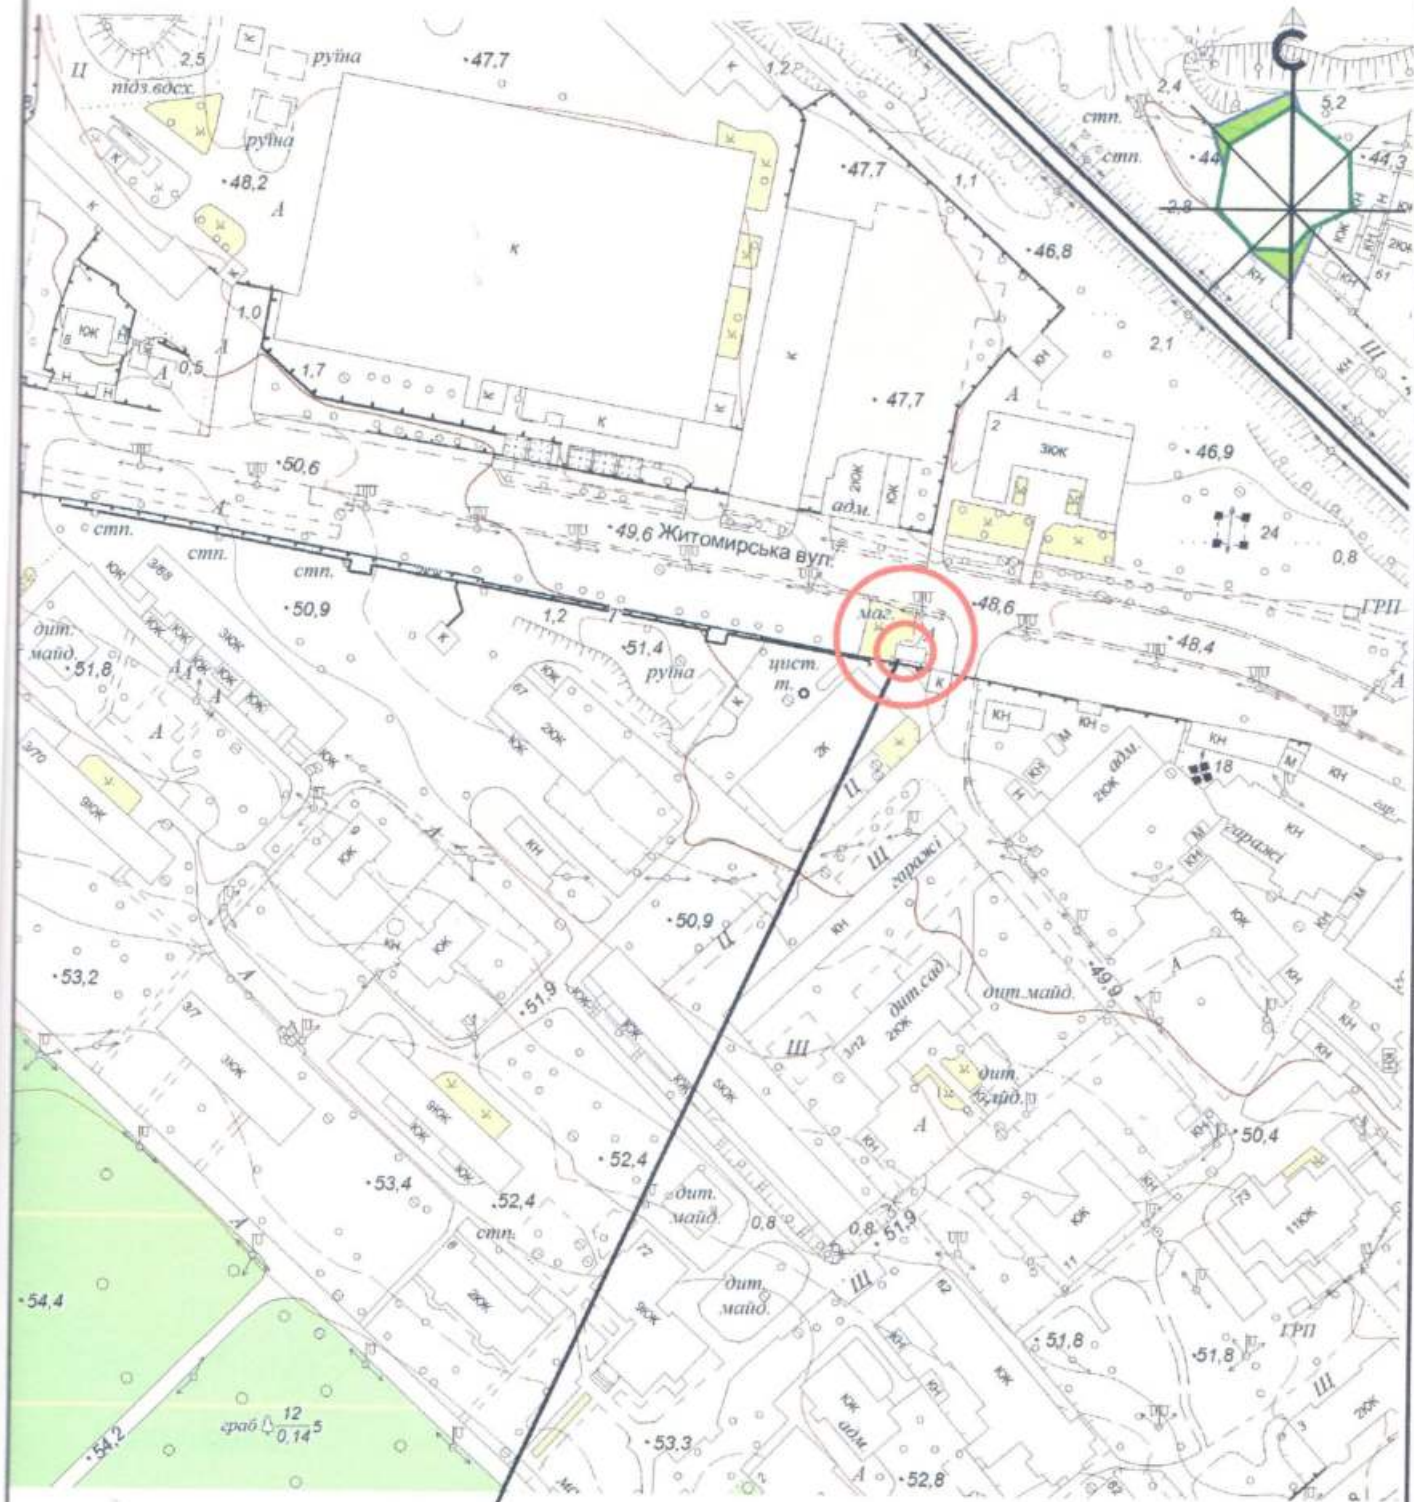місце розміщення групи ТС

Директор ТОВ "ЕКО Містобудівельник"

Архітектор



Л.И. Графова

О.А. Спінул