

ПОЯСНЮВАЛЬНА ЗАПИСКА

1. Тимчасова споруда призначена для здійснення підприємницької діяльності та має торговельне приміщення для тимчасового перебування людей.

За умовну позначку ± 0.000 прийнятий рівень чистої підлоги ТС.

Ступень вогнестійкості - III

Габаритні розміри в плані - 5.60 м. х 4.10 м.;

У павільоні розташоване приміщення площею 21.06 кв.м.;

Внутрішня висота павільону від рівня чистої підлоги складає - 2.40 м.

Загальна висота павільону складає - 2.90 м.

Ґрунт заснування, до встановлення ТС, ретельно утрамбовані щебнем та покладена асфальто-бетонне покриття.

Стіни споруди запроектовані по типу "Сендвич", товщиною 100 мм. із утеплювачем з мінеральної вати й обшивкою.

Обшивка стін по каркасу: зовнішня - металеві профільовані листи; внутрішня (стіни та стеля) - пластикова вагонка.

Підлога з покриттям дошки 40 мм. і утеплювачем (керамзитовий ґравій) - 200 мм.

та покриття з негорючого матеріалу.

Покрівля - по металевим прогонам і решетуванню з покриттям із профільованого сталевих листів, з утеплювачем з мінераловатних плит, гідро і пароізоляцією.

Зовнішня обробка:

поверхні стін - колірний металевий профіль;

вікна - металопластикові;

двері - металопластикові;

покрівля - профільований сталевий лист;

2. ТС підключене до мережі електропостачання згідно з діючими нормами та ТУ. Точка підключення - близька опора, що розташована поряд з територією ділянки.

Опалювання здійснюється від електричного обогрівача.

Освітлення приміщення виконане стельовими світильниками з люмінесцентними лампами.

Розподільні мережі павільонів, виконані проводами з мідними жилами, що прокладені у трубах то приховані в обшивці стін. Мережі обрані по тривалодопустимим струмам навантаження.

Захист мережі від дії струмів коротких замикань та перевантажень здійснюється автоматичними вимикачами щитка.

3. Благоустрій прилеглої території виконується згідно з планом благоустрою. Освітлення території передбачене світильниками, що розміщуються на головному фасаді над входом у ТС.

Директор ООО "Альфа"

Госзаказ № 030757

Архітектор



М.В.Краєвська


В.Ю.Петрушина

ЕСКІЗИ ФАСАДІВ ТС, М 1:50

Фасад в осях "1"- "2", М 1:50



Фасад в осях "А"- "Б", М 1:50

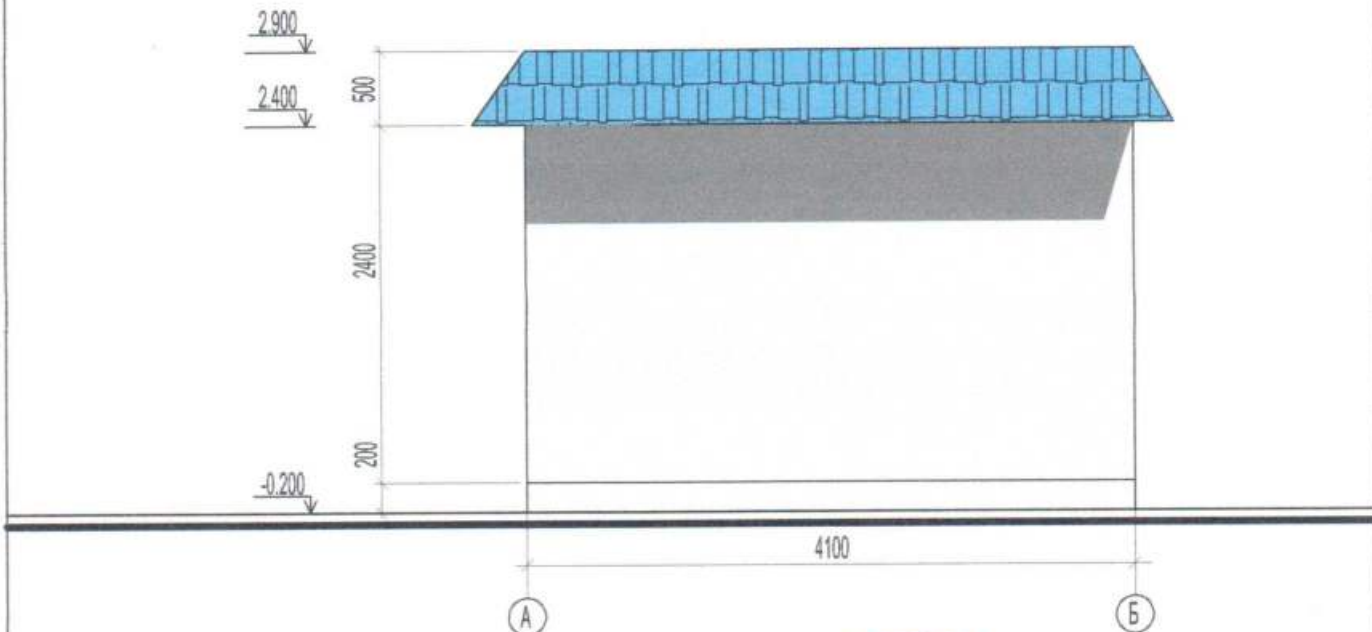

Директор ООО "Альфа"
Гос. реєстрація АД № 030757


Архітектор



М.В. Краєвська

В.Ю. Петрушина

План на отм. 0.000, М 1:50

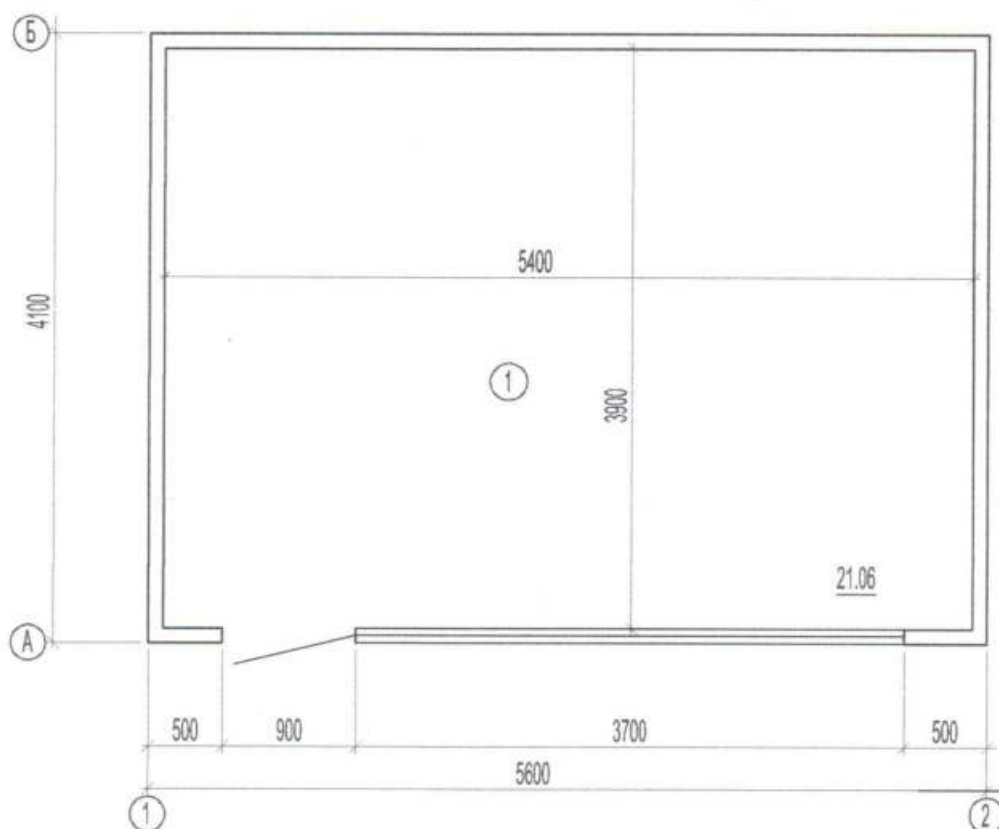

Експлікація

№/№ по плану	Найменування	Площа м2
1	Торгівельне приміщення	21.06
	Загальна площа	21.06
	Площа застройки	22.96

Директор ООО "Альфа"
Госліцензія АД № 030757

Архітектор




М.В. Краєвська

В.Ю. Петрушина

СХЕМА РОЗМІЩЕННЯ ТС, М 1:500

Площа земельної ділянки згідно з документами
на землекористування - землі міста.

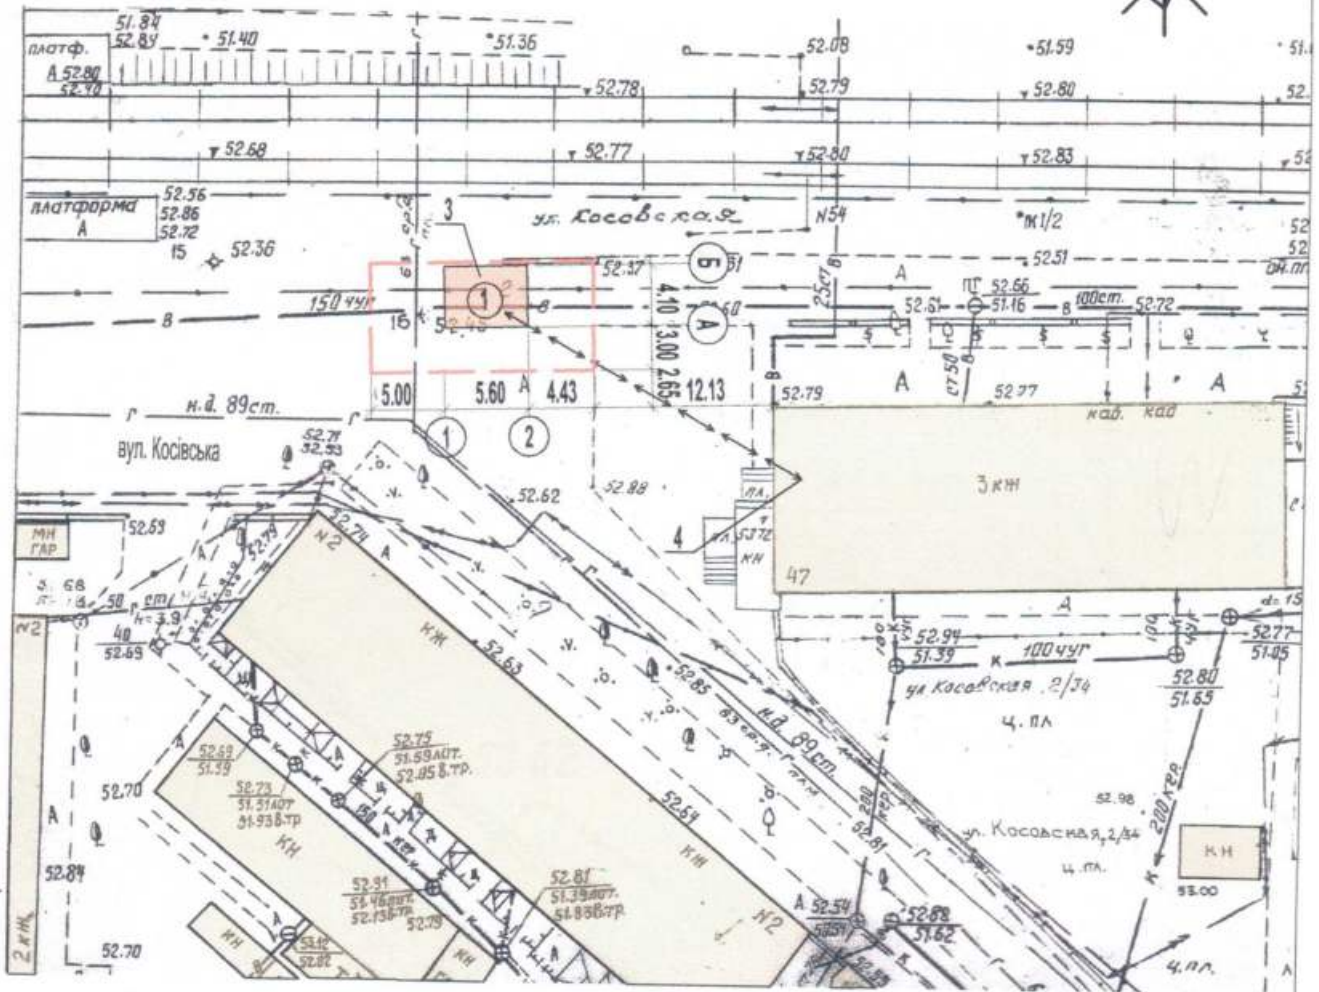

Експлікація:

- 1) місце розташування ТС;
- 2) червоні лінії;
- 3) лінії регулювання забудови;
- 4) місця підключення до інженерних мереж;

Умовні позначення:

- межа благоустрою ділянки розміщення ТС
- проектна ТС
- існуючі будівлі
- підключення до мереж електропостачання

Директор ООО "Альфа"
Госпінспекція АД № 030757


Архітектор



М.В.Краєвська

В.Ю.Петрушина

Ситуаційний план, М 1:2000

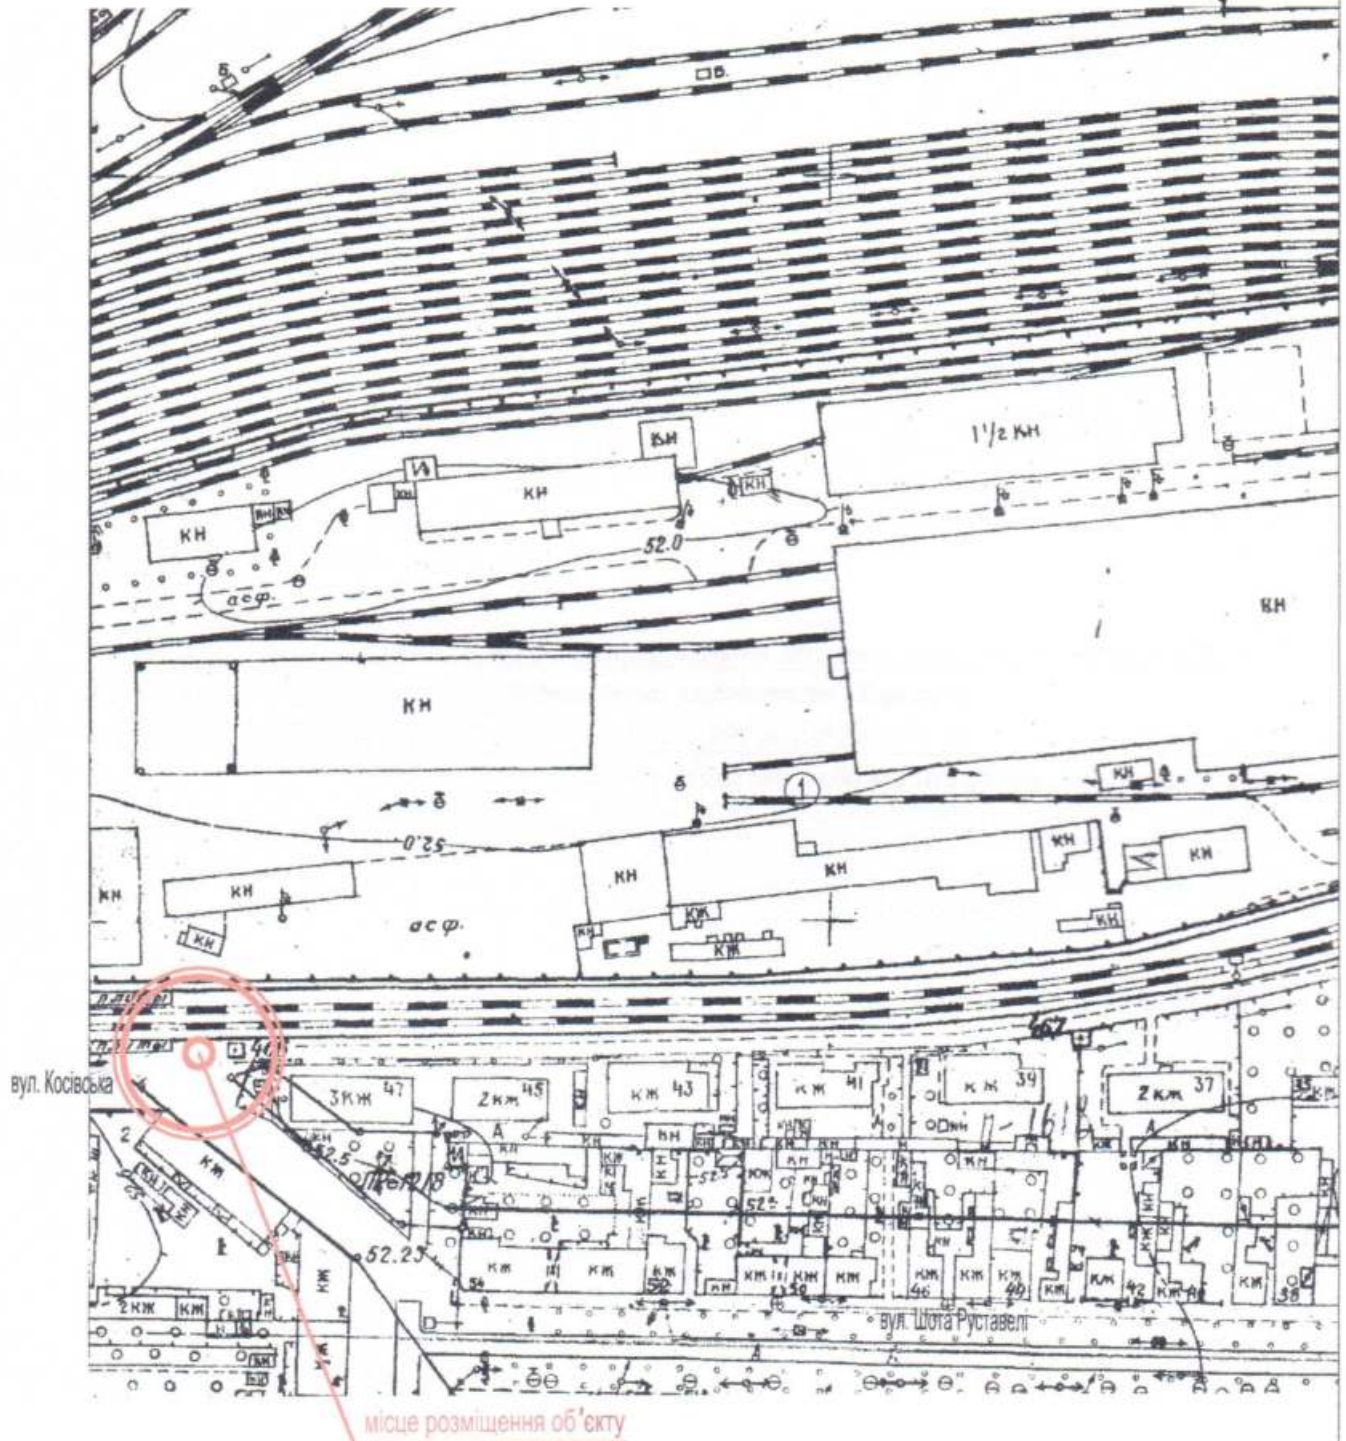

Директор ООО "Альфа"
Госліцензія АД № 030757

Архітектор



М.В. Краєвська

В.Ю. Петрушина