

СТИСЛА ПОЯСНЮВАЛЬНА ЗАПИСКА

1. Стационарна тимчасова споруда для здійснення підприємницької діяльності, яка має торговельні приміщення для тимчасового перебування людей.

Ступінь вогнестійкості — IIIa

Павільйон має прямокутну форму.

Габаритні розміри у плані — 5.00м x 4.00м

Площа забудови — 20.00м²

Площа твердого покриття — 20.00м²

Загальна площа — 18.24м²

Загальна висота — 3.00 м

Внутрішня висота складає — 2.70м.

Ґрунт заснування, до встановлення ТС, ретельно утрамбовується щебенем без улаштування фундаменту та укладається тротуарна плитка.

Стіни споруди запроектовані товщиною 100 мм із сертифікованим утеплювачем із мінеральної вати та обшивкою з обох сторін.

Обшивка сторін по каркасу: зовнішня — профільовані металеві листи, внутрішня (стіни та стеля) — пластикова вагонка.

Підлога — дерев'яні дошки 40 мм по металевому каркасу з утеплювачем з пенополістерольних плит та покриттям антипірінами та антигрибковими засобами.

Покрівля — по металевим прогонам і решетуванню з покриттям металочерепицею, з утеплювачем з мінераловатних плит.

Зовнішня обробка:

поверхні стін — профільовані металеві листи,

вікна та двері — металопластикові із вакуумними склопакетами,

покрівля — металочерепиця.

2. ТС підключається до мереж електропостачання згідно з чинними нормами та ТУ. Точка підключення згідно з ТУ.

Опалення - електричне з встановленням навісних електро-конвекторів з регулюванням температури.

Освітлення приміщення виконується світильниками з діодними лампами.

Розподільні мережі виконані проводами із мідними жилами, що прокладені у трубах та приховані в обшивці стін.

Захист мереж від дії струмів, коротких замикань та перевантажень здійснюється автоматичними вимикачами щитка. Передбачене заземлення.

3. Благоустрій прилеглої території виконується згідно з планом благоустрою, Освітлення території передбачене світильниками, що розміщуються на основному фасаді та над входом в ТС.

Директор ТОВ "Архітектурне Бюро "АРКАДІЯ"

Смаглій Д.П.

Архітектор


Кваліфікаційний сертифікат серія АА №002590

Глінін Д.Ю.




ЕСКІЗИ ФАСАДІВ ТС

Головний фасад ТС М 1:50

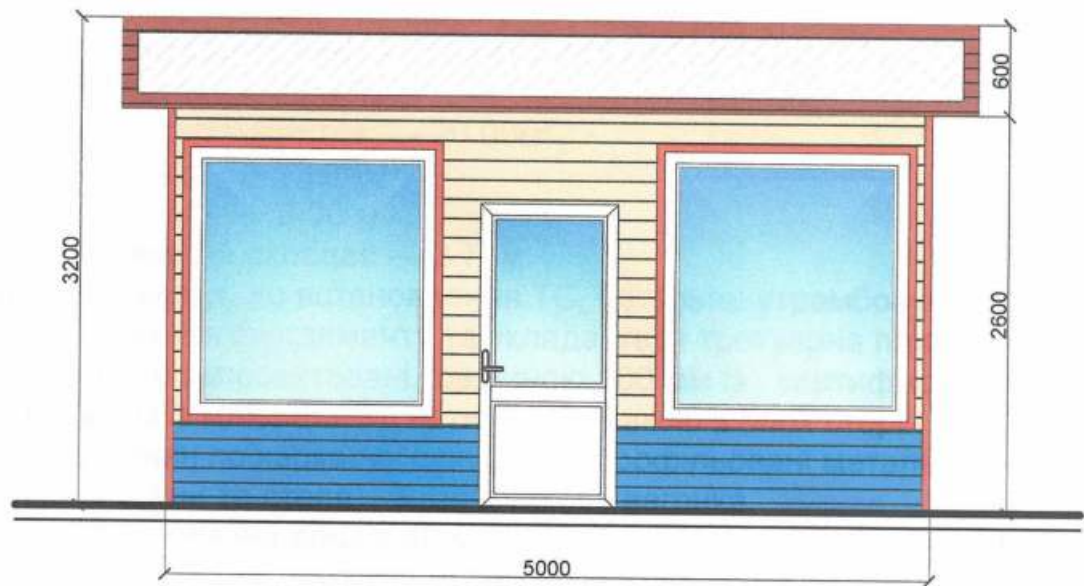

Бічний фасад ТС М 1:50

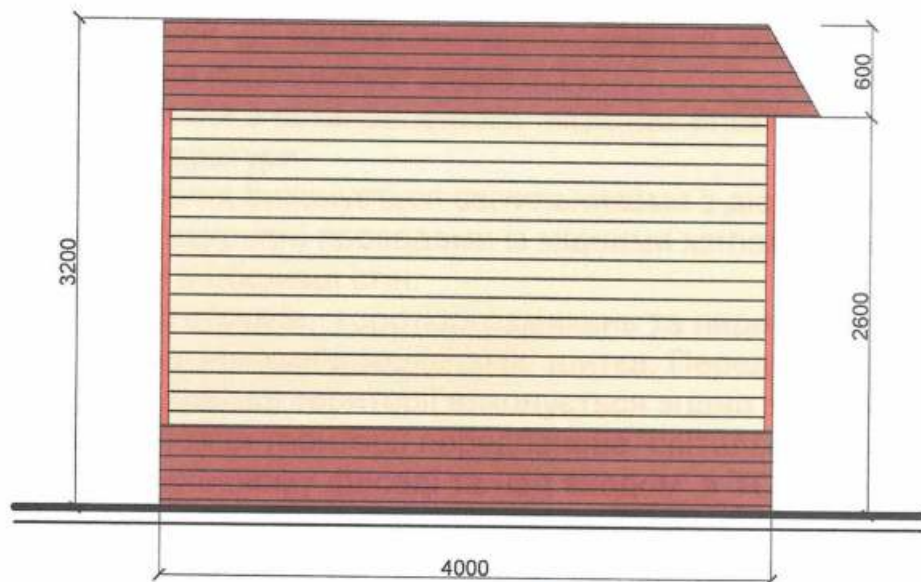

Директор ТОВ "Архітектурне Бюро "Аркадія"

Архітектор


Кваліфікаційний сертифікат серія АА №002590



Смаглій Д.П.

Глінін Д.Ю.

ПЛАН ТС М 1:50

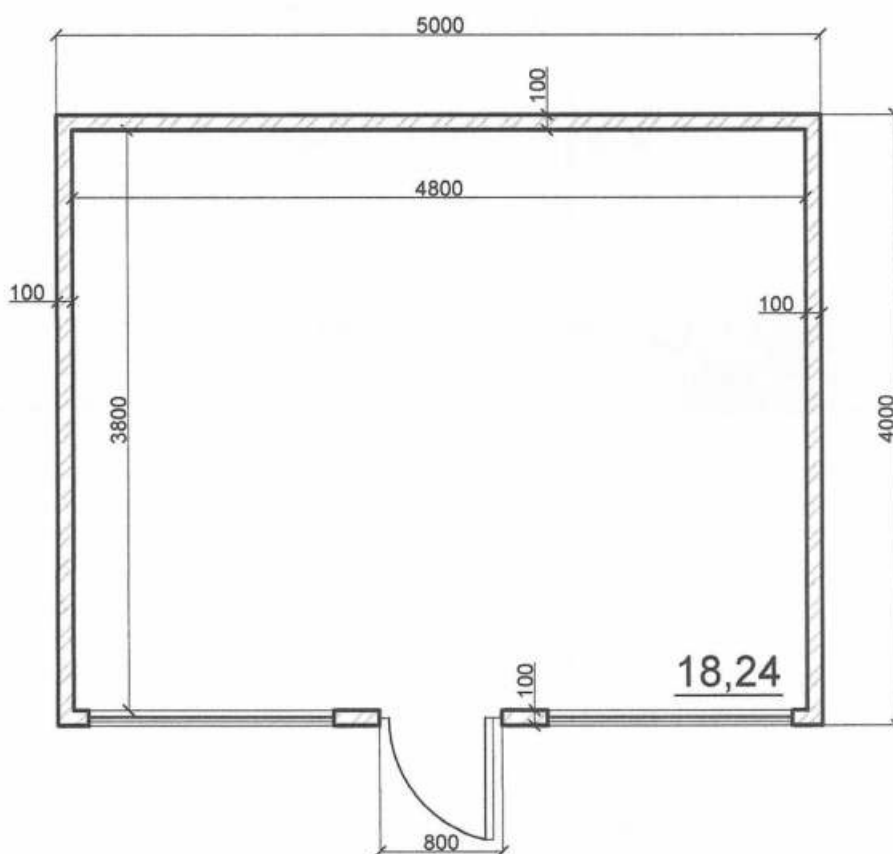

Директор ТОВ "Архітурне Бюро "Аркадія"
Архітектор



Смаглій Д.П.
Білін Д.Ю.

СХЕМА РОЗМІЩЕННЯ ТС М 1:500

Площа земельної ділянки згідно з документами на
землекористування - землі міста



Експлікація:

- 1) місце розташування ТС;
- 2) червона лінія;
- 3) регулювання забудови;
- 4) місця підключення до інженерних мереж

Умовні позначення:

- межа благоустрою ділянки розміщення ТС
- існуюча ТС
- існуючі дороги
- існуючі будівлі

Директор ТОВ "Архітектурне Бюро "Аркадія"

Архітектор

Кваліфікаційний сертифікат серія АА №002590




Смаглій Д.П.

Грін Д.Ю.

СИТУАЦІЙНИЙ ПЛАН М 1:2000

Місце розміщення об'єкту

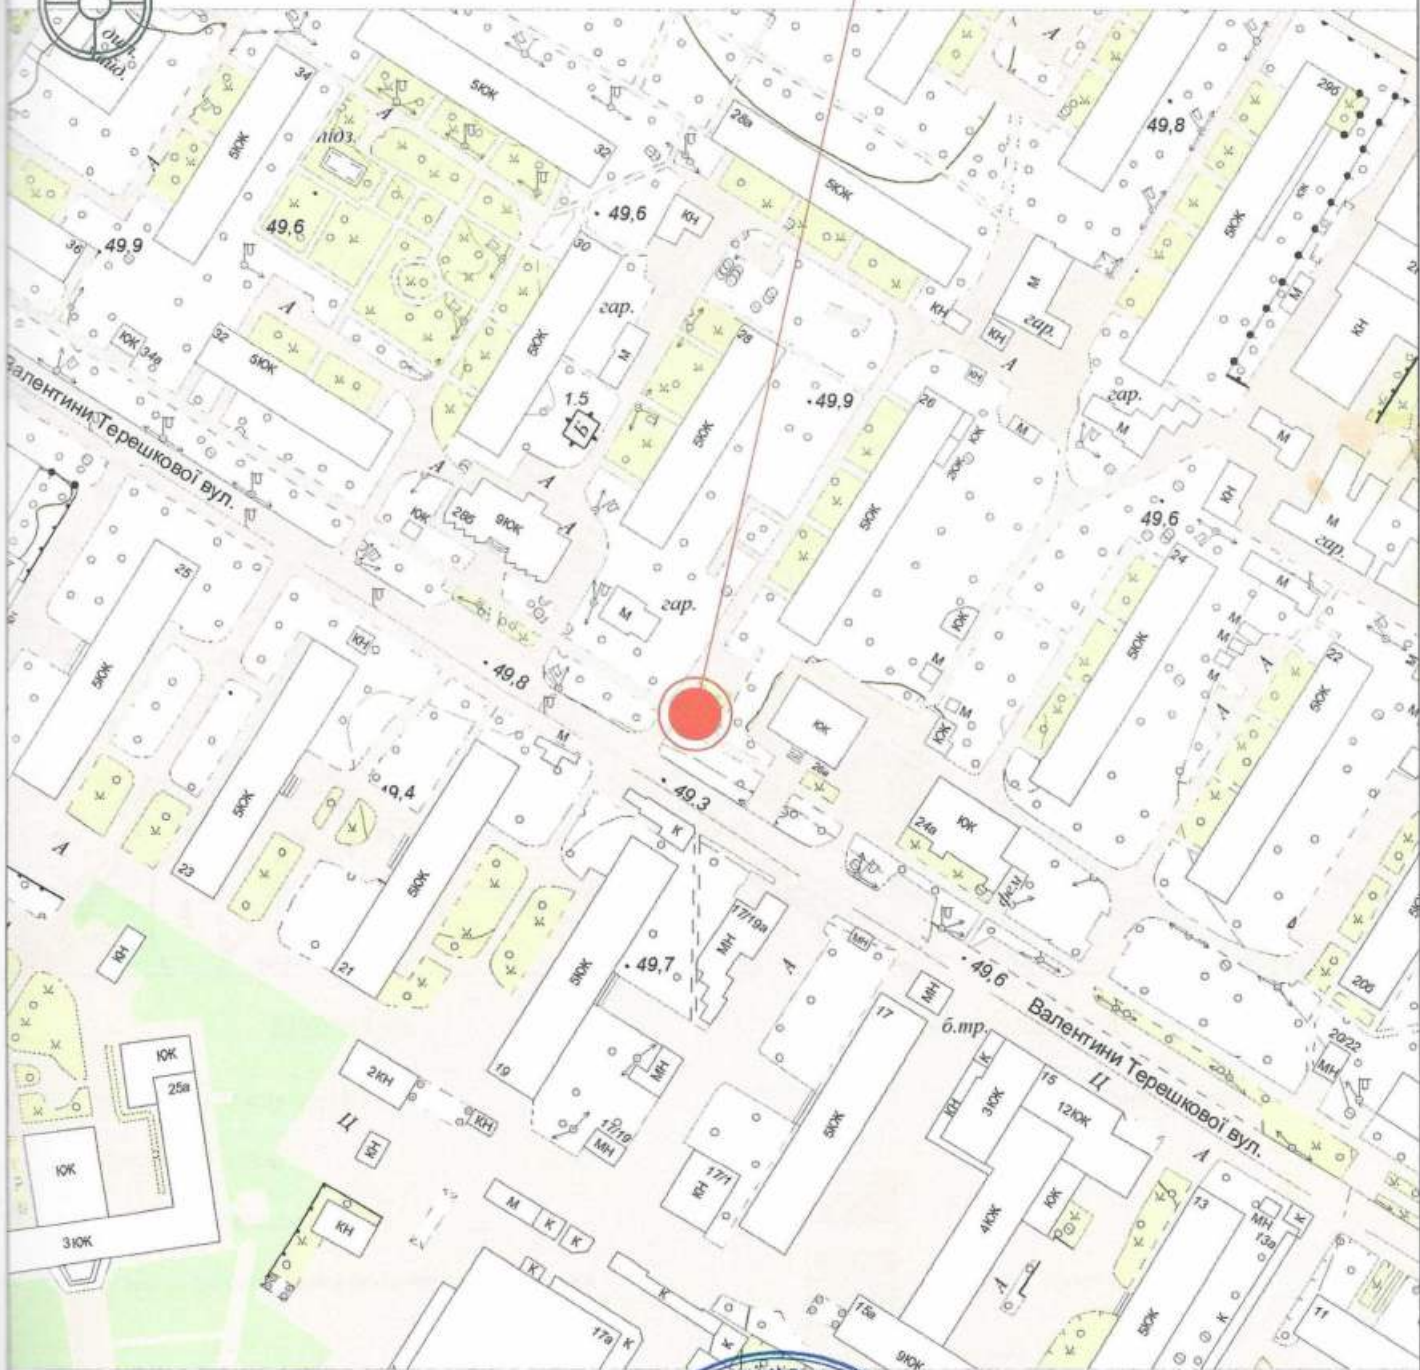

Директор ТОВ "Архітектурне Бюро "Аркадія" Маглій Д.П.
Архітектор
Кваліфікаційний сертифікат серія АА №002590

