

СТИСЛА ПОЯСНЮВАЛЬНА ЗАПИСКА

1. Тимчасова стаціонарна споруда для здійснення підприємницької діяльності, яка має торговельні приміщення для тимчасового перебування людей.
Ступінь вогнестійкості — IIIa
Павільйон має форму приблизну до прямокутної.
Габаритні розміри у плані — 4.20м x 4.10м x 0.45м x 1.45 м x 3.30м 1.45м x 0.45м x 4.10м.
Загальна площа ТС — 24.46м²
Загальна висота — 3.20 м
Внутрішня висота складає — 2.85м
Грунт заснування, до встановлення ТС, ретельно утрамбовується щебнем та укладається тротуарна плитка.
Стіни споруди запроектовані товщиною 100 мм із сертифікованим утеплювачем із мінеральної вати та обшивкою з обох сторін.
Обшивка сторін по каркасу: зовнішня - "Сендвіч" панелі.
внутрішня (стіни та стеля) — гіпсокартонні листи.
Підлога — дерев'яні дошки 40 мм по металевому каркасу з утеплювачем з мінераловатних плит та покриттям антипіринами та антигрибковими засобами.
Покрівлю — по металевим прогонам і решетуванню з покриттям металевими листами, з утеплювачем з мінераловатних плит.
Зовнішня обробка:
поверхні стін — "Сендвіч" панелі.
вікна та двері — металопластикові із вакуумними склопакетами;
покрівля — металеві листи.
2. Тимчасова споруда підключається до мереж електропостачання згідно з чинними нормами та ТУ. Точка підключення згідно з ТУ.
Опалення - електричне з встановленням навісних електро-конвекторів з регулюванням температури.
Освітлення приміщення виконується світильниками з діодними лампами.
Розподільні мережі виконані проводами із мідними жилами, що прокладені у трубах та приховані в обшивці стін.
Захист мереж від дії струмів, коротких замикань та перевантажень здійснюється автоматичними вимикачами щитка. Передбачене заземлення.
3. Благоустрій прилеглої території виконується згідно з планом благоустрою, Освітлення території передбачене світильниками, що розміщуються на основному фасаді та над входом в ТС.

Директор ТОВ "Архітектурне Бюро "АРКАДІЯ"  Смаглій Д.П.

Архітектор


Кваліфікаційний сертифікат серія АА №002590




Глінін Д.Ю.

ЕСКІЗИ ФАСАДІВ ТС

Головний фасад ТС М 1:50

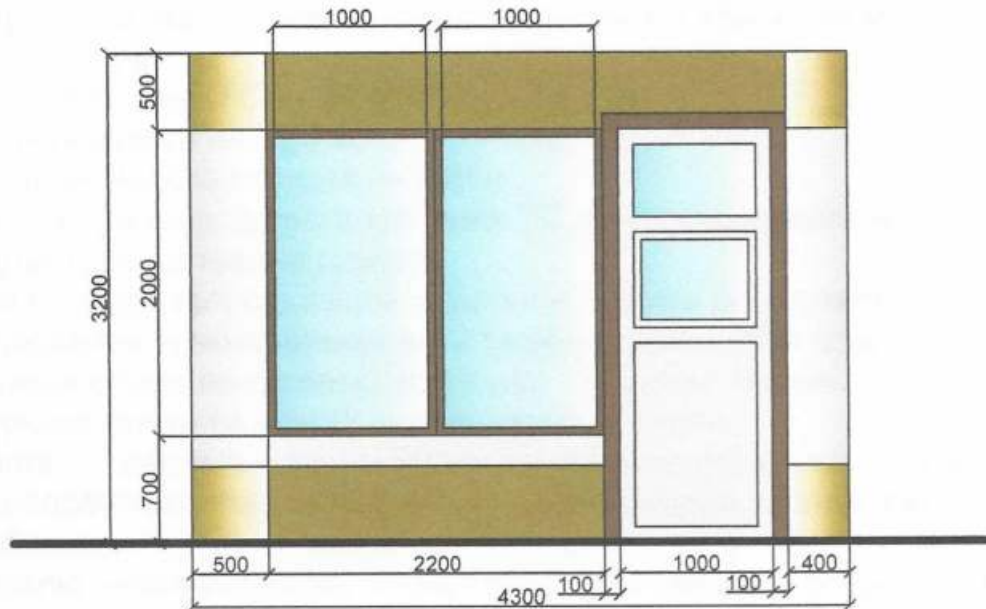

Бічний фасад ТС М 1:50

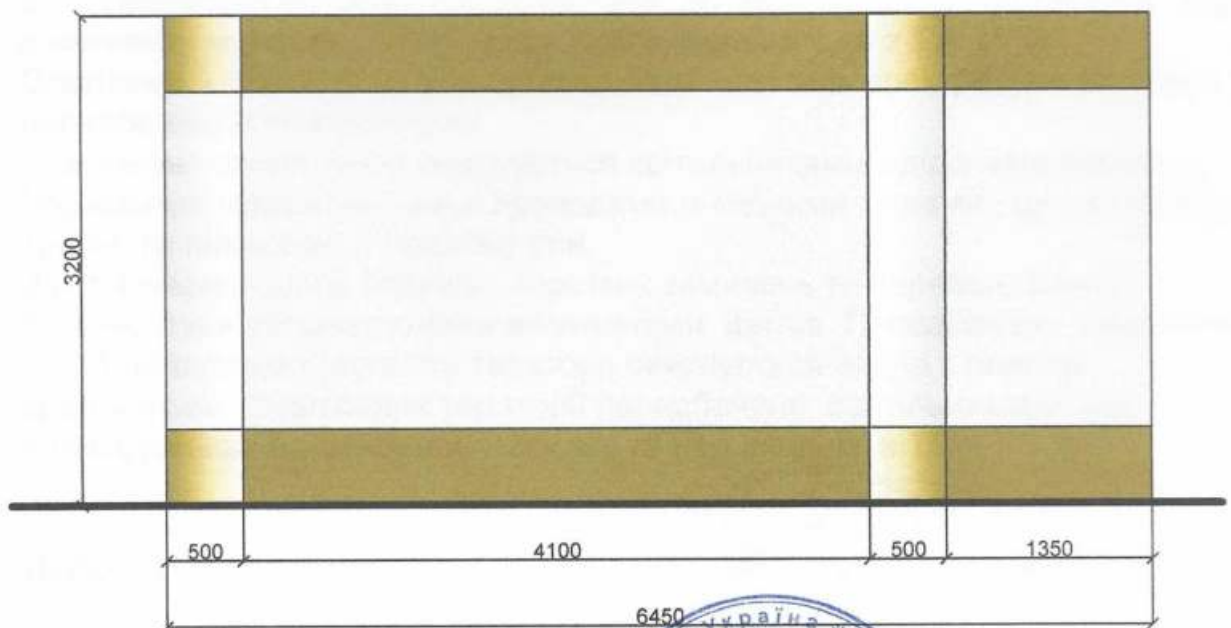

Директор ТОВ "Архітектурне Бюро "Аркадія"

Архітектор

Кваліфікаційний сертифікат серія АА №002590



Смаглій Д.П.

Білін Д.Ю.



Кваліфікаційний сертифікат серія АА №002590



Глінін Д.Ю.

СХЕМА РОЗМІЩЕННЯ ТС М 1:200

Площа земельної ділянки згідно з документами на
землекористування - землі міста



Умовні позначення:

- | | | | |
|--|------------------------------|--|--|
| | - існуючі газони | | - межа благоустрою ділянки розміщення ТС |
| | - тротуарна плитка | | - існуюча ТС |
| | - існуюче асфальтне покриття | | - існуючі будівлі |
| | - урна | | - існуючі дороги |
| | - вуличний ліхтар | | - існуючі дерева |

Директор ТОВ "Архітектурне Бюро "Архадія"

Архітектор

Кваліфікаційний сертифікат серії АА №002590




Смаглій Д.П.

Глінін Д.Ю.

СИТУАЦІЙНИЙ ПЛАН М 1:2000

Місце розміщення об'єкту

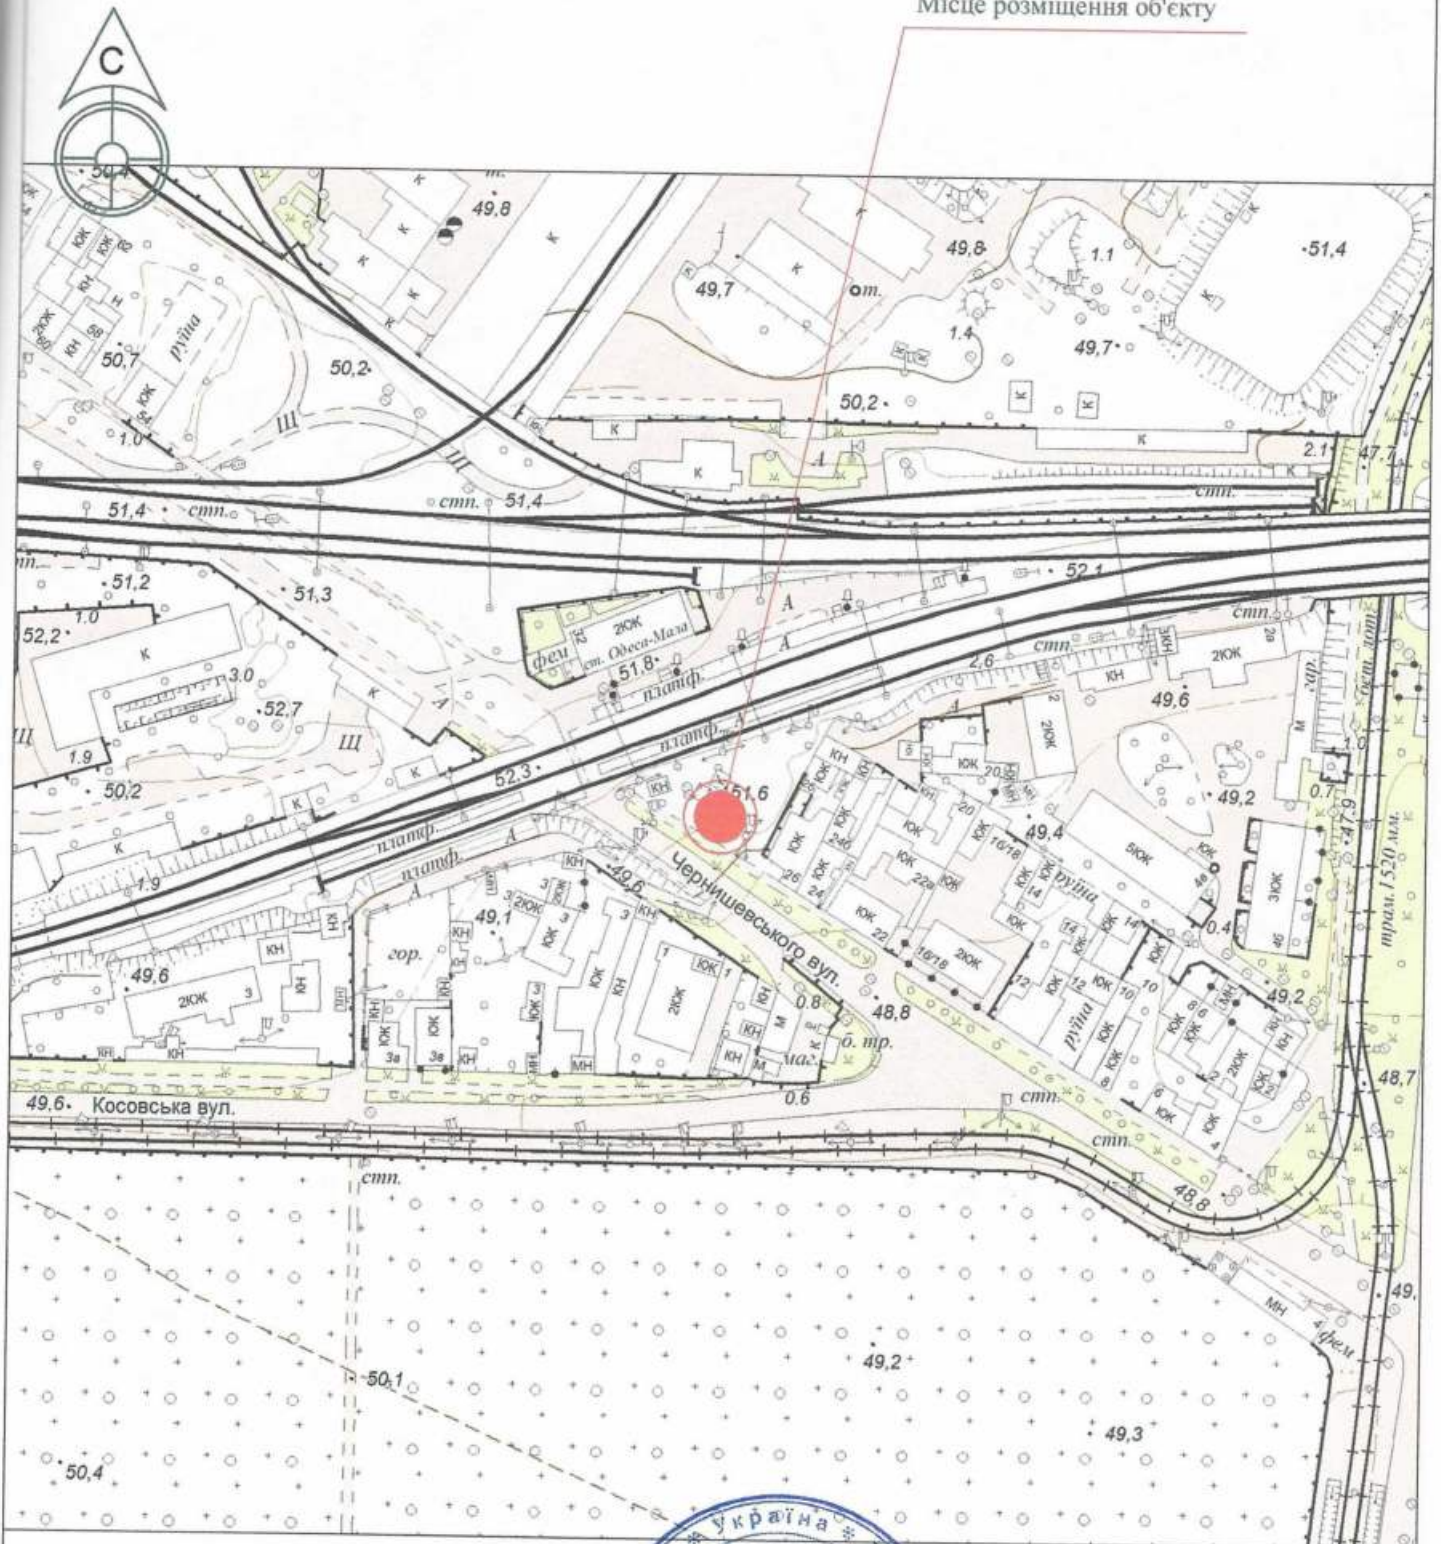

Директор ТОВ "Архітектурне Бюро "Аркадія"

Архітектор

Кваліфікаційний сертифікат серія АА №002590



Маглій Д.П.

Мінін Д.Ю.