

ПОЯСНЮВАЛЬНА ЗАПИСКА

1. Група тимчасових споруд (ТС) для здійснення підприємницької діяльності має закриті приміщення для тимчасового перебування людей.
За умовну позначку 0.000 прийнятий рівень чистої підлоги ТС.
Ступінь вогнестійкості - Ша. Кількість споруд - 2шт.
Габаритні розміри стаціонарних тимчасових споруд в плані -
1 - 6.05м х 4.25м. Площа ТС - 25.71м²;
2 - 3.40м х 4.25м. Площа ТС - 14.45м².
Площа забудови групи ТС - 40.20м².
У павільйонах розташовані приміщення, загальною площею - 35.99м².
Внутрішня висота групи ТС від рівня чистої підлоги складає - 2.50м.
Загальна висота групи ТС - 3.20м.
Грунт заснування, до встановлення групи ТС, ретельно утрамбован щебнем та покладен асфальтобетон. Група ТС встановлена без улаштування фундаментів.
Стіни споруд запроектовані по типу «Сендвич», товщиною 100мм із утеплювачем з мінеральної вати та обшивкою з обох сторін.
Обшивка стін по каркасу: зовнішня - кольорові алюмінієві композитні панелі, внутрішня (стіни й стеля) - пластикова вагонка.
Підлога - дерев'яні дошки 40мм по металевому каркасу з утеплювачем із мінераловатних плит та покриттям з негорючого матеріалу.
Покрівля - по металевим прогонам і решетуванню з покриттям із профільованого сталевих листа, з утеплювачем із мінераловатних плит, гідро- і пароізоляцією.

Зовнішня обробка.

поверхні стін - кольорові алюмінієві композитні панелі;
вікна - відсутні;
двері - металопластикові;
покрівля - металевий профнастил;
козирок - кольорові алюмінієві композитні панелі.

2. Група ТС підключається до мереж електропостачання згідно з діючими нормами та ТУ. Точка підключення - близька опора, що розташована поряд з територією ділянки, згідно з ТУ.
Опалювання - електричне з встановленням навісних електро-конвекторів з регулюванням температури.
Освітлення приміщення виконується стельовими світильниками з люмінесцентними лампами.
Розподільні мережі павільйонів, виконані проводами з мідними жилами, що прокладені у трубах та приховані в обшивці стін. Мережі обрані по тривалодопустимим струмам навантаження.
Захист мереж від дії струмів коротких замикань і перевантаження здійснюється автоматичними вимикачами щитка.
3. Благоустрій прилеглої території виконується згідно з планом благоустрою.
Освітлення території передбачене світильниками, що розташовані під козирками ТС.

ГАП
Кваліфікаційний сертифікат серія АА №000199

Архітектор


Дата складання "22" 03. 2019 року



Ігнатова Л.А.

Чабан Л.В.

Головний фасад

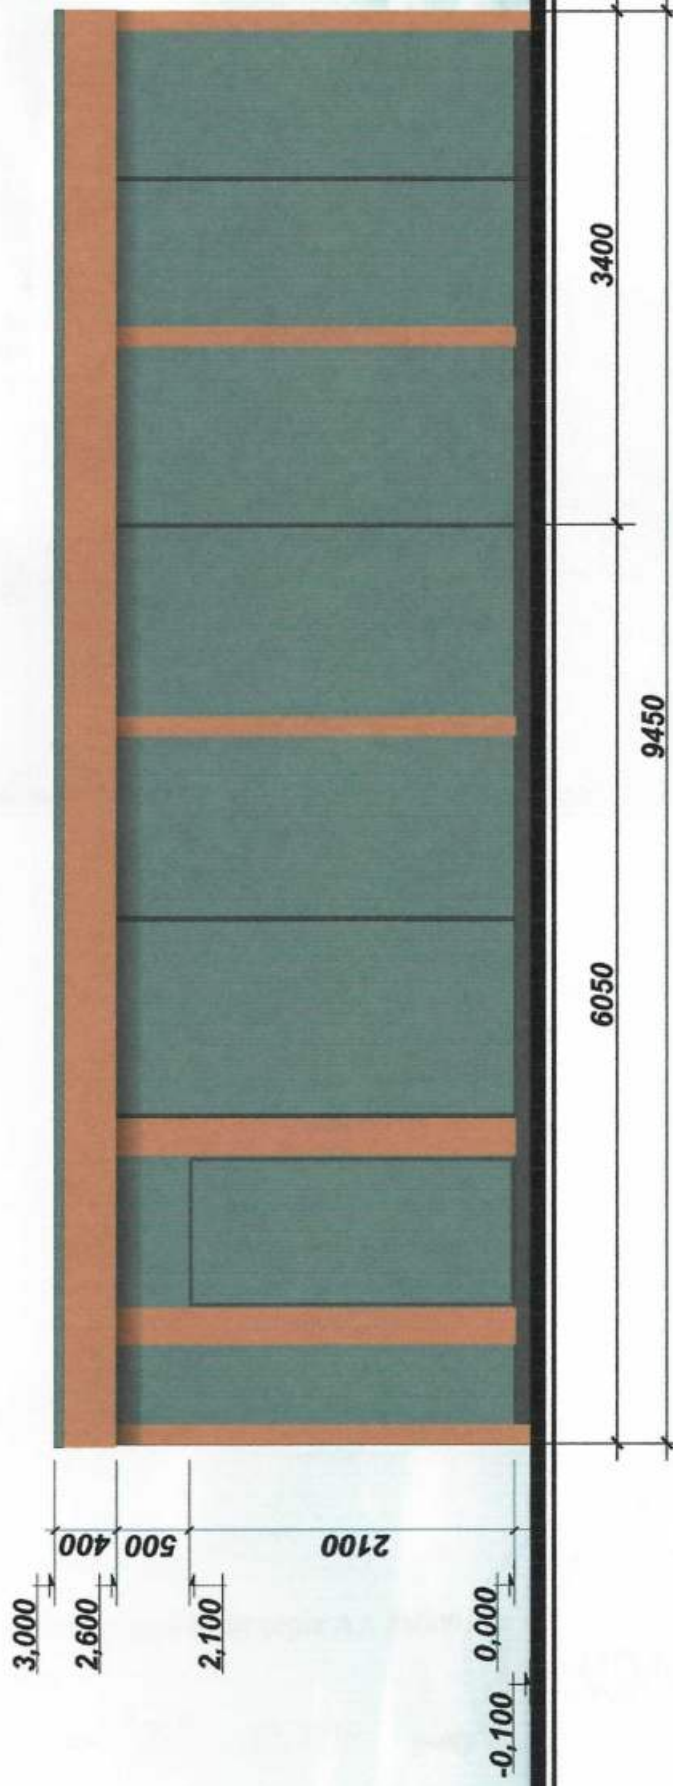

Ігнатова Л.А.


Чабан Л.В.

ГАП
Кваліфікаційний сертифікат серія АА №000199

Архітектор

Дата складання " 22 " 03. 2019 року

Бічний фасад

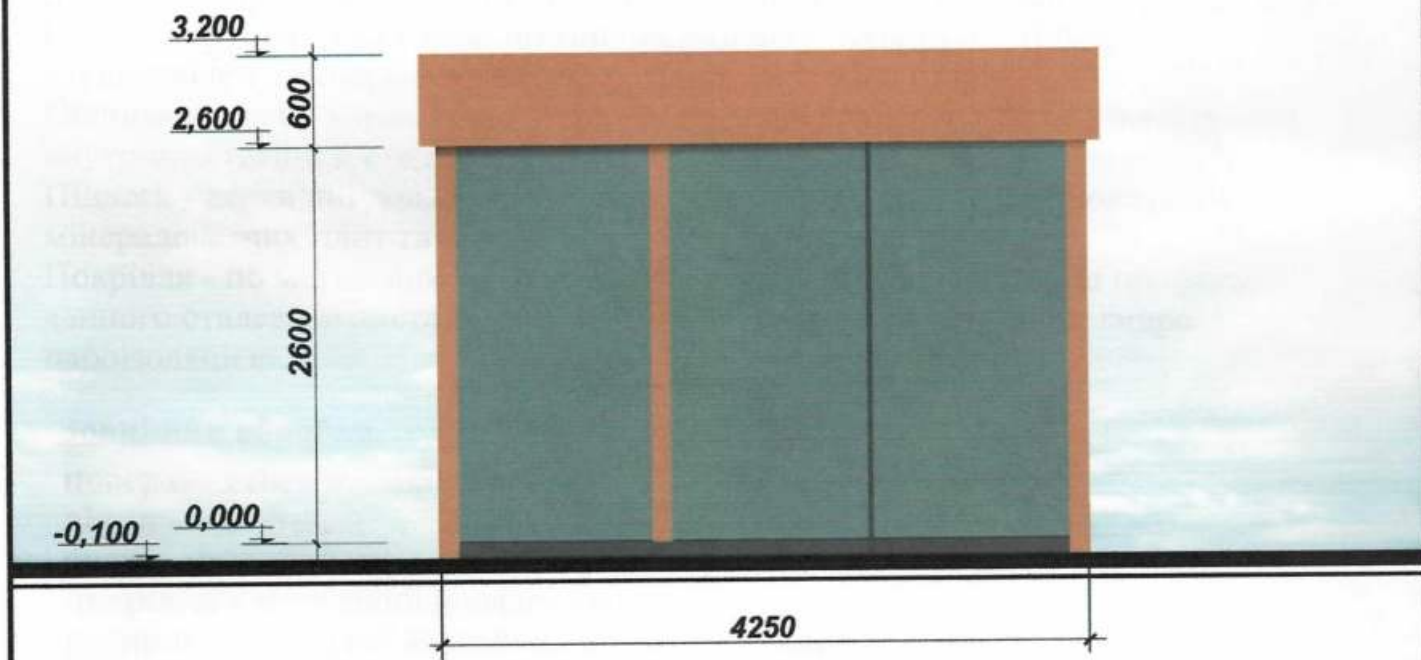

ГАП
Кваліфікаційний сертифікат серія АА №000199


Архітектор

Дата складання "22" 03. 2019 року

Ігнатова Л.А.

Чабан Л.В.



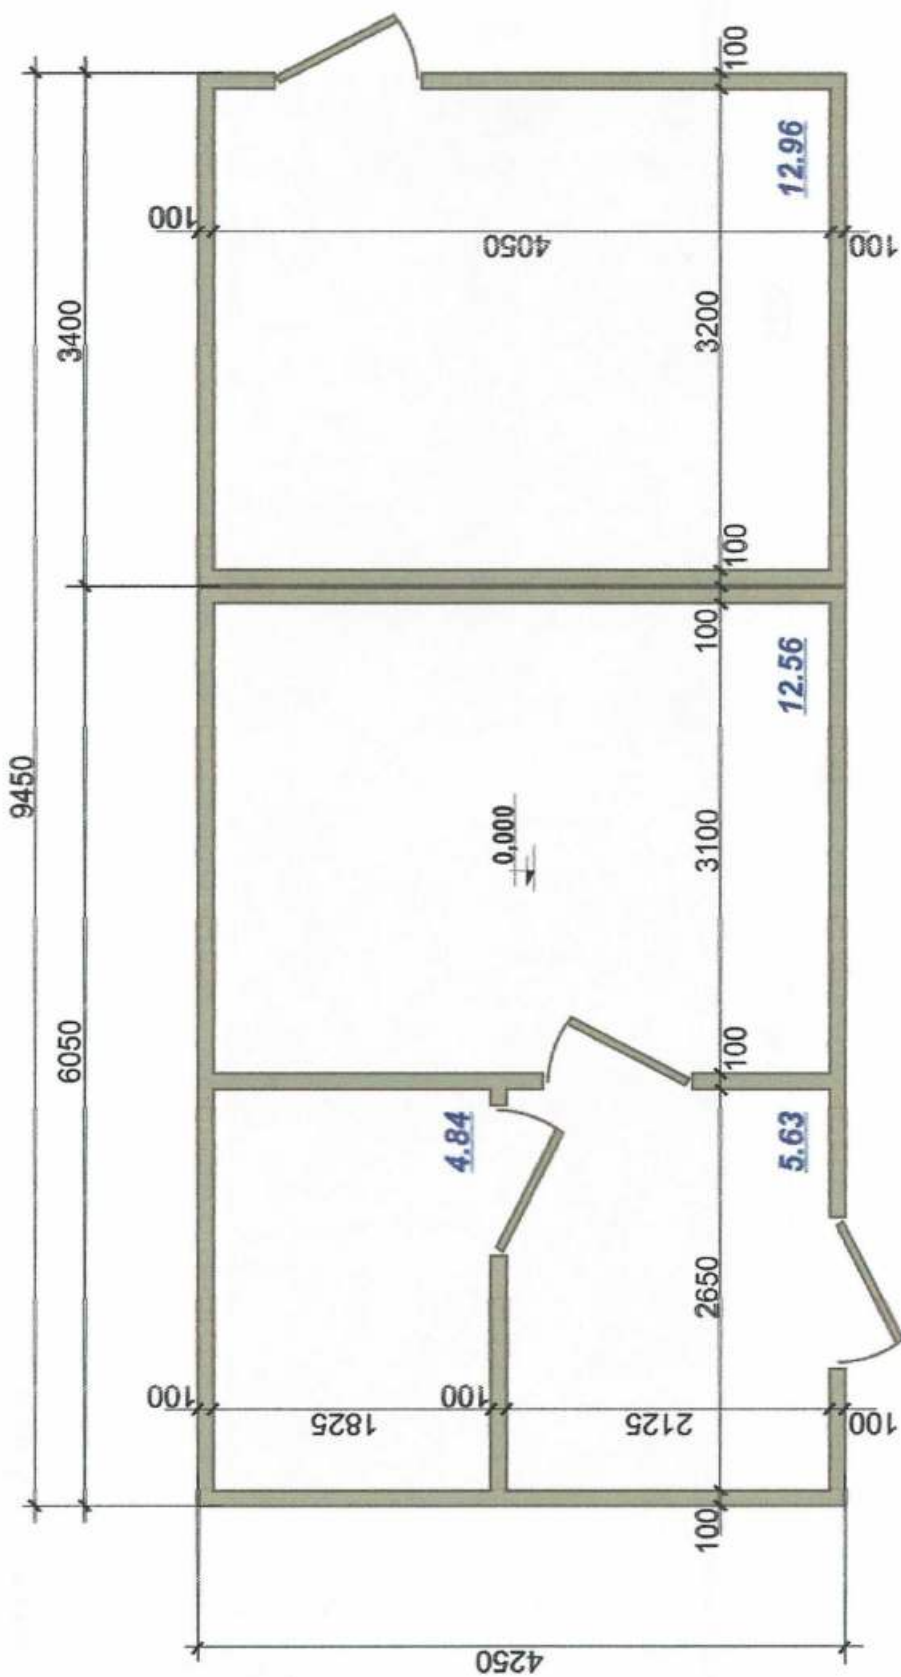

Ігнатова Л.А.

Чабан Л.В.


ГАП
Кваліфікаційний сертифікат серія АА №000199

Архітектор

Дата складання " 22 " 03, 2019 року

СХЕМА РОЗМІЩЕННЯ ТС М 1:500


Площа земельної ділянки згідно з документами на землекористування
Город земель фонд земля м.Одеси

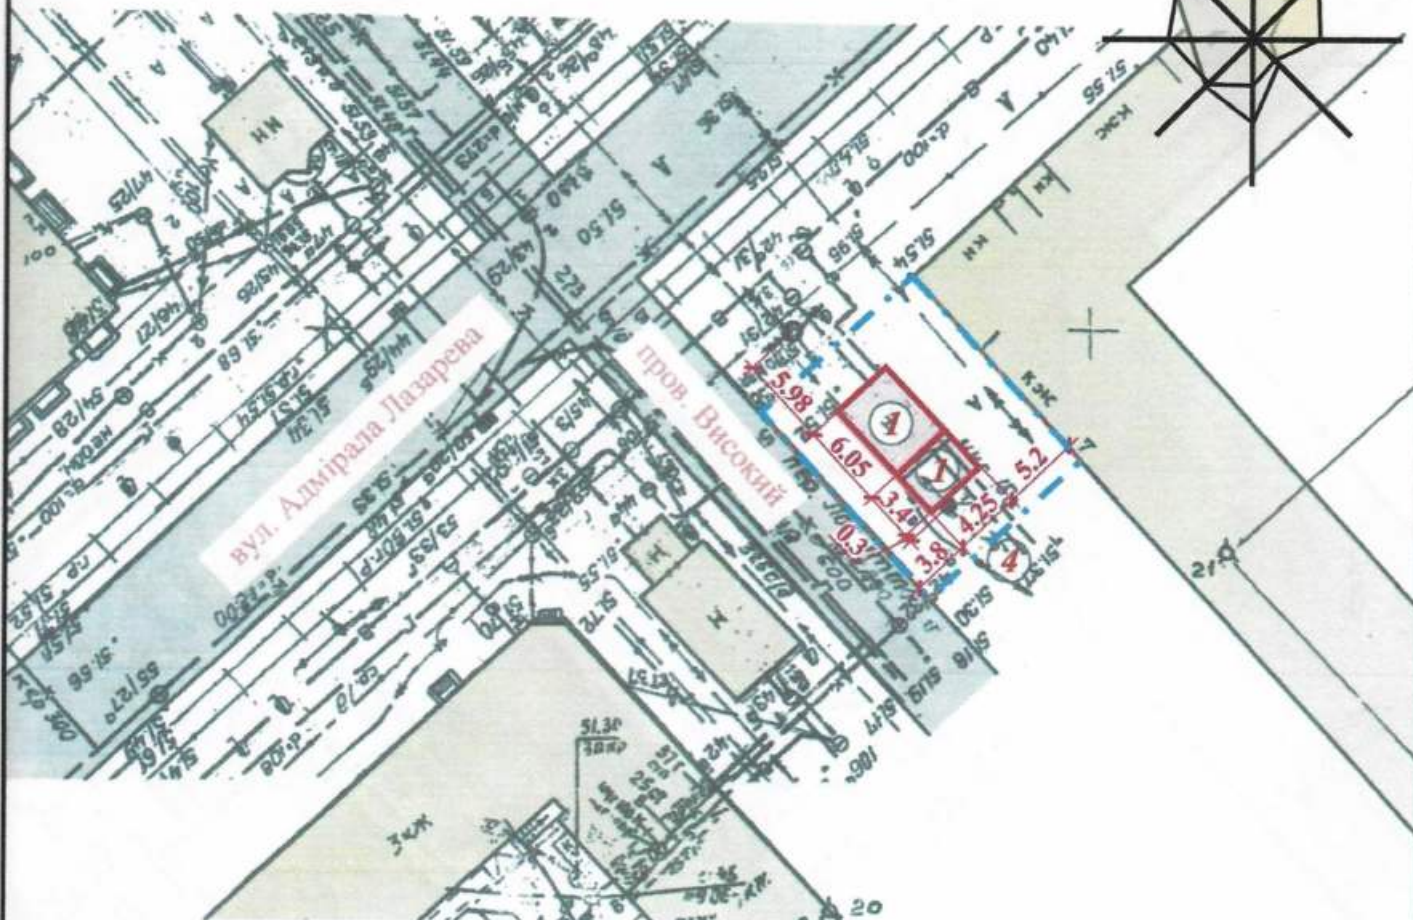

Умовні позначення:

Експлікація:

- 1) місце розташування ТС;
- 2) лінії регулювання забудови;
- 3) червоні лінії;
- 4) місця підключення до інженерних мереж.

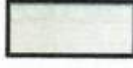-  - межа благоустрою ділянки розміщення ТС
-  - проектна група ТС
-  - існуючі будівлі
-  - існуючі дороги
-  - підключення до мереж електропостачання

ГАП
Кваліфікаційний сертифікат серія АА №000199

Архітектор


Дата складання "22" 03. 2019 року

Ігнатова Л.А.

Чабан Л.В.



СИТУАЦІЙНИЙ ПЛАН, М 1:2000

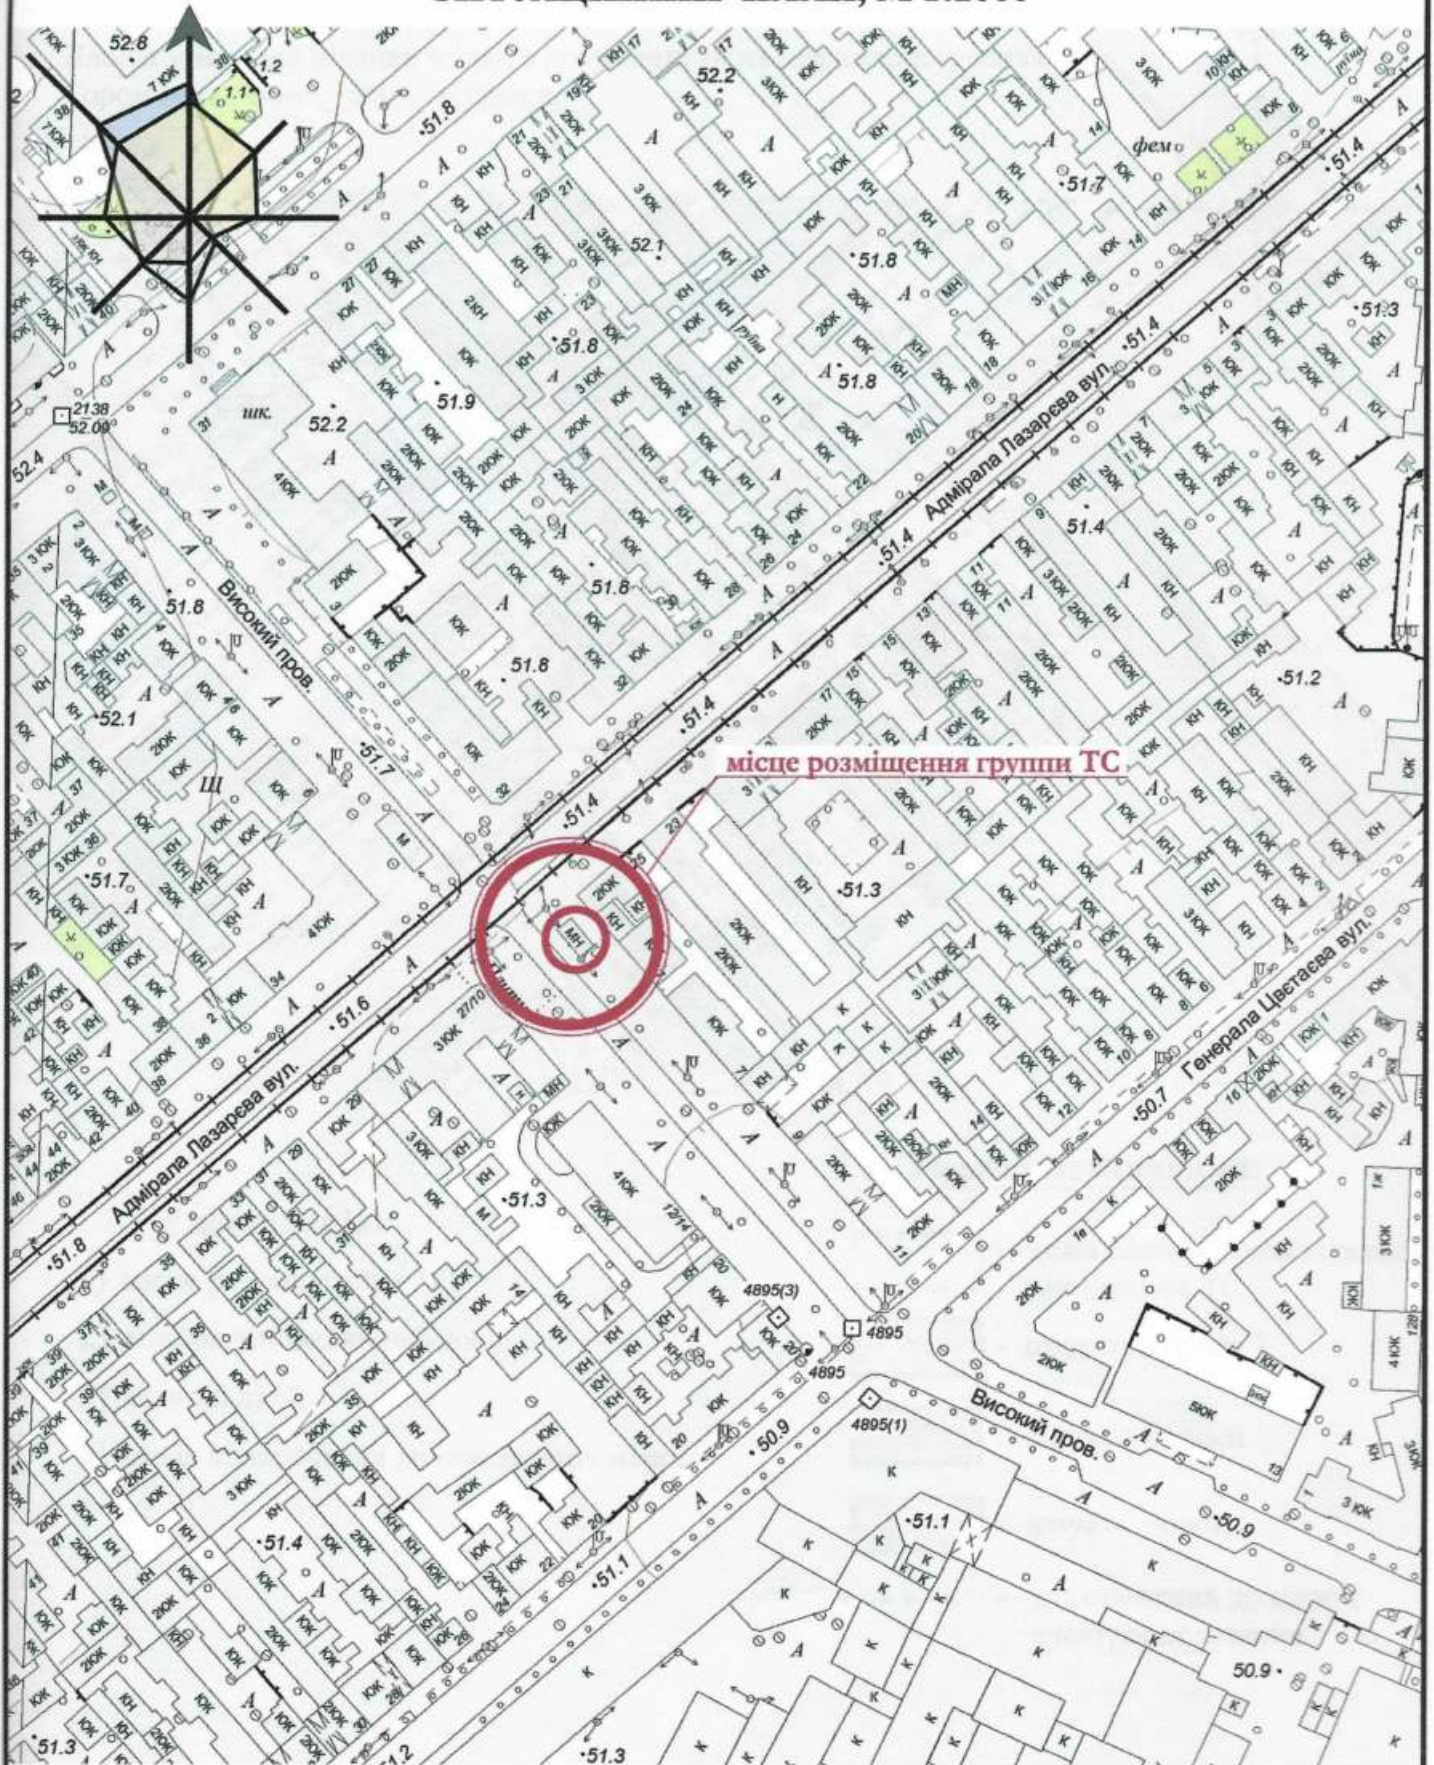

ГАП

Кваліфікаційний сертифікат серія АА №000199

Архітектор

Дата складання "22" 03. 2019 року



Ігнатова Л.А.

Чабан Л.В.