

ПОЯСНЮВАЛЬНА ЗАПИСКА

1. Тимчасова споруда (ТС) для здійснення підприємницької діяльності має торговельне приміщення для тимчасового перебування людей.

За умовну позначку ± 0.000 прийнятий рівень чистої підлоги ТС.

Ступень вогнестійкості - III

Габаритні розміри в плані ТС - 2.50 м. x 3.30 м. ;

У павільоні розташоване приміщення площею - 7.13 кв.м.

Внутрішня висота павільйону від рівня чистої підлоги складає - 2.40м.

Загальна висота павільйону складає - 3.15 м.

Ґрунт заснування , до встановлення павільйону, ретельно утрамбован щебнем та укладання тротуарна плитка.

Тимчасова споруда запроектована по типу "Марсель"-цільносварний металевий каркас зроблений із профільної труби.

Обшивка стін по каркасу: зовнішня - металеві профільовані листи; внутрішня (стіни та стеля) - пластикова вагонка.

Підлога - цільносварний металевий каркас + дерев ный каркас, доска сосна 40 мм,

ДСП, лінолеум;.

Покрівля - кровельний профнастил.

Зовнішня обробка:

поверхні стін - колірний металевий профіль;

вікна - металопластикові;

двері - металопластикові;

покрівля - кровельний профнастил;

цоколь - колірний поліуритановий профіль.

2. Тимчасова споруда підключена до мереж електропостачання згідно з діючими нормами та ТУ. Точка підключення - близька опора, що розташована поряд з територією ділянки.

Опалювання-електричне з встановленням навісних електро-конвекторів з регулюванням температури.

Освітлення приміщення виконане стельовими світильниками з люмінесцентними лампами.

Розподільні мережі павільйонів , виконані проводами з мідними жилами , що прокладені у трубах то приховані в обшивці стін. Мережі обрані по тривалодопустимим струмам навантаження .

Захист мереж від дії струмів коротких замикань та перевантажень здійснюється автоматичними вимикачами щитка.

3. Благоустрії прилеглої території виконується згідно з планом благоустрою. Освітлення території передбачене світильниками, що розміщуються на головному фасаді над входом у ТС.

Директор ООО "Альфа"


Госліцензія АД № 030757

Архітектор




ЕСКІЗИ ФАСАДІВ ТС, М 1:50

Фасад в осях "1" - "2"

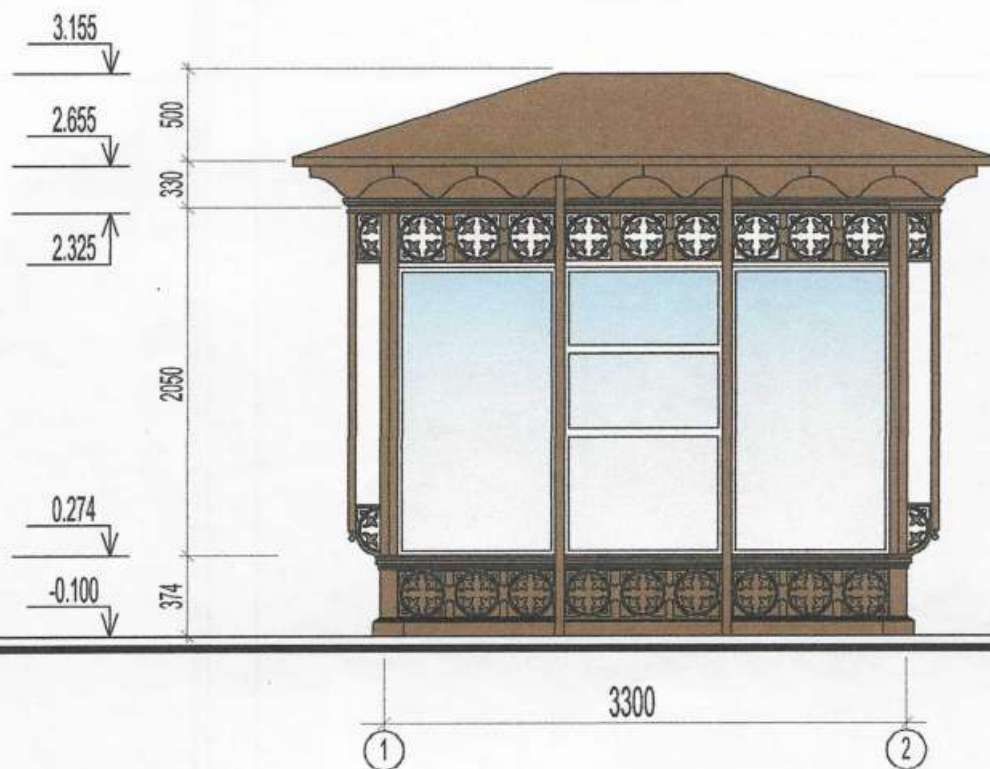

Фасад в осях "А" - "Б"

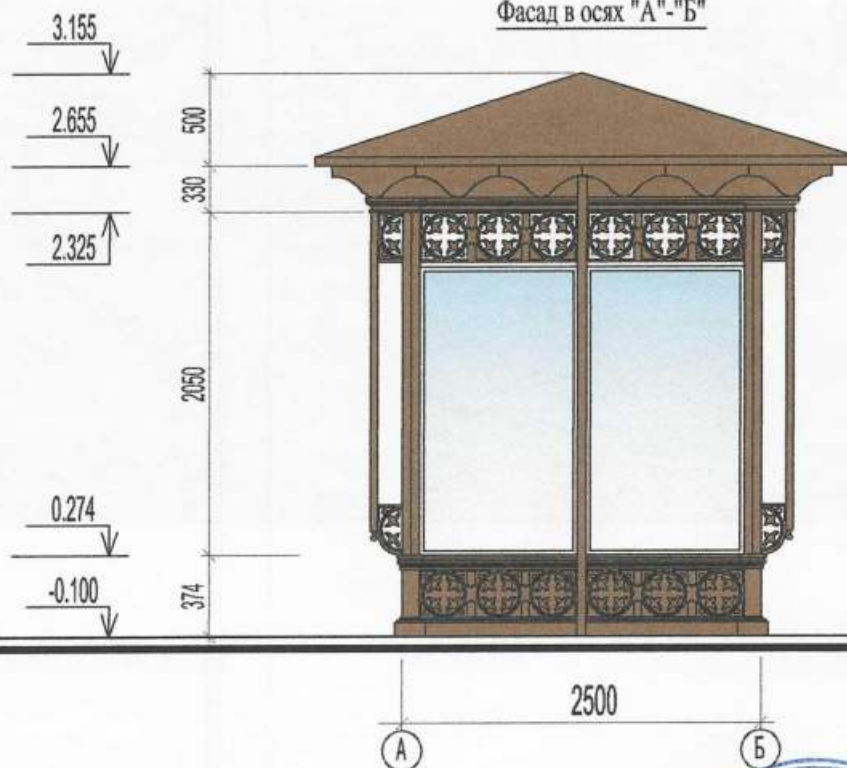


Директор ООО "Альфа"
Гослицензия АД № 030757

Архітектор



План на отг. 0.000, М 1:50

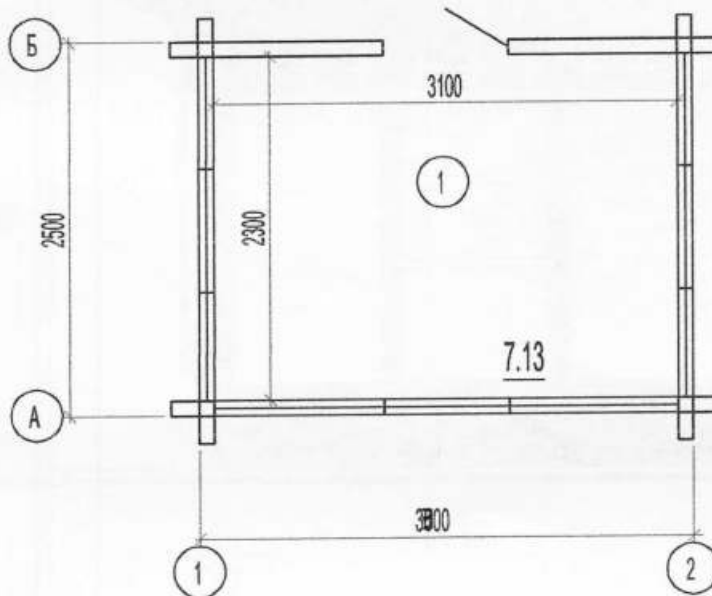

Єксплікація

№/№ по плану	Найменування	Площа м2
1	Тимчасова споруда	7.13
	Загальна площа	7.13
	Площа забудови	8.25


Директор ООО "Альфа"
Госліцензія АД № 030757

Архітектор



СХЕМА РОЗМІЩЕННЯ ТС, М 1:500

Площа земельної ділянки згідно з документами
на землекористування - землі міста.

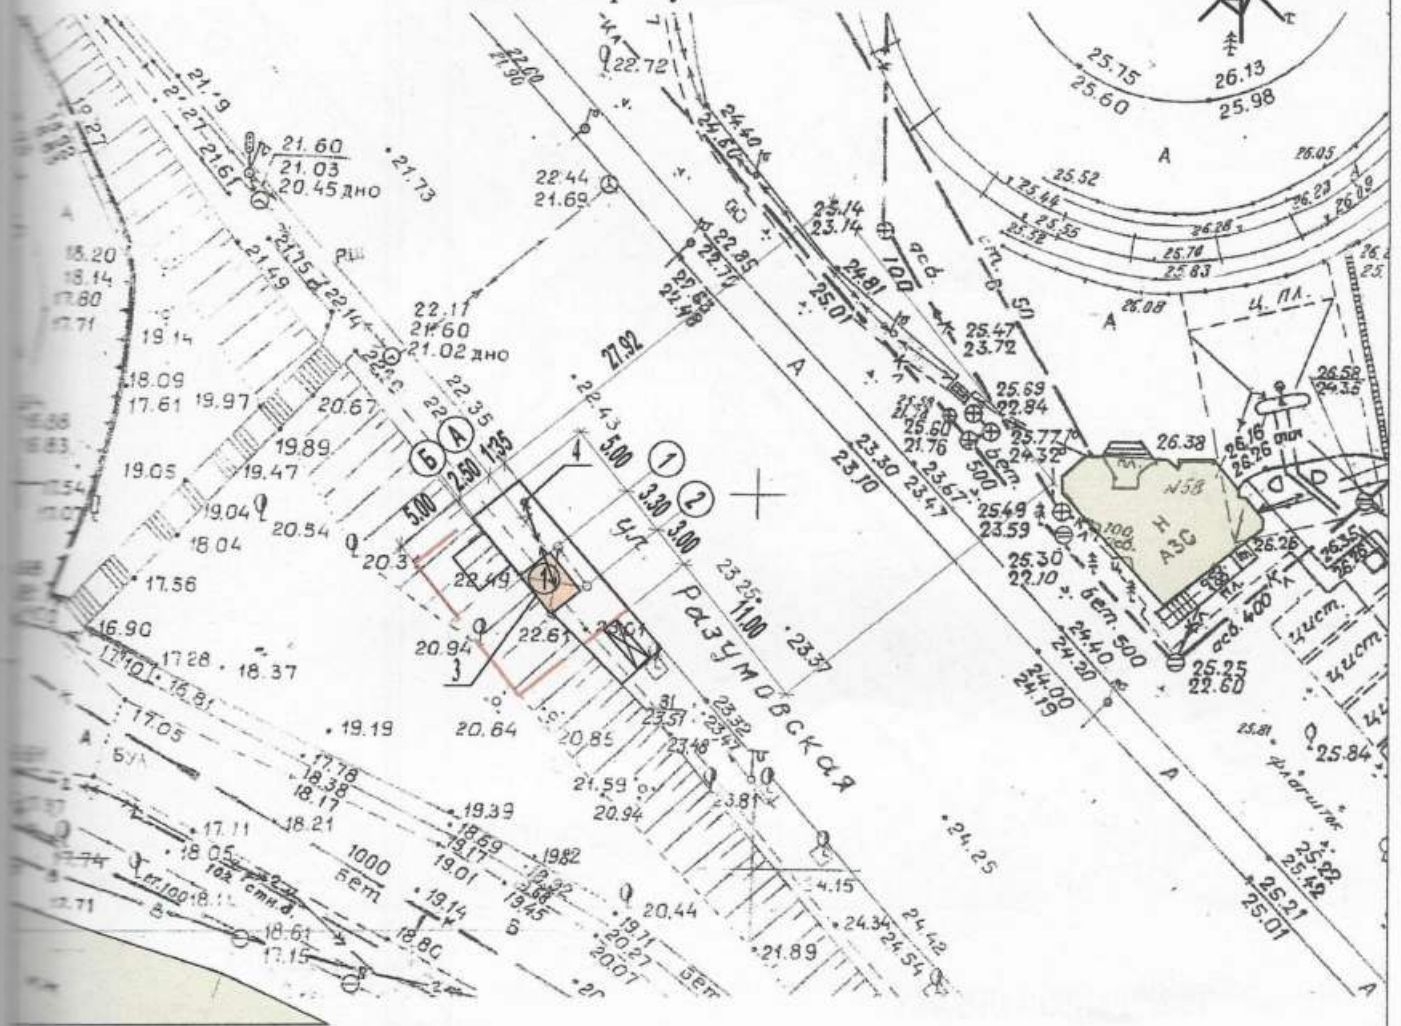

Експлікація:

- 1 місце розташування ТС;
- 2 червоні лінії;
- 3 лінії регулювання забудови;
- 4 місця підключення до інженерних мереж;

Умовні позначення:

- межа благоустрою ділянки розміщення ТС
- проектна ТС
- існуючі будівлі
- підключення до мереж електропостачання

Директор ООО "Альфа"
Госпідприємств АД № 030757


Архітектор



М.В.Краєвська

В.Ю.Петрушина

Ситуаційний план, М 1:2000

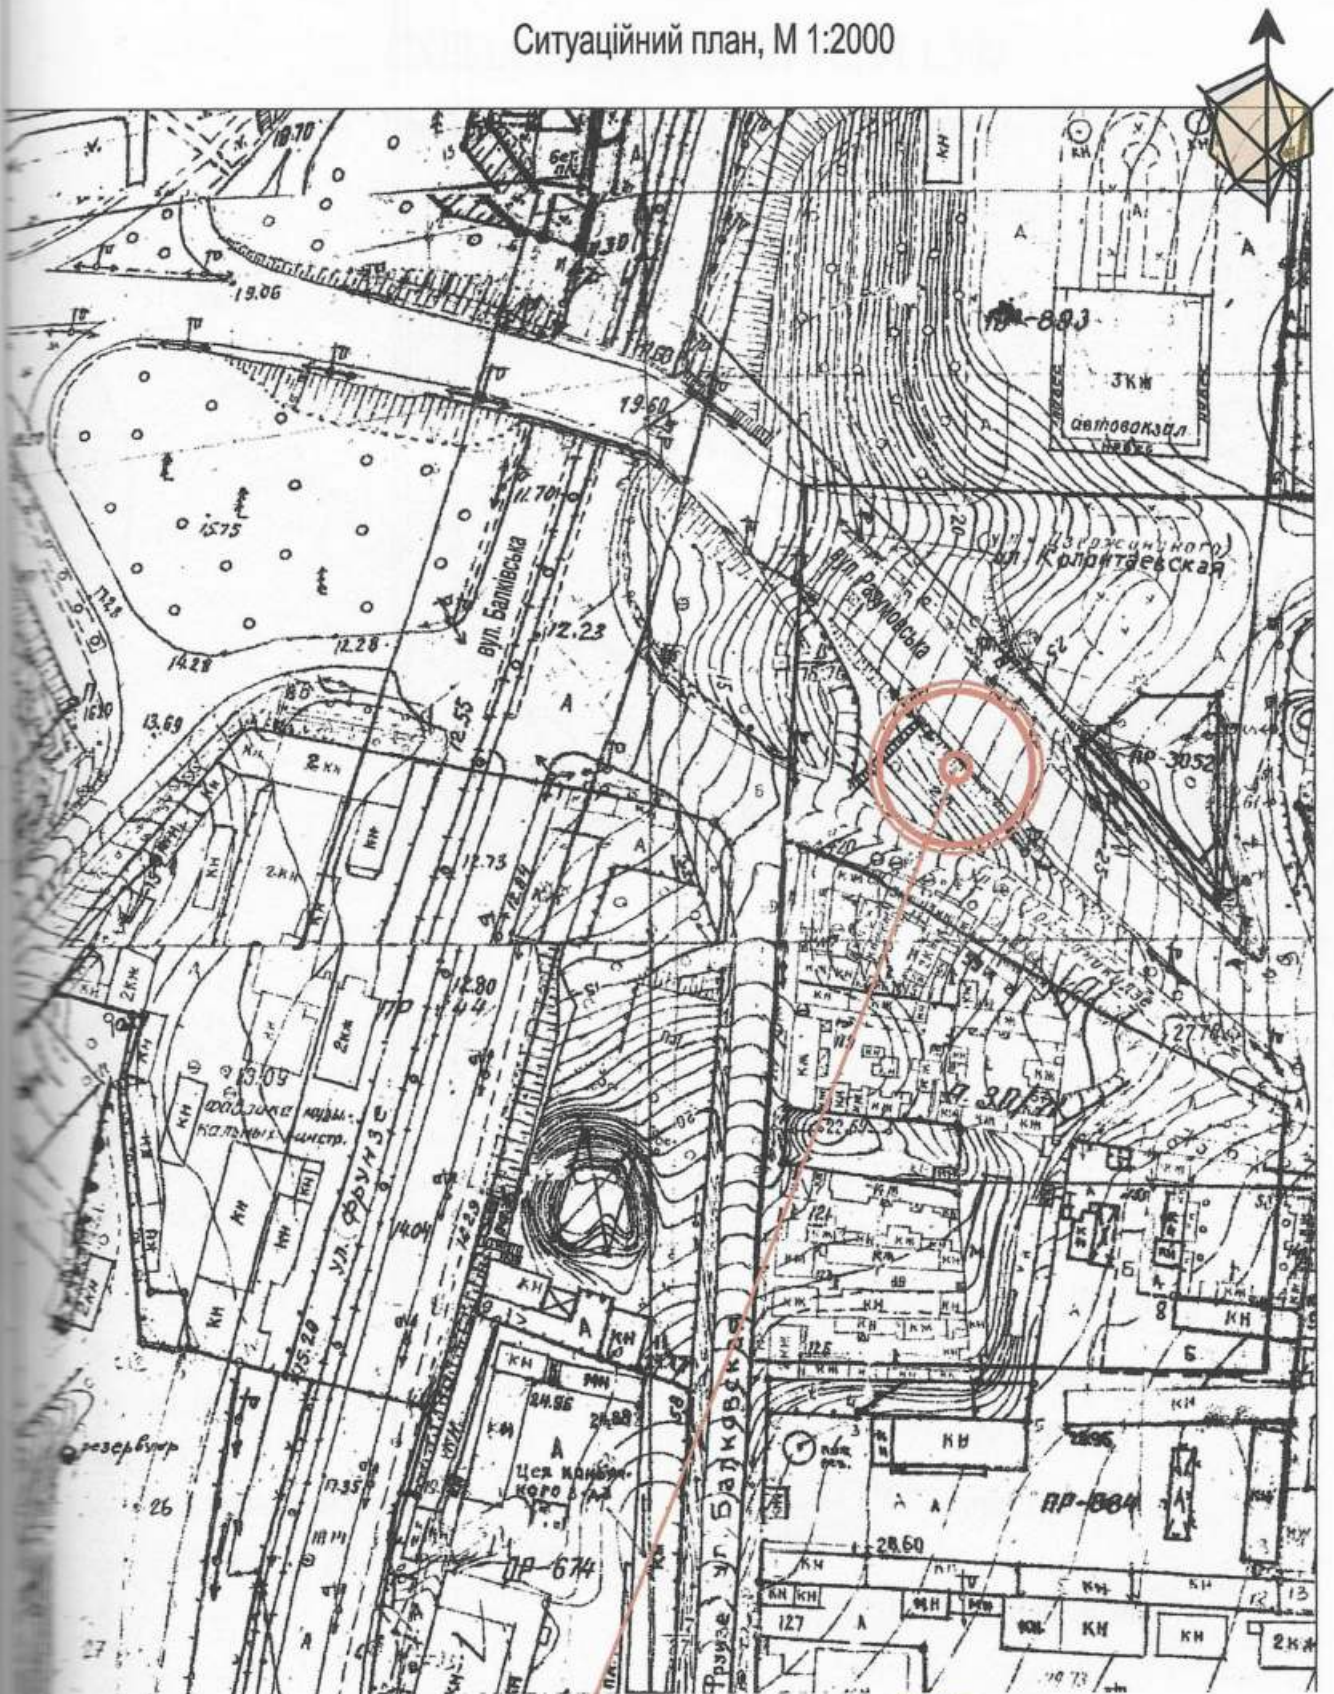

місце розміщення ТС

Директор ООО "Альфа"

Гослицензія АД № 030757

Архітектор



М.В. Краєвська

В.Ю. Петрушина