

ПОЯСНЮВАЛЬНА ЗАПИСКА

1. Група стаціонарних тимчасових споруд для здійснення підприємницької діяльності має торгівельні приміщення для тимчасового перебування людей.

Ступінь вогнестійкості - III а.

Стаціонарних тимчасових споруд - 2 шт.

Габаритні розміри у плані

1- 2,45 м X 5,7 м.

2- 4,2 м X 5,7 м.

Площа забудови - 40,71 м²

Загальна площа - 37,91 м²

Площа твердого покриття - 40,71 м²

Загальна висота - 3,00 м

Внутрішня висота складає - 2,60 м

Грунт заснування, до встановлення ТС, ретельно утрамбовується щебенем такладається бетонна тротуарна плитка.

Стіни групи споруд запроектовані товщиною 100 мм із сертифікованим утеплювачем із мінеральної вати та обшивкою з обох сторін.

Обшивка стін по каркасу: зовнішня - композитні матеріали типу Алюкобонд; внутрішня стіни й стеля) - пластикова вагонка.

Підлога - дерев'яні дошки 40 мм по металевому каркасу з утеплювачем пенополістерольних плит та покриттям з негорючого матеріалу.

Заповнення прорізів з метало пластикового профілю та рольгратами.

Окрівля - по металевих прогонах і решетуванню з покриттям із профільованного сталевих листа, з утеплювачем з мінераловатних плит, гідро- і пароізоляцією.

Водостік передбачити зовнішній організований по жолобах і ринвам.

Зовнішня обробка:

Зовнішні стін - композитні матеріали типу Алюкобонд;

Вікна - металопластикові;

Двері - металопластикові;

Окрівля - профільований сталевий лист;

Колірне вирішення фасадів дивись графічний додаток.

Внутрішню обробку виконати згідно індивідуального дизайну-проекту із застосуванням негорючих оздоблювальних матеріалів, з підтвердженням сертифікатом.

2. Підключення до інженерних мереж:- тимчасова споруда підключається до існуючої електромережі, згідно договору про постачання електричної енергії.

Опалювання - електричне з встановленням навісних електро - конвекторів з регулюванням температури.

Освітлення приміщення виконане стельовими світильниками з люмінесцентними лампами.

Архітектор


Кваліфікаційний сертифікат, серія АА № 002057




Давидова В.В.

ЕСКІЗИ ФАСАДІВ ТС М 1:50

Фасад в осях 1-2

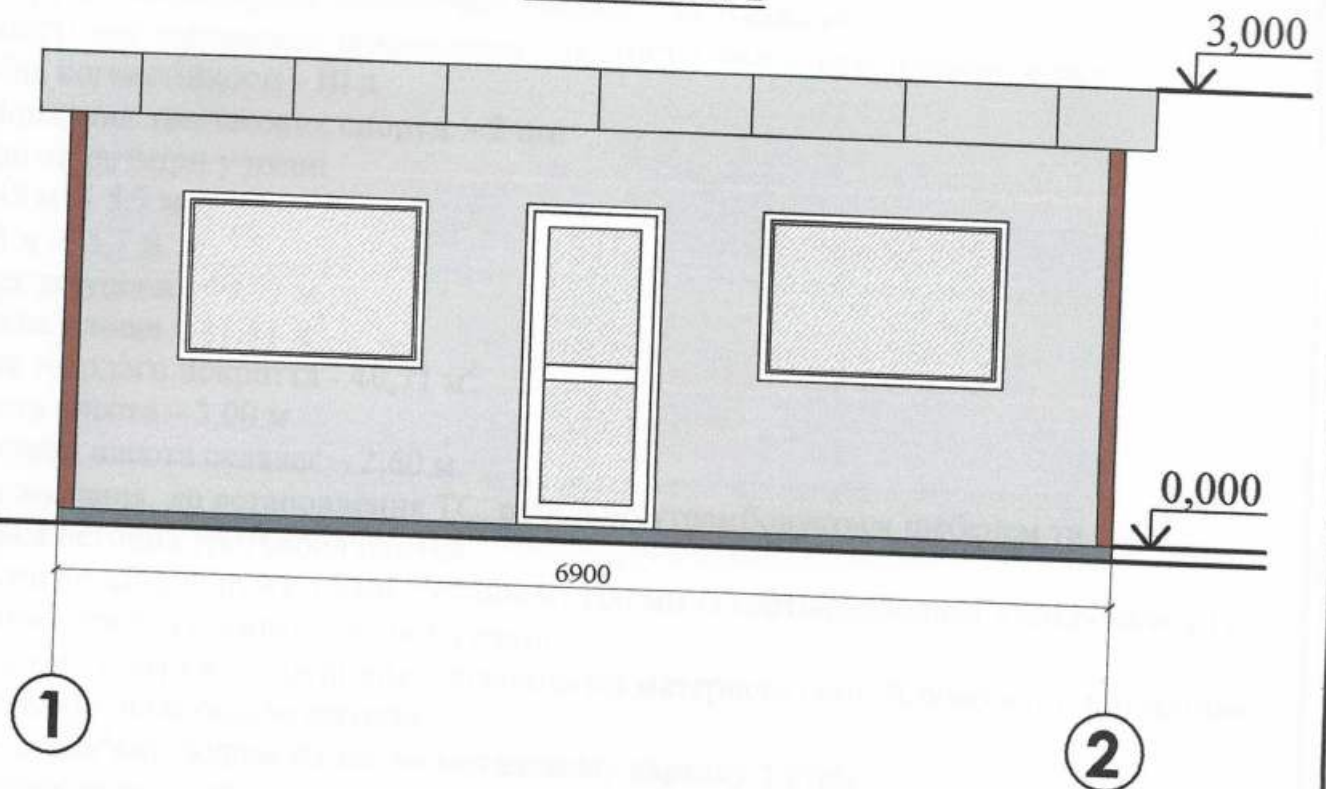

Фасад в осях А-Б

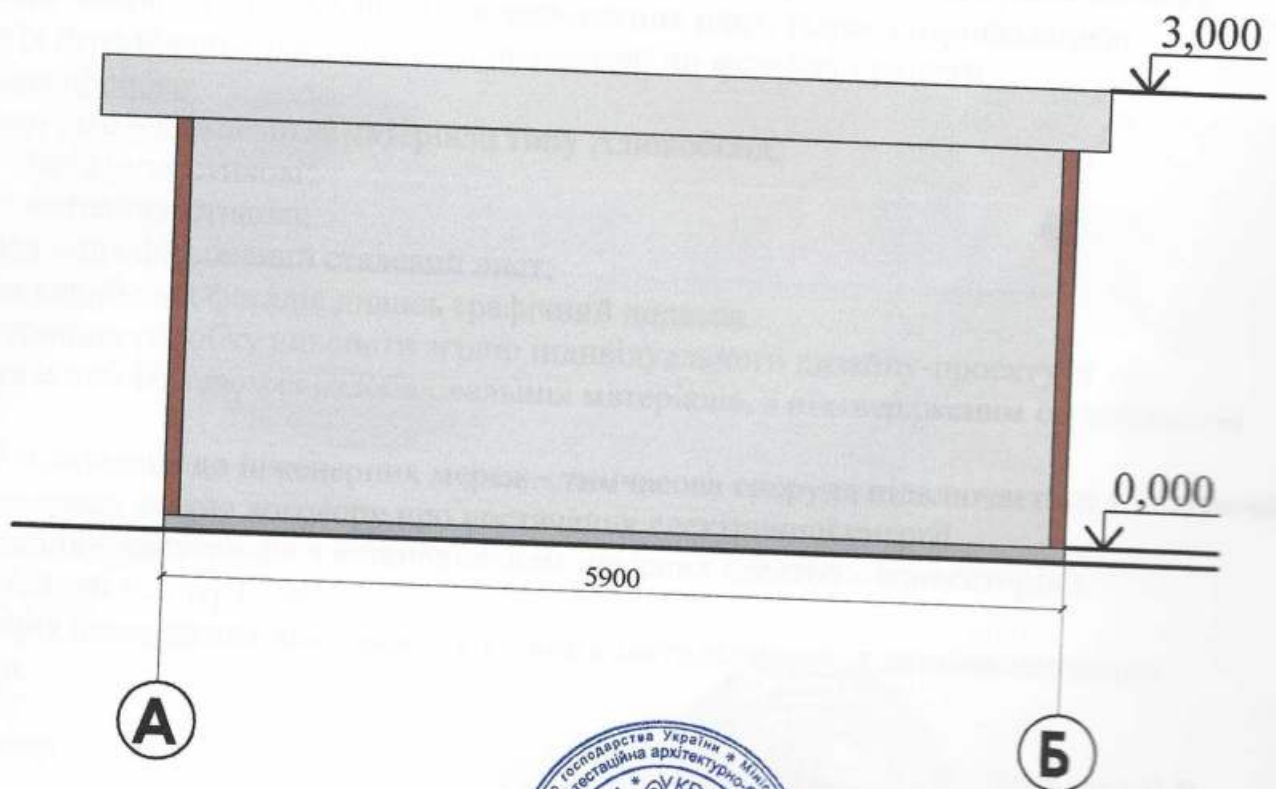


Архітектор

Кваліфікаційний сертифікат, серія АА № 00204



Давидова В.В.

ПЛАН ТС М 1:50

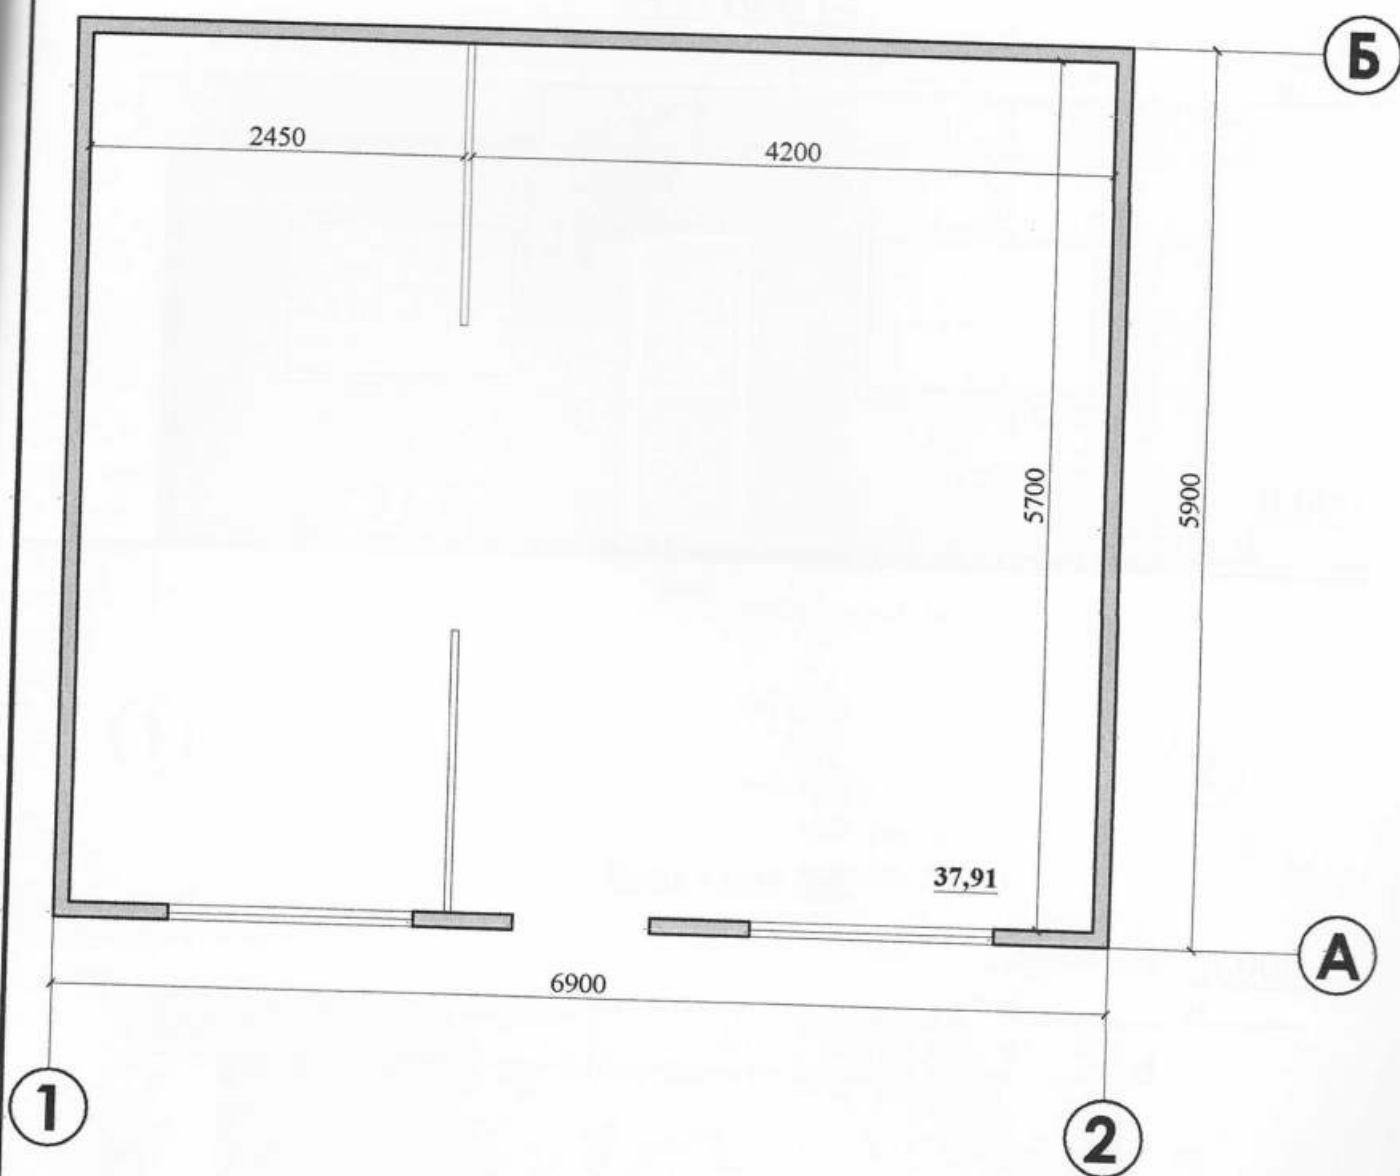

Архітектор


Кваліфікаційний сертифікат, серія АА № 002057



Давидова В.В.

СХЕМА РОЗМІЩЕННЯ ТС М 1:500

Площа земельної ділянки згідно з документами на землекористування - землі міста

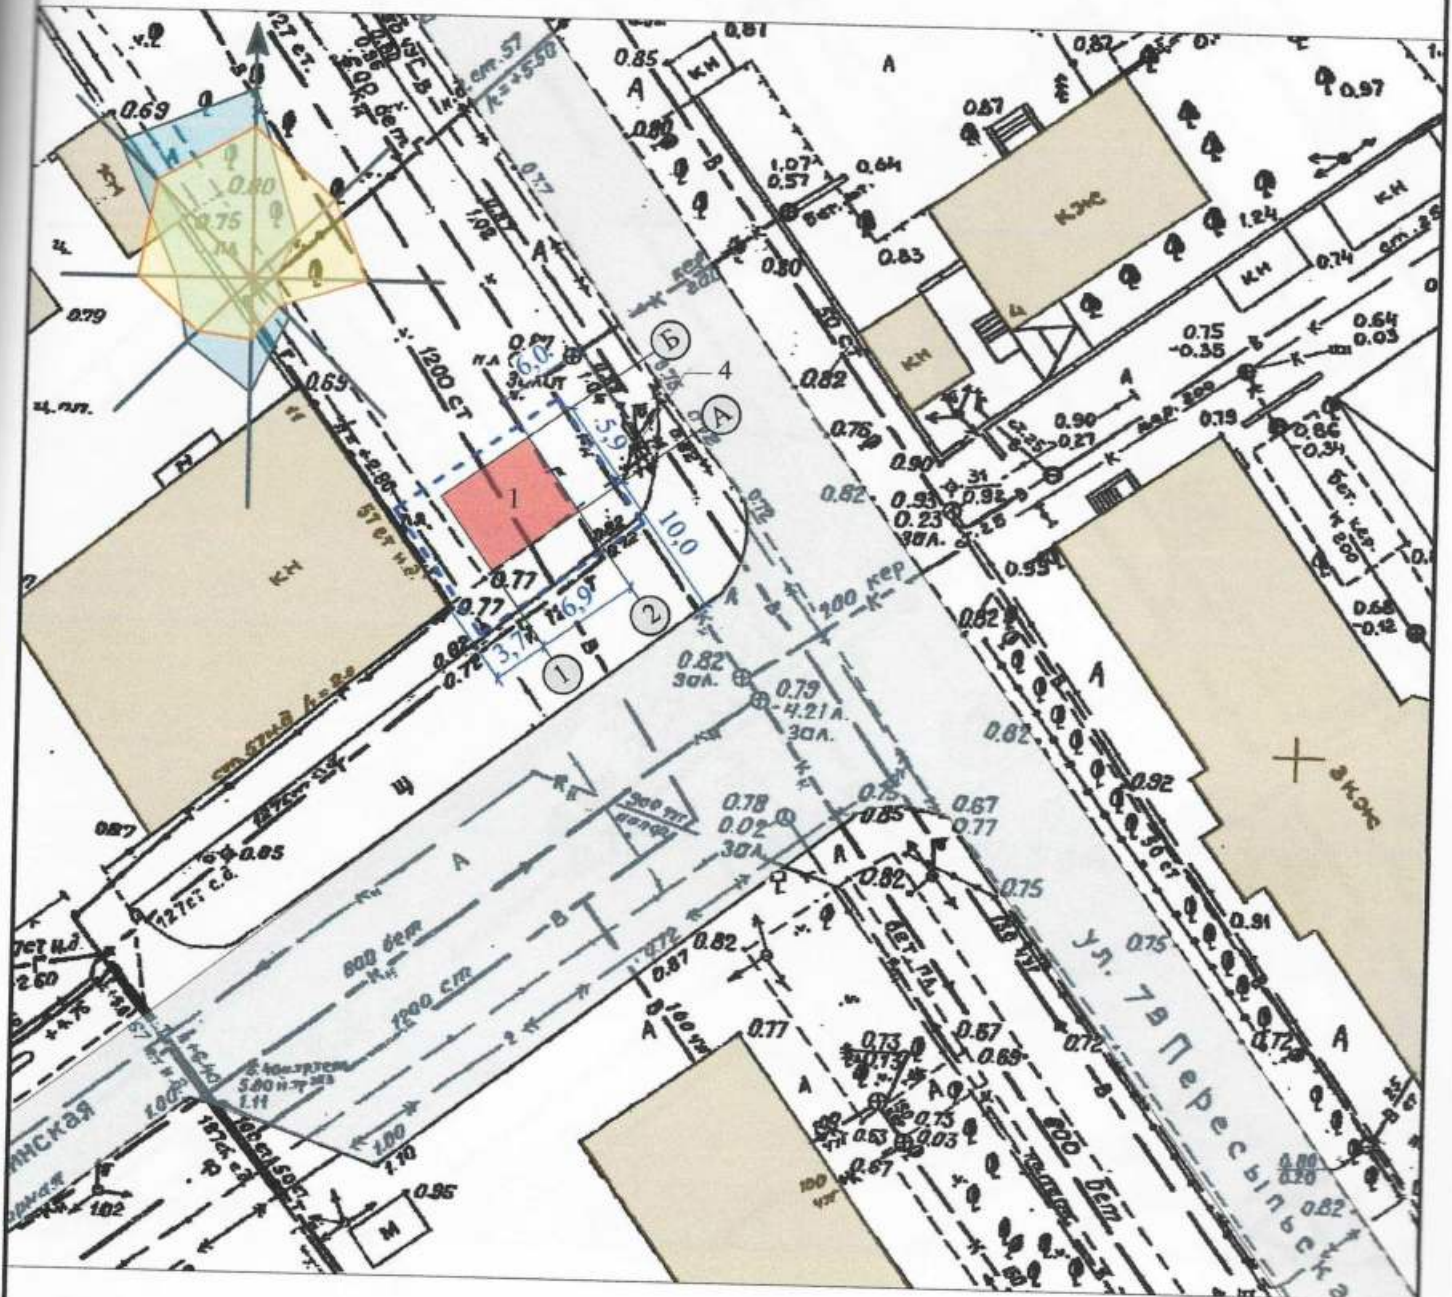

Експлікація:

- 1) місце розташування ТС;
- 2) червоні лінії;
- 3) лінії регулювання забудови;
- 4) місця підключення до інженерних мереж.

Умовні позначення

- Існуюча дорога
- Існуючі споруди
- Існуюче озеленення
- Тимчасова споруда
- Територія, що підлягає благоустрою


Архітектор

Кваліфікаційний сертифікат, серія АА № 002057



Давидова В.В.

СИТУАЦІЙНИЙ ПЛАН М 1:2000

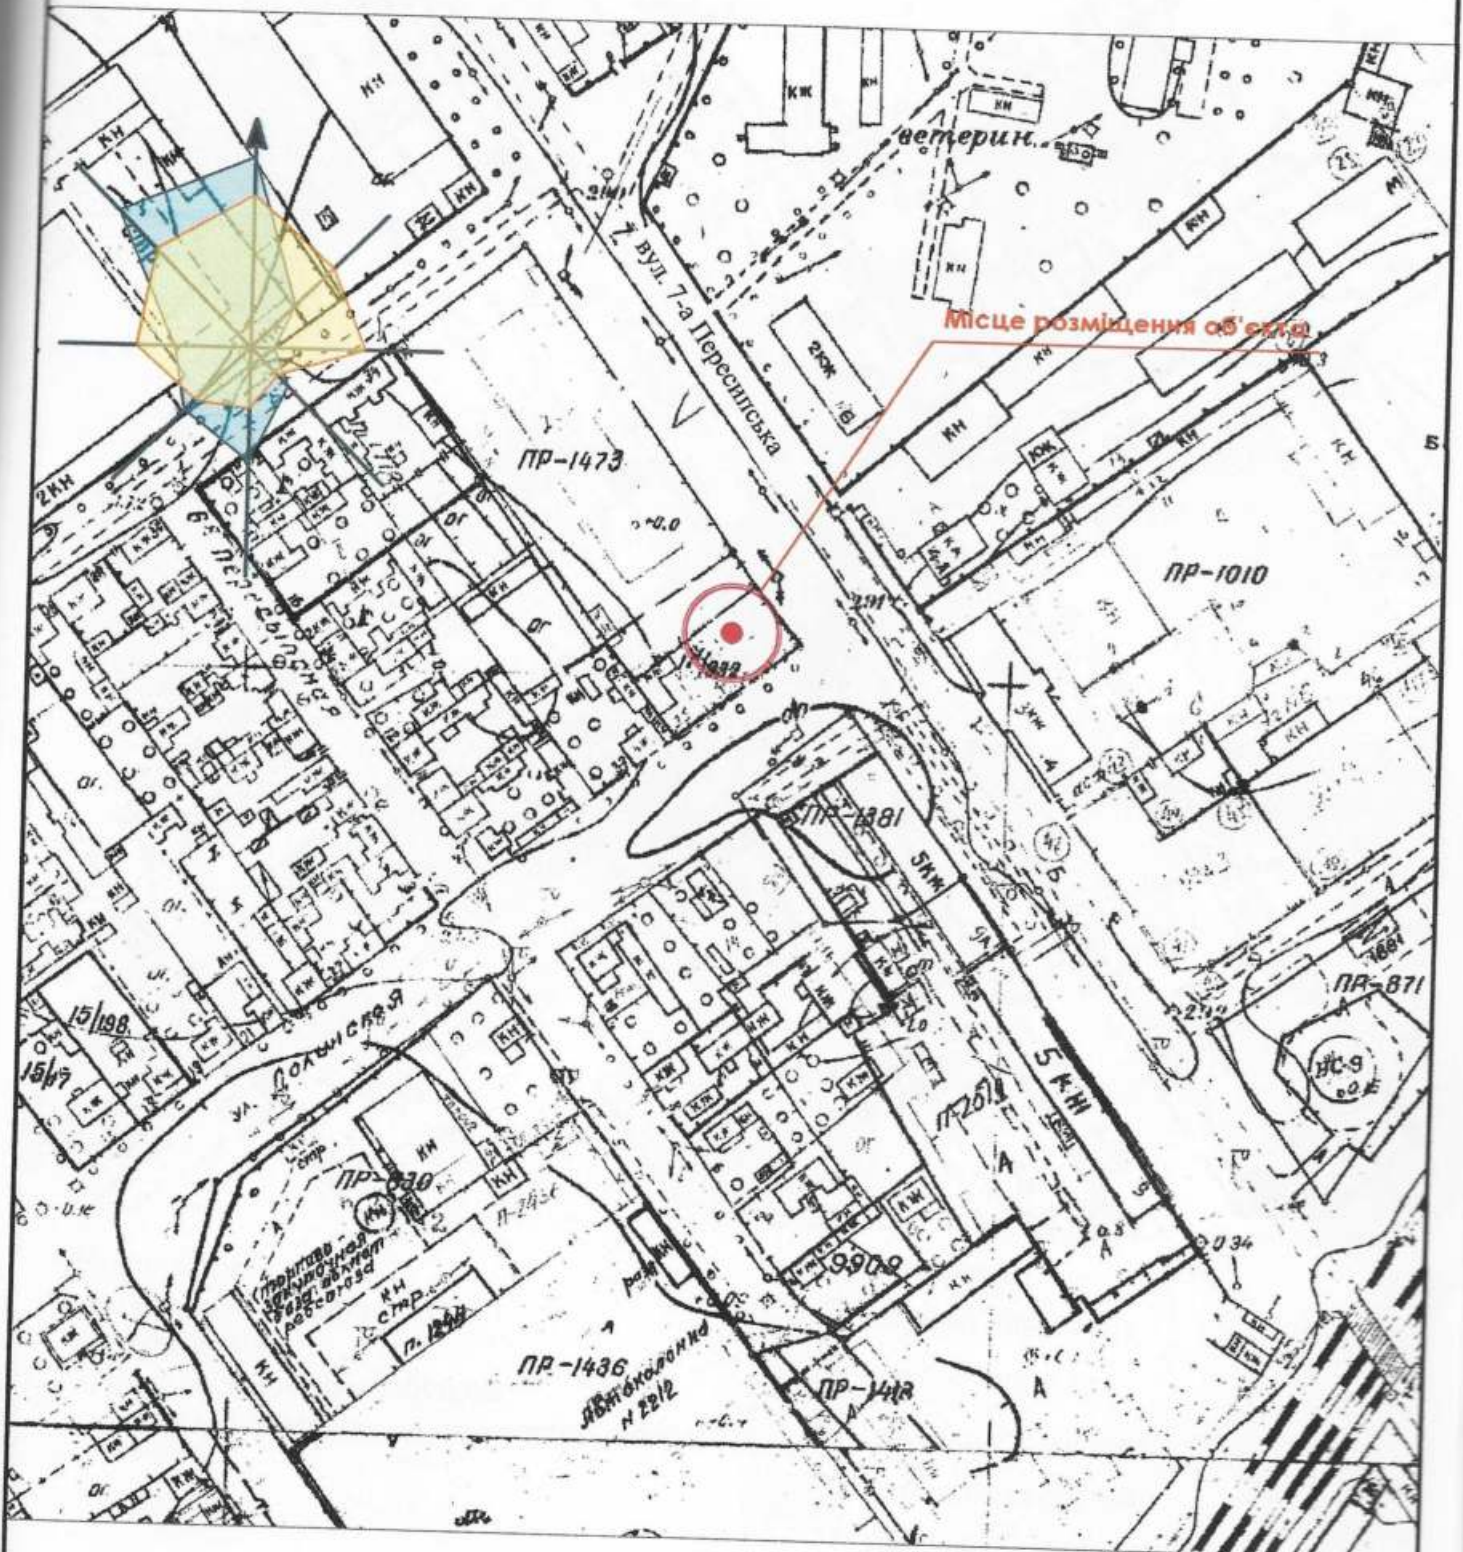

Архітектор
Кваліфікаційний сертифікат, серія АА № 002057



Давидова В.В.