

ПОЯСНЮВАЛЬНА ЗАПИСКА

1. Стационарна тимчасова споруда для здійснення підприємницької діяльності ~~мзе~~
торгівельні приміщення для тимчасового перебування людей.

За умовну позначку 0,000 прийнятий рівень чистої підлоги ТС.

Ступінь вогнестійкості тимчасової споруди III а.

Габаритні розміри в плані – 3,2 X 2,8 м.

Площа забудови – 8,96 м²

Загальна висота – 3,30 м.

Внутрішня висота складає – 2,80 м.

ТС встановлюється без закладення фундаменту на існуючому асфальтобетонному покритті.

Запроектований ТС має вхід з бокового фасаду. Торгівля передбачається з фасадного вікна.

Стіни споруди запроектовані по типу “Сендвич” товщиною 100 мм із утеплювачем з мінеральної вати й обшивкою. Обшивка стін по каркасу: зовнішня – алюмінієві сандвіч панелі; внутрішня (стіни й стеля) – металопластикова вагонка.

Підлога - деревні дошки 40 мм по металевому каркасу з утеплювачем та покриттям з негорючого матеріалу.

Покрівля – по металевих прогонах і решетуванню з покриттям із профільованого сталевих листа, з утеплювачем з мінераловатних плит, гідро- і пароізоляцією.

Зовнішня обробка:

Поверхні стін – колірні алюмінієві сандвіч панелі, типа «Алюкобонд»;

Вікна – металопластикові;

Вері – металопластикові;

Покрівля – профільований сталевий лист;

Поколь – колірні алюмінієві сандвіч панелі

2. Підключення до інженерних мереж:- тимчасова споруда підключається до існуючої електромережі, згідно договору про постачання електричної енергії.

Опалювання – електричне з встановленням навісних електро - конвекторів з регулюванням температури.

Освітлення приміщення виконане стельовими світильниками з люмінесцентними лампами.


Архітектор

Кваліфікаційний сертифікат, серія АА № 002057





Давидова В.В.

ФАСАДИ В ОСЯХ 1-2
М 1:50

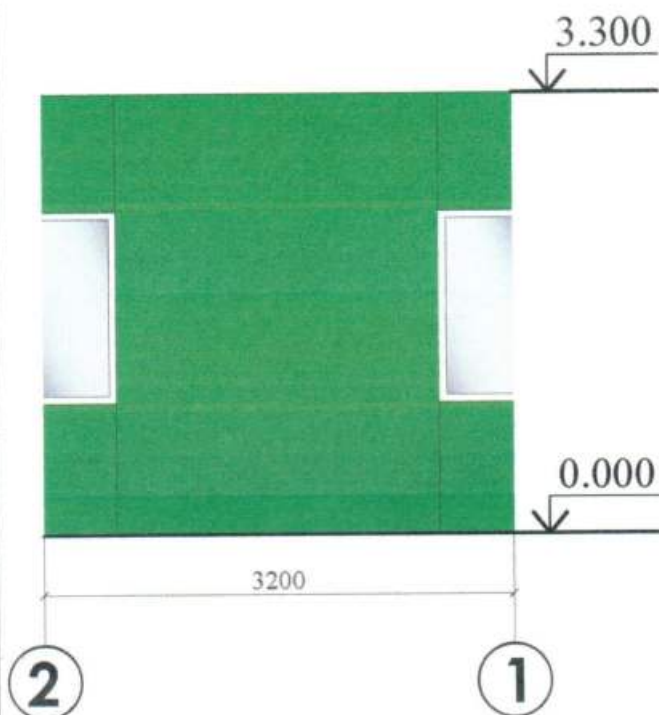

ФАСАДИ В ОСЯХ А-Б
М 1:50

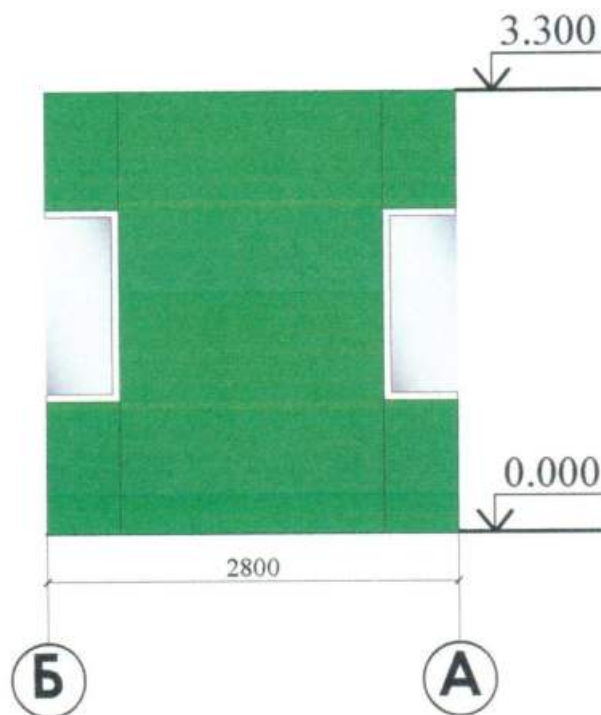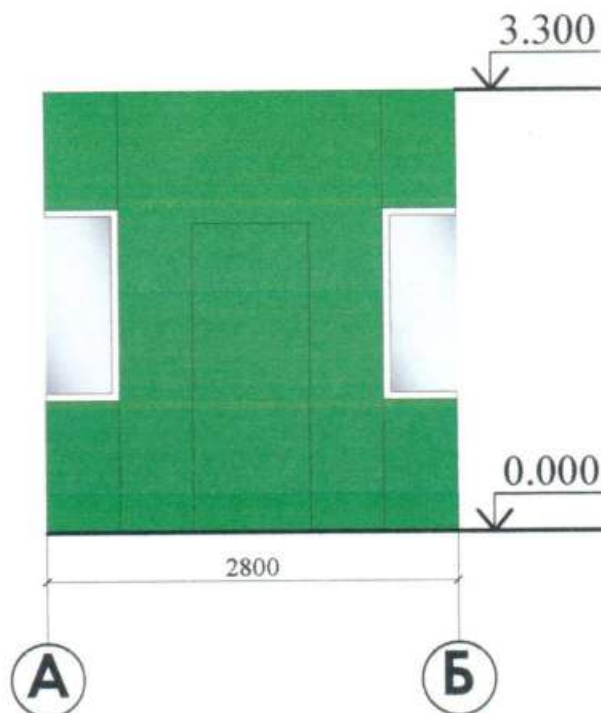


Архітектор
Кваліфікаційний сертифікат, серія АА № 002057



Давидова В.В

ПЛАН ТС М 1:50

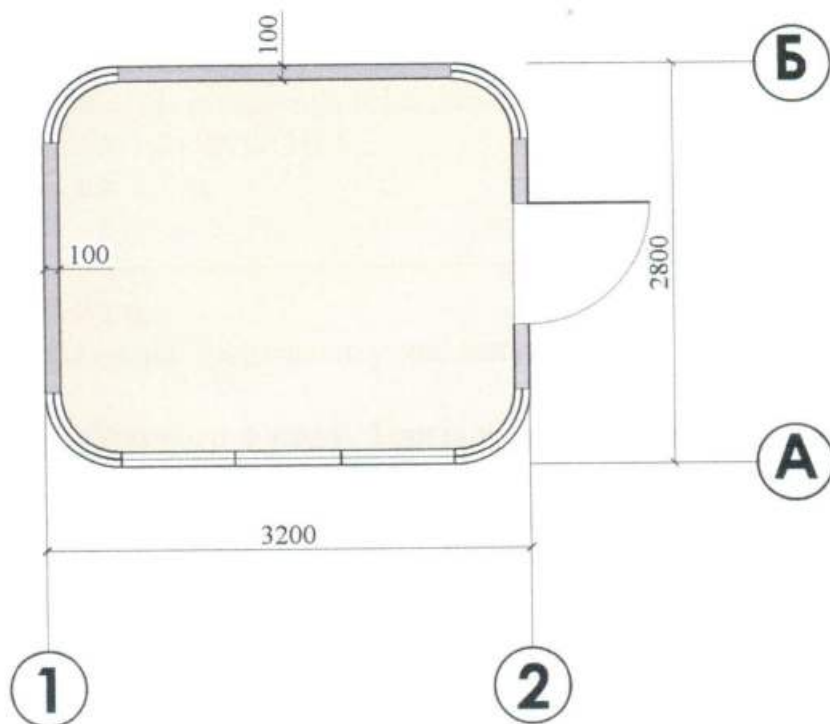

Архітектор


Кваліфікаційний сертифікат, серія АА № 002057



Давидова В.В

СХЕМА РОЗМІЩЕННЯ ТС М 1:500

Площа земельної ділянки згідно з документами на землекористування під ТС відсутня

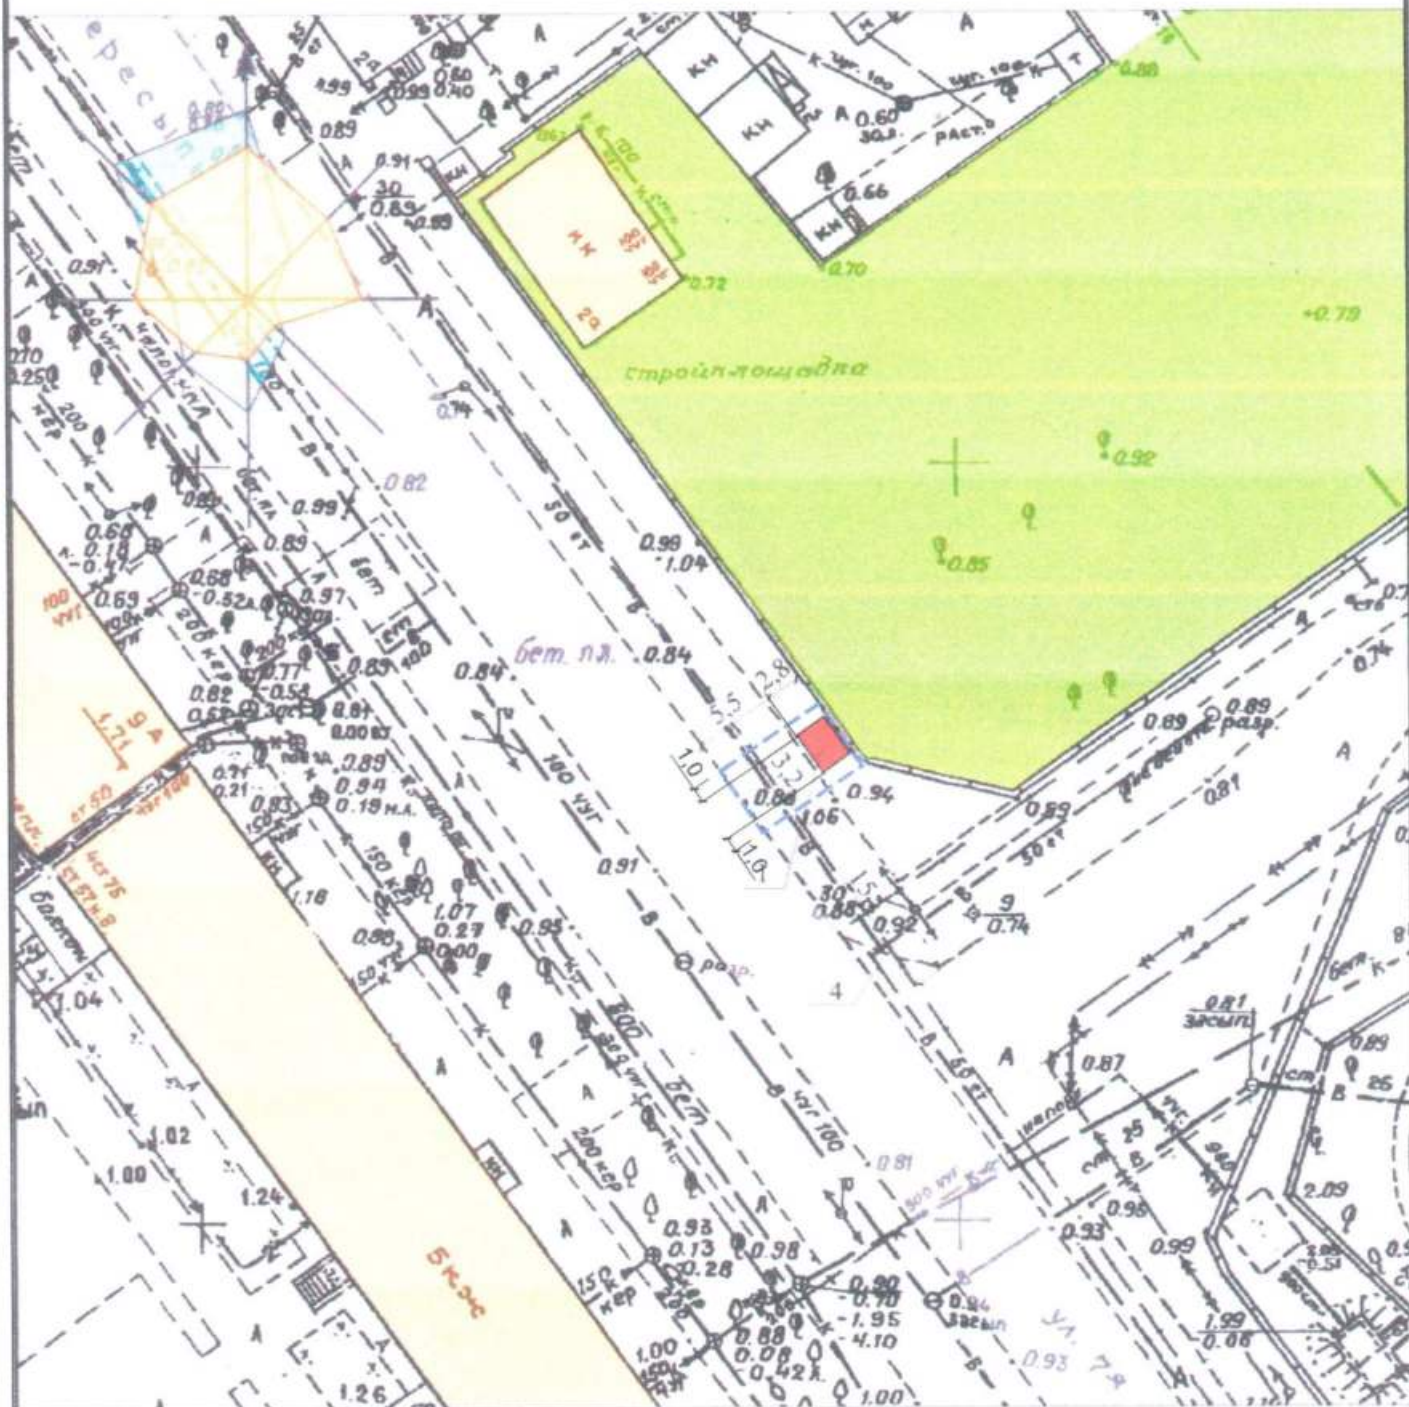

Експлікація:

- 1) місце розташування ТС;
- 2) червоні лінії;
- 3) лінії регулювання забудови;
- 4) місця підключення до інженерних мереж.

Умовні позначення

- Існуючі споруди
- Озеленення
- Тимчасова споруда
- Територія, що підлягає благоустрою


Архітектор

Кваліфікаційний сертифікат, серія АА № 002057



Давидова В.В

СИТУАЦІЙНИЙ ПЛАН
М 1:2000

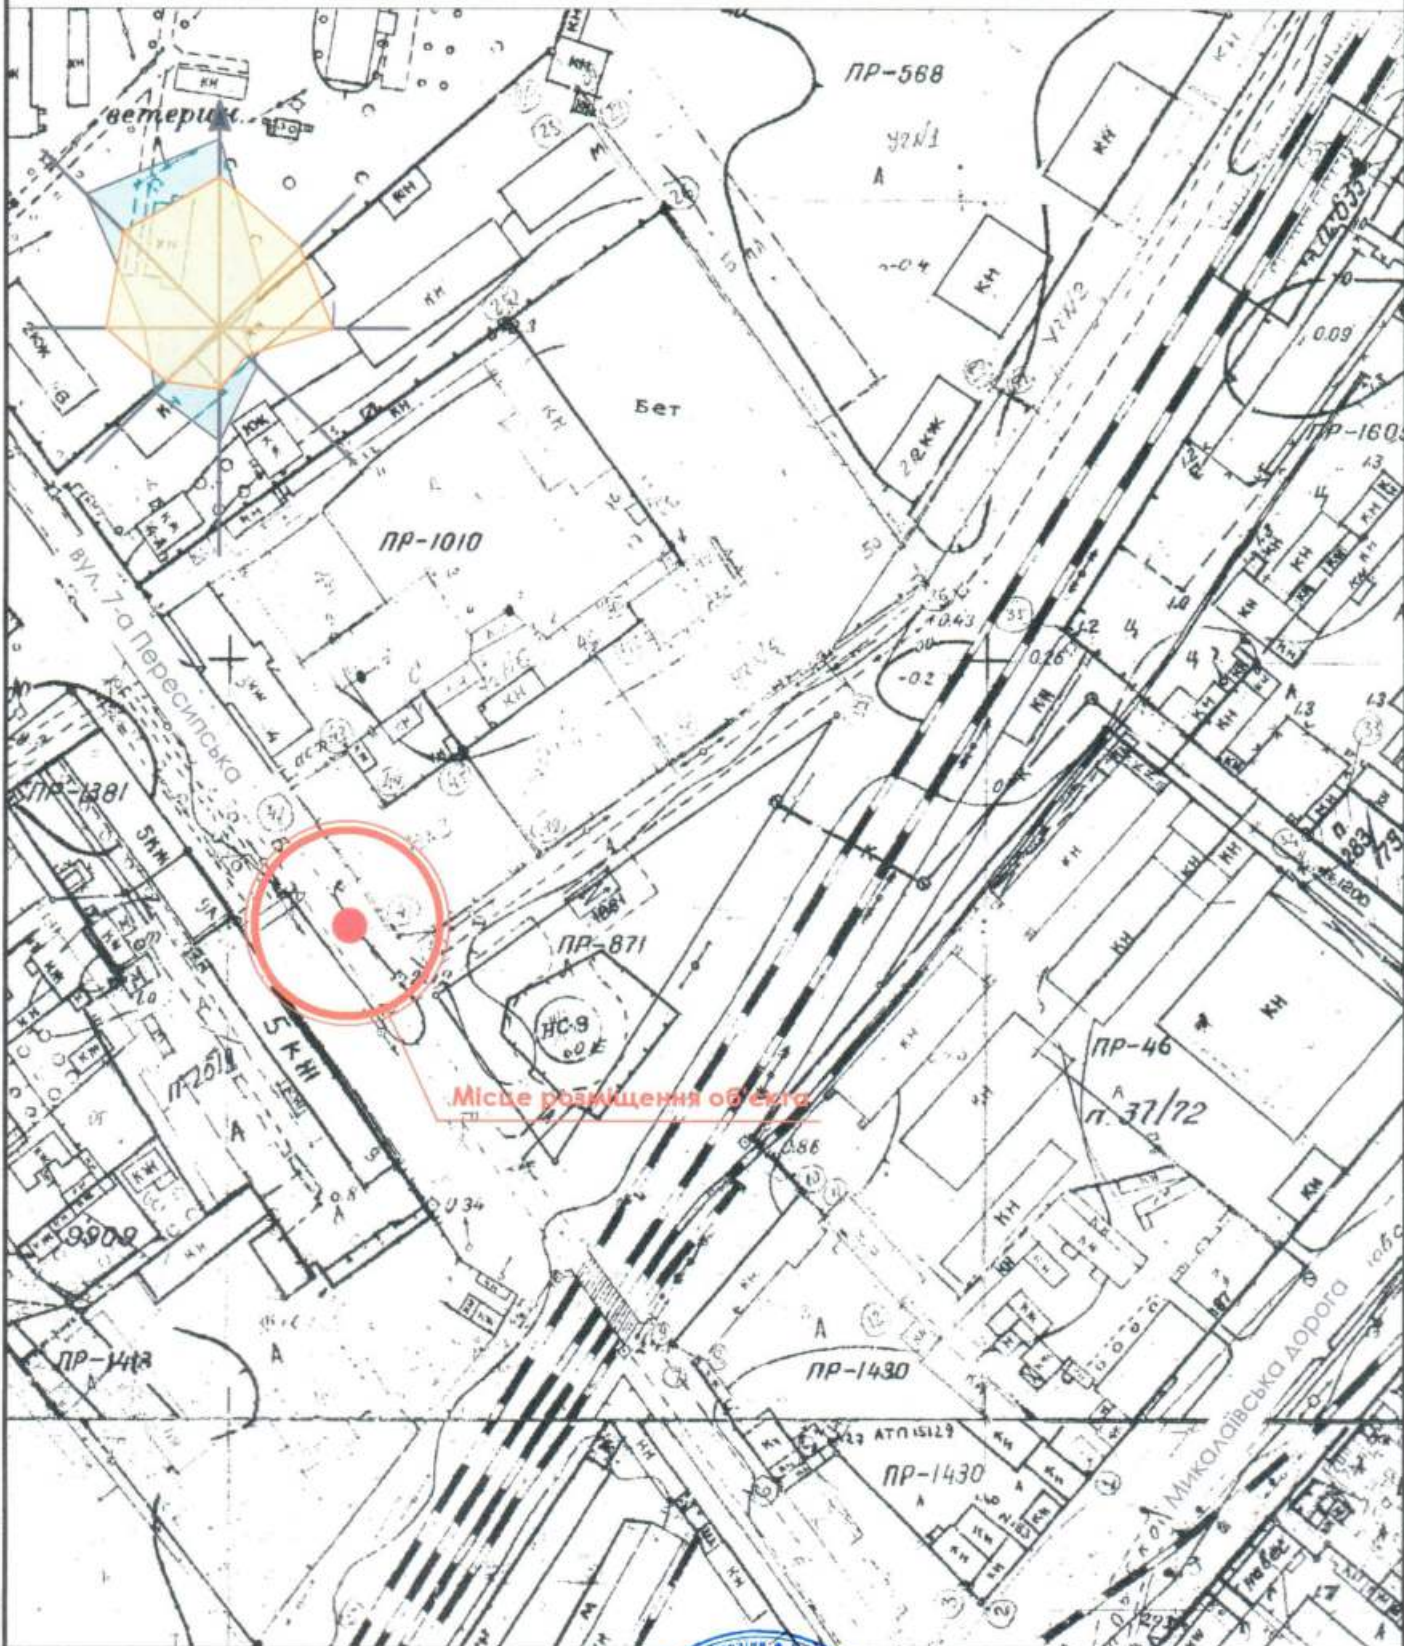

Архітектор

Кваліфікаційний сертифікат, серія АА № 002057



Давидова В.В