

СТИСЛА ПОЯСНЮВАЛЬНА ЗАПИСКА

1. Група стаціонарних тимчасових споруд для здійснення підприємницької діяльності, яка має торговельні приміщення для тимчасового перебування людей.
Ступінь вогнестійкості — IIIa
Павільйони мають приблизну до прямокутної форму.
Габаритні розміри групи у плані — 7.75м x 4.15м.
Площа забудови — 31.90м²
Площа твердого покриття — 31.90м²
Загальна площа групи — 27.42м²
Загальна висота групи — 2.30 м
Внутрішня висота складає — 1.90м
Ґрунт заснування, до встановлення ТС, ретельно утрамбовується щебенем та укладається тротуарна плитка.
Стіни споруди запроектовані товщиною 100 мм із сертифікованим утеплювачем із мінеральної вати та обшивкою з обох сторін.
Обшивка сторін по каркасу: зовні - композитні матеріали типу Алюкобонд внутрішня (стіни та стеля) — пластикова вагонка.
Підлога — дерев'яні дошки 40 мм по металевому каркасу з утеплювачем з мінераловатних плит та покриттям антипіринами та антигрибковими засобами.
Покрівлю — по металевим прогонам і решетуванню з покриттям профнастілом, з утеплювачем з мінераловатних плит.
Зовнішня обробка:
поверхні стін — композитні матеріали типу Алюкобонд .
вікна та двері — металопластикові із вакуумними склопакетами;
покрівля — пофнастіл.

2. Група стаціонарних тимчасових споруд підключається до мереж електропостачання згідно з чинними нормами та ТУ. Точка підключення згідно з ТУ.

Опалення - електричне з встановленням навісних електро-конвекторів з регулюванням температури.

Освітлення приміщення виконується світильниками з діодними лампами.

Розподільні мережі виконані проводами із мідними жилами, що прокладені у трубах та приховані в обшивці стін.

Захист мереж від дії струмів, коротких замикань та перевантажень здійснюється автоматичними вимикачами щитка. Передбачене заземлення.

3. Благоустрій прилеглої території виконується згідно з планом благоустрою, Освітлення території передбачене світильниками, що розміщуються на основному фасаді та над входом в ТС.

Директор ТОВ "Архітектурне Бюро "АРКАДІЯ"

Смаглій Д.П.

Архітектор


Кваліфікаційний сертифікат серія АА №002590




Глінін Д.Ю.

ЕСКІЗИ ГРУПИ ФАСАДІВ ТС

Головний фасад групи ТС М 1:50

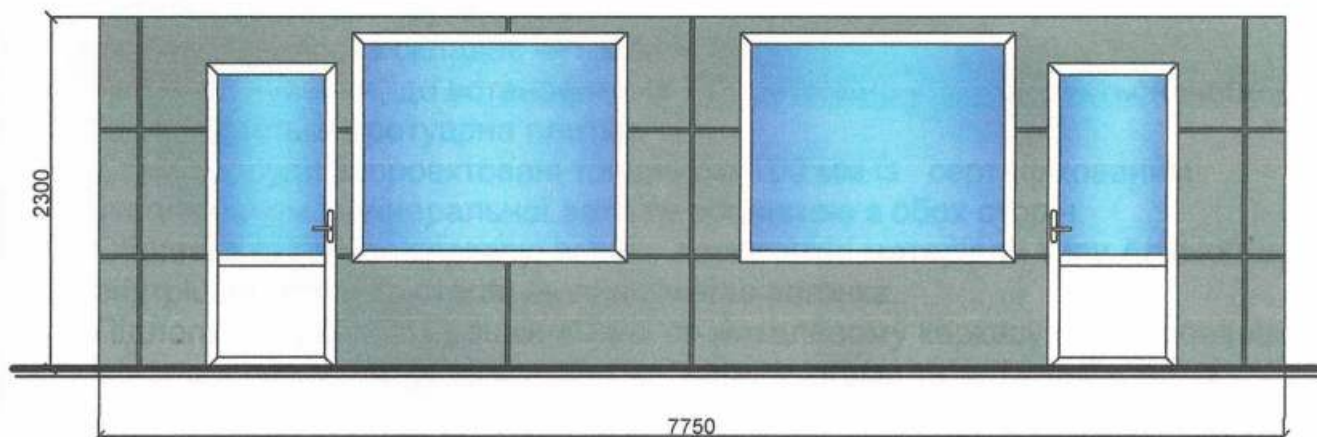

Бічний фасад групи ТС М 1:50

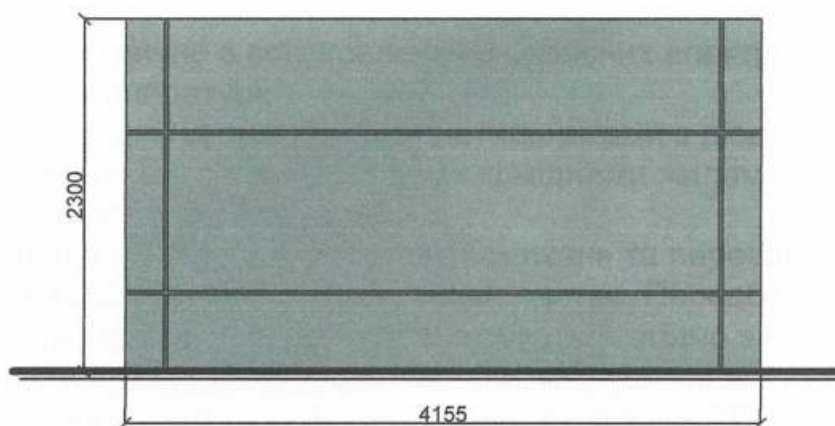

Директор ТОВ "Архітектурне Бюро "Аркадія"

Архітектор


Кваліфікаційний сертифікат серія АА №002590



Смаглій Д.П.

Глінін Д.Ю.

ПЛАН ГРУПИ ТС М 1:50

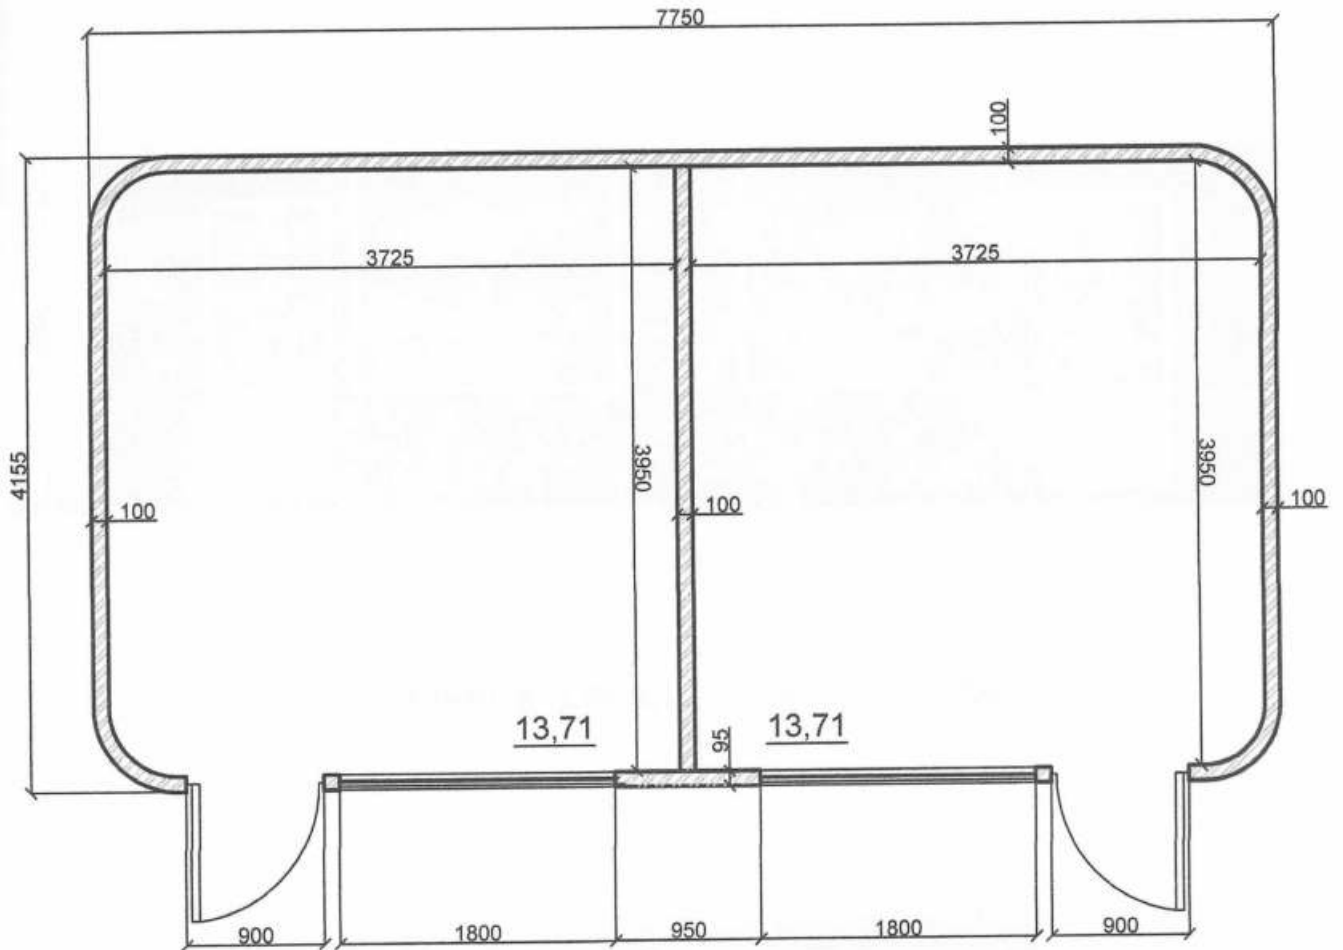

Директор ТОВ "Архітектура Бюро " Аркадія

Архітектор

Кваліфікаційний сертифікат серія АА №002590




Смаглій Д.П.

Глінін Д.Ю.

СХЕМА РОЗМІЩЕННЯ ГРУПИ СТАЦІОНАРНИХ ТС М 1:500

Площа земельної ділянки згідно з документами на
землекористування - землі міста

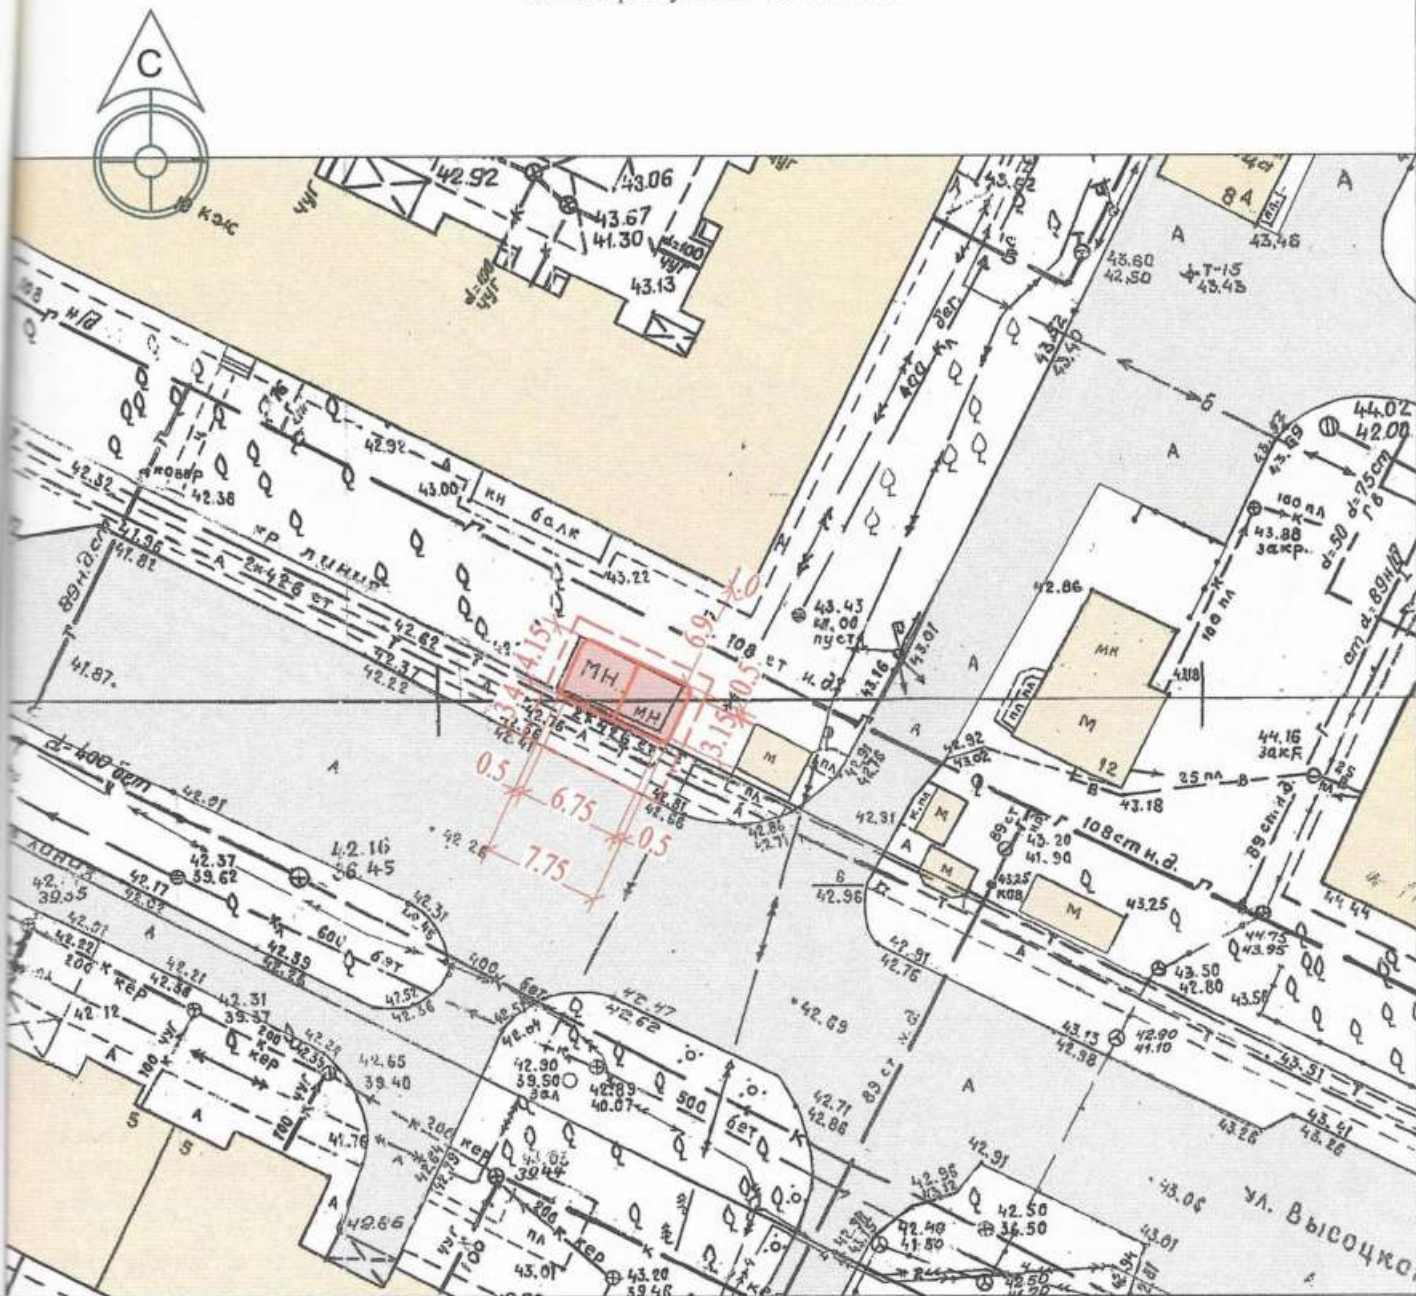

Експлікація:

- 1) місце розташування ТС;
- 2) червона лінія;
- 3) регулювання забудови;
- 4) місця підключення до інженерних мереж

Умовні позначення:

- межа благоустрою ділянки розміщення ТС
- існуюча ТС
- існуючі дороги
- існуючі будівлі

Директор ТОВ "Архітектурне Бюро "Аркадія"

Архітектор

Кваліфікаційний сертифікат серія АА №002590




Смаглюк Д.П.

Елещук Д.Ю.

СИТУАЦІЙНИЙ ПЛАН М 1:2000

Місце розміщення об'єкту

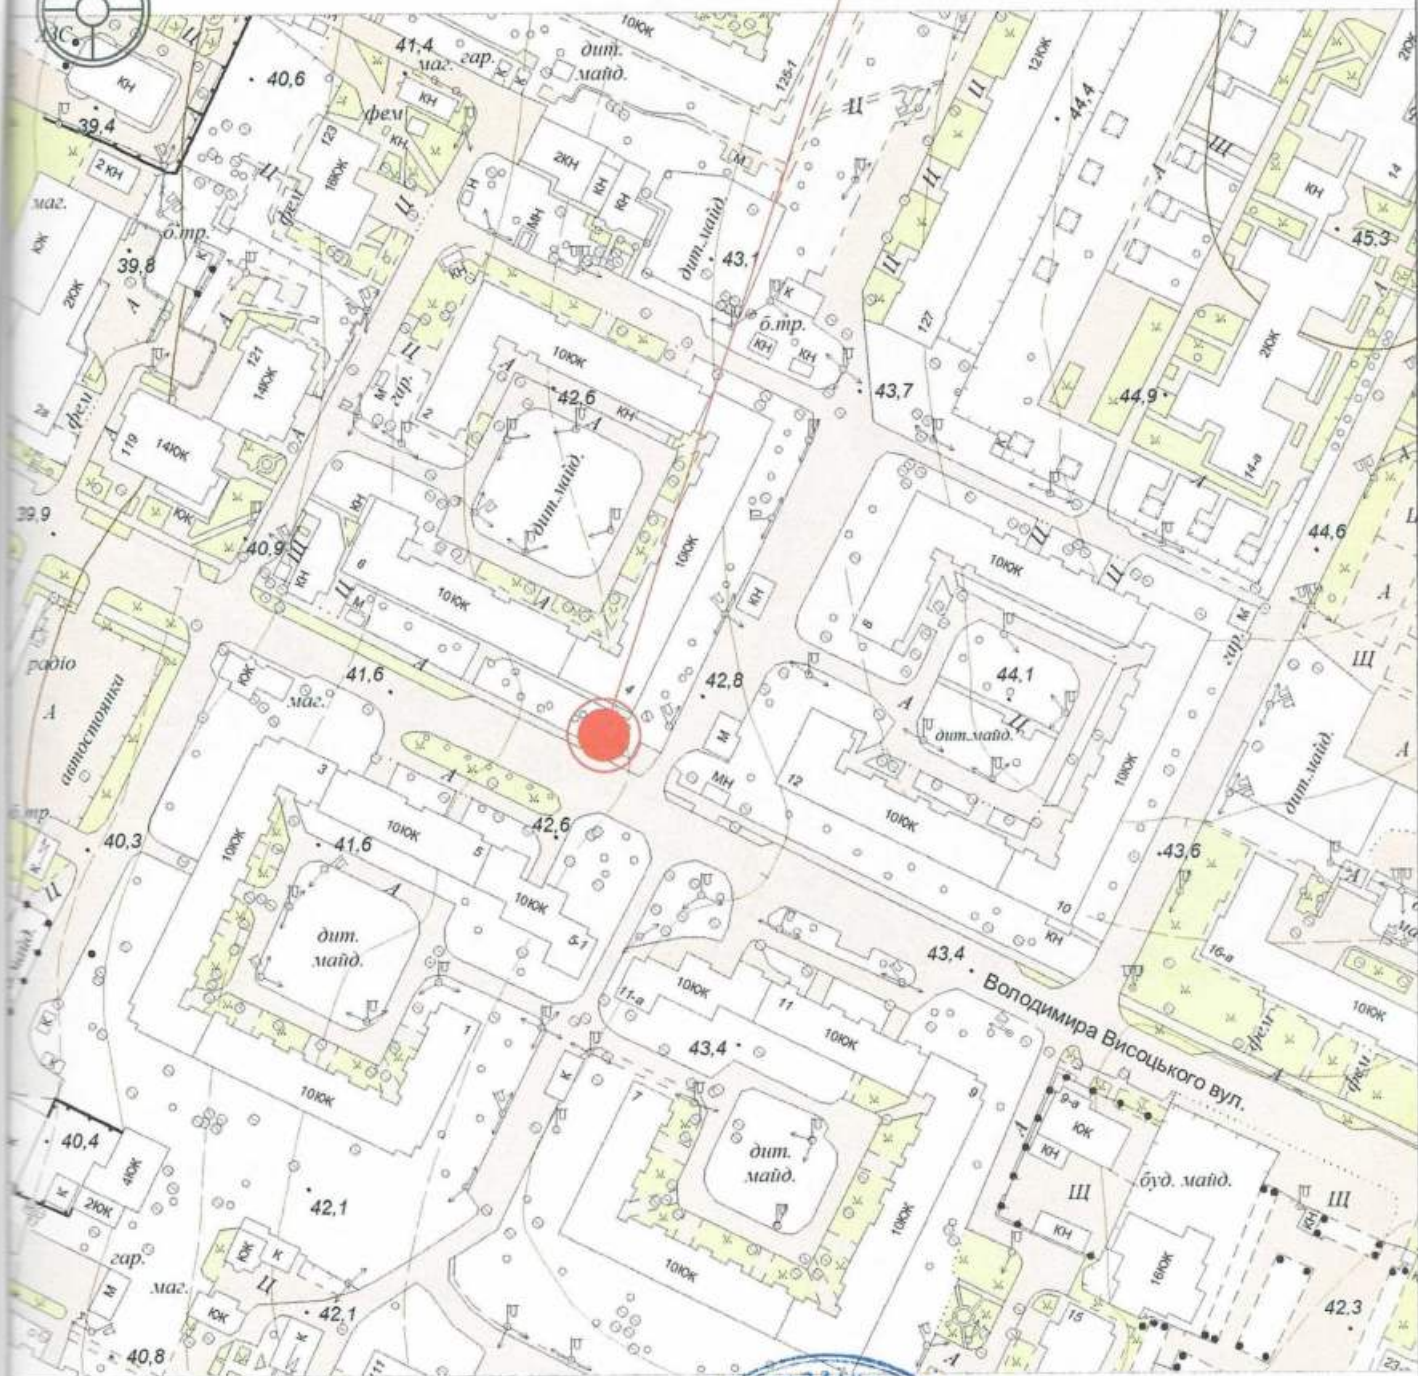

Директор ТОВ "Архітектурне Бюро "Аркадія"

Архітектор

Кваліфікаційний сертифікат серія АА №002590



Смагій Д.П.

Еліан Д.Ю.