

СТИСЛА ПОЯСНЮВАЛЬНА ЗАПИСКА

1. Тимчасова споруда для здійснення підприємницької діяльності має приміщення для тимчасового перебування людей.
За умовну позначку 0.0000 прийнятий рівень чистої підлоги ТС.
Ступень вогнестійкості – IIIа.
Габаритні розміри кіоска у плані 4,0х3,0м. Загальна площа ТС – 12,00м².
Внутрішня висота складає - 2,70м.
Загальна висота складає – 2,0м.
Ґрунт заснування, до встановлення ТС, ретельно утрамбовується щебенем та укладається бетонна тротуарна плитка.
Підлога – дерев'яні дошки 40мм по металевому каркасу з утеплювачем з мінераловатних плит та покриттям з негорючого матеріалу.
Покрівля – по металевим прогонам і решетуванню з покриттям покрівельними профільованими металевими листами, з утеплювачем з мінераловатних плит, гідро- і пароізоляцією.

Зовнішня обробка:

Вікна та двері – металопластикові з вакуумними склопакетами;
Покрівля – покрівельні профільовані металеві листи.

2. Тимчасова споруда підключається до мереж електропостачання згідно діючими нормами та ТУ. Точка підключення – згідно з наданими ТУ.
Опалення – електричне з встановленням навісних електро-конвекторів з регулюванням температури.
Освітлення приміщення виконується світильниками з люмінісцентними лампами.
Розподільні мережі виконані проводами з мідними жилами, що прокладені у трубах та приховані в обшивці стін.
Захист мереж від дії струмів коротких замикань та перевантажень здійснюється автоматичними вимикачами щитка.
3. Благоустрій прилеглої території виконується згідно с планом благоустрою. Освітлення території передбачене світильниками, що розміщуються на головному фасаді ТС.

Інженер-проектувальник


Кваліфікаційний сертифікат № 010376




С.В. Даркін

ЕСКІЗ ФАСАДІВ ТС

Головний фасад

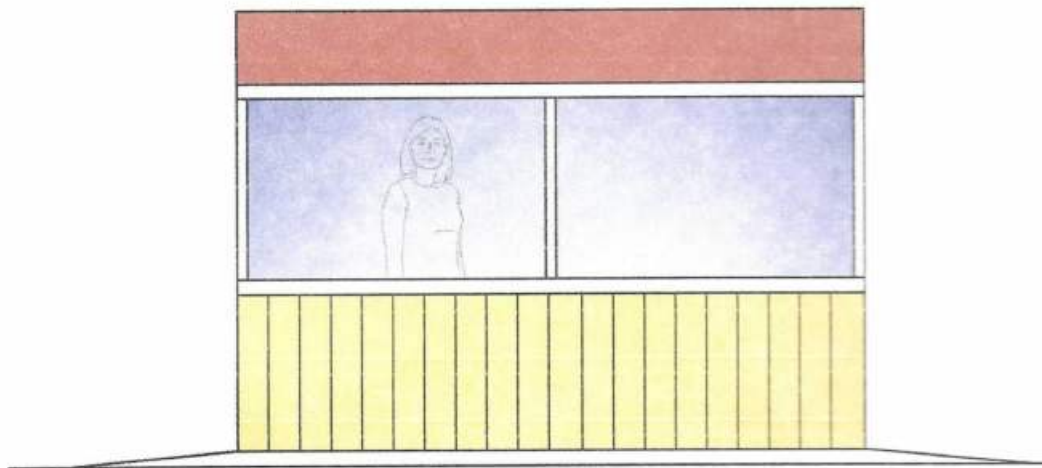

Бічний фасад

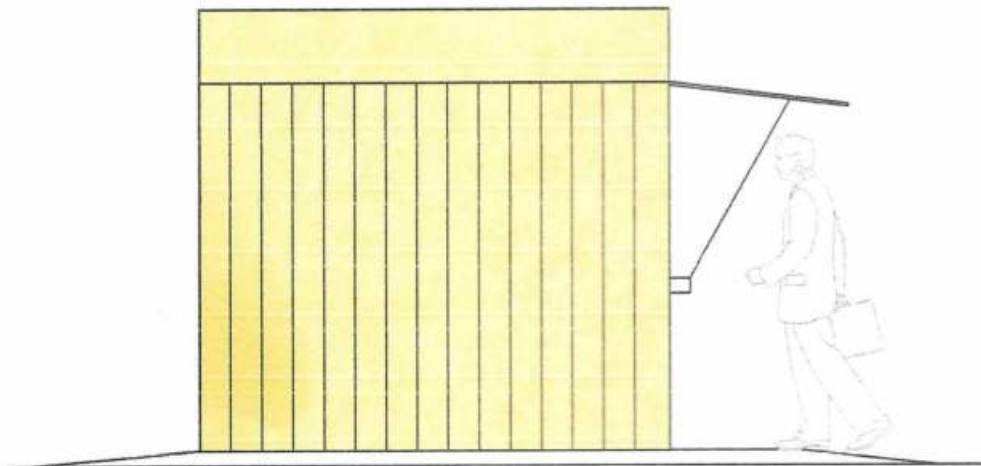


Інженер-проектувальник
Кваліфікаційний сертифікат № 010376



С.В. Даркін

ПЛАН ТС НА ВІДМ. 0.0000

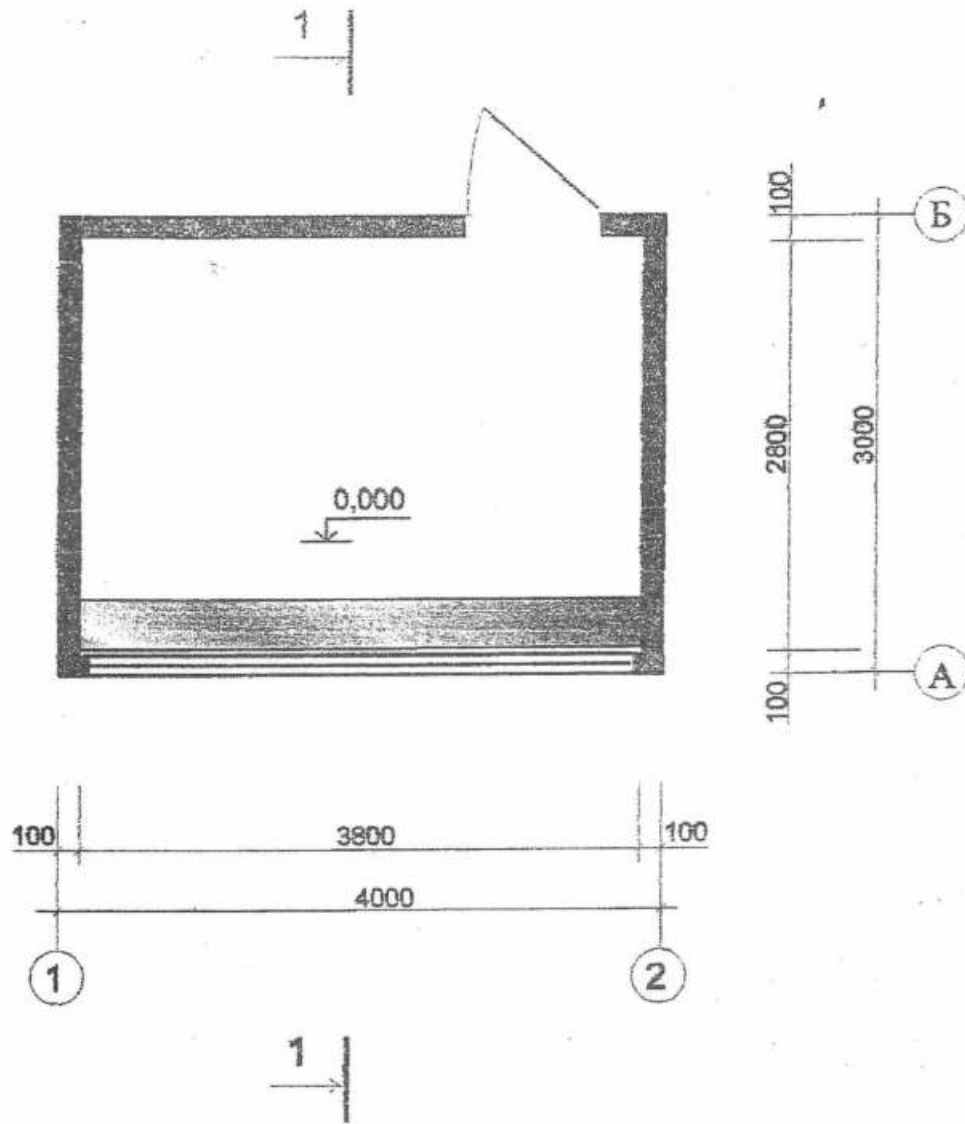


Інженер-проектувальник
Кваліфікаційний сертифікат № 010376



С.В. Даркін

СХЕМА РОЗМІЩЕННЯ ТС М 1:500

Площа земельної ділянки згідно з документами на землекористування - землі міста

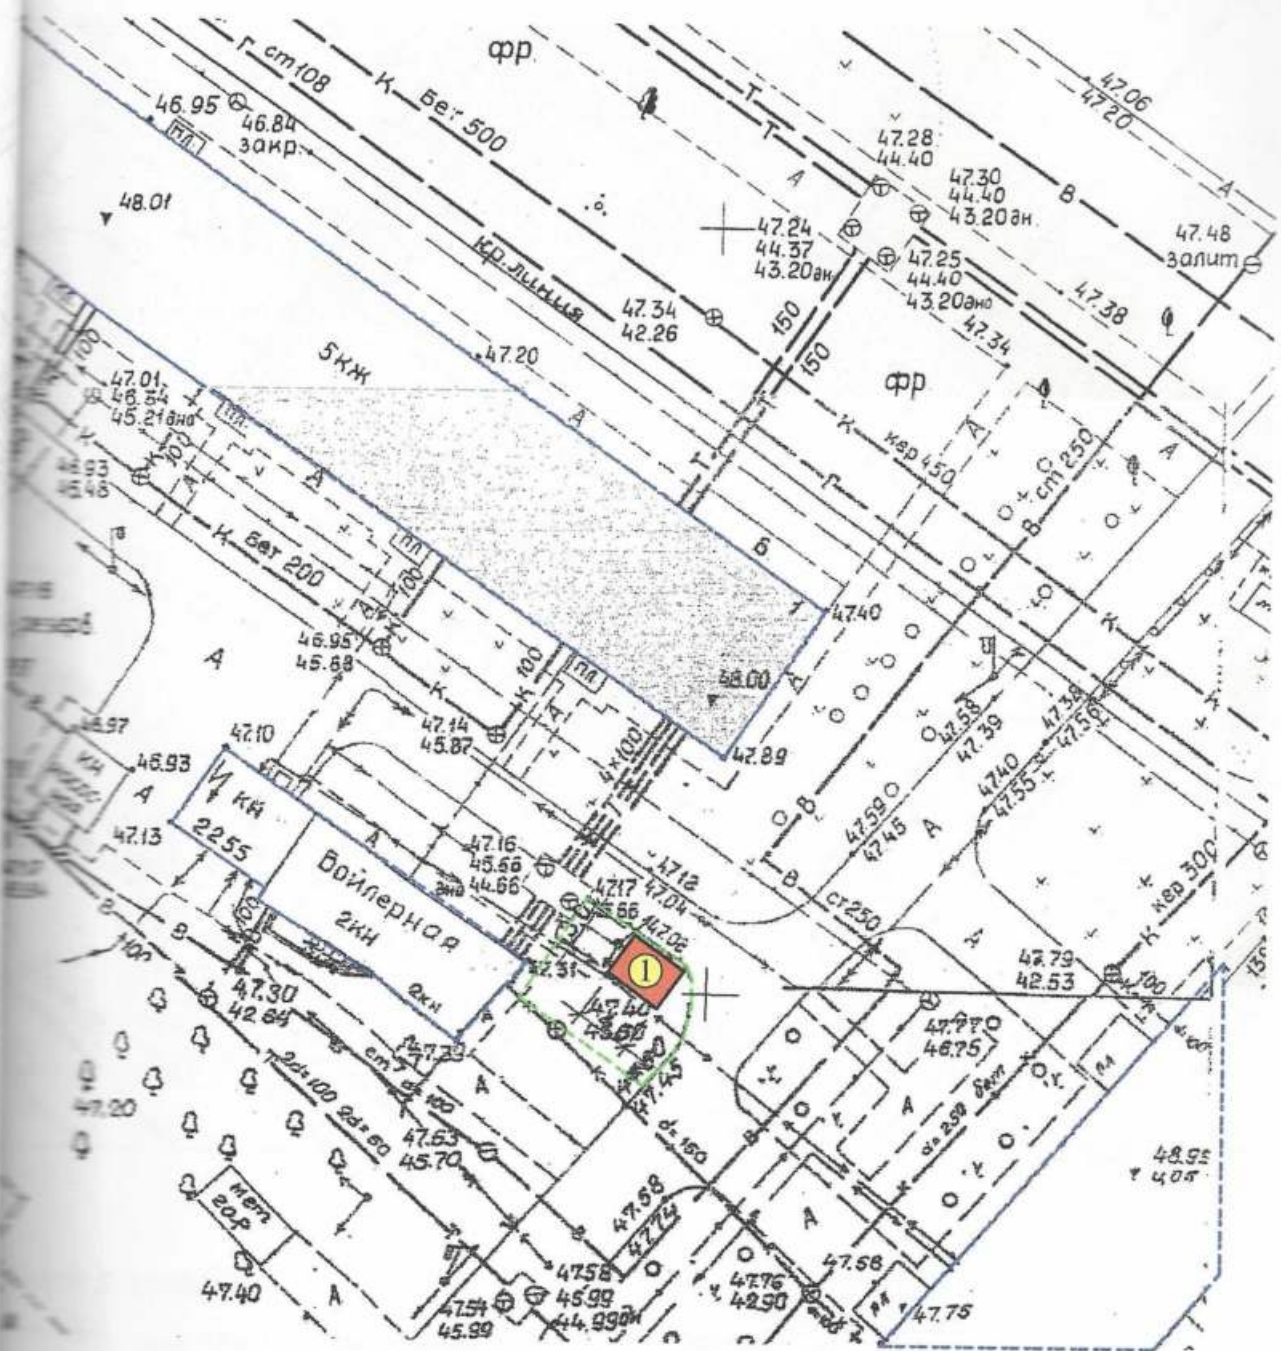

Легенда:

- місце розташування ТС;
- червоні лінії;
- лінії регулювання забудови;
- місце підключення до
внутрішніх мереж


- межа благоустрою ділянки
розміщення ТС
- проектна ТС
- існуючі будівлі
- існуючі дороги
- підключення до мереж
електропостачання



Інженер-проектувальник
Кваліфікаційний сертифікат № 010376

С.В. Даркін

СИТУАЦІЙНИЙ ПЛАН М 1:2000

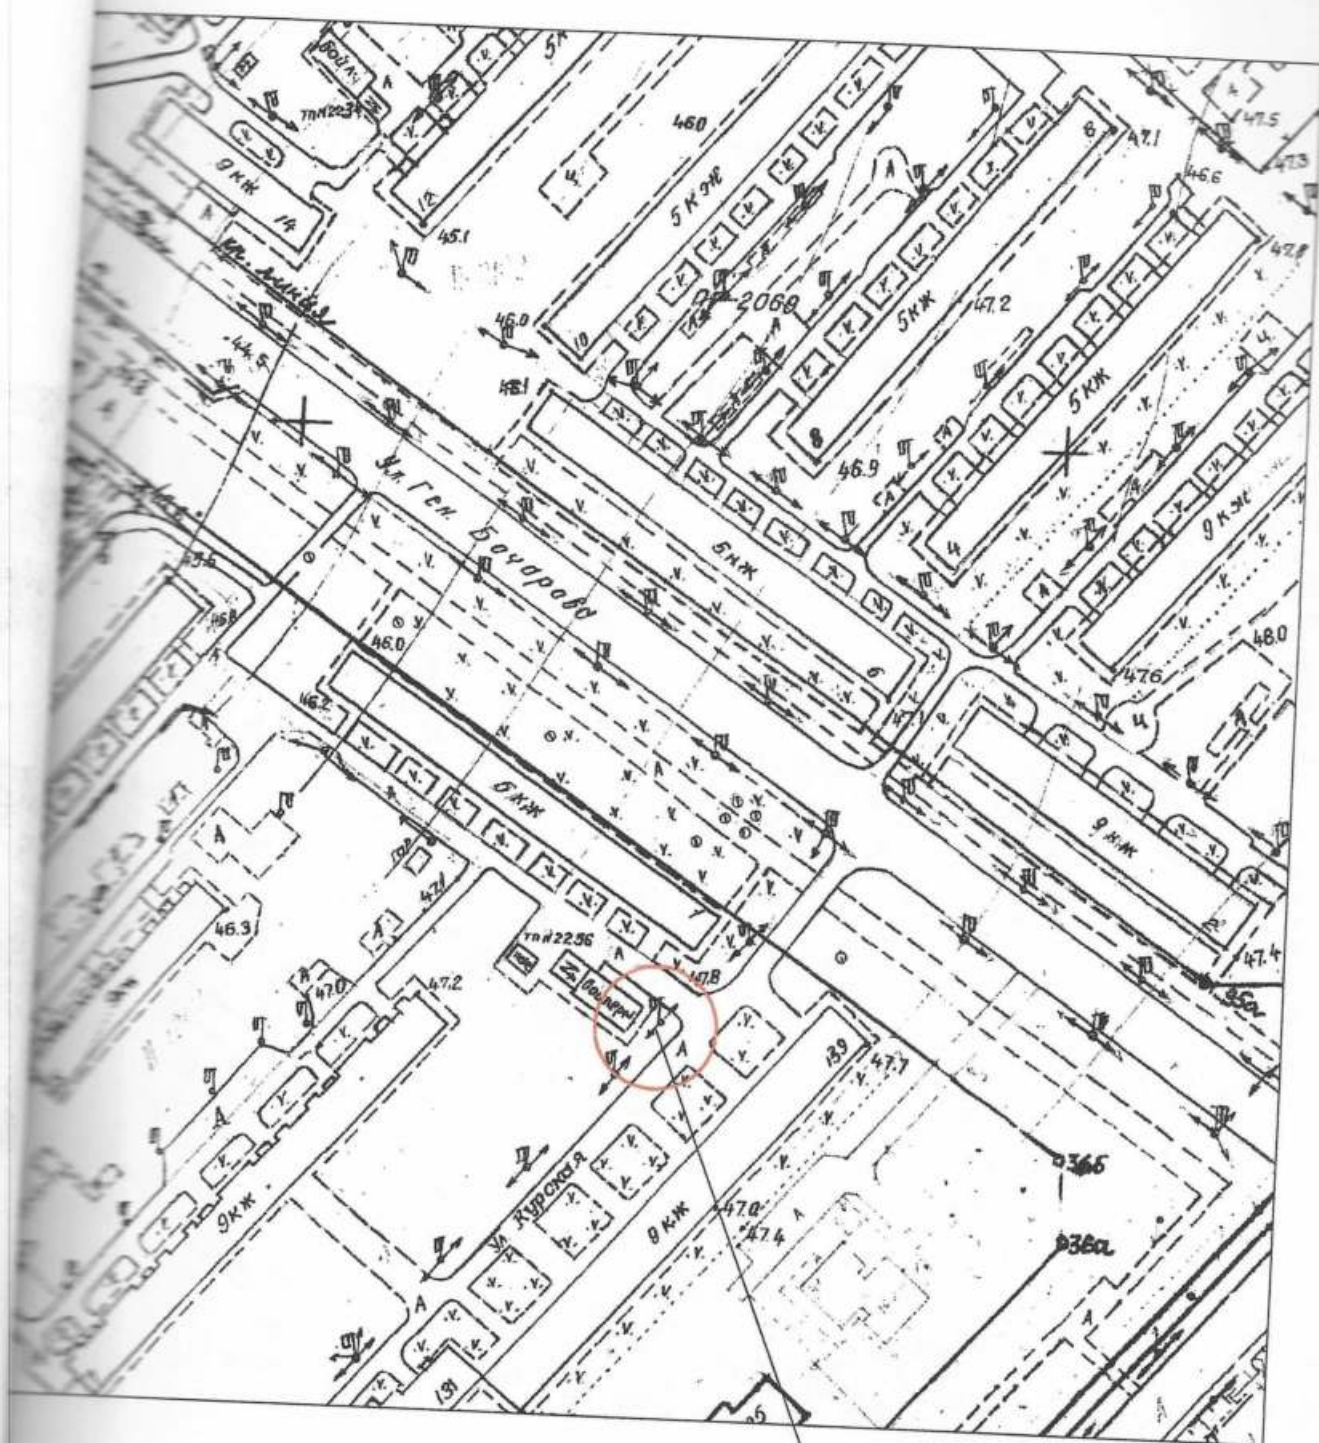

Місце розміщення ТС

Інженер-проектувальник
Кваліфікаційний сертифікат № 010376



С.В. Даркін