

СТИСЛА ПОЯСНЮВАЛЬНА ЗАПИСКА

1. Група стаціонарних тимчасових споруд для здійснення підприємницької діяльності має торгівельні приміщення для тимчасового перебування людей. За умовну позначку ± 0.000 прийнятий рівень чистої підлоги ТС. Ступінь вогнестійкості - IIIа.

Група тимчасових споруд складається з двох павільйонів. ТС1 прямокутної форми в плані з габаритними розмірами - 3,92 x 5,00 м;

ТС2 прямокутної форми в плані з габаритними розмірами - 3,18 x 5,00 м.

Загальна площа групи ТС - 35,50 м².

Внутрішня висота павільйонів від рівня чистої підлоги складає - 2,60 м.

Загальна висота складає - 2,90 м.

Група ТС встановлюється на існуюче асфальтове покриття, без влаштування фундаменту.

Стіни споруд запроектовані товщиною 100 мм із утеплювачем з мінеральної вати та обшивкою з обох сторін.

Обшивка стін по каркасу: зовнішня - композитні матеріали типу "Алюкобонд"; внутрішня - гіпсокартонні листи.

Підлога - дерев'яні дошки 40 мм по металевому каркасу з утеплювачем з мінераловатних плит та покриттям з негорючого матеріалу.

Покрівля - по металевим прогонам і риштуванню з покриттям оцинкованою покрівельною сталлю, з утеплювачем з мінераловатних плит, гідро- і пароізоляцією.

Зовнішня обробка:

поверхні стін - композитні матеріали типу "Алюкобонд";

вікна та двері - металопластикові з вакуумними склопакетами;

покрівля - оцинкована покрівельна сталь.

2. Група тимчасових стаціонарних споруд підключається до мереж електропостачання згідно з діючими нормами та ТУ. Точка підключення - згідно з ТУ.

Опалення - електричне з встановленням навісних електро-конвекторів з регулюванням температури.

Освітлення приміщення виконується світильниками з люмінесцентними лампами.

Розподільні мережі виконані проводами з мідними жилами, що прокладені у трубах та приховані в обшивці стін.

Захист мереж від дії струмів коротких замикань та перевантажень здійснюється автоматичними вимикачами щитка.

3. Благоустрій прилеглої території виконується згідно з планом благоустрою.

Освітлення території передбачене світильниками, що розміщуються на головному фасаді над входами у ТС.

В.о.директора ТОВ "АРХІТЕКС-ТУРИСМ" В.В.Сличенко

Головний інженер


Кваліфікаційний сертифікат серія АА № 012191




Т.Т.Євченко

ЕСКІЗИ ФАСАДІВ ТС

Головний фасад групи ТС М 1:50

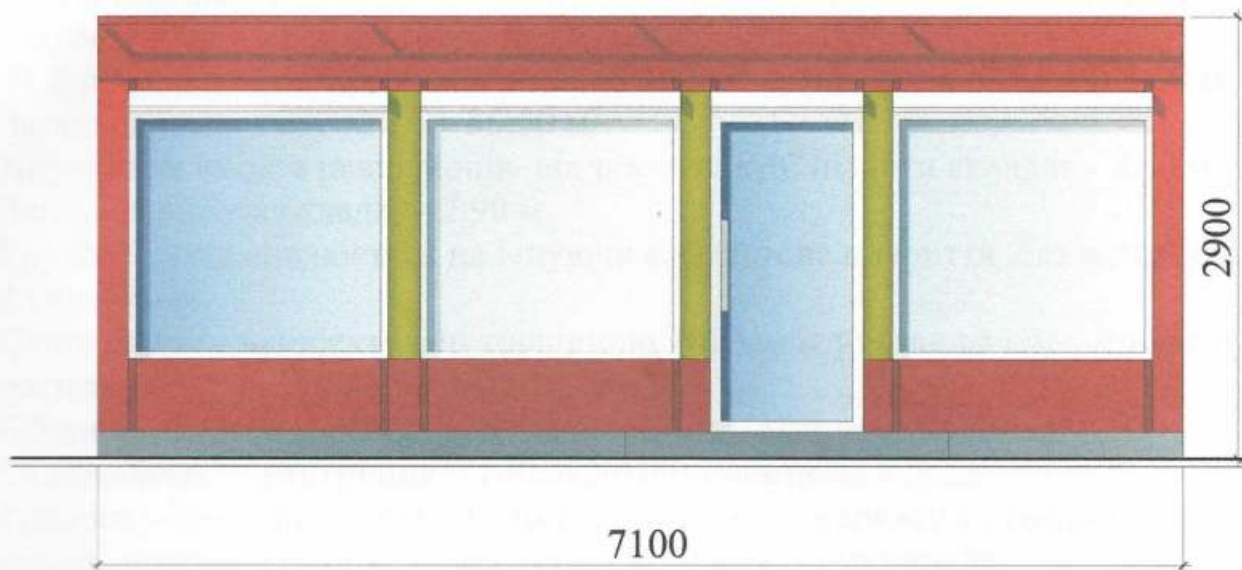

Бічний фасад групи ТС М 1:50

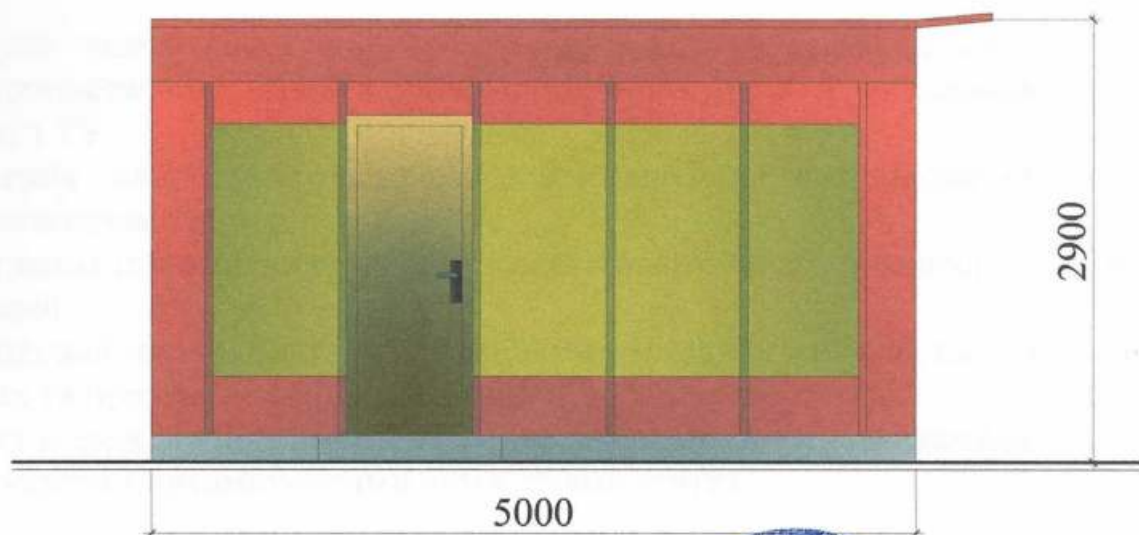

В.о.директора ТОВ "АРХІТЕКС-ТУРИЦЯ"

Головний інженер

Кваліфікаційний сертифікат серія АА № 012191



В.В. Сліпченко

Т.Т. Євченко

План групи ТС М 1:50




В.о.директора ТОВ "АРХІТЕКС-Гурія" В.В. Євченко

Головний інженер
Кваліфікаційний сертифікат серія АА № 012191

СХЕМА РОЗМІЩЕННЯ ТС М 1:500

Площа земельної ділянки згідно з документами
на землекористування - землі міста

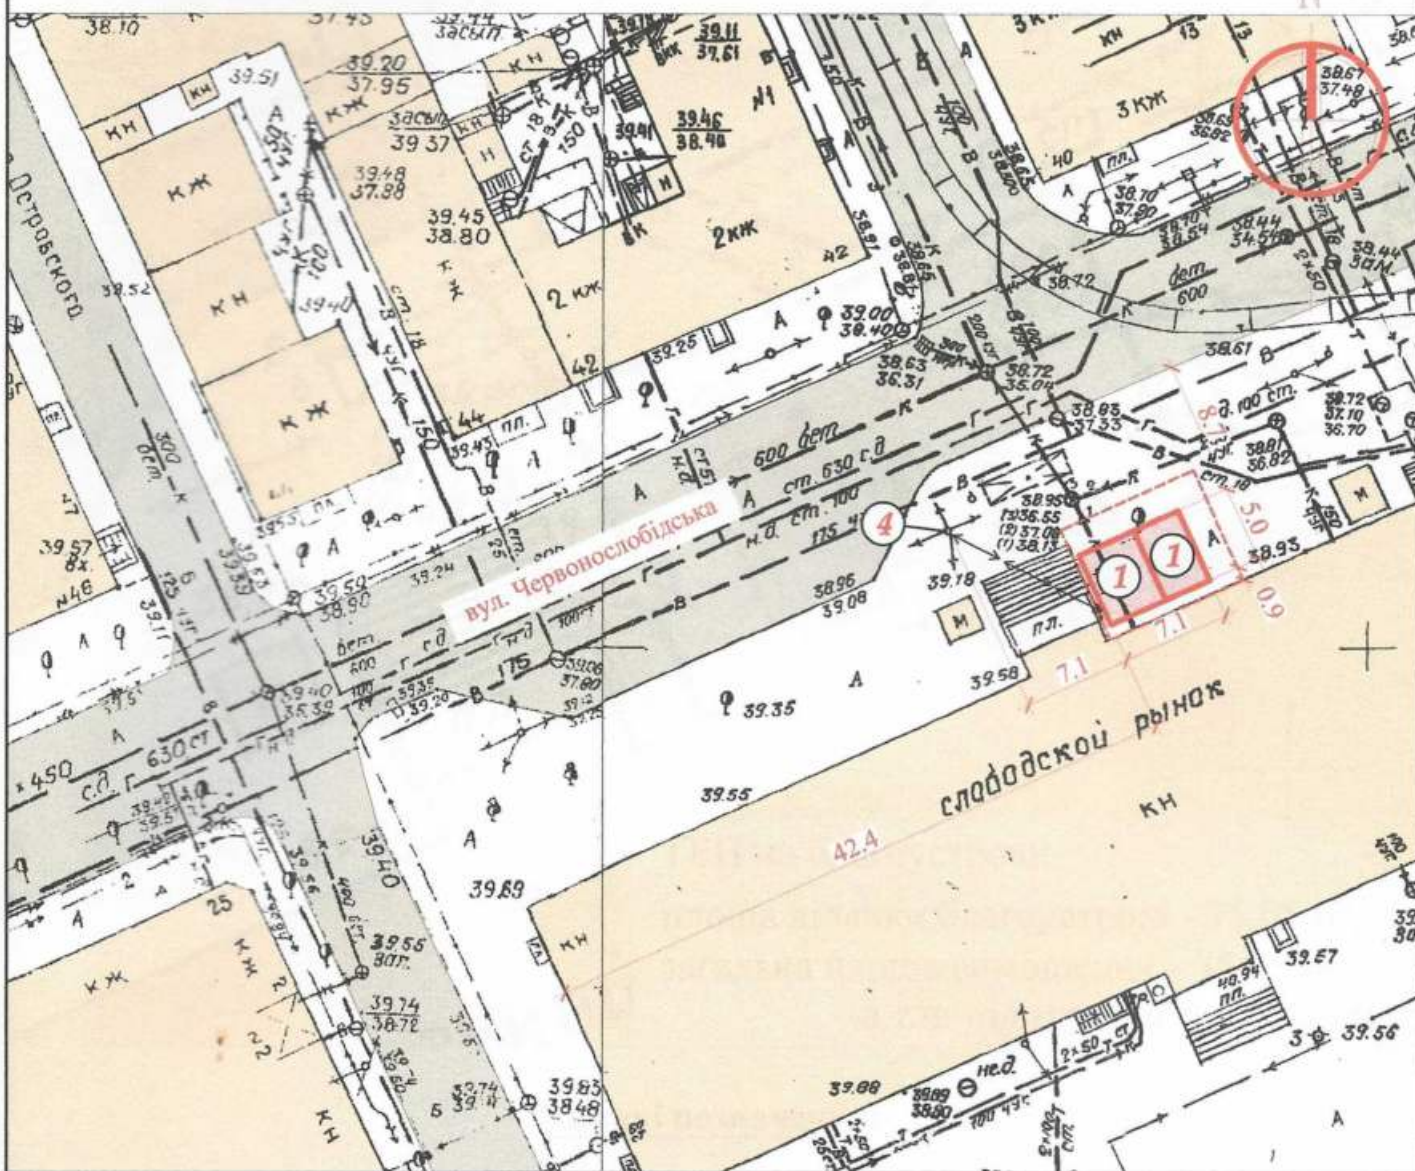

Експлікація:

- 1) місце розташування ТС;
- 2) червоні лінії;
- 3) лінії регулювання забудови;
- 4) місця підключення до інженерних мереж.

Умовні позначення:

- межа благоустрою ділянки розміщення ТС
- проектна ТС
- існуючі будівлі
- існуючі дороги

підключення до мереж електропостачання


В.о.директора ТОВ "АРХІТЕКс-ТУРИЯ"

В.В. Ситиченко

Головний інженер

Т.Т. Євченко

Кваліфікаційний сертифікат серія АА № 012191

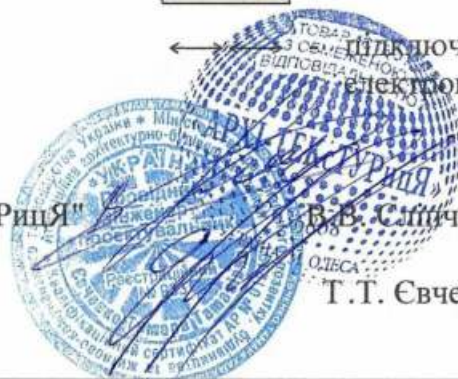

Ситуаційний план М 1:2000

Місце розміщення об'єкту

N



В.о.директора ТОВ "АРХТЕКс-ТУРиЯ"

В.В. Сліпченко

Головний інженер

Кваліфікаційний сертифікат серія АА № 012191

Г. Євченко

