

ПОЯСНЮВАЛЬНА ЗАПИСКА

1. Група тимчасових стаціонарних споруд призначена для здійснення підприємницької діяльності та має торговельні приміщення для тимчасового перебування людей.
- За умовну позначку ± 0.000 прийнятий рівень чистої підлоги ТС.
- Ступень вогнестійкості - III
- Габаритні розміри в плані ТС - 6.00 м. x 5.00 м.;
- У павільоні розташовано два приміщення площею по 13.68 кв.м.;
- Внутрішня висота павільону від рівня чистої підлоги складає - 2.50 м.
- Загальна висота павільону складає - 3.10 м.
- Ґрунт заснування, до встановлення ТС, ретельно утрамбовані щебнем та укладені асфальтобетонні покриття.
- Стіни споруд запроектовані товщиною 100 мм. із утеплювачем з мінеральної вати й обшивкою.
- Обшивка стін по каркасу: зовнішня - вентиляційні фасадні системи композитні матеріали типу "Алюкобонд"; внутрішня (стіни та стеля) - гіпсокартонні листи.
- Підлога з покриттям дошки 40 мм. по металевому каркасу і утеплювачем з мінераловатних плит та покриття з негорючого матеріалу.
- Покрівля - по металевим прогонам і решетуванню з покриттям із черепицею по орієнтовано-стружковій плиті "OSB", з утеплювачем з мінераловатних плит, гідро і пароізоляцією.

Зовнішня обробка:

- поверхні стін - композитні матеріали типу "Алюкобонд";
- вікна - металопластикові;
- двері - металопластикові;
- покрівля - бітумна черепиця;

2. Тимчасова споруда підключена до мереж електропостачання згідно з діючими нормами та ТУ. Точка підключення - близька опора, що розташована поряд з територією ділянки.

Опалювання-електричне з встановленням навісних електро-конвекторів з регулюванням температури.

Освітлення приміщення виконане стельовими світильниками з люмінесцентними лампами.

Розподільні мережі виконані проводами з мідними жилами, що прокладені у трубах то приховані в облицівці стін.

Мережі обрані по тривалодопустимим струмам навантаження.

Захист мереж від дії струмів коротких замикань та перевантажень здійснюється автоматичними вимикачами щитка.

3. Благоустрій прилеглої території виконується згідно з планом благоустрою. Освітлення території передбачене світильниками, що розміщуються на головному фасаді над входом у ТС.

Директор ООО "Альфа"

Госліцензія АД № 030757

Архітектор




М.В.Краєвська


В.Ю.Петрушина

ЕСКІЗИ ФАСАДІВ ТС, М 1:50

Фасад в осях "1"- "2"

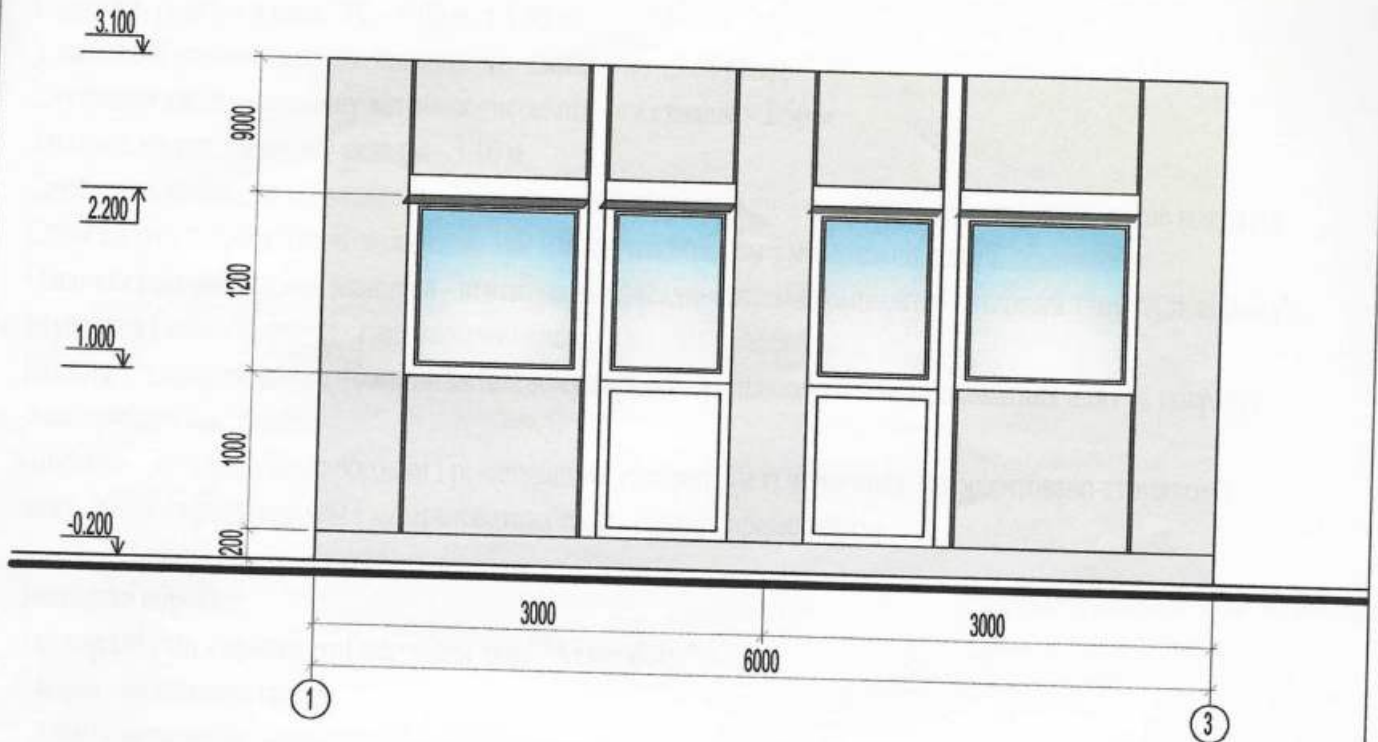

Фасад в осях "А"- "Б"

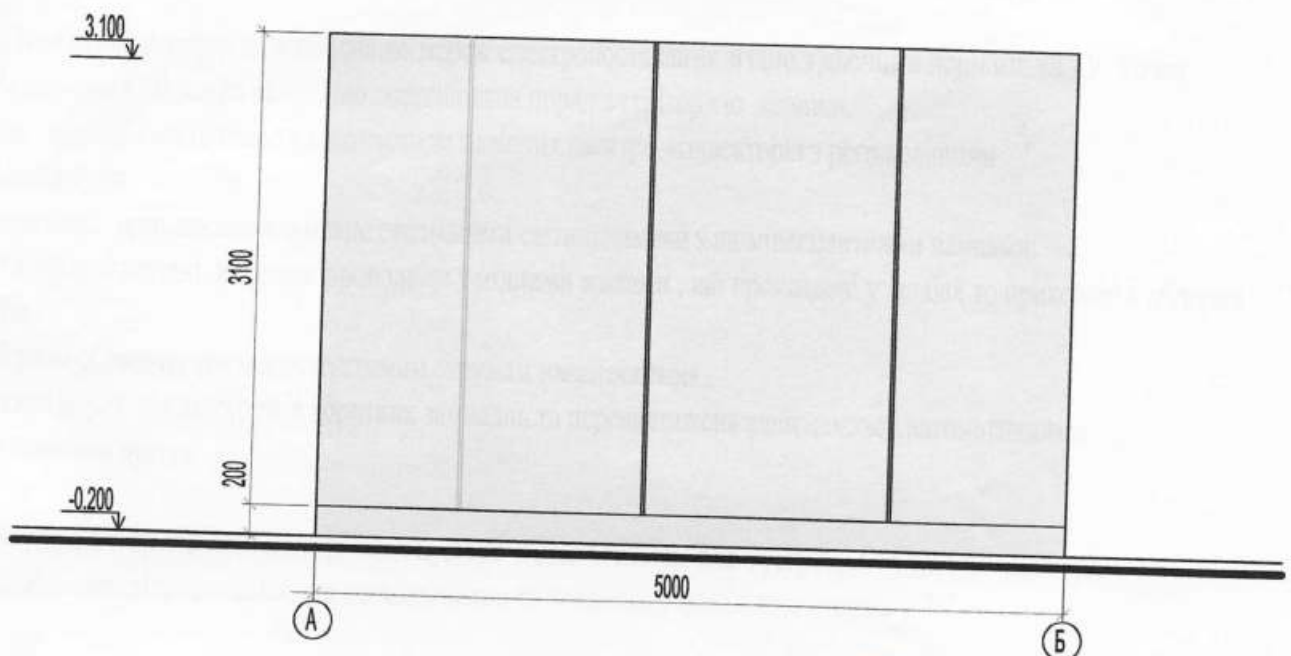


Директор ООО "Альфа"
Госліцензія АД № 030757

Архітектор



М.В.Краєвська

В.Ю.Петрушина

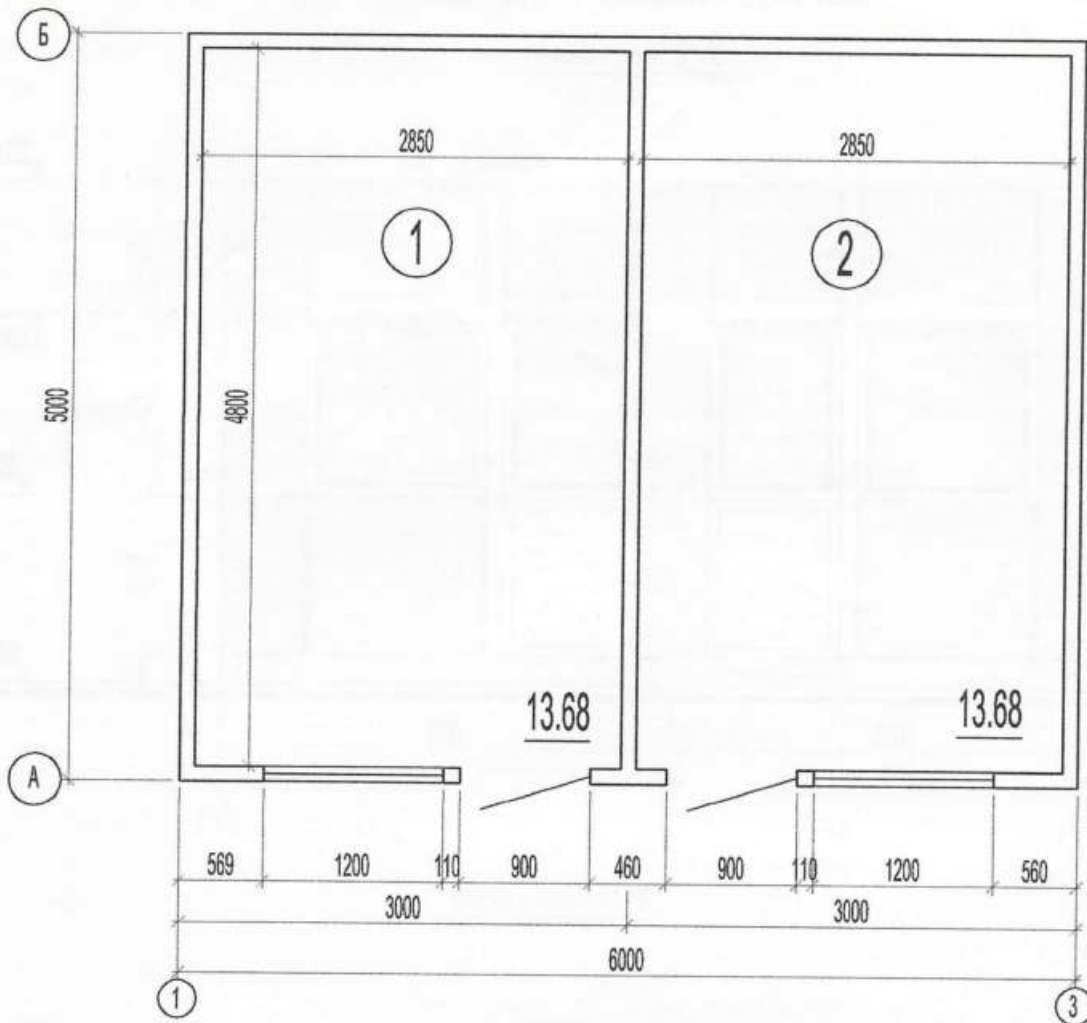

Експлікація

№/№ по плану	Найменування	Площа м2
1	Торгівельне приміщення	13.68
2	Торгівельне приміщення	13.68
	Загальна площа	27.36
	Площа застройки	30.00

Директор ООО "Альфа"
Госліцензія АД № 030757


Архітектор



М.В.Краєвська

В.Ю.Петрушина

Площа земельної ділянки згідно з документами
на землекористування - землі міста.

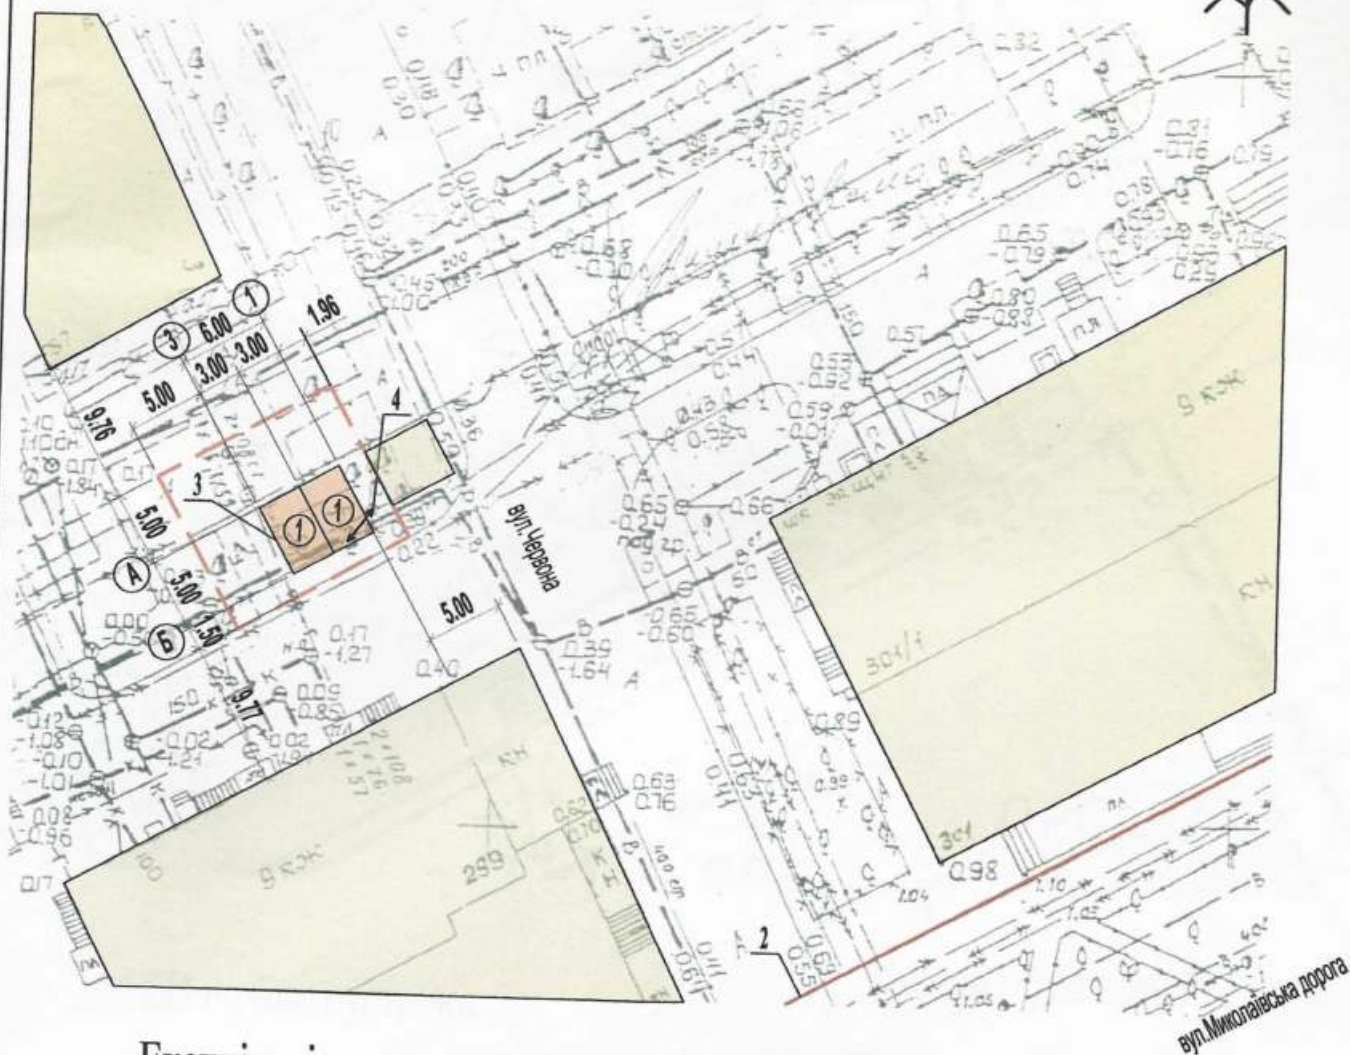

- 1) місце розташування групи ТС;
- 2) червоні лінії;
- 3) лінії регулювання забудови;
- 4) місця підключення до інженерних мереж;

- - межа благоустрою ділянки розміщення групи ТС
- - проектна група ТС
- - існуючі будівлі
- - підключення до мереж електропостачання

Директор ООО "Альфа"
Гослицензия АД № 030757


Архітектор



М.В.Краєвська

В.Ю.Петрушина

Ситуаційний план, М 1:2000

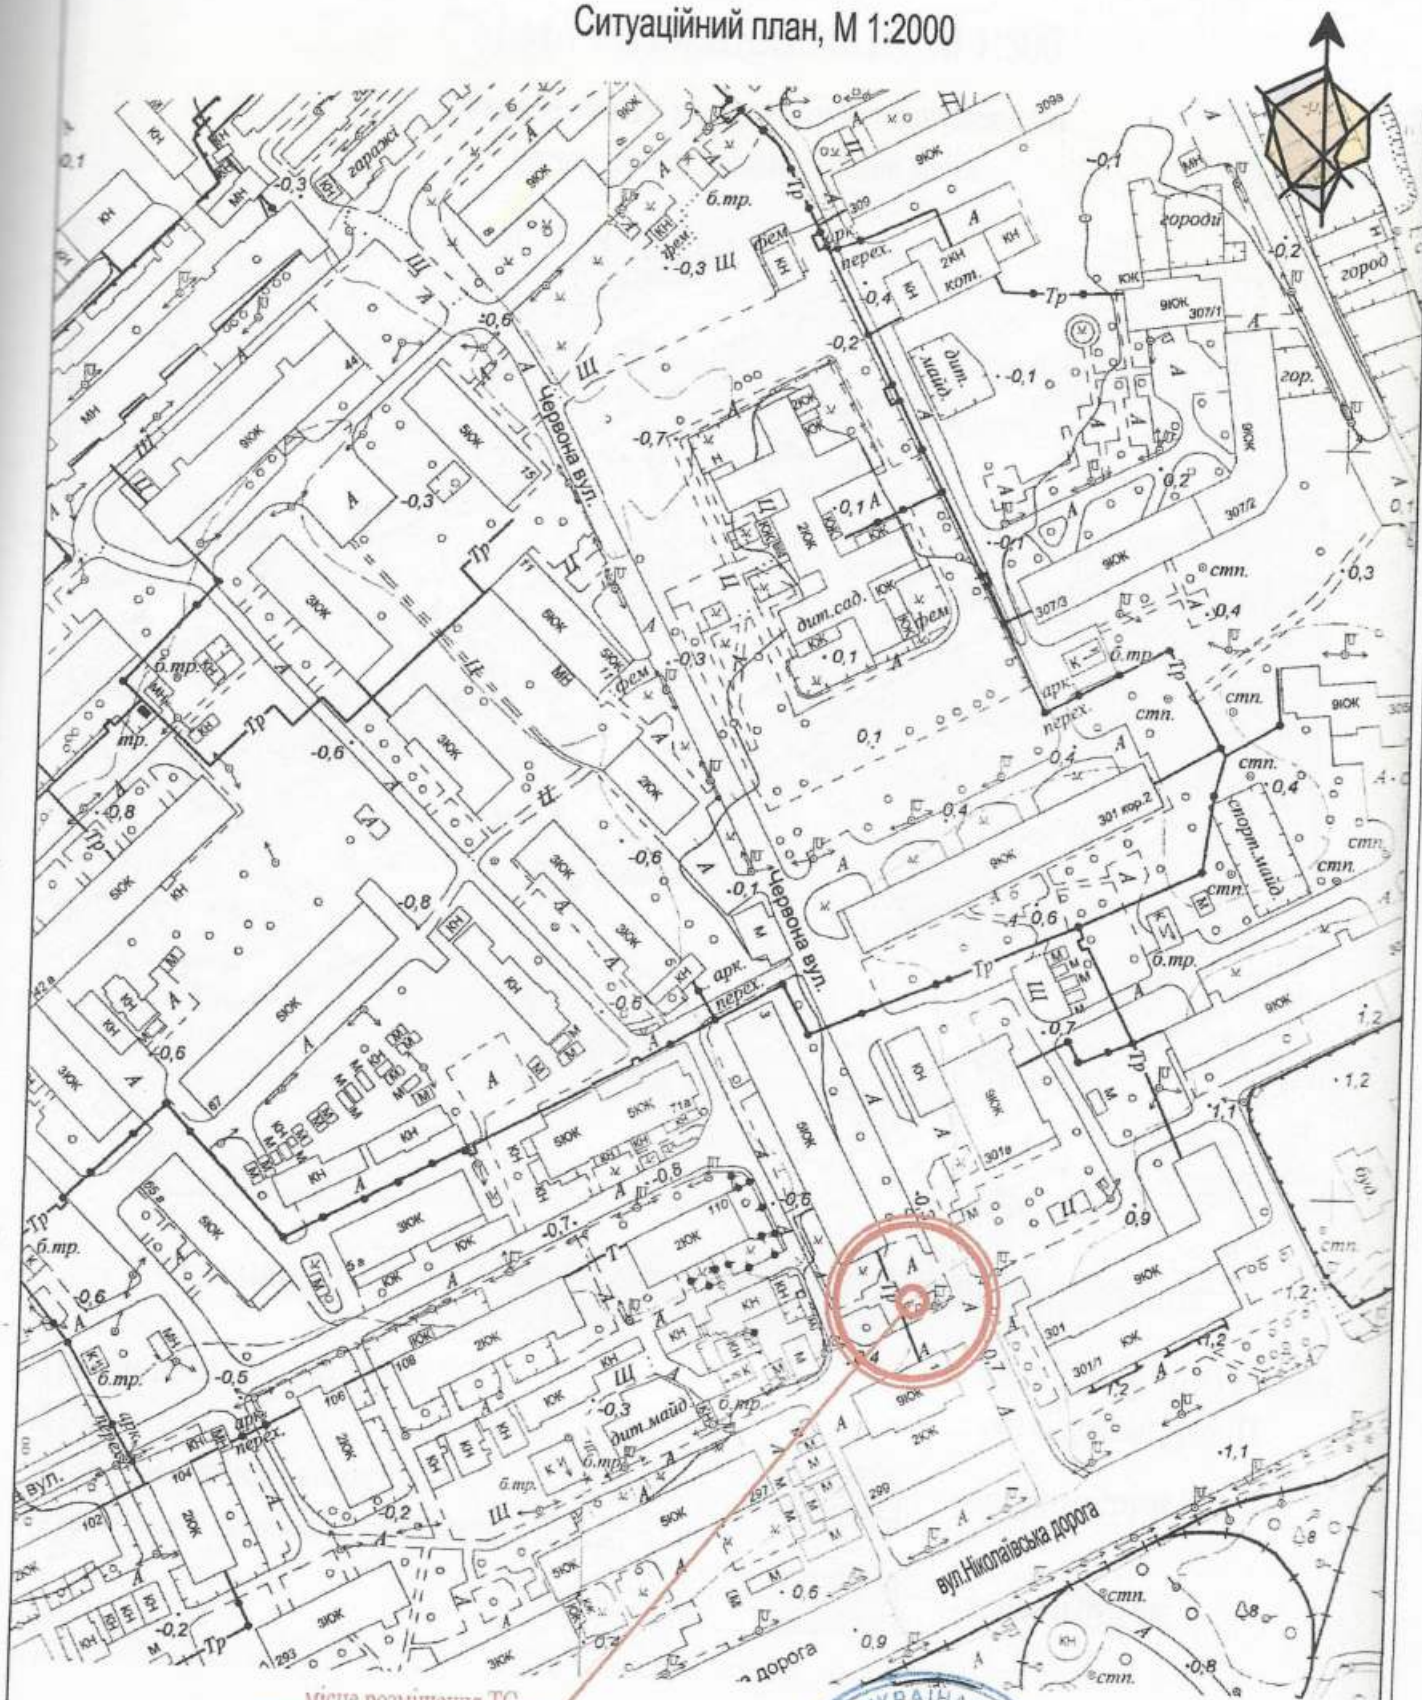

місце розміщення ТС

Директор ООО "Альфа"

Госпідприємство АД № 030757

Архітектор



М.В. Краєвська

В.Ю. Петрушина