

ПОЯСНЮВАЛЬНА ЗАПИСКА

1. Тимчасова споруда являє собою одноповерхову споруду, яка виконується зі збірно-розбірних металевих конструкцій та встановлюється безпосередньо на існуюче покриття.

За умовну позначку 0,000 прийнятий рівень чистої підлоги ТС.

Ступінь вогнестійкості тимчасової споруди III а.

Габаритні розміри в плані – 4,8 X 2,8 м.

Висота павільйону від рівня землі – 3,30 м.

Запроектований ТС має вхід з головного фасаду. Торгівля передбачається в приміщенні відкритого типу.

Стіни споруди запроектовані по типу "Сендвич" товщиною 100 мм із утеплювачем з мінеральної вати й обшивкою. Обшивка стін по каркасу: зовнішня – алюмінієві сандвіч панелі; внутрішня (стіни й стеля) – металопластикові вагонки.

Підлоги передбачені з покриттям дошки 40 мм і утеплювачу та покриттям з негорючого матеріалу.

Заповнення прорізів з метало пластикового профілю та рольгратами.

Покрівля – по металевих прогонах і решетуванню з покриттям із профільованого сталевих листа, з утеплювачем з мінераловатних плит, гідро- і пароізоляцією.

Водостік передбачити зовнішній організований по жолобах і ринвам.

Зовнішня обробка:

Поверхні стін – колірні алюмінієві сандвіч панелі, типа «Алюкобонд»;

Вікна – металопластикові;

Двері – металопластикові;

Покрівля – профільований сталевий лист;

Цоколь – колірні алюмінієві сандвіч панелі

Колірне вирішення фасадів дивись графічний додаток.

Внутрішню обробку виконати згідно індивідуального дизайну-проекту із застосуванням негорючих оздоблювальних матеріалів, з підтвердженням сертифікатом.

2. Підключення до інженерних мереж:- тимчасова споруда підключається до існуючої електромережі, згідно договору про постачання електричної енергії.


Опалювання – електричне з встановленням навісних електро - конвекторів з регулюванням температури.

Освітлення приміщення виконане стельовими світильниками з люмінесцентними лампами.

Назва об'єкта, адреса розміщення Тимчасова споруда (стаціонарна) пр. Добровольського, 159 (згідно схеми посадки)	Посада виконавця	ПІБ	Підпис
	Архітектор	Давидова В.В.	
М.П.	Кваліфікаційний сертифікат, серія АА № 002057		

ФАСАДИ В ОСЯХ 1-2
М 1:50

ФАСАДИ В ОСЯХ А-Б
М 1:50

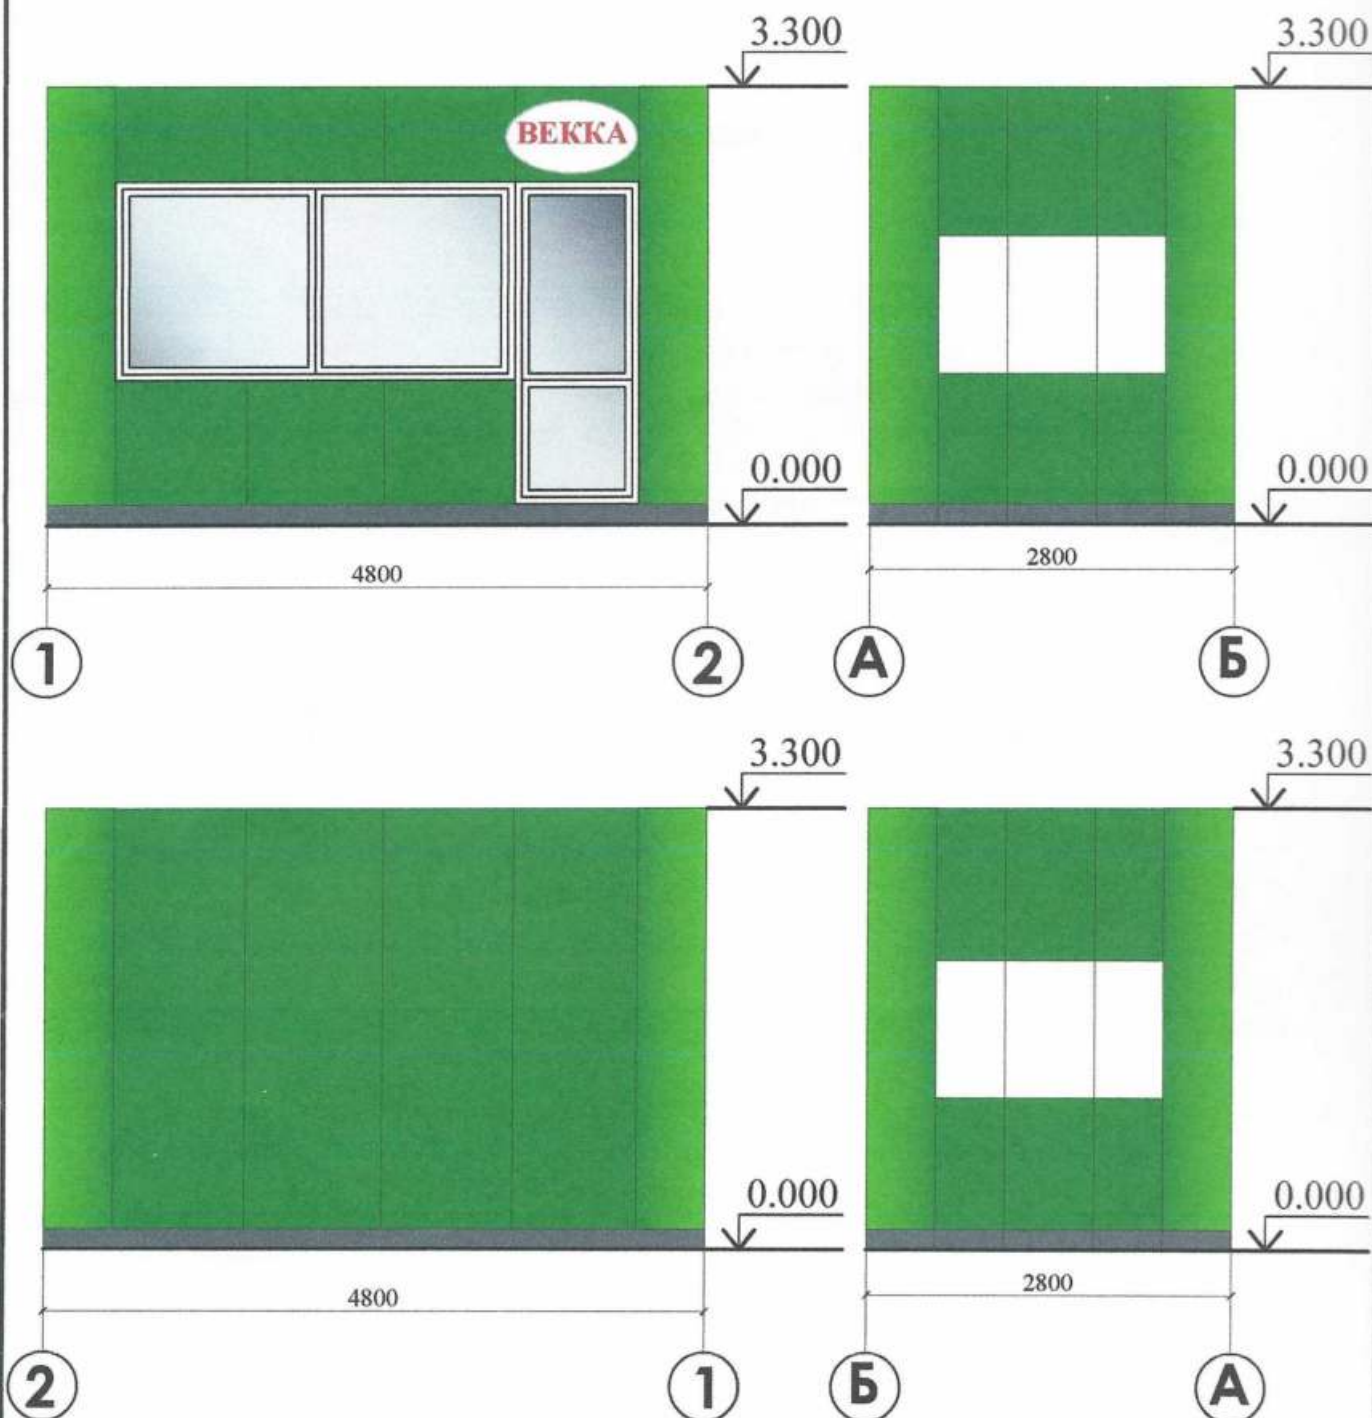

Тимчасова споруда - (заг. площею 13,44 кв.м.) по
продажу товарів змішаної групи за адресою:
м. Одеса, проспект Добровольського, 159

Посада виконавця

ПІБ

Підпис

Архітектор


Давидова В.В.

М.П.

Кваліфікаційний сертифікат, серія АА № 002057

Дата складання _____ 20 ____ року


ПЛАН НА ОТМ. 0.000

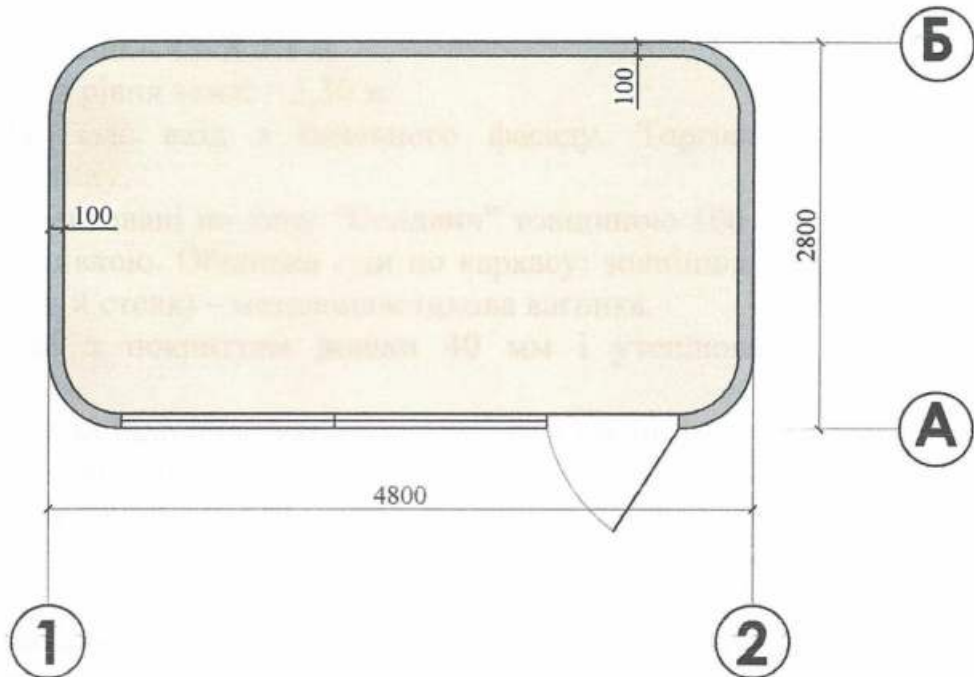

 Тимчасова споруда (заг. площею 13,44 кв.м.) по продажу товарів змичаної групи за адресою: м. Одеса, проспект Добровольського, 159 М.П.	Посада виконавця	ПІБ	Підпис
	Архітектор	Давидова В.В.	
Кваліфікаційний сертифікат, серія АА № 002057			
Дата складання _____ 20__ року			

СХЕМА РОЗМІЩЕННЯ ТС М 1:500

Документи на землекористування відсутні

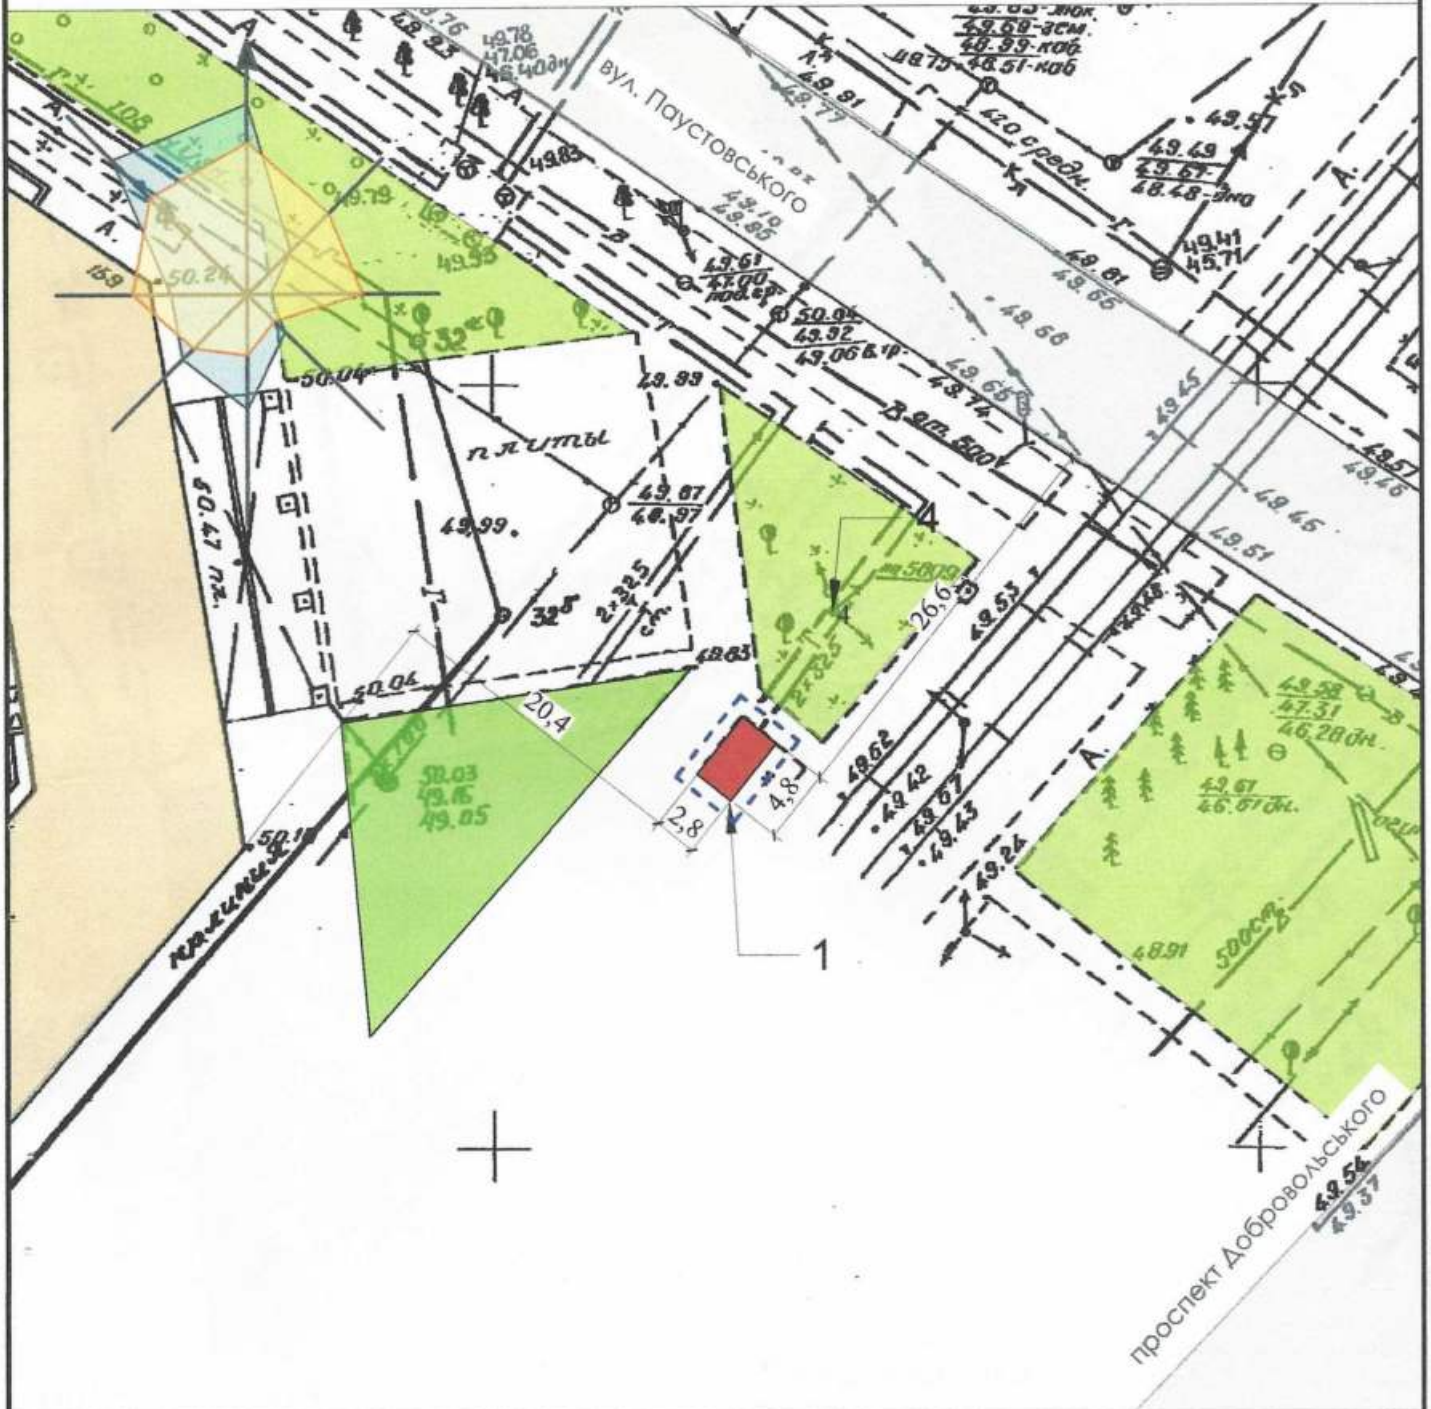

Експлікація:

- 1) місце розташування ТС;
- 2) червоні лінії;
- 3) лінії регулювання забудови;
- 4) місця підключення до інженерних мереж.

Умовні позначення


- Існуючі споруди
- Озеленення
- Тимчасова споруда
- Територія, що підлягає благоустрою



Посада виконавця	ГПБ	Підпис
Архітектор	Давидова В.В.	
Кваліфікаційний сертифікат, серія АА № 002057		
Дата складання _____ 20__ року		

СИТУАЦІЙНИЙ ПЛАН

М 1:2000

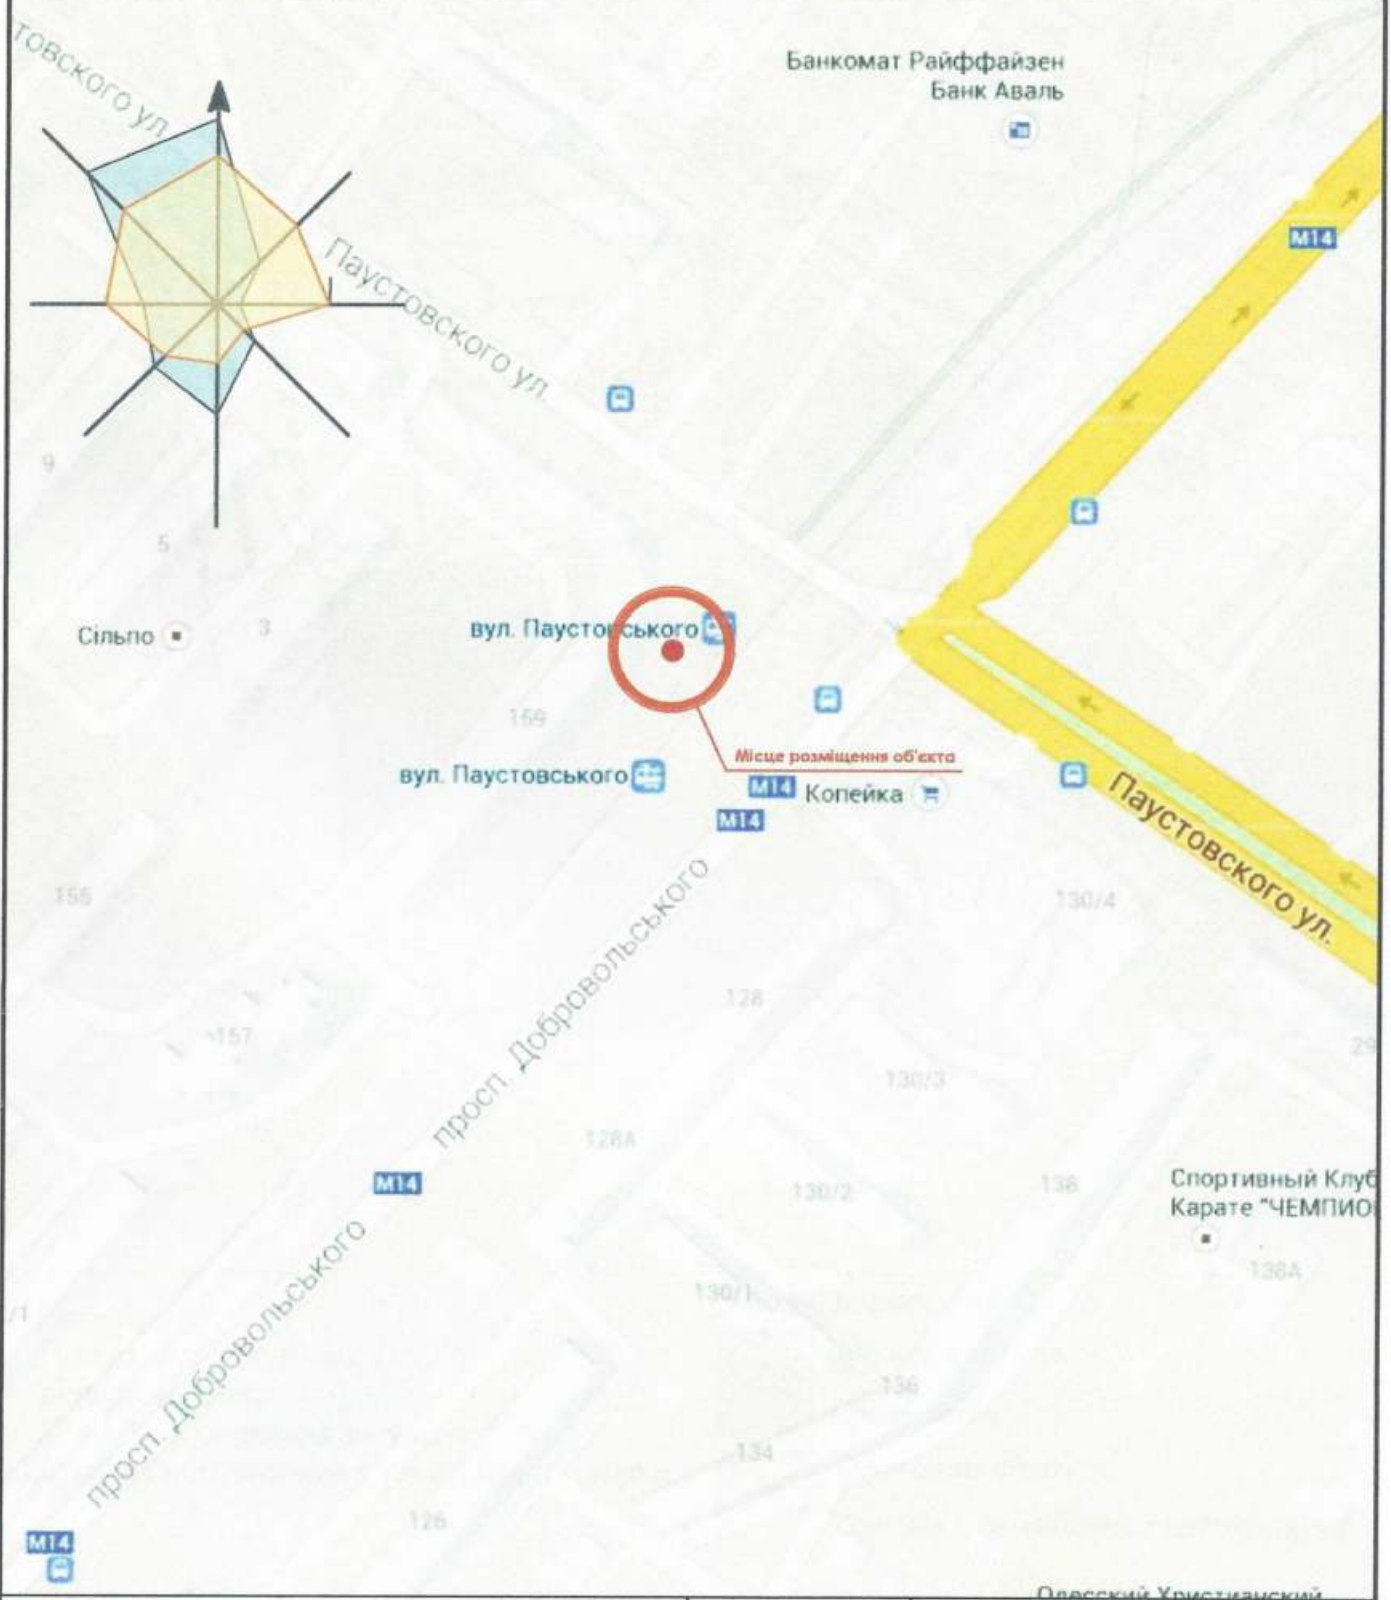

Тимчасова споруда - (заг. площею 13,44 кв.м.) по продажу товарів змішаної групи за адресою: м. Одеса, проспект Добровольського, 159	Посада виконавця	ГПБ	Підпис
	Архітектор	Давидова В.В.	
М.П.	Кваліфікаційний сертифікат, серія АА № 002057		
	Дата складання ____ 20__ року		