


СТИСЛА ПОЯСНЮВАЛЬНА ЗАПИСКА

1. Стационарна тимчасова споруда для здійснення підприємницької діяльності ФОП Жуков О.М., розташована за адресом: вул. Семена Гірного (Дніпропетровська дорога), 125.
Ступінь вогнестійкості — IIIа.
Габаритні розміри ТС в осях 1-4; А-Г- 8,8м x 3,95м.
Загальна висота ТС - 2,95 м.
Площа забудови ТС — 25,65 м².
Загальна площа ТС — 23,13 м².
ТС встановлюється без закладення фундаменту на існуючому асфальтобетонному покритті.
Основні конструкції виконані по металевому каркасу.
Стіни споруди виконані по типу «Сендвич», товщиною 100мм з утепленням та обшивкою.
Зовнішня обробка - Алюмінієві композитні панелі Ukabond 3 021 Г2 R.
Утеплювач - «Ізовер» по розрахунку.
Внутрішня обробка: стін — гіпсокартоні конструкції, підшивка стелі — гіпсокартон.
Підлога в приміщенні - утеплений лінолеум.
Покрівля — по металевим прогонам і решетуванню з покриттям із профільованого сталевих листа, з утеплювачем з мінераловатних плит з гідро- та пароізоляцією.
Віконні та дверні отвори заповнено металопластиковими блоками з енергозберігаючими властивостями.
Несучі конструкції покриття - металеві ферми.
2. Стационарна тимчасова споруда забезпечена електроконвекторами для підключенням к існуючим внутрішньоквартальним мережам.
Підключення — опора, що розташована поряд з ТС.
Освітлення приміщень виконане стельовими світлодіодними світильниками.
Для урахування електроенергії на вводі встановлено вводно - лічильний пристрій типу ПВУ.
Захист мереж від дії струмів коротких замикань і перенавантаження здійснюється автоматичними вимикачами щитка.
Електропостачання - згідно договору про користування електричною енергією з ВАТ «Одесаобленерго», та відповідно ТУ.
3. Благоустрій прилеглої території виконується згідно з планом благоустрою території.
Освітлення території передбачене світильниками, що розміщуються на головному фасаді ТС.

Вит. № 001/16	Рішення / Дата	Візнав. Вит. № 001/16

Ескіз фасадів ТС М 1 : 50


Бічний фасад

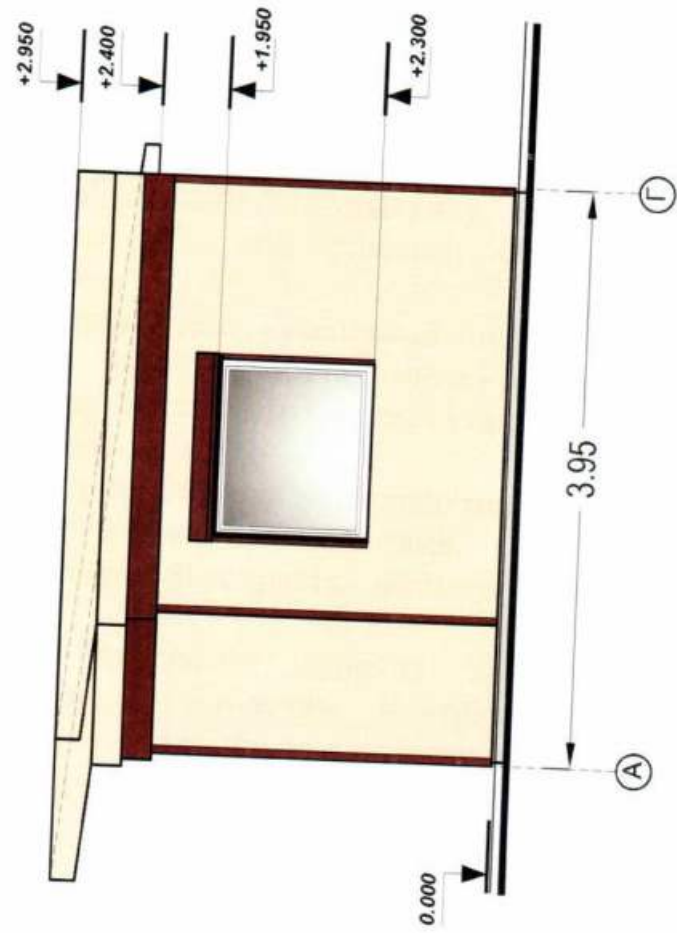

Керівник ПП "ОДЕСЬКЕ БІТІ" Г.Г. Шеремета
Архітектор Лукин Д.Е.
ІНСТРУМЕНТ № 003910 від 31.08.2017р.

Дата складання 31.08.2017 року

ПЛАН ПРИМІЩЕННЯ М 1 : 50

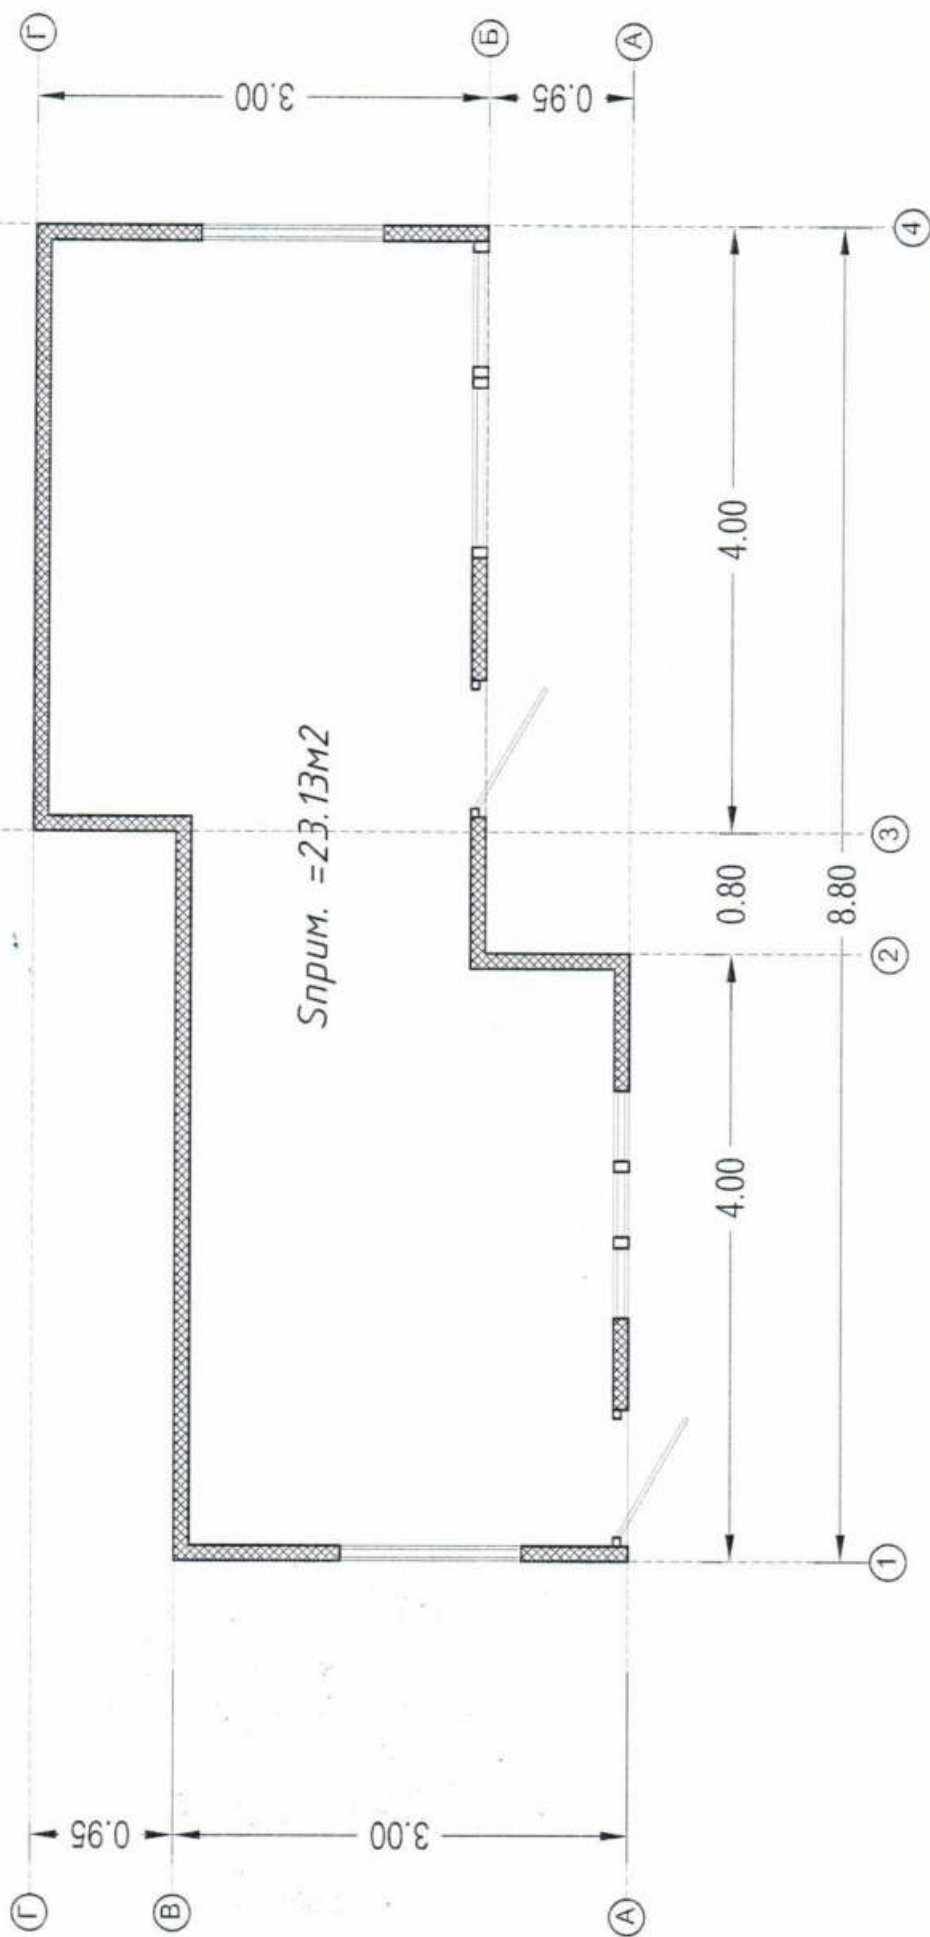


Квал. сертифікат серії
АА № 003910 від 31.08.2017р


Дата складання 20

СХЕМА розміщення ТС М 1 : 500

Площа земельної ділянки згідно з документами на землекористування - землі міста

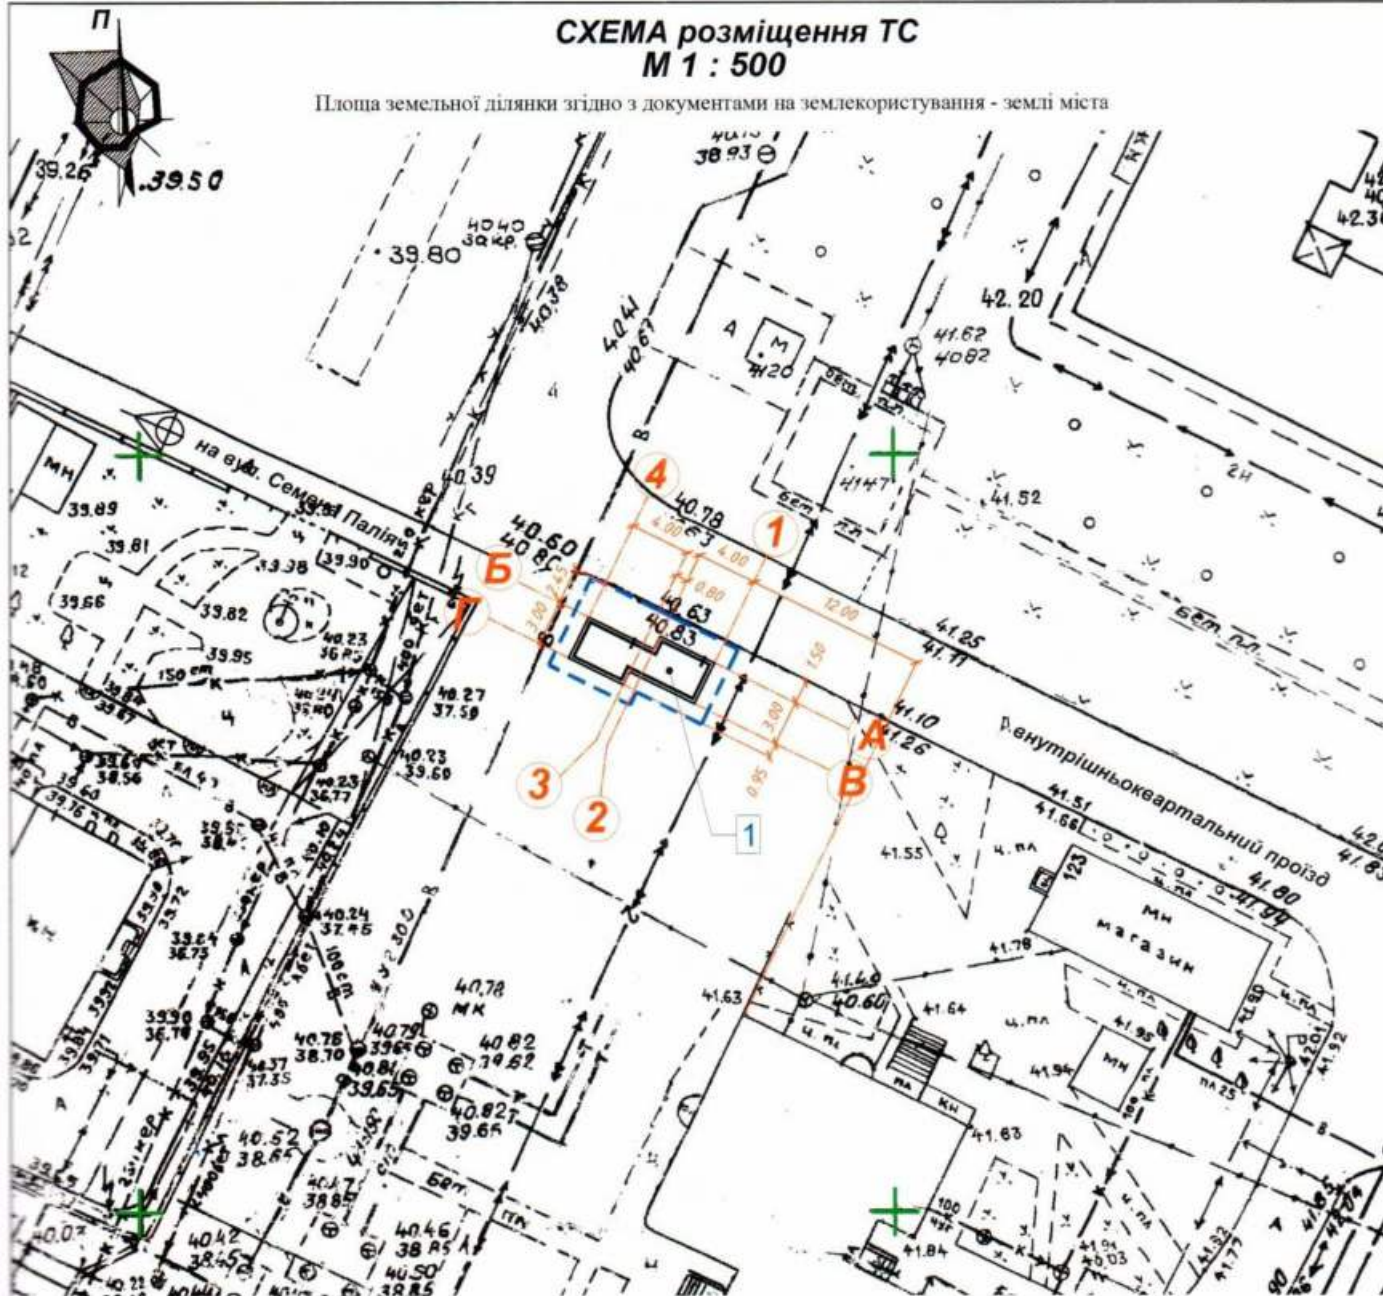

УМОВНІ ПОЗНАЧЕННЯ

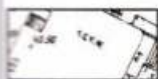


- Існуючі споруди, будівлі



- Існуючі дороги, проїзди



- Існуючі споруди для провадження підприємницької діяльності (ТС)

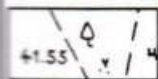

- Озелення (існ.)

- Мережі телекомунікацій
- Умовні межі благоустрою
- Дороги, під'їзди, пішохідні доріжки (існ.)
- Лінії електромереж
- В — Мережі Водопостачання
- Г — Мережі газопостачання
- К — Мережі комунальної каналізації
- Т — Мережі теплопостачання

ЕКСПЛІКАЦІЯ

1. місце розташування ТС - ФО-П Жуков О.М.
2. червоні лінії
3. лінії регулювання забудови
4. місця підключення до інженерних мереж
(ТУ отримуються самостійно у балансоутримувача відповідних мереж)

Керівник ПП "ОДЕСЬКЕ БТ"

Кармаліта Г.Г.

Архітектор
Лукін С.Б.

Квал. сертифікат серії


АА № 003910 від 31.08.2017р

Дата складання

20 року

СИТУАЦІЙНА СХЕМА

Градостроительный кадастр

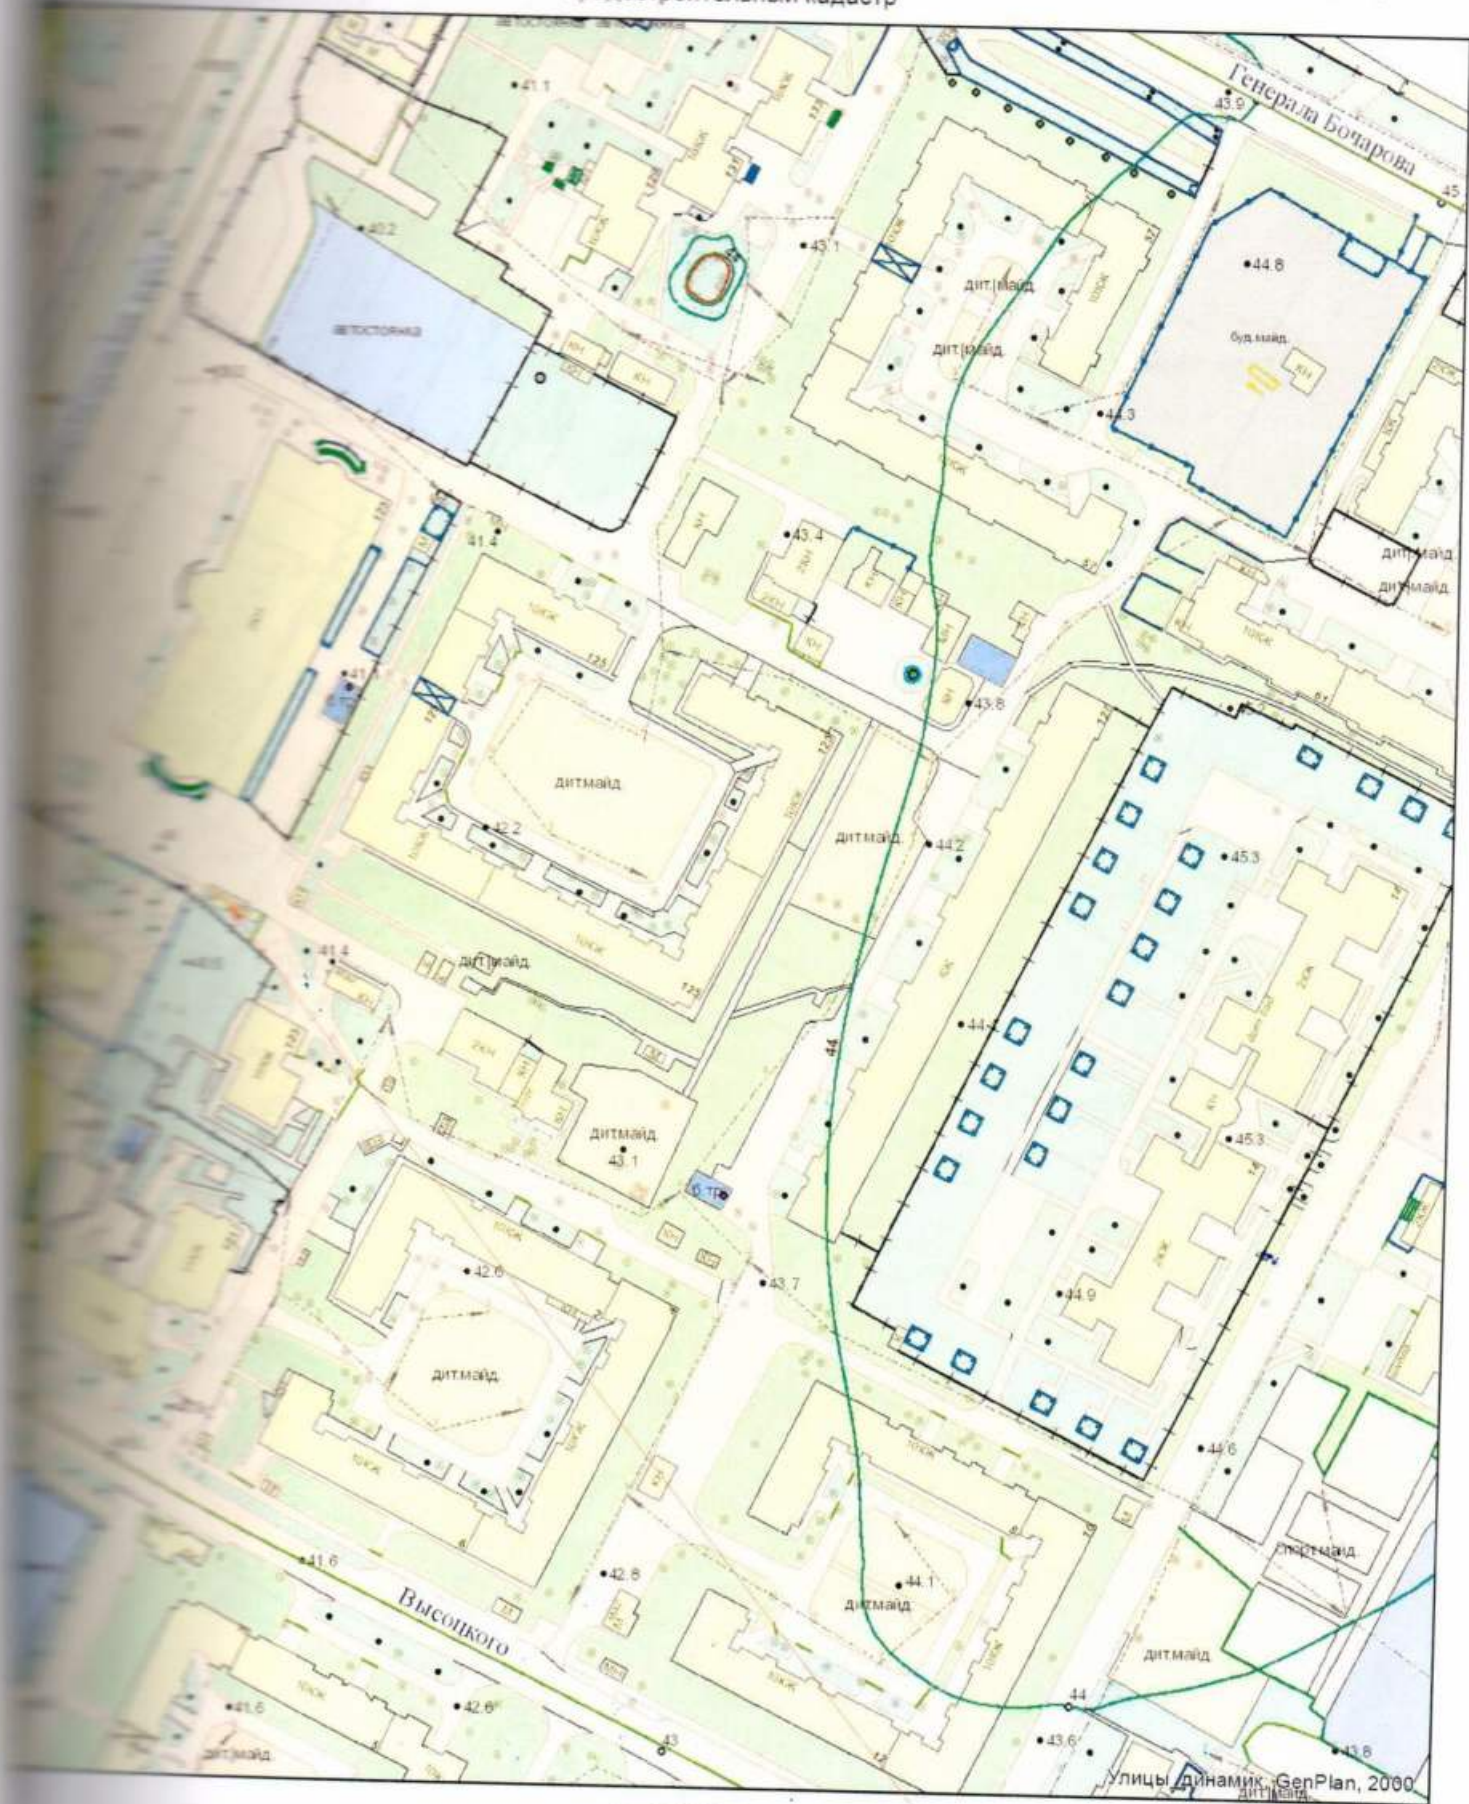

1:2000

Місце розміщення
ТС для ФО-П Жуков О.М.