

Пояснювальна записка

Група стаціонарних тимчасових споруд (далі - ТС) складається з п'яти кіосків, зблокованих між собою.

Група ТС встановлюється на ділянці, яка розташована у Суворовському районі міста Одеси за адресою:
просп. Добровольського, 98.

Тимчасова споруда - торгівельного призначення для здійснення підприємницької діяльності. Кожна з ТС, що підлягає встановленню, уявляє собою одноповерховий об'єм, який має одне приміщення, що використовується для розміщення торгівельного обладнання.

Вхід для відвідувачів до приміщення не передбачається.

ТС встановлюється без улаштування фундаменту на покриття, виконане по ретельно ущільненому ґрунту основи.

Ступінь вогнестійкості ТС - IVa.

ТС - прямокутна в плані, з зовнішніми габаритними розмірами 2,00 x 2,025 x 3,05 (Н) м.

Площа приміщення ТС встановлює 3,90 м².

За умовну позначку 0,000 прийнятий рівень чистої підлоги ТС.

Внутрішня висота приміщення від рівня чистої підлоги до стелі складає 2,70 м.

Огороджувальні конструкції ТС виконуються з полегшеного металевих каркасу з зовнішньою обшивкою сталевими профільованими листами.

Товщина стін складає 50 мм.

Внутрішня обшивка стін та стелі виконується з плит ДСП.

Покрівля виконується по металевому каркасу з покриттям з профільованих сталевих листів.

Покриття підлоги - лінолеум по листам ДСП, які укладаються по металевому каркасу.

Головний фасад перекривається у неробочий час металевою ролетною конструкцією, закріпленою вздовж всього фасада.

При встановленні ТС всі існуючі зелені насадження підлягають збереженню.

Зовнішня обробка :

Поверхні стін - металеві профільовані листи забарвлені;

Покриття покрівлі - профільовані сталеві листи.

Інженерне обладнання:

Стаціонарна тимчасова споруда підключається до мереж електропостачання згідно з діючими нормами та ТУ. Кожна тимчасова споруда розглядаємої групи оснащується лічильником електроенергії.

Освітлення приміщення виконується стельовими світильниками з люмінесцентними лампами.

Зовнішнє освітлення планується світильниками, закріпленими на опорах, розташованих на території ділянки.

Опалення приміщень кіосків не передбачається.

Точка підключення до мереж електропостачання - найближча опора, що розташована на території ділянки.

ТЭП :

Площа умовного благоустрою - 44,25 м²

Площа забудови - 20,25 м²

Площа мостіння - 24,0 м²

Директор КП "Одеспроект"


Архітектор




Ткаченко Н.Б.

Ескізи фасадів

Головний фасад ТС М 1 : 50

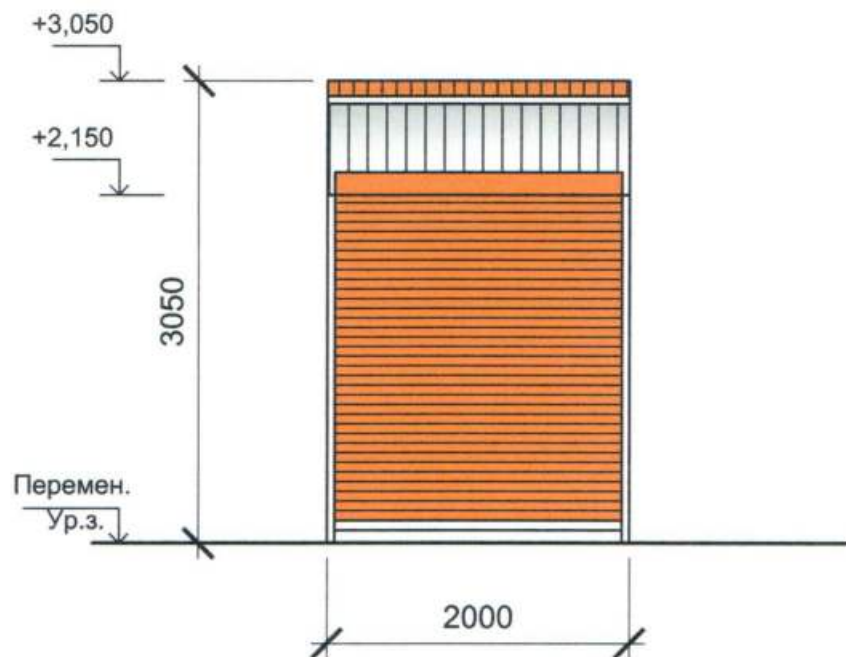

Боковий фасад ТС М 1 : 50

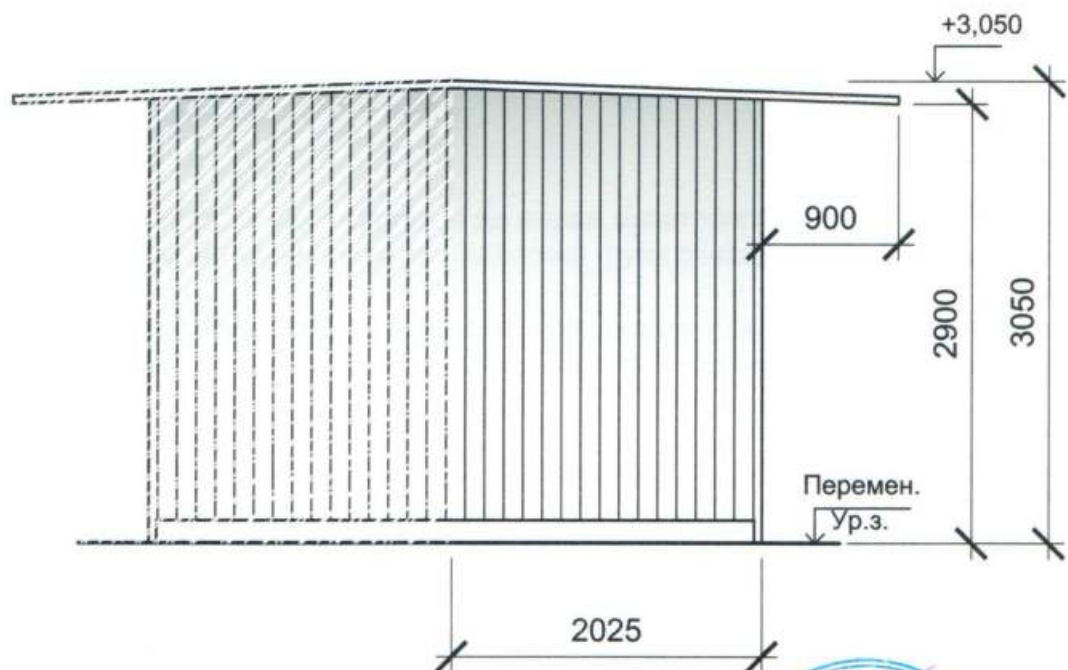


Директор КП "Одеспроект"

Архітектор



Ткаченко Н.Б.

План ТС
М 1 : 50

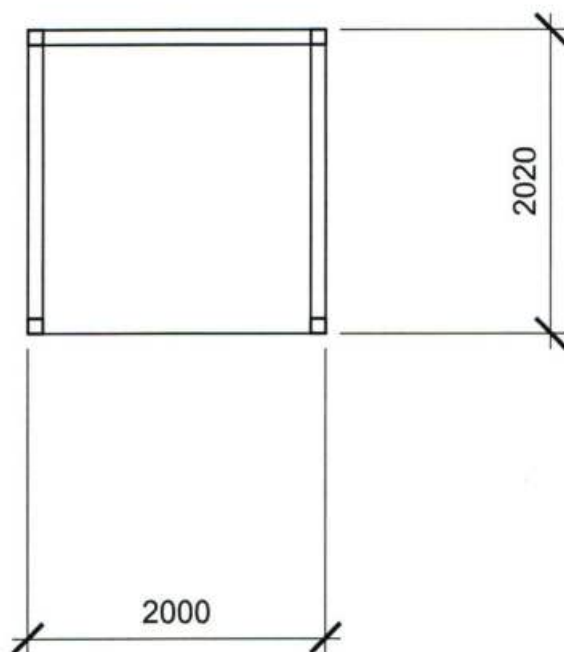


Директор КП "Одеспроект"

Архітектор




Муріна С.Ю.

Ткаченко Н.Б.

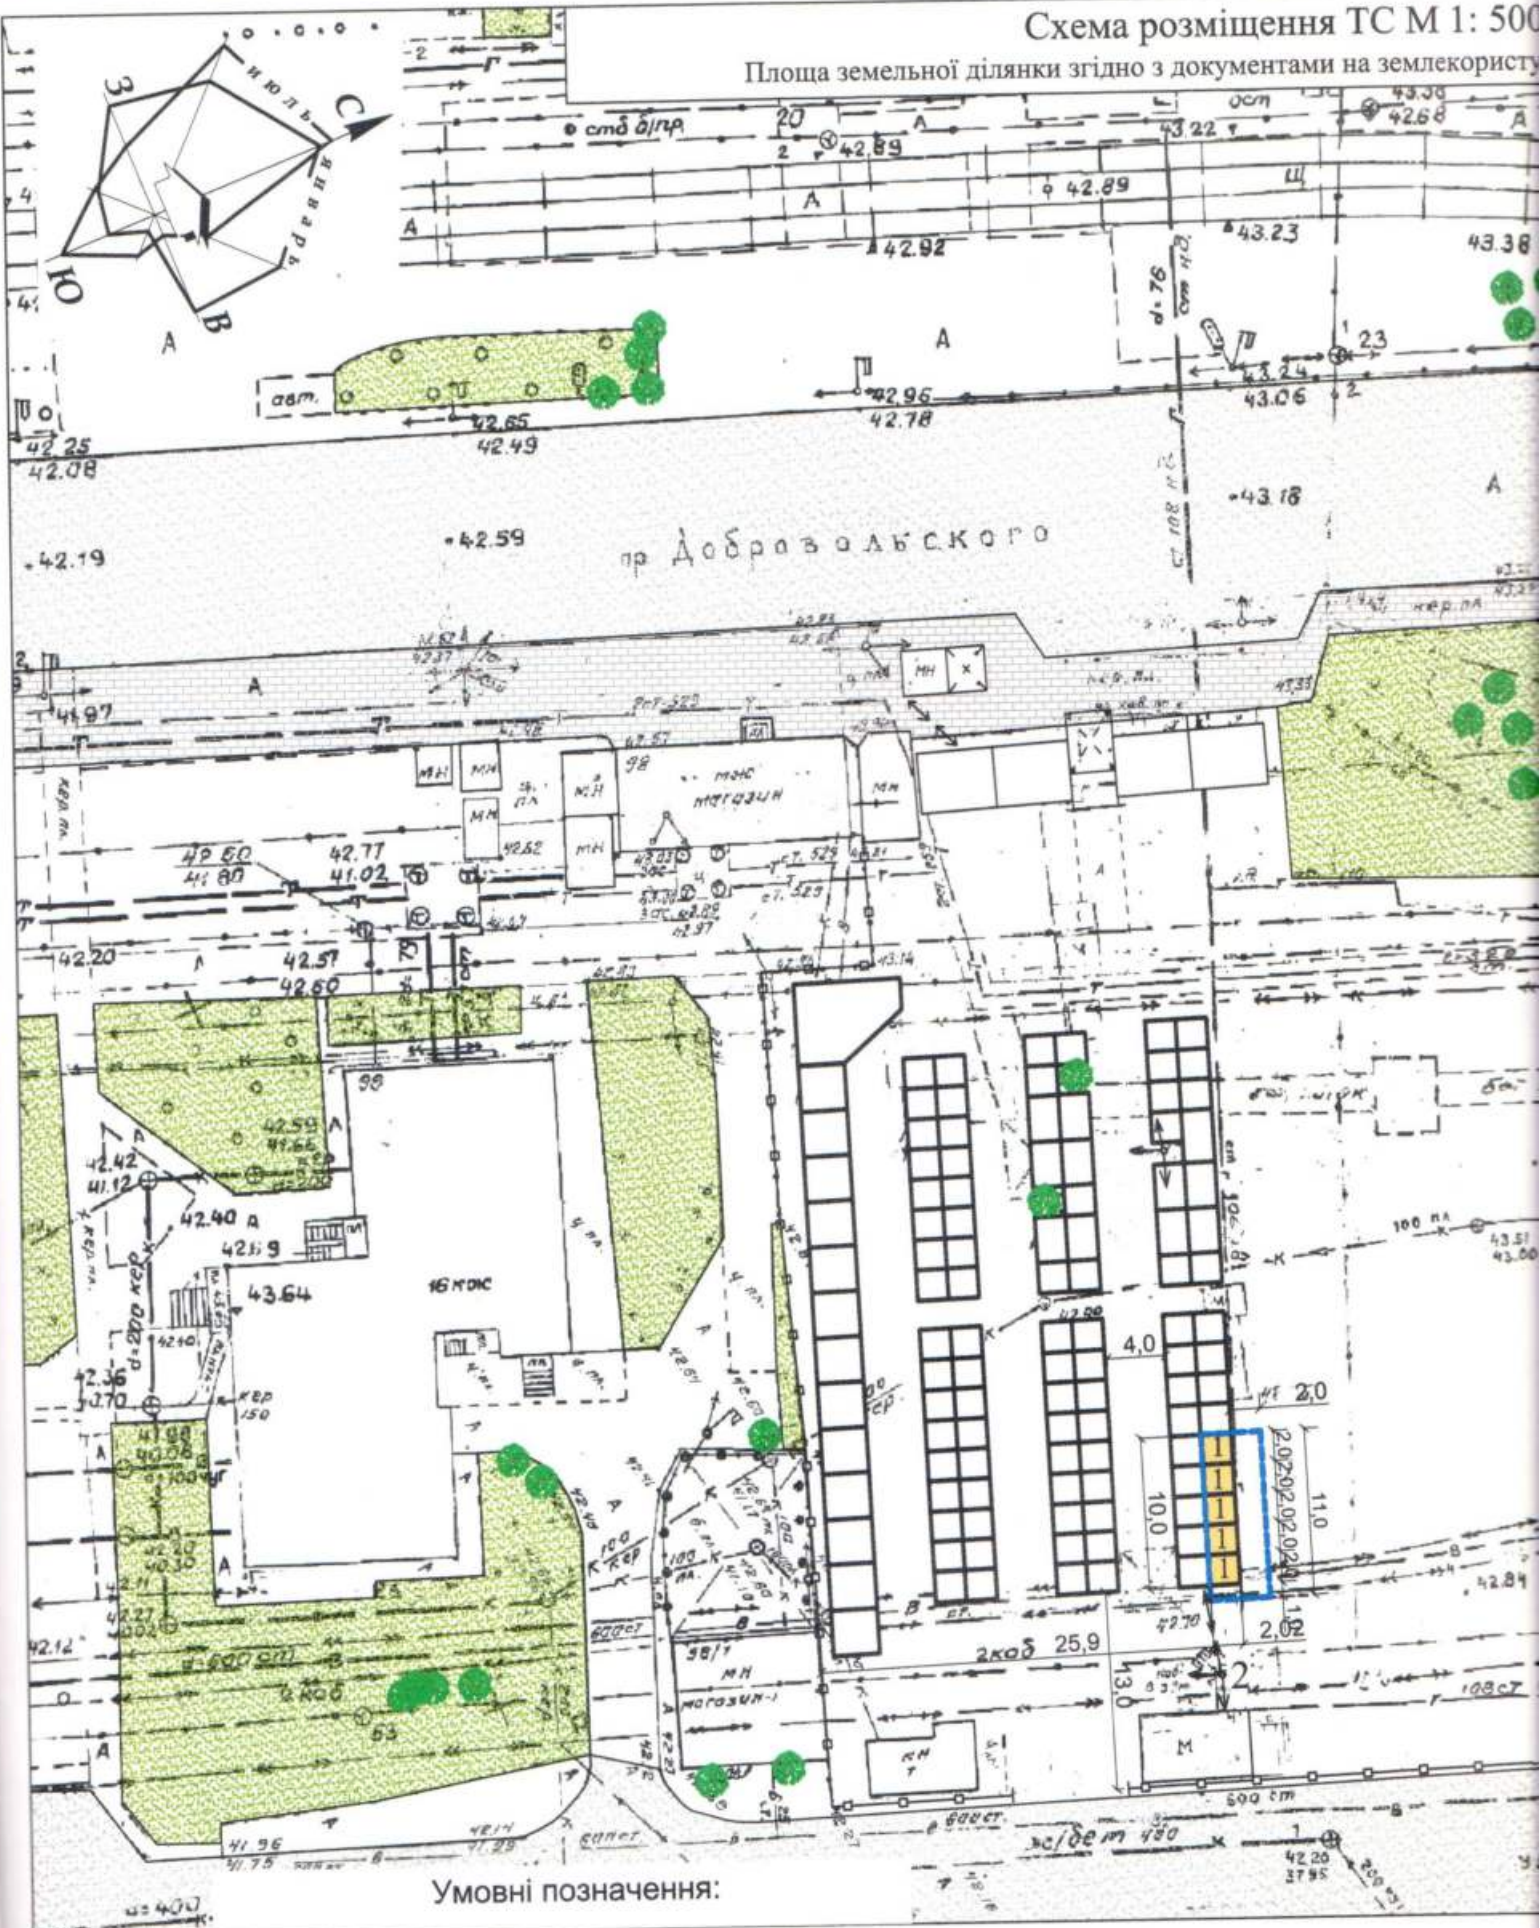

Умовні позначення:

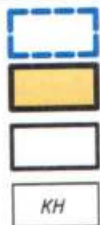

межа благоустрою ділянки розміщення ТС
проектна ТС, призначена до розміщення
проектна ТС
існуючі будівлі і споруди



існуюче мостіння
автодорожнє покриття
озеленення
підключення до мереж електропостачання

1:500

риштування землі міста



Експлікація:

- 1 - Місце розташування Т
- 2 - Місце підключення до інженерних мереж

Директор КП "Одеспроект"

Архітектор

чання



M 1: 2000

