

СТИСЛА ПОЯСНЮВАЛЬНА ЗАПИСКА.

1. Стационарна тимчасова споруда (ТС) для здійснення підприємницької діяльності має приміщення для короткочасного перебування людей .

Ступі вогнестійкості IIIa.

За умовну позначку ± 0.000 прийнятий рівень чистої підлоги.

Габаритні розміри тимчасової споруди в плані 5.8 x 4.8 м.

Загальна площа ТС - 28,0 м²

Загальна площа твердого покриття - 69,0 м².

Внутрішня висота від рівня чистої підлоги складає - 2,8 м.

Споруда встановлюється тимчасово, без влаштування фундаментів.

Грунт заснування, до встановлення ТС, ретельно утрамбовується щебнем та вкладається бетонна тротуарна плитка.

Стіни споруди запроектовані товщиною 100мм із утеплювачем з мінеральної вати та ошивкою з обох сторін.

Обшивка стін по каркасу. Фасадне скління з вакуумними склопакетами, внутрішнє оздоблення -

пластикові вагонки.

Підлога - дерев'яні дошки 40мм по металевому каркасу з утеплювачем з мінераловатних плит та покриттям з негорючого матеріалу.

Покрівля - по металевим прогонам з покриттям листами оцинкованої покрівельної сталі з утеплювачем

з мінераловатних плит та гідро-і пароізоляцією.

Зовнішня обробка - Поверхні стін- фасадне скління, обшивка металевим листом для зовнішніх робіт.

2. Тимчасова споруда підключається до мереж електропостачання, водопроводу та каналізації згідно з діючими нормами та ТУ.

Опалювання - електричне з встановленням навісних електроконвекторів з регулюванням температури.

Освітлення ТС виконується світильниками з світлодіодними лампами.

Мережі обрані по тривалодопустимим струмам навантаження.

Захист мереж від дії струмів коротких замикань і перевантаження здійснюється автоматичними вимикачами щитка.

3. Благоустрій прилеглої території виконується згідно з планом благоустрою. Освітлення прилеглої території передбачено від підсвічування фасаду ТС.


Архітектор

Кваліфікаційний сертифікат архітектора серія АР № 003129




Каразейський Ю.В.

Головний фасад М 1:50 .

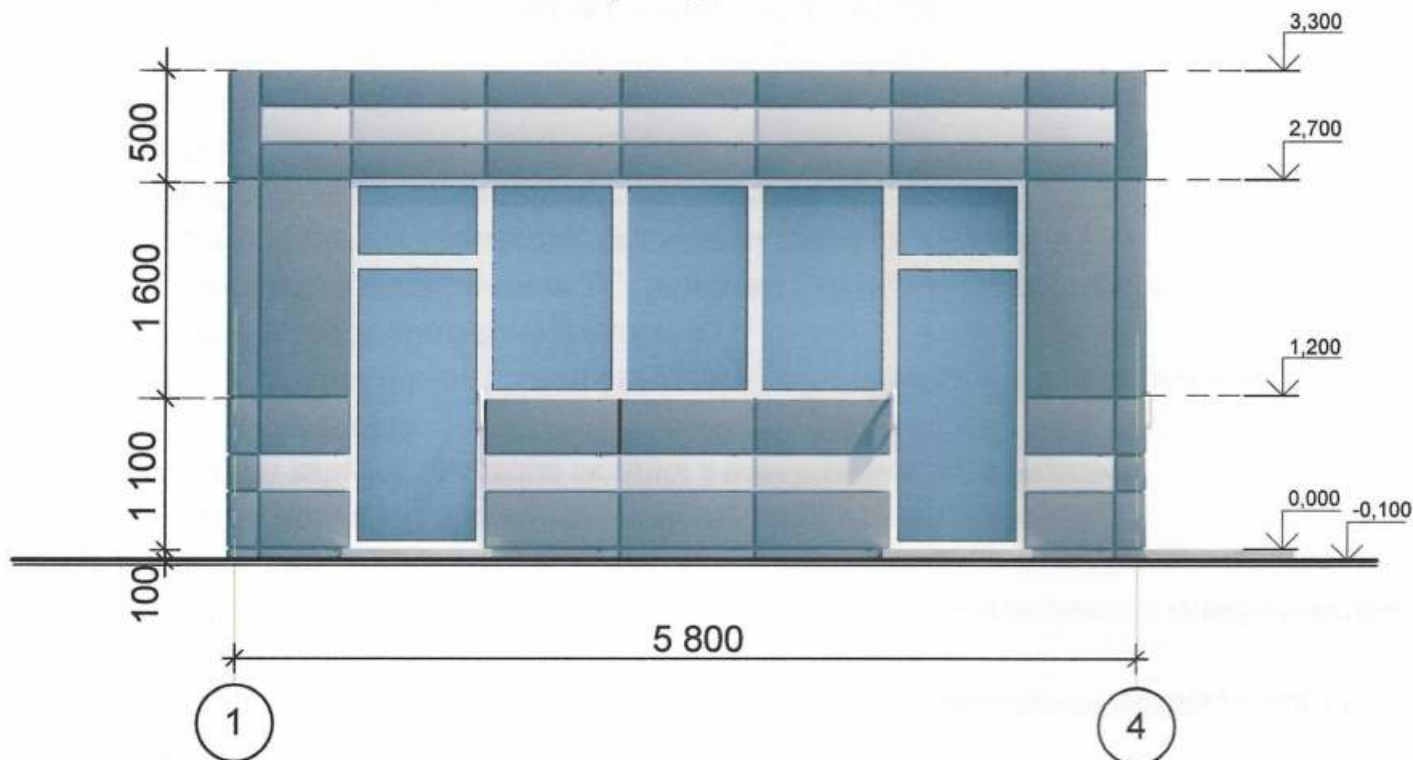

Боковий фасад М 1:50 .

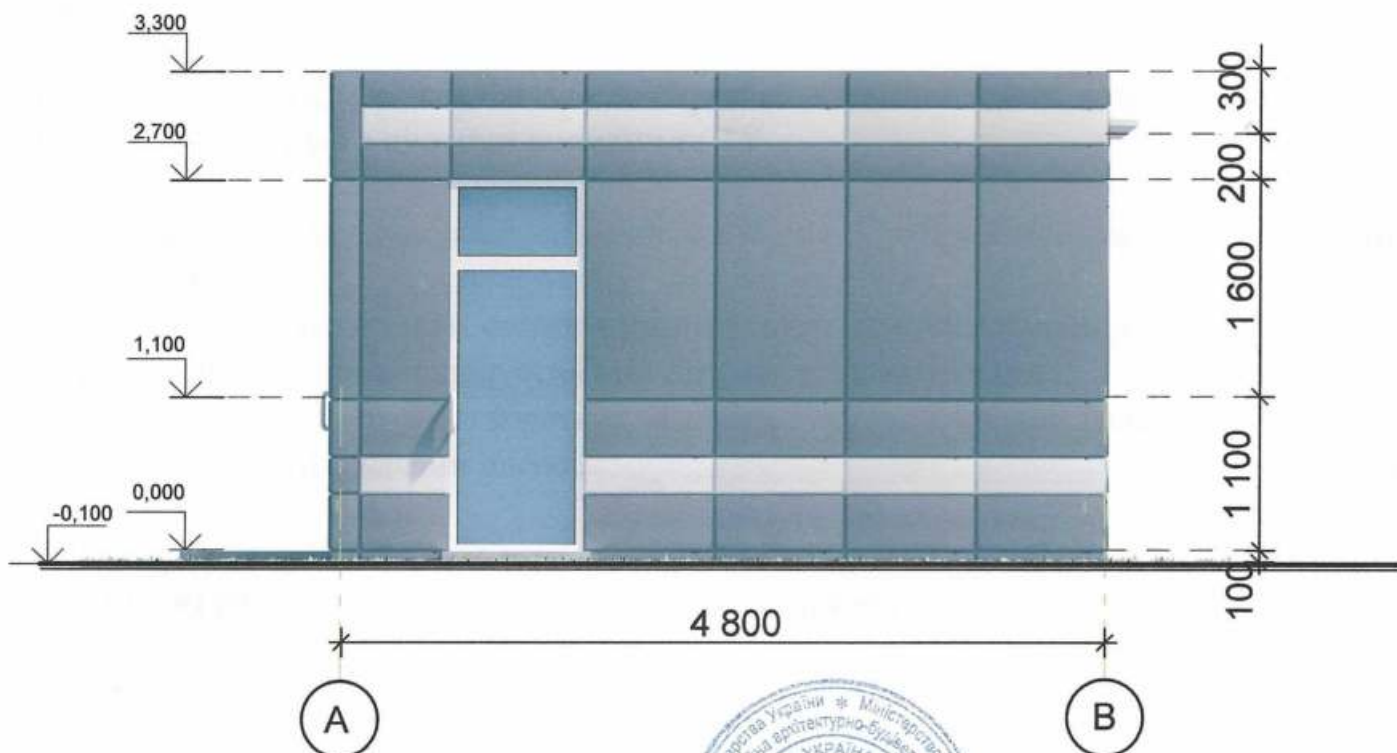


Архітектор

Кваліфікаційний сертифікат архітектора серія АР № 003129



Каразейський Ю.В.

ПЛАН ТИМЧАСОВОЇ СПОРУДИ М 1:50.

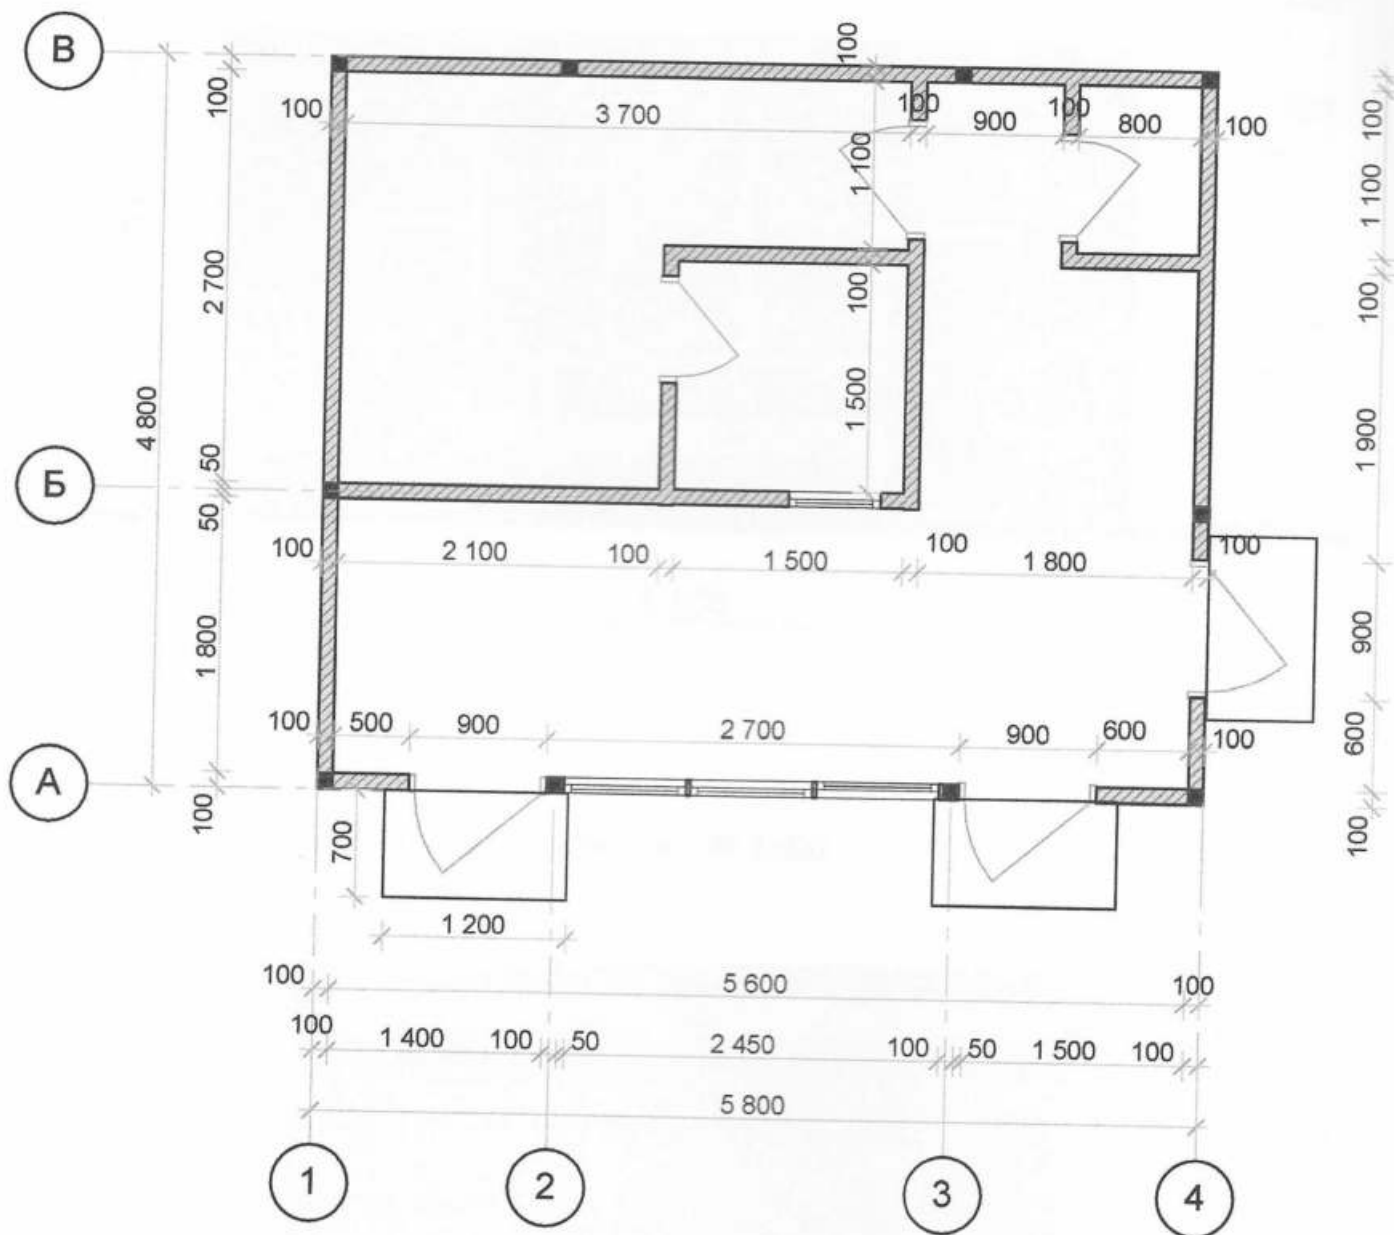

Загальна площа тимчасової споруди - 28,0 м²

Архітектор


Кваліфікаційний сертифікат архітектора серія АР № 003129



Каразейський Ю.В.

СХЕМА РОЗМІЩЕННЯ ТИМЧАСОВОЇ СПОРУДИ, М 1:500 .

Площа земельної ділянки згідно з документами на землекористування
міськ. земел. фонд земля м. Одеси

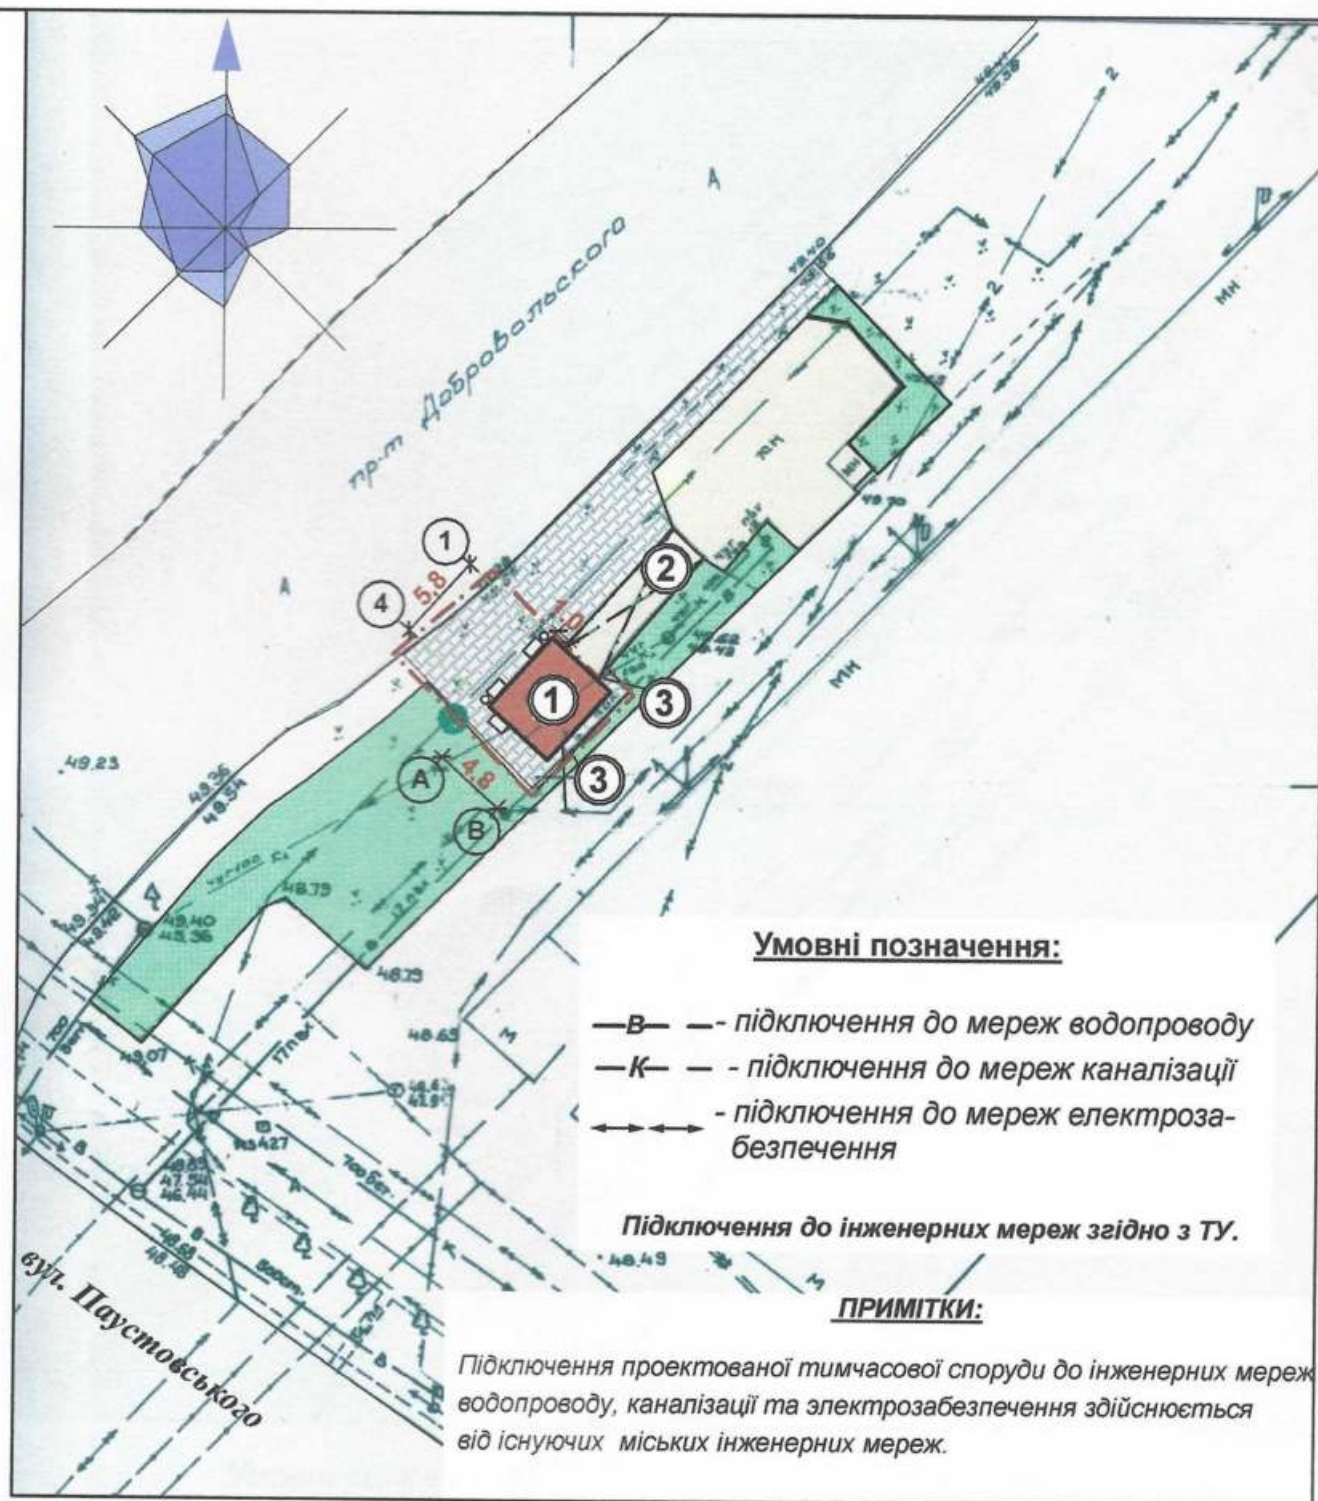

Експлікація:

1. місце розташування ТС
2. лінії регулювання забудови
3. місце підключення до інженерних мереж

Умовні позначення:

- | | | | |
|--|---|--|---|
| | - об'єкт проєктування (тимчасова споруда) | | - проєктоване мостіння тротуарною плиткою |
| | - існуючі споруди | | - існуюче озеленення |
| | - існуючі дороги | | - межа благоустрою ділянки розміщення ТС |


Архітектор

Кваліфікаційний сертифікат архітектора серія АР № 003129



Каразейський Ю.В.

СИТУАЦІЙНИЙ ПЛАН, М 1:2000.

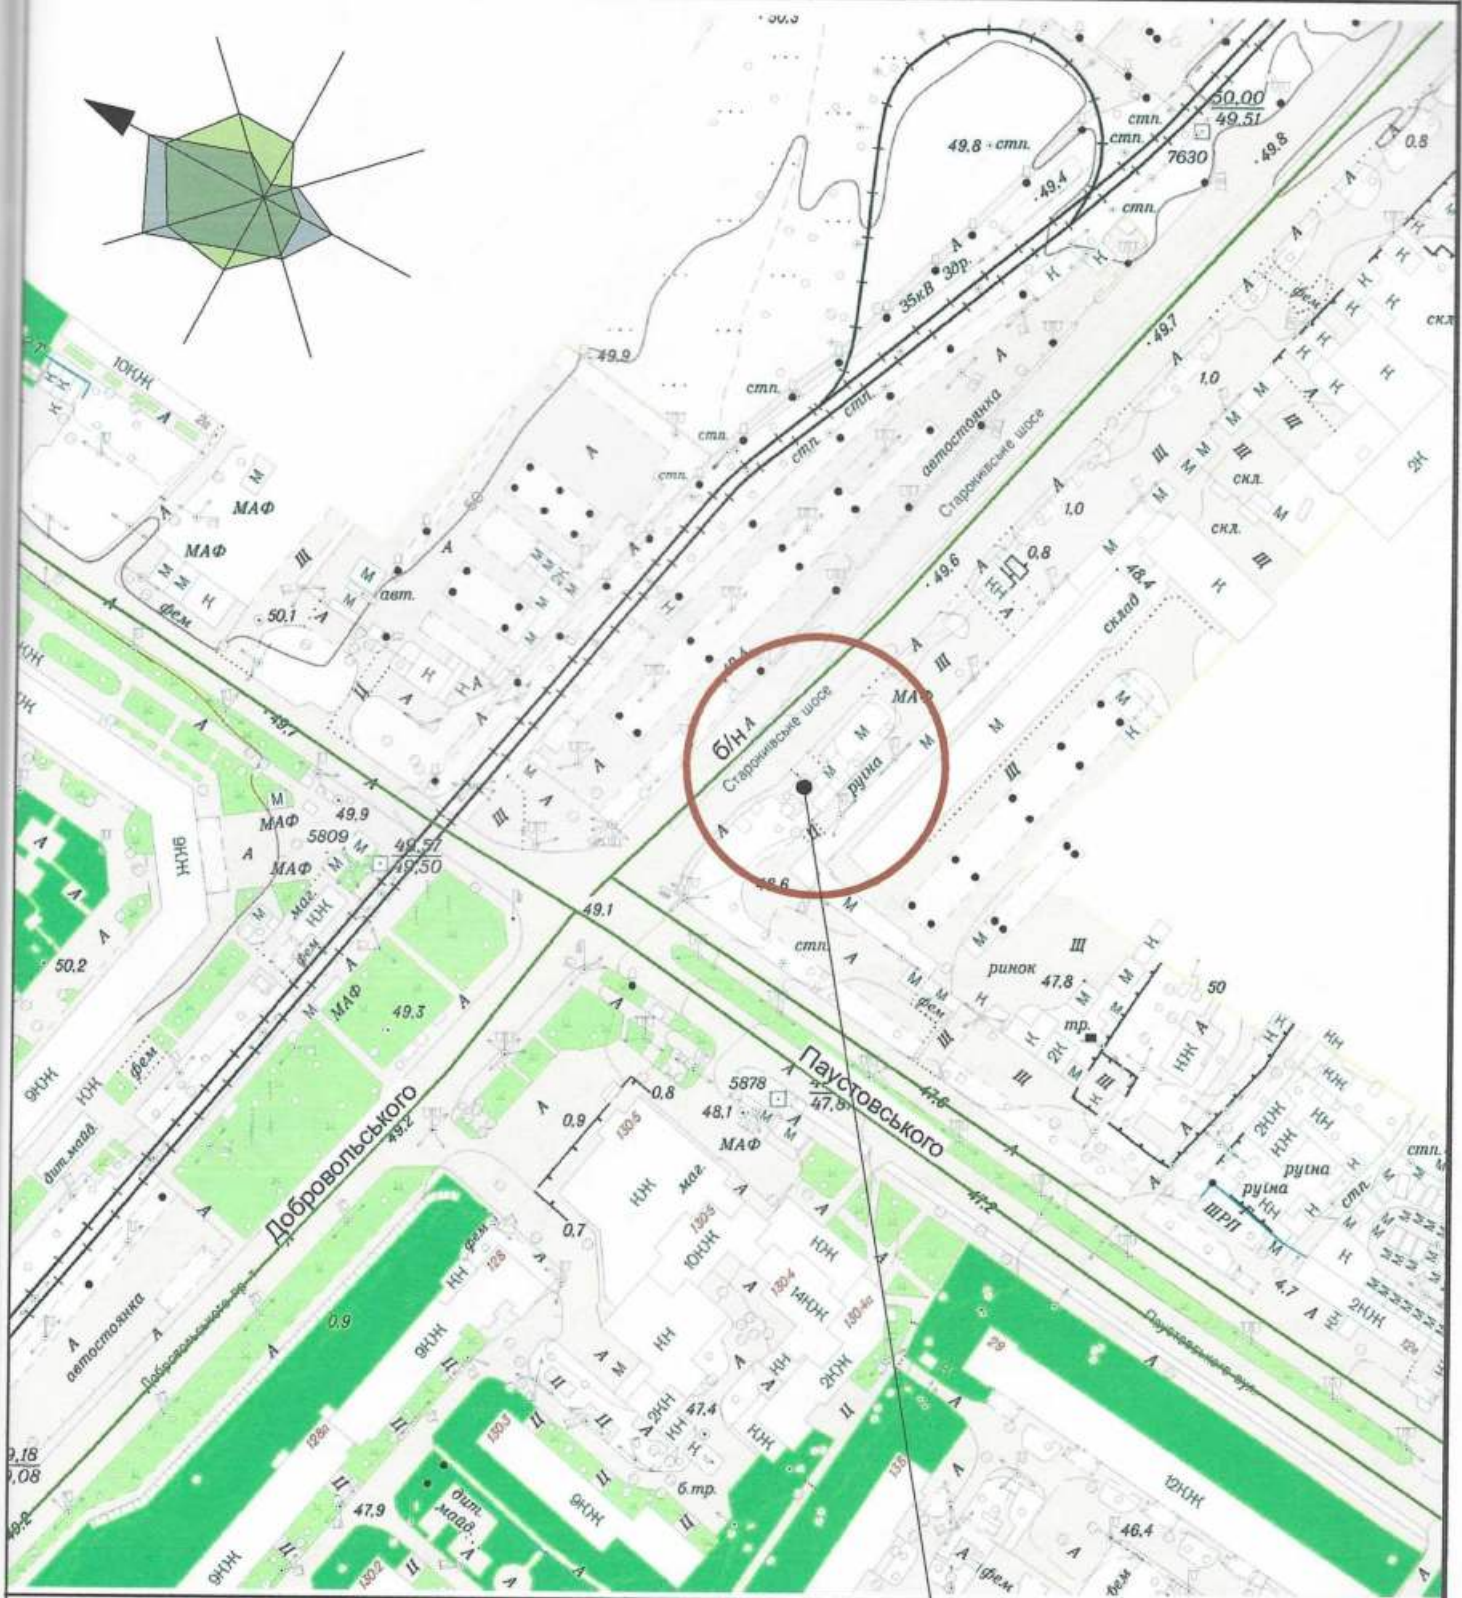

Місце розміщення об'єкта

Архітектор

Кваліфікаційний сертифікат архітектора серія АР № 003129



Каразейський Ю.В.