

СТИСЛА ПОЯСНЮВАЛЬНА ЗАПИСКА

1. Тимчасова споруда (ТС) для здійснення підприємницької діяльності має закриті приміщення для тимчасового перебування людей.
За умовну позначку 0.000 прийнятий рівень чистої підлоги ТС.
Ступінь вогнестійкості - IIIа
Габаритні розміри павільйона в плані - 5.55 x 4.00 м.
Загальна площа ТС - 22.20 м.кв.
Загальна висота ТС - 3.10м.
Внутрішня висота ТС - 2.80м.
Встановлюється ТС на існуючу тротуарну плитку.
Стіни споруди дерев'яні із утеплювачем з мінеральної вати та обшивкою.
Обшивка стін по каркасу: зовнішня - дерев'яні бруси;
внутрішня (стіни й стеля) - дерев'яна вагонка.
Підлога з покриттям дошки 40мм. і утеплювачем (керамзитовий ґравій - 200мм.) та покриття з негорючого матеріалу.
Покрівля - по металевим прогонам і решетуванню з покриттям із профільованного сталевго листа, з утеплювачем з мінераловатних плит, гідро-і пароізоляцією.

ЗОВНІШНЯ ОБРОБКА:

поверхні стін - обшивка металевий лист для зовнішніх робіт;
вікна - металопластикові;
двері - металопластикові;
покрівля - профільований сталевий лист;
ТС встановлюється без улаштування фундаменту.

2. Стационарна тимчасова споруда підключається до мереж електропостачання згідно з діючими нормами та ТУ. Точка підключення - тільки згідно з ТУ. ТУ на підключення не були надані Замовником під час розробки паспорту привязки.
Опалювання - електричне з встановленням навісних електро-конвекторів з регулюванням температури.
Освітлення приміщення виконується стельовими світильниками з люмінесцентними лампами.
Розподільні мережі виконані проводами з мідними жилами, що прокладені у трубах та приховані в обшивці стін.
Захист мереж від дії струмів коротких замикань і перевантаження здійснюється автоматичними вимикачами щитка.

3. Благоустрій прилеглої території виконується згідно з планом благоустрою. Освітлення території передбачене світильниками, що розміщуються на головному фасаді ТС.

Директор ФОП "Волкова Г.А."

Кваліфікаційний сертифікат серія АА № 001828


Архітектор




Волкова Г.А.

Скаденко Л.М.

Головний фасад

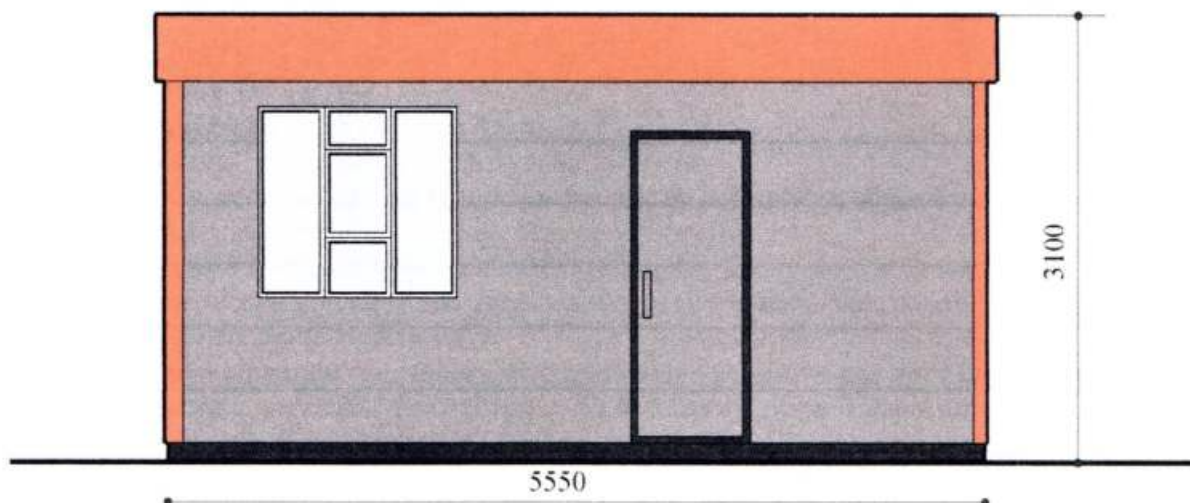

Боковий фасад

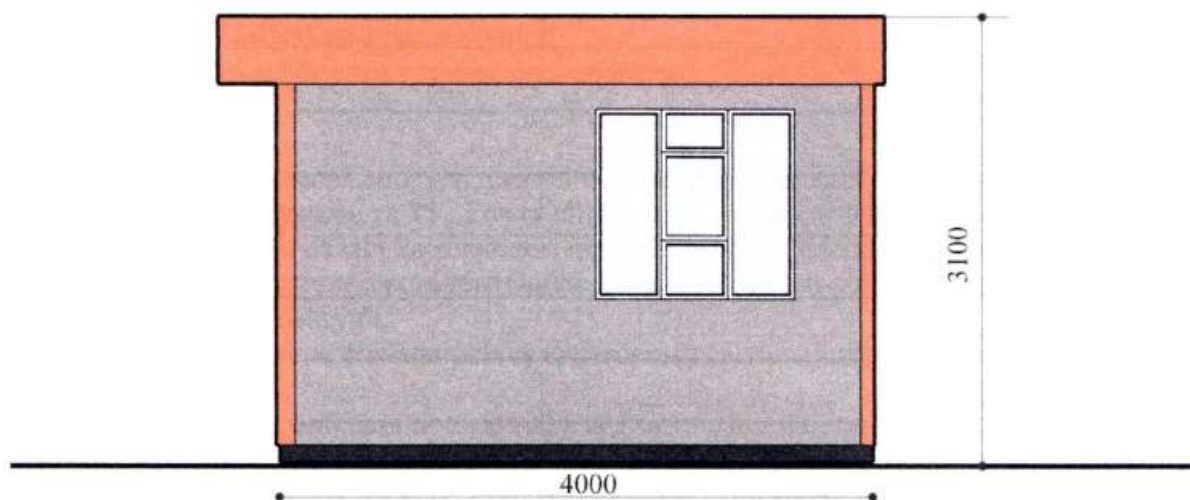


Директор ФОП "Волкова Г.А."
Кваліфікаційний сертифікат серія АА № 001828

Архітектор



ПЛАН ТС М.1:50

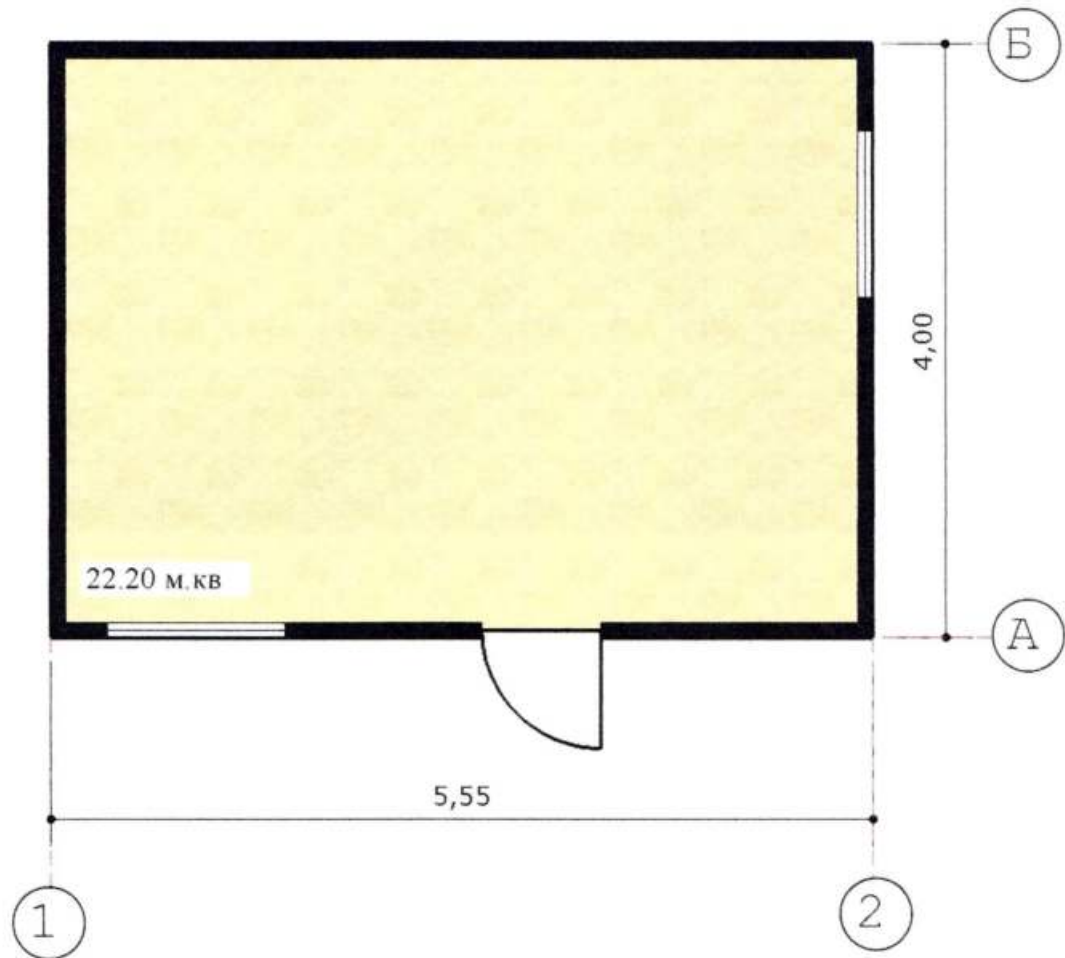

Площа мощення під ТС 22.20 м.кв

Директор ФОП "Волкова Г.А."
Кваліфікаційний сертифікат серія АА № 001828

Архітектор




Волкова Г.А.

Архітектор
Регістраційний
№ 1628

Скаленко Л.М.

СХЕМА РОЗМІЩЕННЯ ТС м. 1:500

Площа земельної ділянки згідно з документами
на землекористування - землі міста

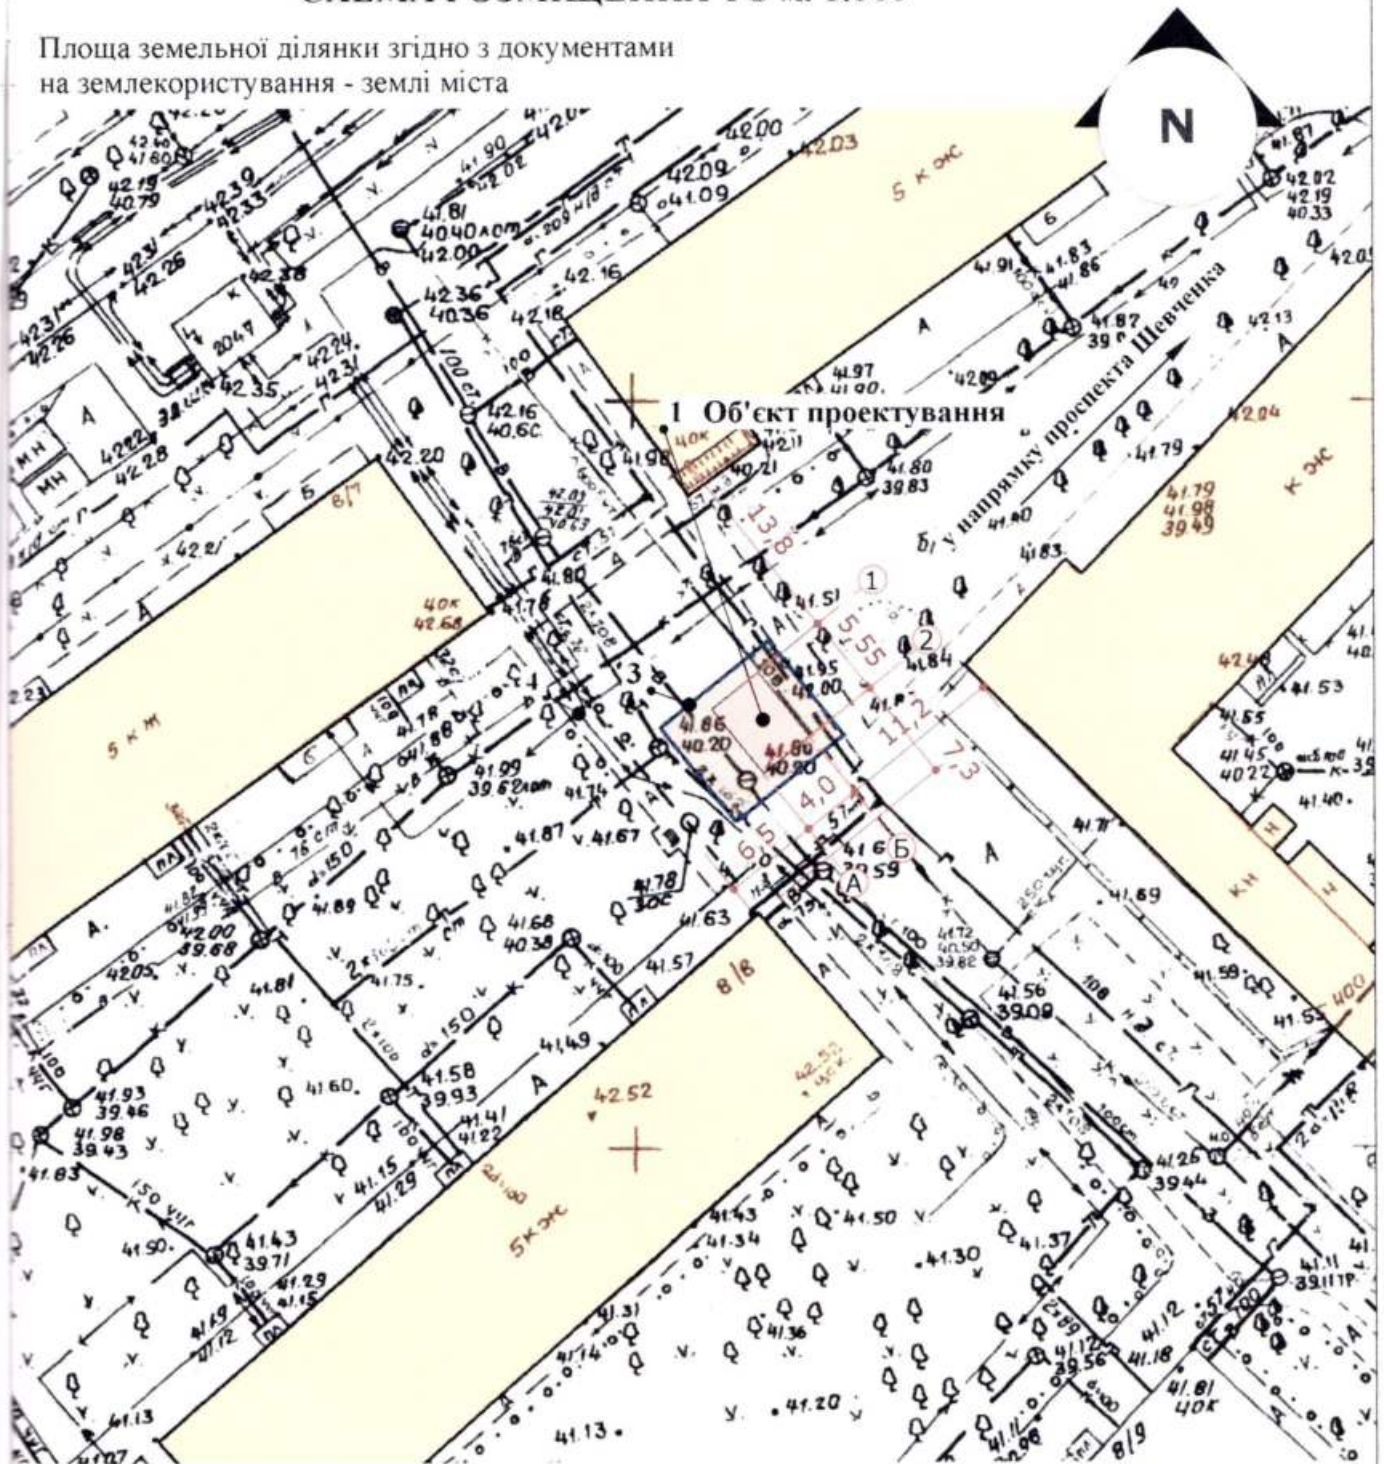

Експлікація:

- 1) місце розташування ТС;
- 2) червоні лінії;
- 3) лінії регулювання забудови;
- 4) місця підключення до інженерних мереж.
(електропостачання)

- Умовні позначення:
- межа благоустрою ділянки розміщення ТС
 - ТС
 - існуючі будівлі
 - існуючі дороги
 - підключення до мереж електропостачання

Директор ФОП "Волкова Г.А."
Кваліфікаційний сертифікат серія АА № 001828


Архітектор



Архітектор Волкова Г.А.

Регістраційний
№ 1828

Каленко Л.М.

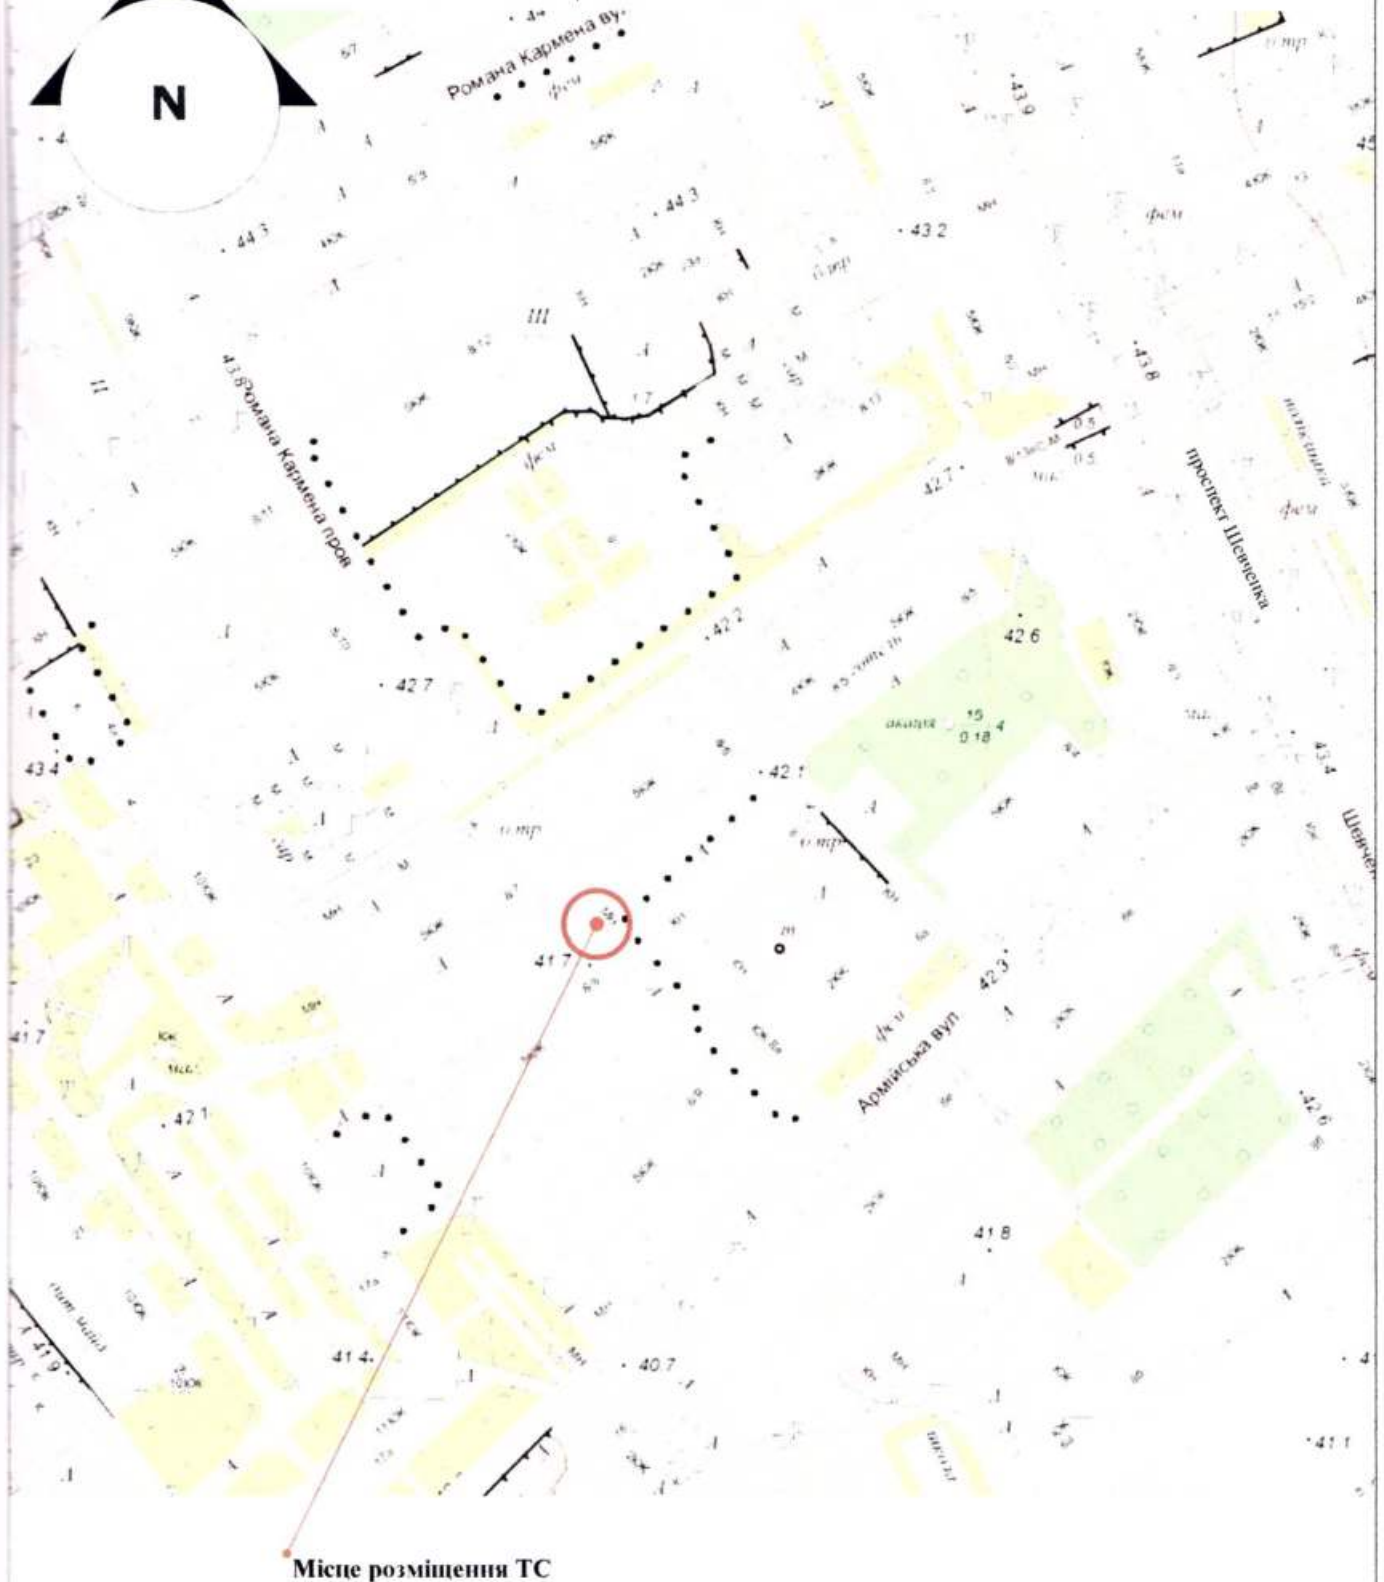

Волкова Г.А.

Скаленко Л.М.